

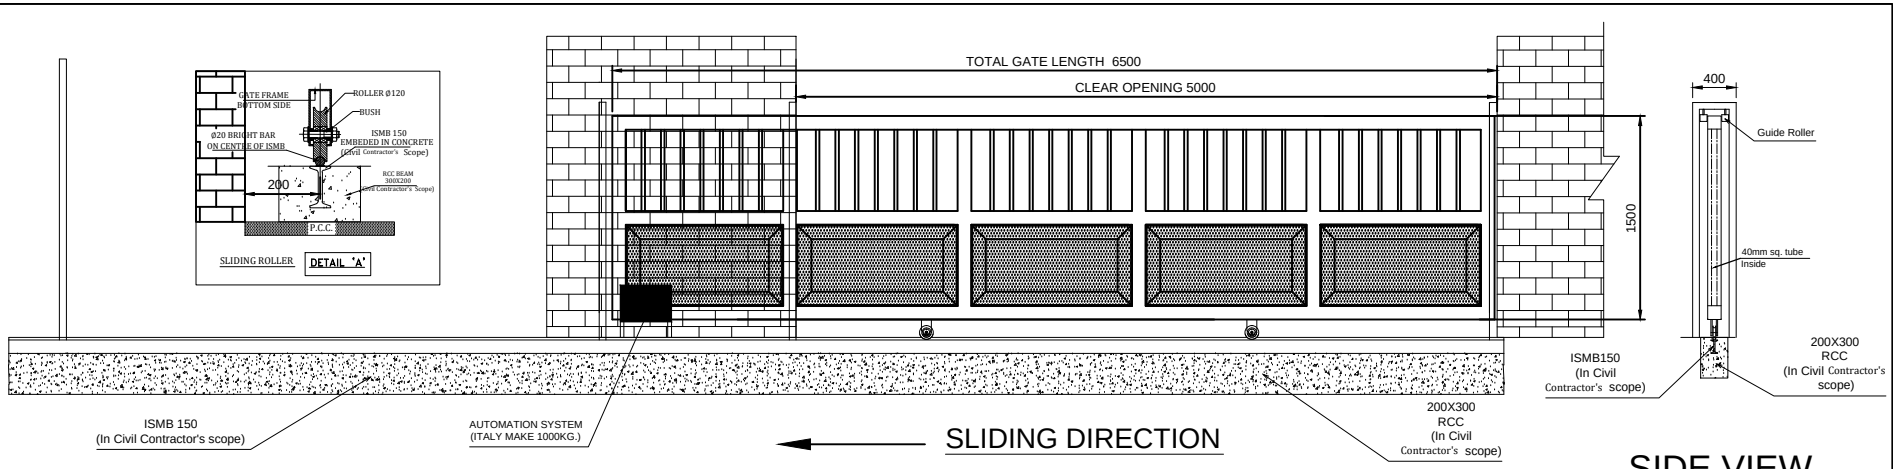



INSIDE VIEW

SIDE VIEW

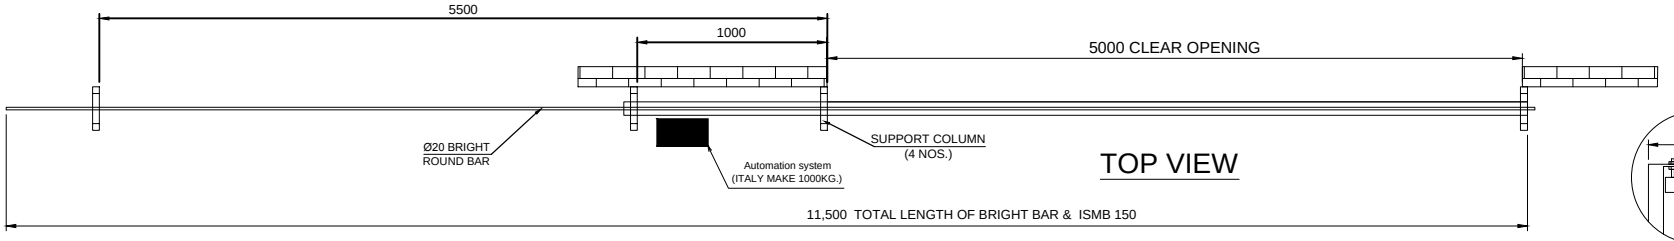

TOP VIEW

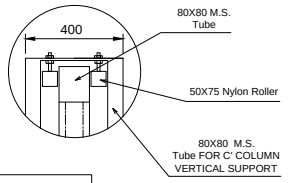

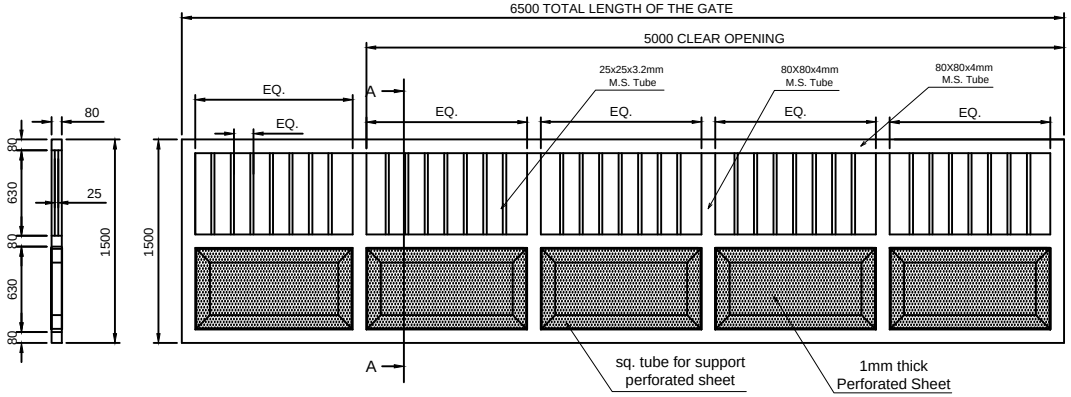

Clear Opening size - 5000X1500mm
Total length of gate - 6500X1500mm
No. Of Column - 4 nos.
Factory paint finish - Red oxide primer coat with Enamel paint Finish
NOTE :- *ALL REQ. CIVIL WORK WILL BE IN YOUR CONTRACTOR'S SCOPE.
NOTE:- As per calculation only 2 wheels are required for Motorized Sliding Gate.

☑ FINAL CERTIFIED

This drawing & designing is the property of NIHVA TECHNOLOGIES. Not be sold or copy to any other concern.

TITLE	MOTORIZED SLIDING GATE		NIHVA TECHNOLOGIES PVT. LTD.
	SIGN	DATE	
DRAWN	ABHIJIT	19/11/15	CLIENT - REWARD CONSTRUCTION
CHECK	ANIL	19/11/15	PROJECT - GIVAUDAN
REV.	05		SITE - RANJANGAON MIDC
APPROVAL			DWG. NO. : NIHVA/15-16/104
If any queries contact : projects@nihva.com			SCALE: 01 / WT: / SHEET: 01 OF 01
ALL DIMENSION ARE IN mm			

NIHVA TECHNOLOGY PVT. LTD. PUNE
Tel : 020 66304033
Email:- info@nihva.com
Website:- www.nihva.com