

DRAWING

KEY PLAN

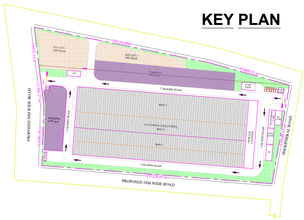

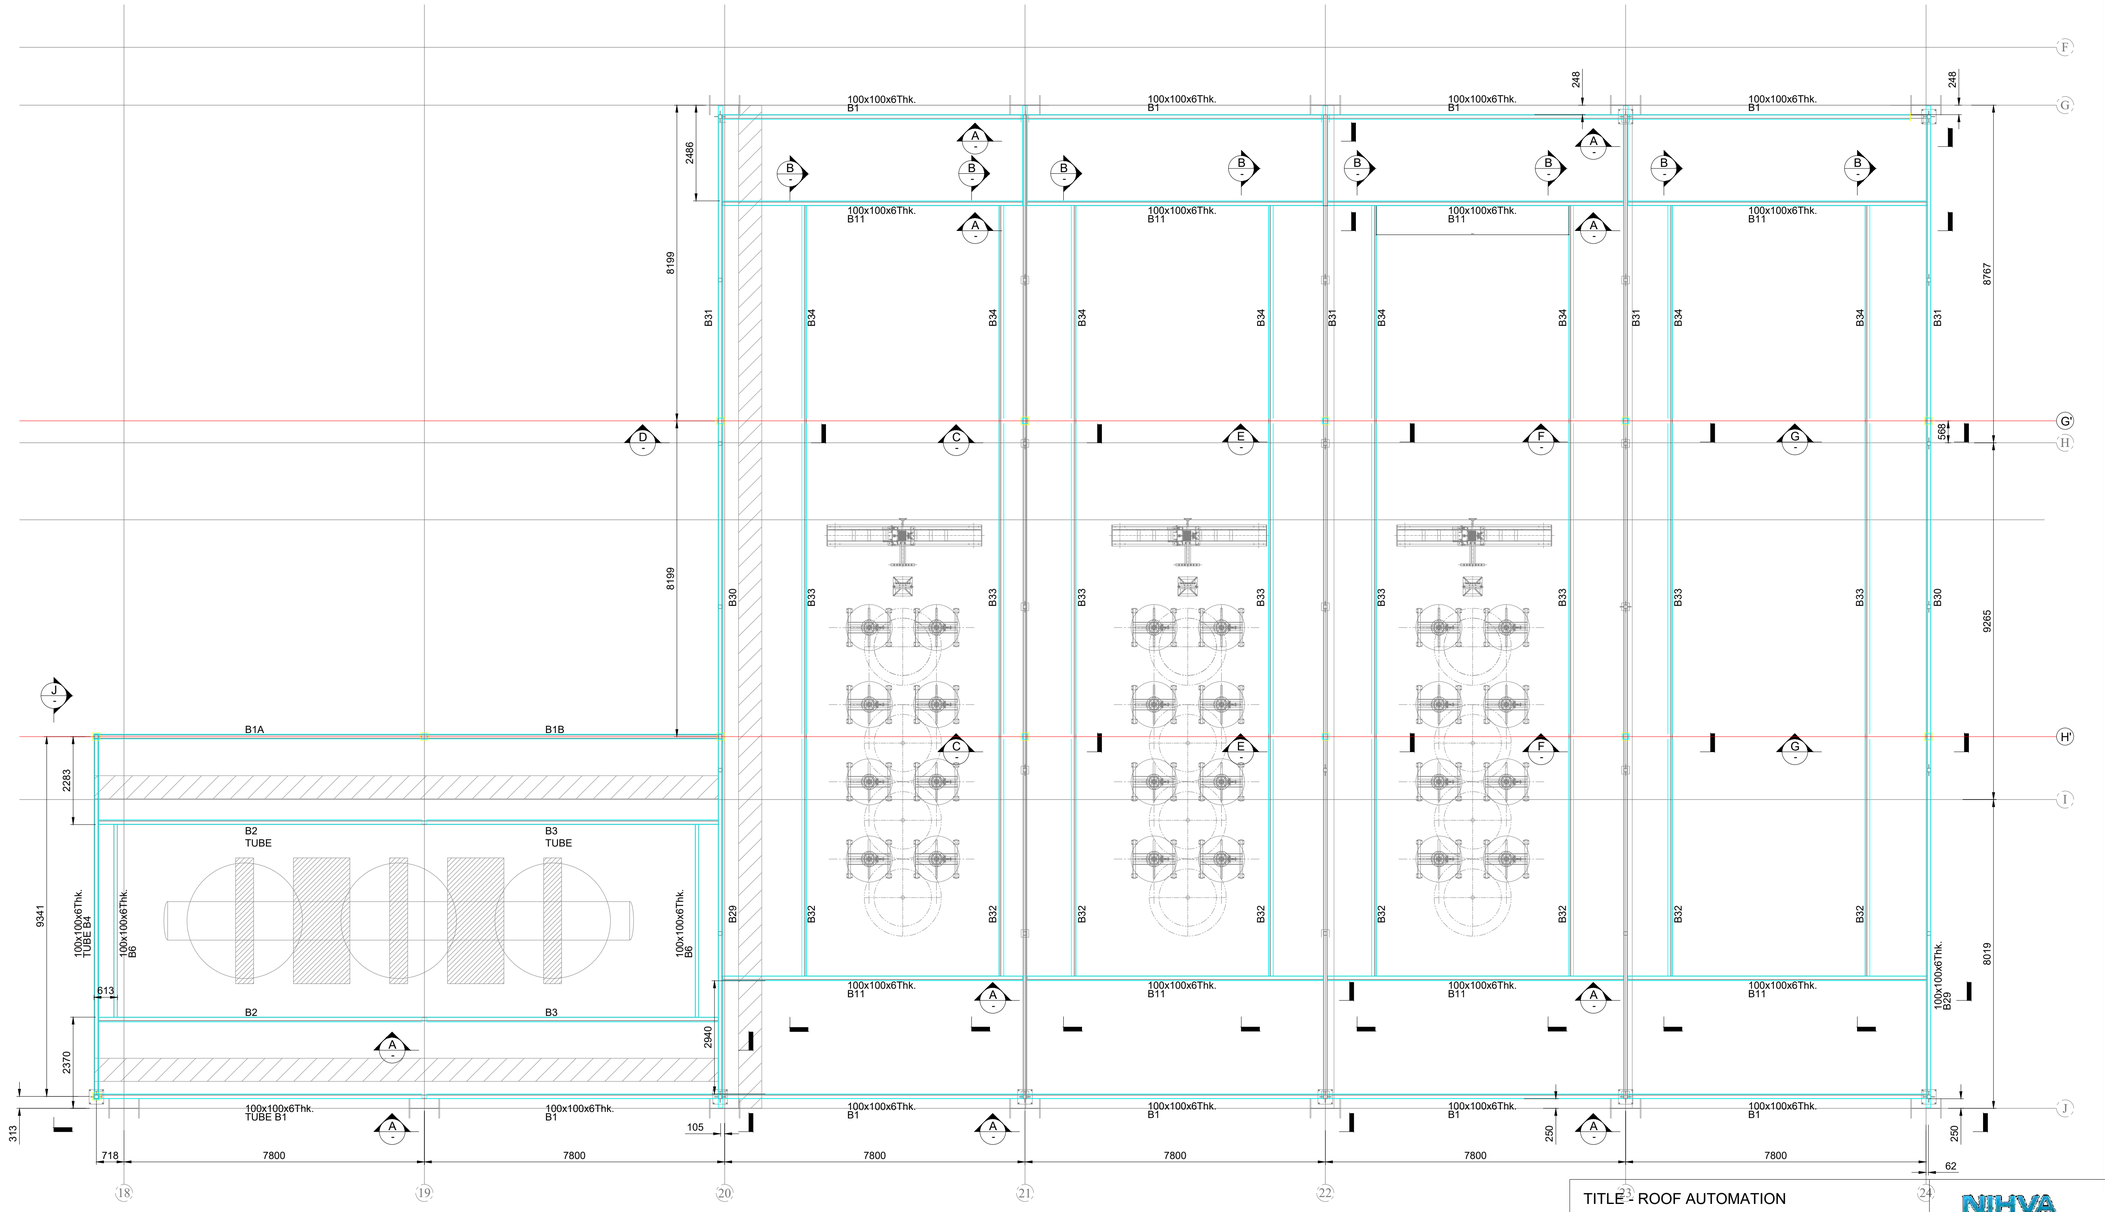

LAYOUT PLAN AT 4.50M LEVEL

TITLE - ROOF AUTOMATION				NIHVA Technologies Pvt. Ltd.	NIHVA TECHNOLOGIES PVT.LTD.PUNE Website - www.nihva.com
DWG NO - NTPL- 401-PM-01					
	NAME	SIGNATURE	DATE	PRODUCT – BASE STRUCTURE VWM-HWM & SPA	
DRAWN	V.W.		09-06-2026	LOCATION - HYDERABAD	REVISION - 00
CHK'D	S.P.		10-09-2026	CLIENT- NEOTRAFO SOLUTIONS PVT. LTD.	
APPV'D	V.T.		10-09-2026		
IF ANY QUERIES CONTACT - info@nihva.com				PROJECTION METHOD	SCALE :
ALL DIMENSIONS ARE IN 'MM'		A1			SHEET 1 OF 1