

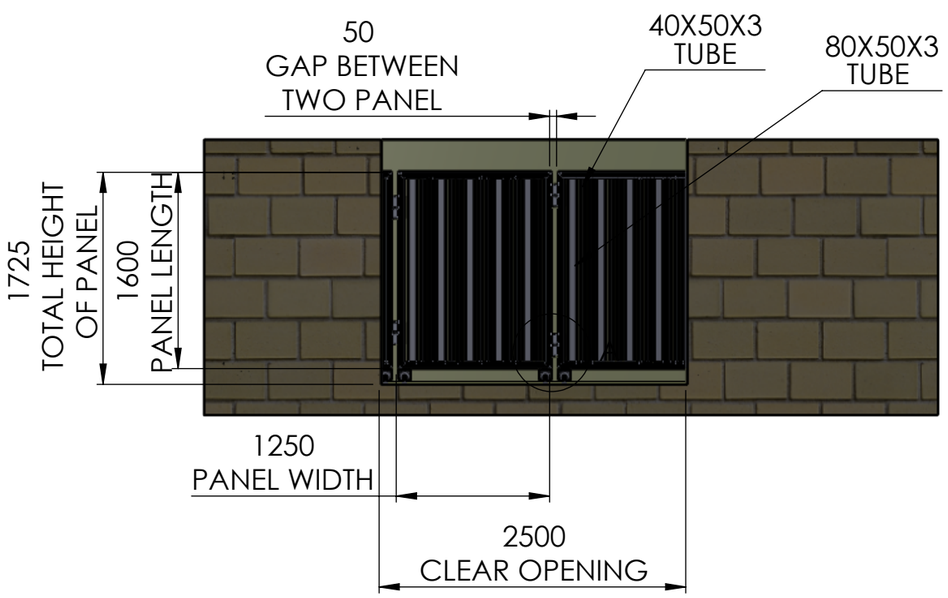


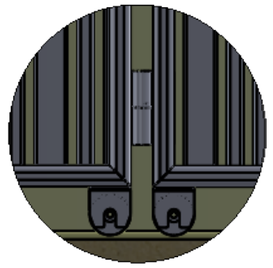


DETAIL A
SCALE 1 : 15

WHEEL ASM.

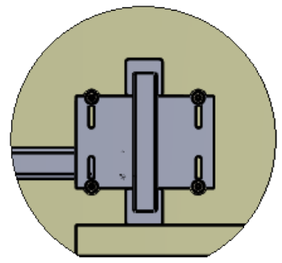


DETAIL B
SCALE 1 : 20

POST AND ROLLER
BEARING ASM.

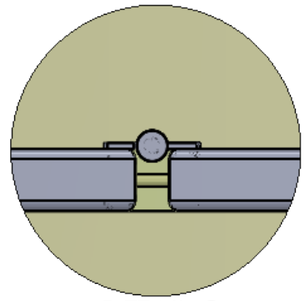


DETAIL C
SCALE 1 : 10


HINGES ASM.

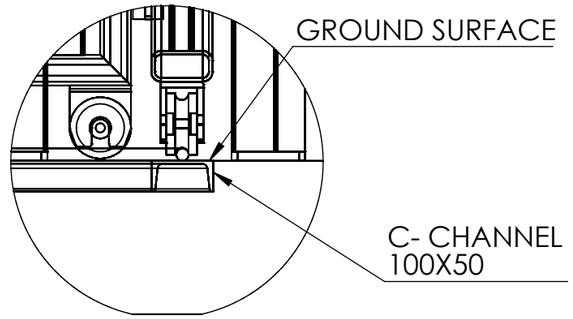

DETAIL E
SCALE 1 : 10
CIVIL STRUCTURE

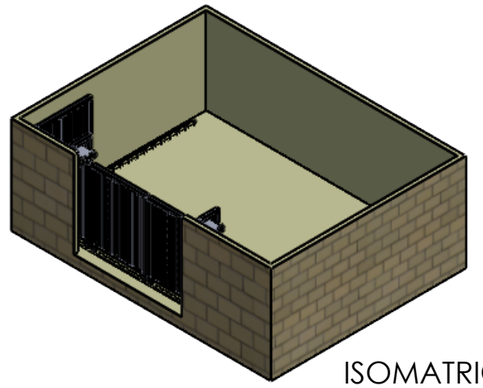


ISOMATRIC VIEW

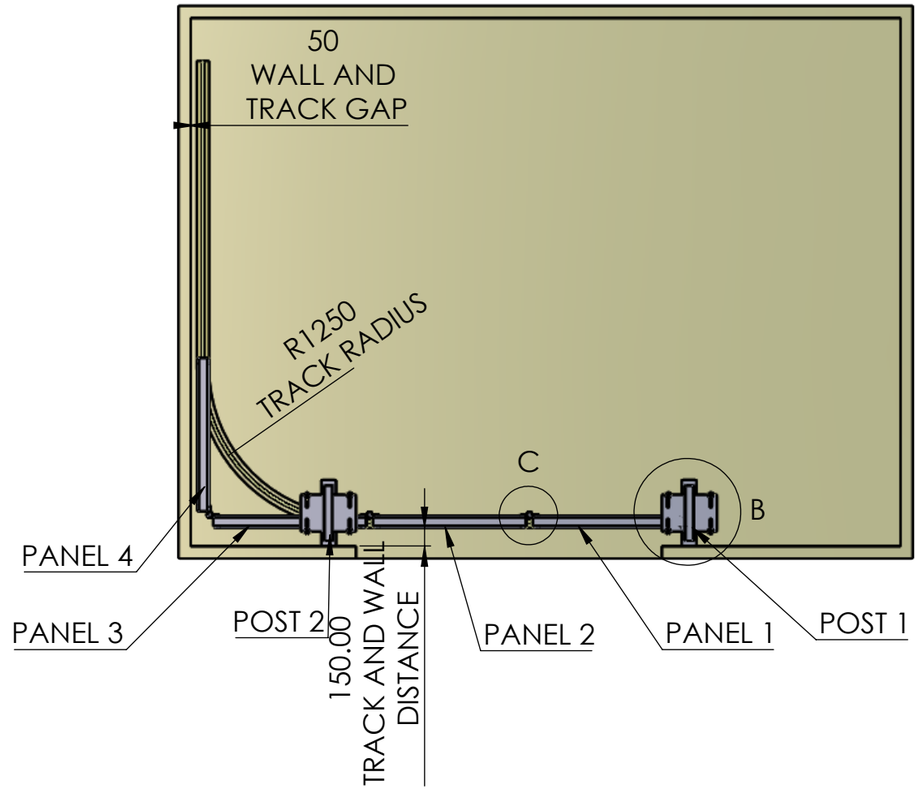



NOTA:- 1) MOTORISED SLIDING FOLDING GATE
2) PARKING AREA 5 M.


TITLE - GATE AUTOMATION				NIHVA TECHNOLOGIES PVT.LTD.PUNE
DWG NO - NTPL268-PM			QTY - 1	Website - www.nihva.com
	NAME	SIGNATURE	DATE	PROJECT NO - NTPL268-PM- AD
DRAWN	V.G		21-05-2025	PRODUCT - SLIDING FOLDING GATE
CHK'D	S.W.		21-05-2025	SITE LOCATION - LUCKNOW
APPV'D	V.T.		21-05-2025	
if any queries contact - supportautomation@nihva.com				REVISION -
ALL DIMENSION ARE IN mm			A3	SCALE - SHEET 1 OF 2

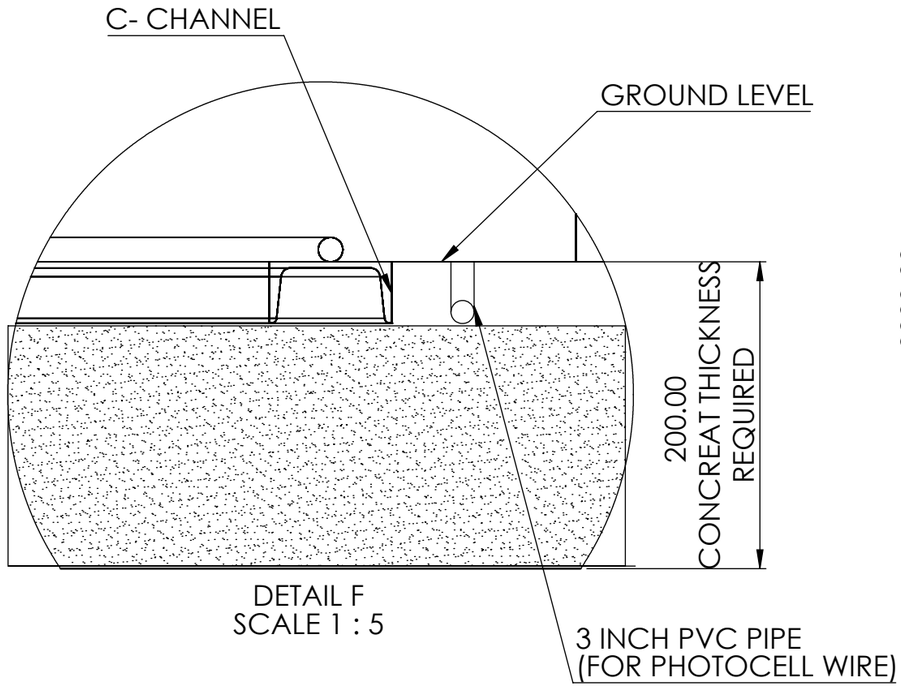

DETAIL F
SCALE 1 : 5

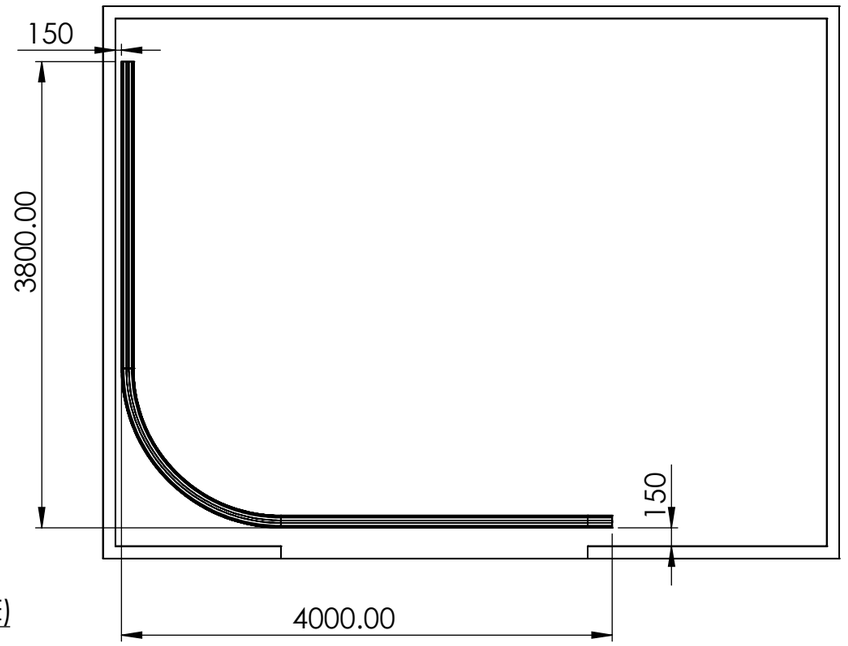

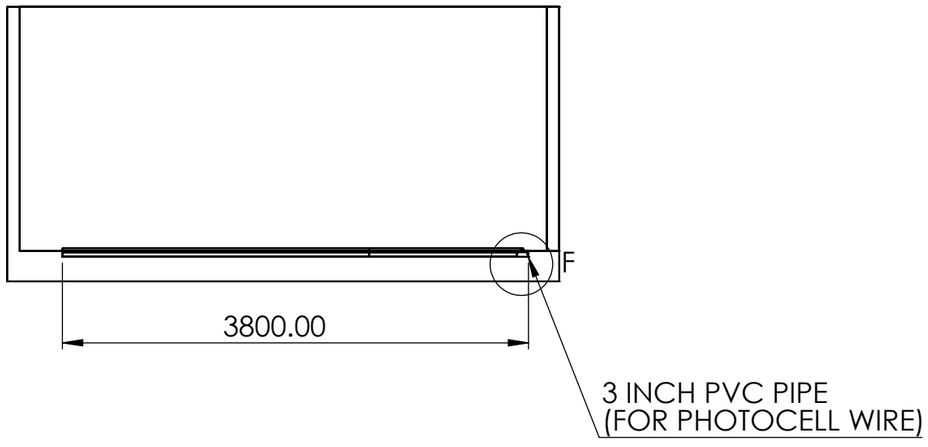

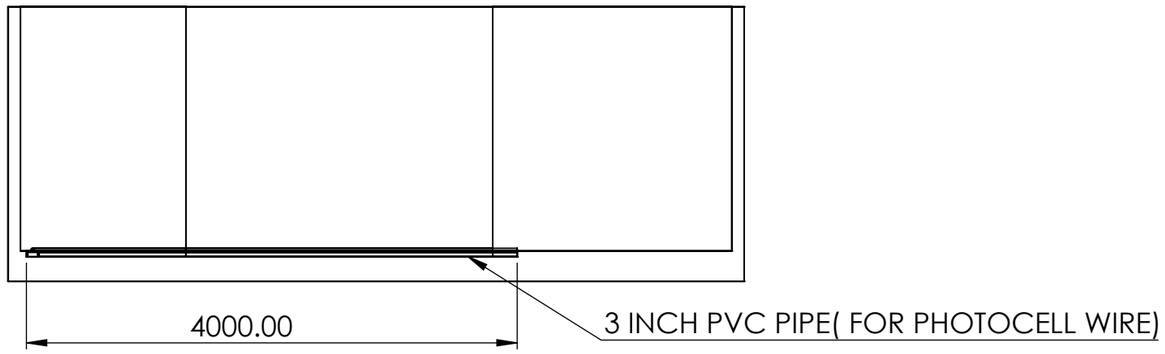

TITLE - RETRACTABLE ROOF				NIHVA TECHNOLOGIES PVT.LTD.PUNE Website - www.nihva.com
DWG NO - NTPL268-PM			QTY - 1	
	NAME	SIGNATURE	DATE	PROJECT NO - NTPL268-PM- AD
DRAWN	S.W		03-03-2025	PRODUCT - RETRACTABLE ROOF
CHK'D	P.M.		03-03-2025	SITE LOCATION - GUJARAT
APPV'D	V.T.		03-03-2025	
if any queries contact - supportautomation@nihva.com				REVISION -
ALL DIMENSION ARE IN mm			A3	SCALE - SHEET 2 OF 2