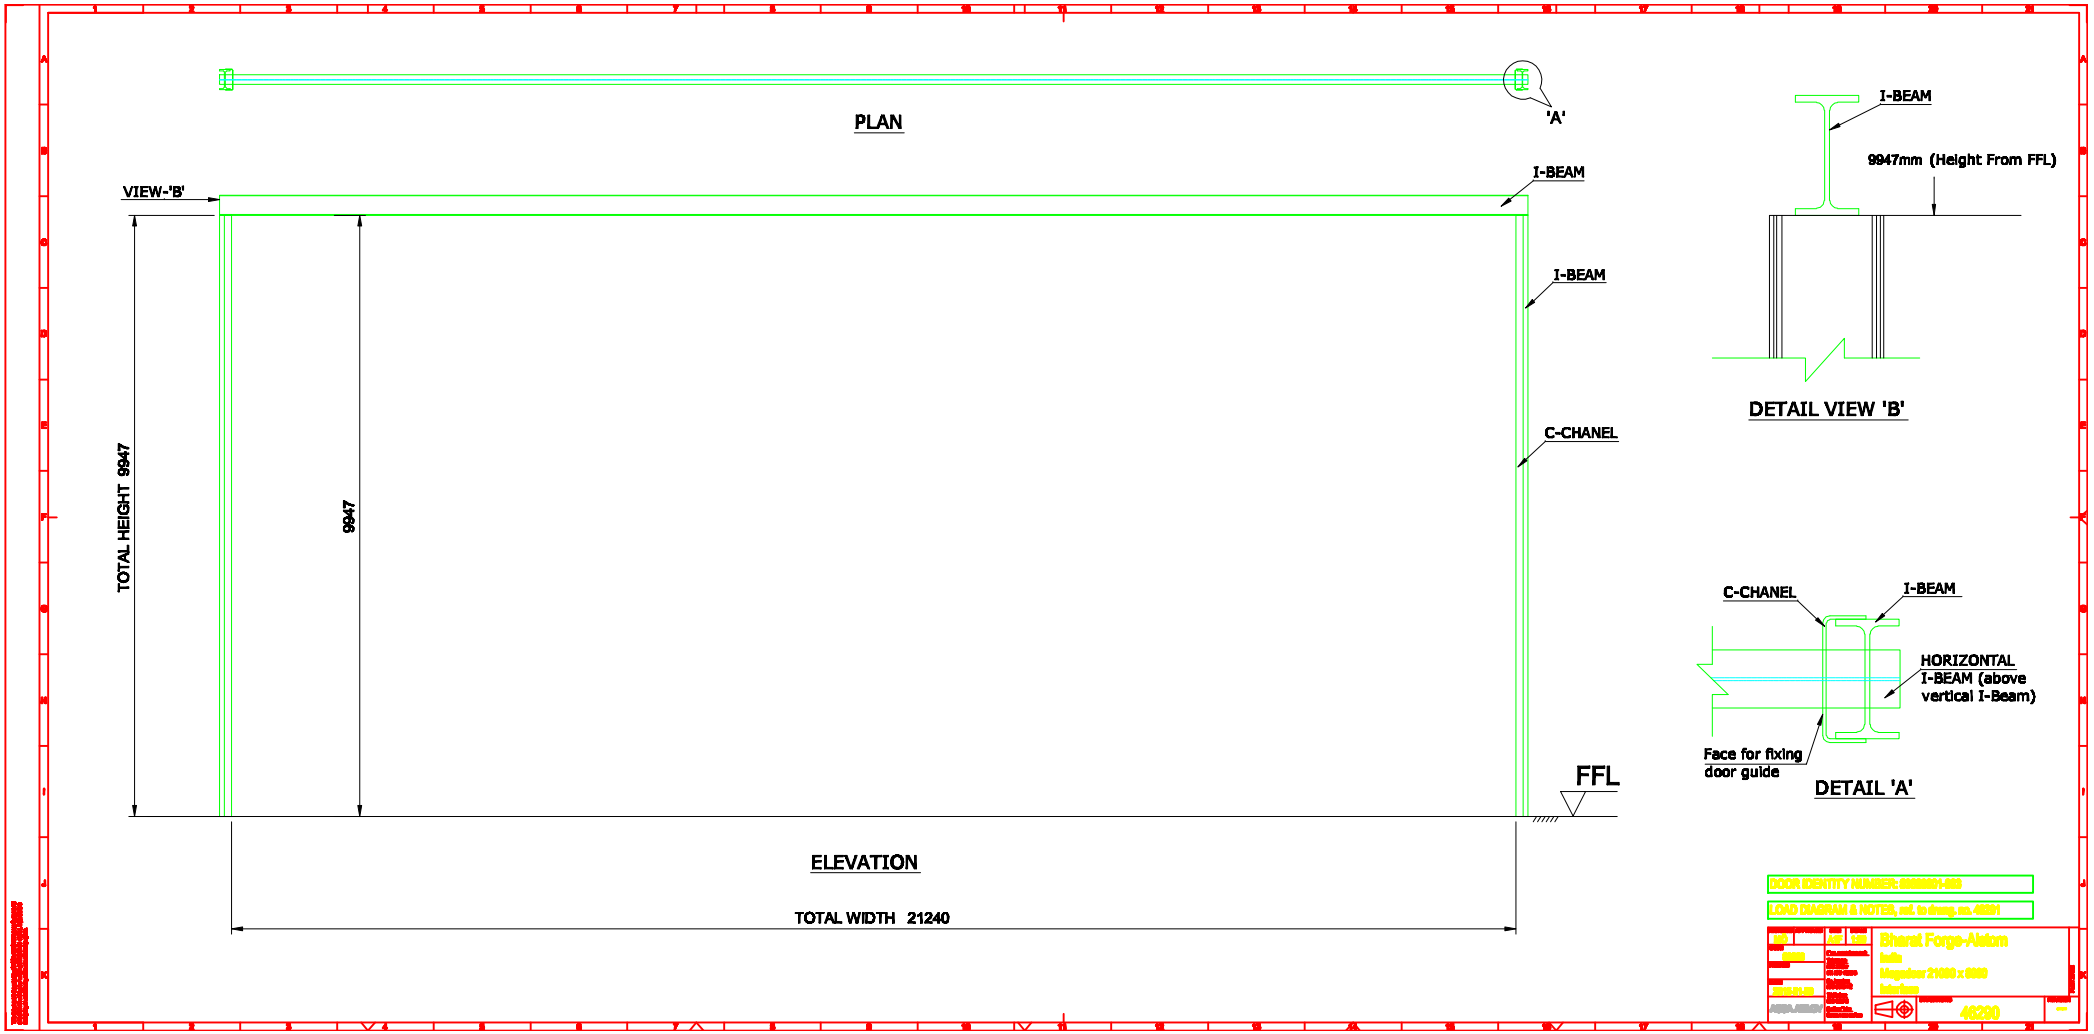

PLAN
'A'
VIEW-'B'
I-BEAM
I-BEAM
C-CHANEL
TOTAL HEIGHT 9947
9947
FFL
ELEVATION
TOTAL WIDTH 21240
I-BEAM
9947mm (Height From FFL)
DETAIL VIEW 'B'
C-CHANEL
I-BEAM
HORIZONTAL
I-BEAM (above
vertical I-Beam)
Face for fixing
door guide
DETAIL 'A'
DOOR IDENTITY NUMBER:
LOAD DIAGRAM & NOTES, ref. to drwng. no.
Bharat Forge-Alstom
46290