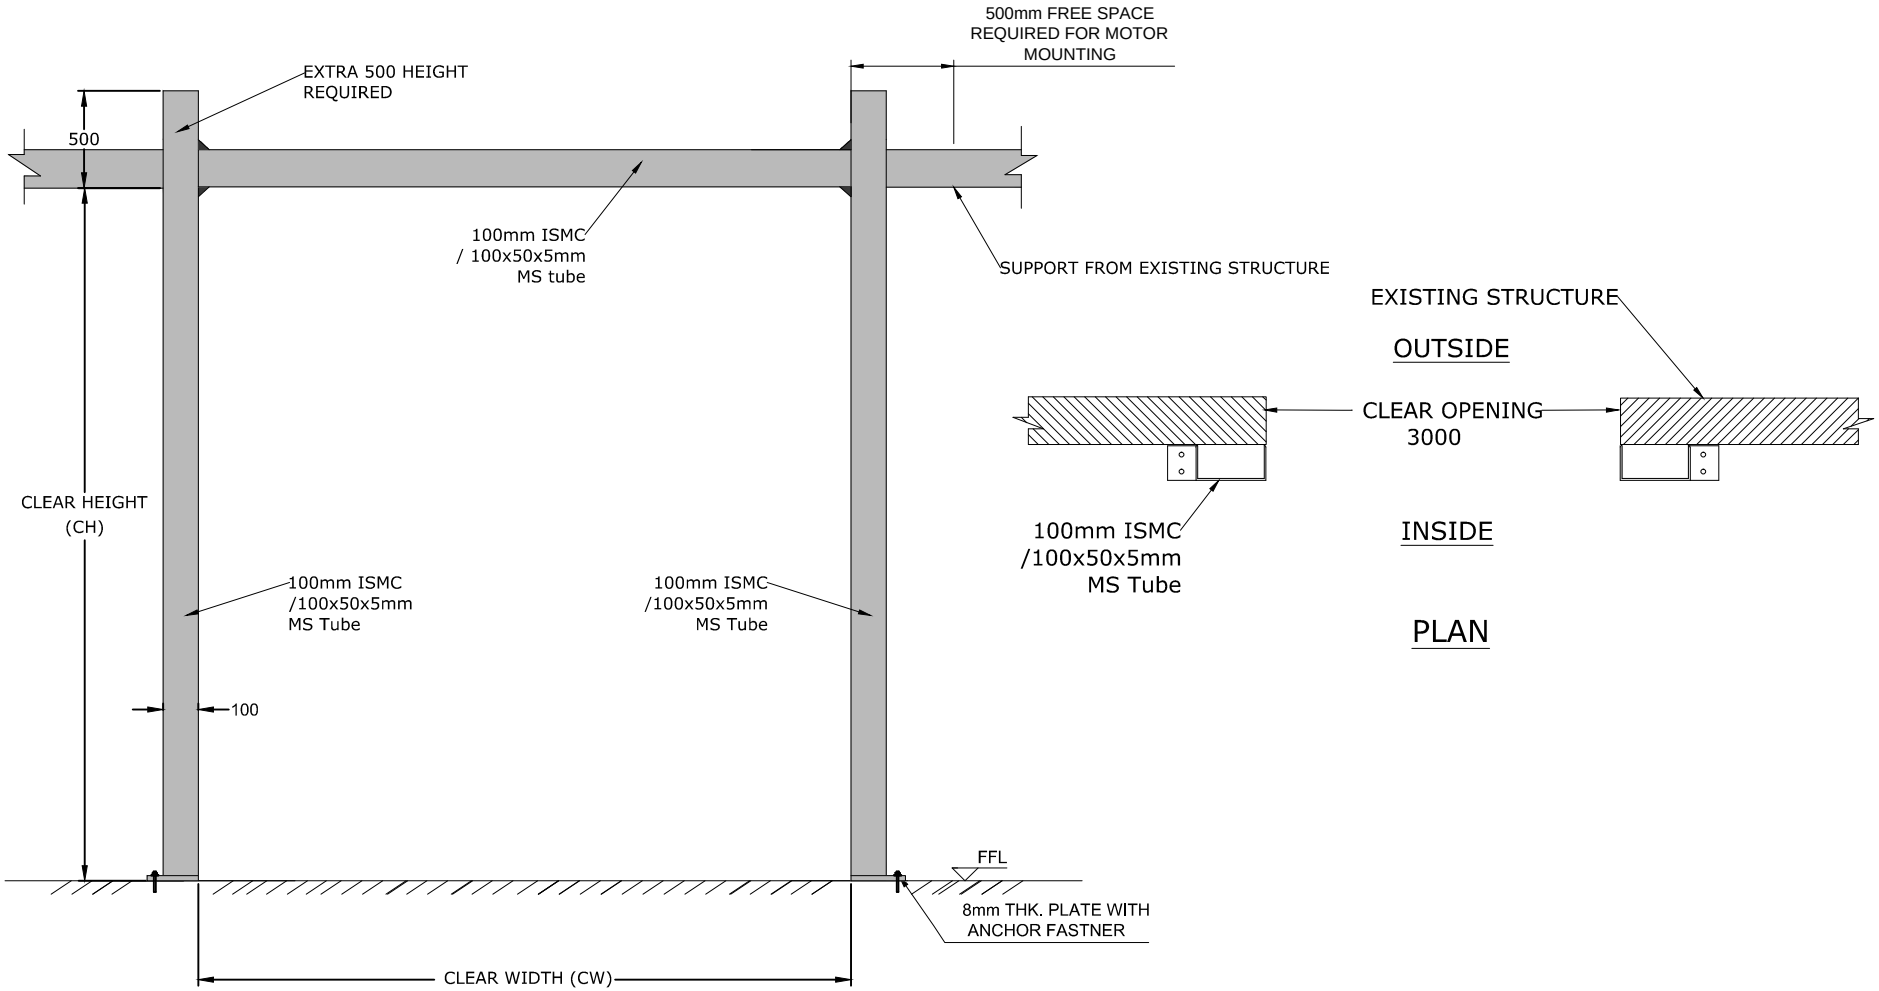


CLEAR WIDTH (CW)	CLEAR HEIGHT (CH)
5000	5000

This drawing & design is the property of NIHVA TECHNOLOGIES. Not be sold or copy to any other concern.

TITLE

STRUCTURE FOR HIGH SPEED DOOR (RR 300+)

CLIENT APPROVAL

ALL DIMENSION ARE IN mm

	SIGN	DATE
DRAWN	OMKAR	10/11/17
CHECK	SHEKHAR	10/11/17
ENG		
APPRD.	SHEKHAR	10/11/17
MFG		
Ref. No.		

NIHVA TECHNOLOGIES PVT. LTD.

NIHVA TECHNOLOGIES PVT. LTD. PUNE
Tel : 020 66304033
Email:- info@nihva.com
Website:- www.nihva.com

CLIENT - TAIIN STEEL FAB & INFRA PVT. LTD.

PROJECT- HYOSUNG T & D

SITE - KHED CITY

DWG. NO. - NIHVA/17-18/0267 | REV-0

SCALE: NTS | WT: | SHEET: 01

If any queries contact : design@nihva.com