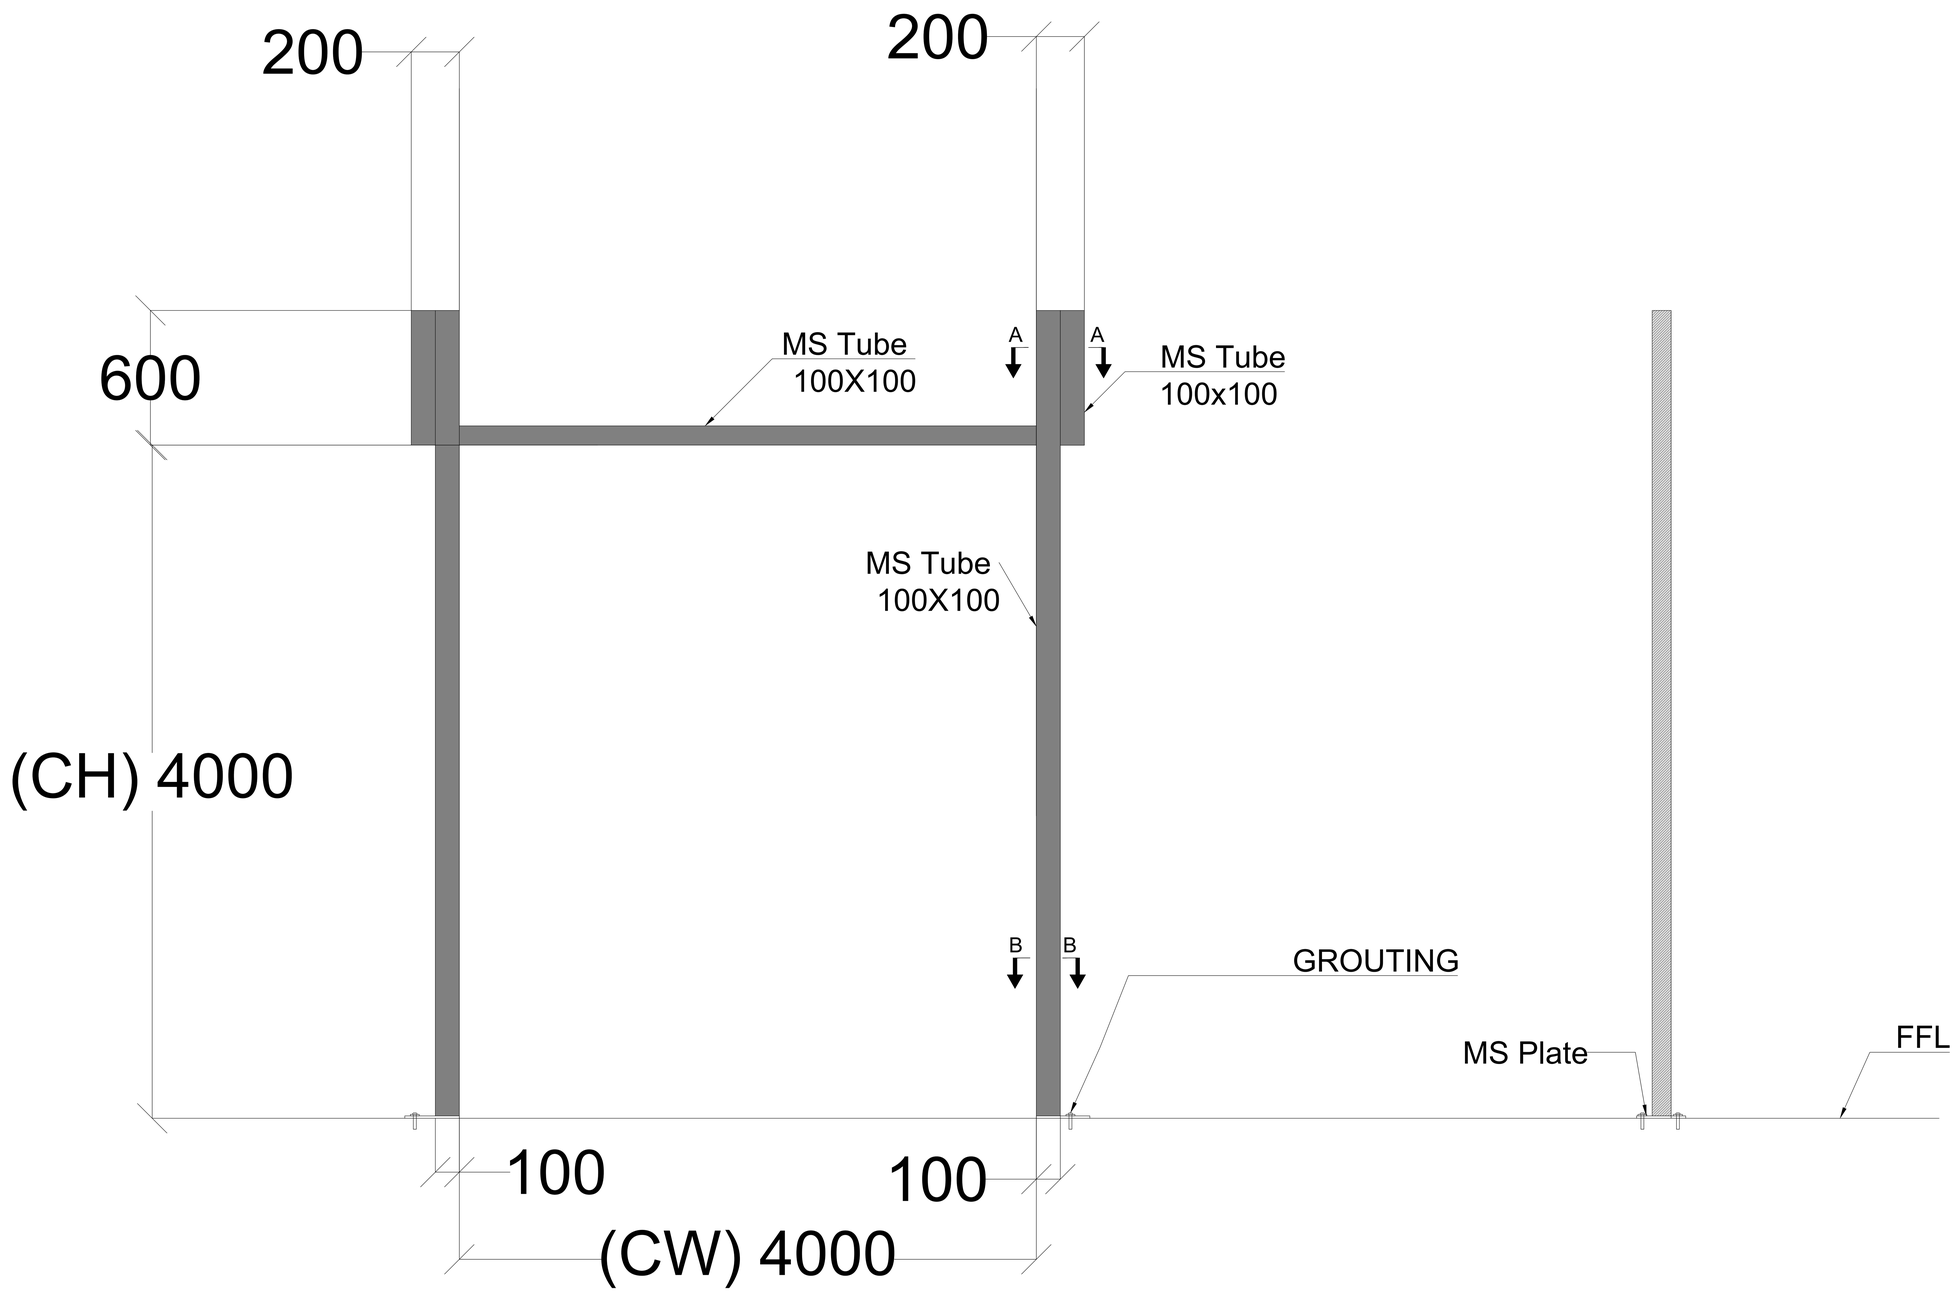


M.S. STRUCTURE DETAILS

SR.	CLEAR WIDTH	CLEAR HEIGHT	QTY.
01	4000	4000	01

This drawing & design is the property of NIHVA TECHNOLOGIES. Not to be sold or copied to any other concern.

TITLE :- SHUTTER ST.

NIHVA TECHNOLOGIES PVT. LTD. PUNE
Tel : 020 66304033
Email:- info@nihva.com
Website:- www.nihva.com

	NAME	SIGN	DATE
DRAWN	S.J.		03.10.2024
CHECK	S.W.		03.10.2024
APPRD.	V.T.		03.10.2024

CLIENT - TATA MOTOR

PROJECT - ROLLING SHUTTER ST.

FORMAT NO - NIHVA-DD-F-03

If any queries contact : projectsupport@nihva.com

DWG. NO. : NIHVA/24-25/00XX

REV- R00

ALL DIMENSION ARE IN mm

SCALE: NTS

WT:

SHEET: