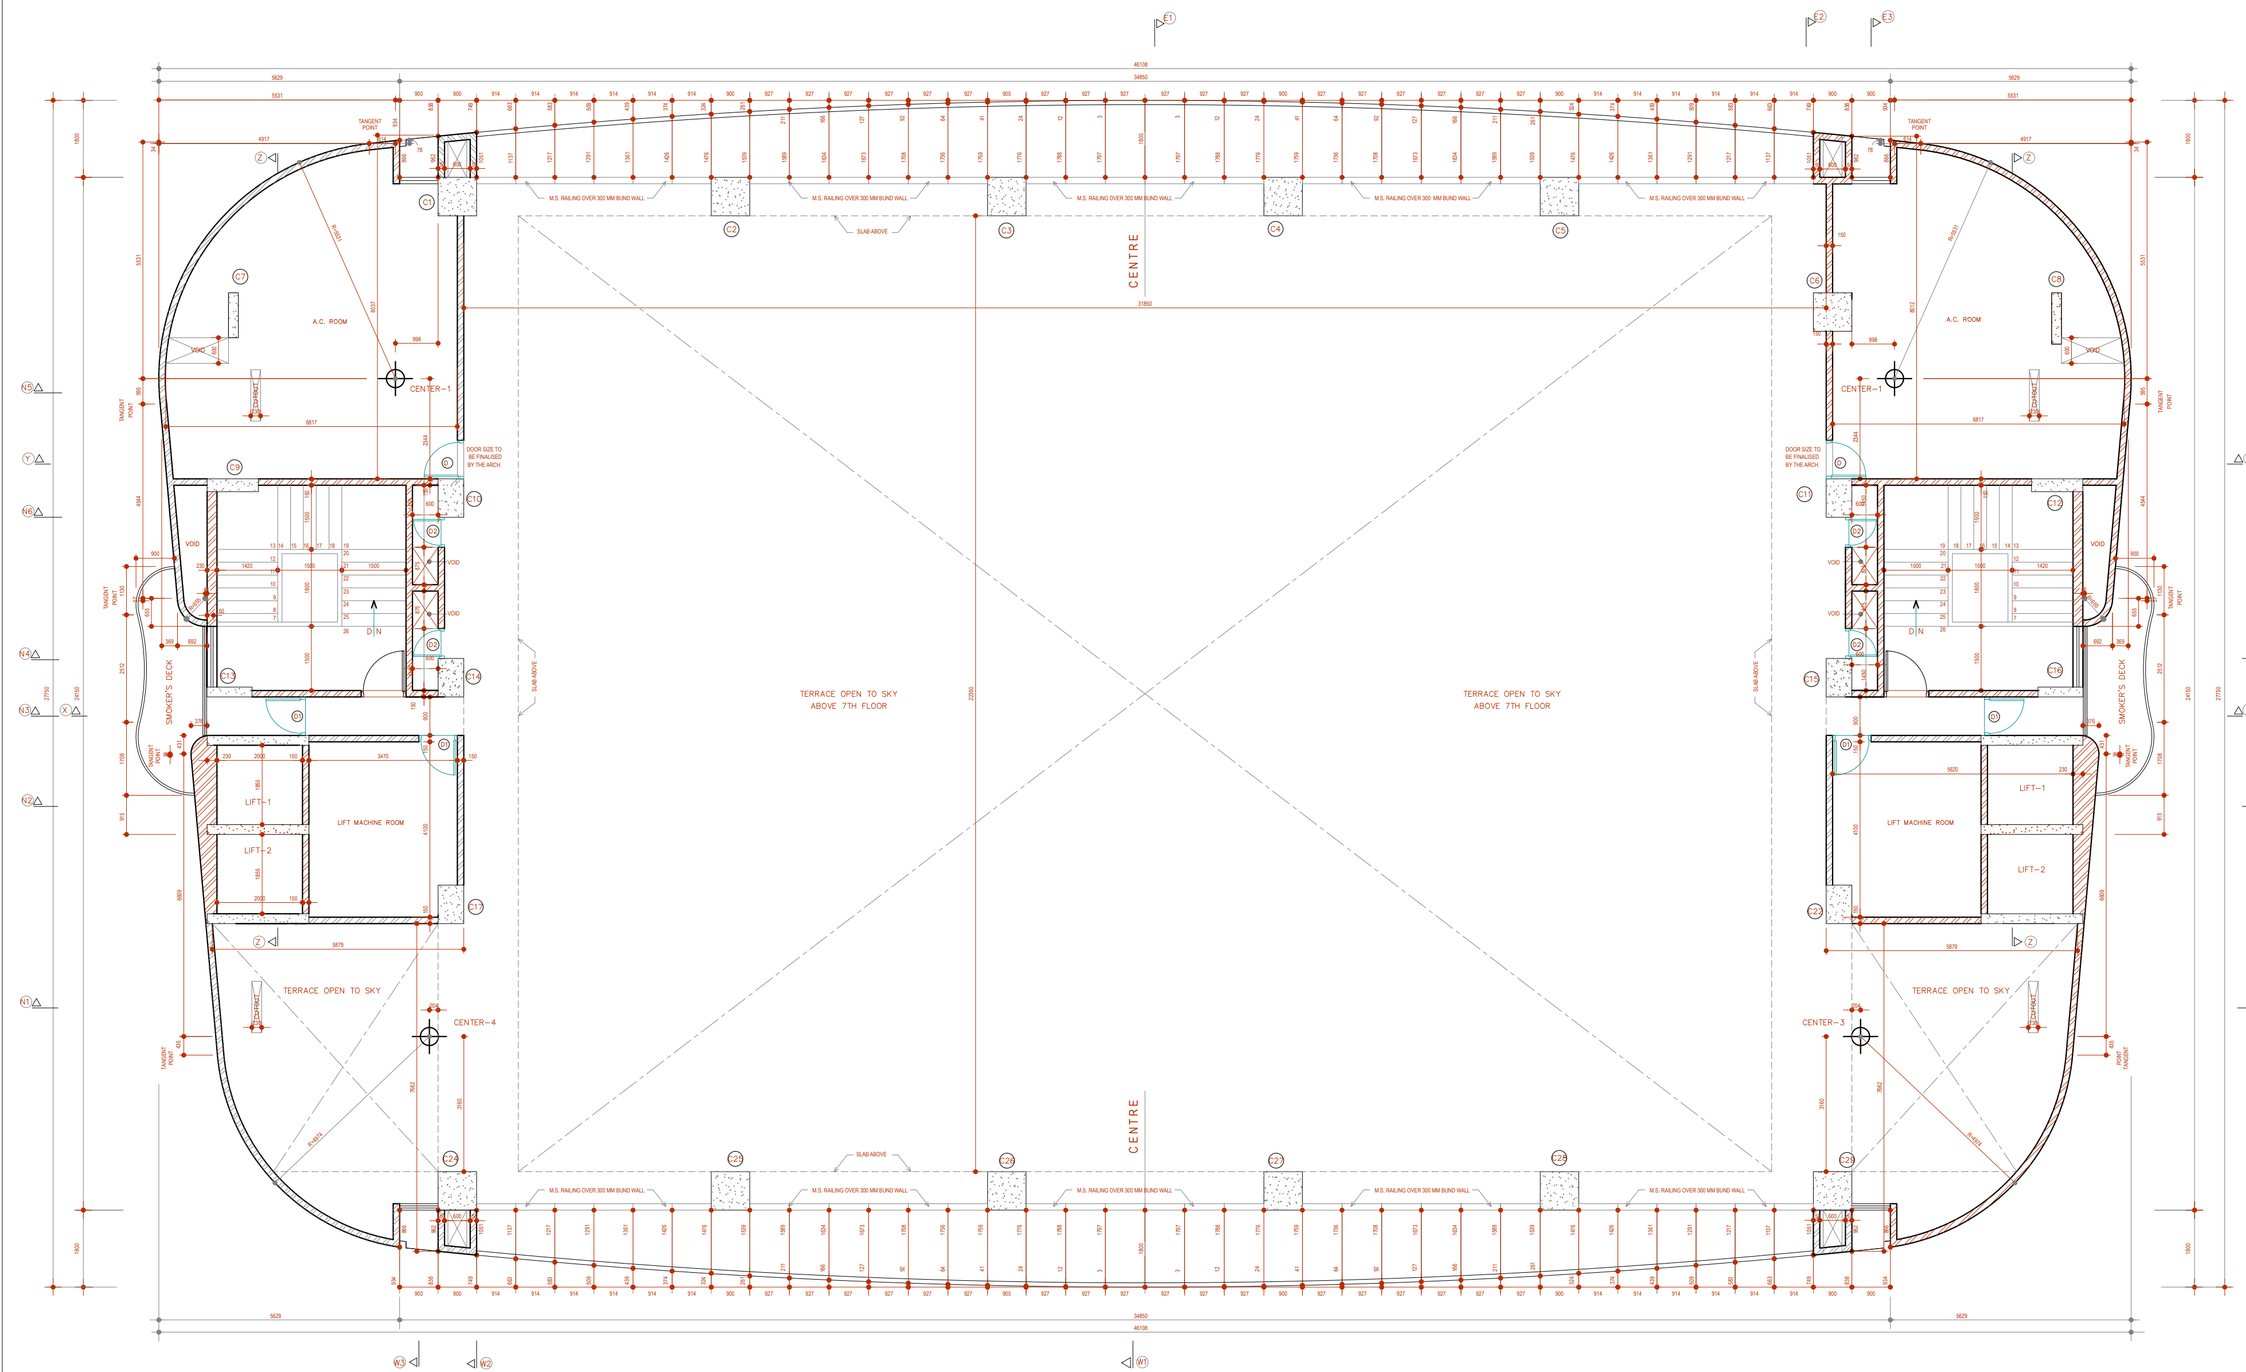


TERRACE FLOOR PLAN

REAR BLDG

SCALE= 1:50

A. GENERAL NOTES

01 ALL DIMENSIONS ARE IN MTS. & MM UNLESS SPECIFIED OTHERWISE.

02 ALL DIMENSIONS AND LEVELS ARE TO BE CHECKED AND VERIFIED BY THE SITE ENG. BEFORE EXECUTION.

03 ALL THE WORK SHOULD BE CARRIED OUT AS PER SPECIFICATIONS AND INSTRUCTIONS GIVEN BY THE ARCHITECTS.

04 ANY DESCRIPANCY IN THIS DRAWING SHOULD BE BROUGHT TO THE IMMEDIATE NOTICE OF THE ARCHITECTS OR STRUCTURAL ENGINEERS.

05 ALL INTERNAL WALLS ARE THICK EXCLUDING PLASTERING AND EXTERNAL WALLS THK EXCLUDING PLASTER.

06 THIS DRAWING IS A COPYRIGHT AND MUST NOT BE USED OR DISCLOSED OR REPRODUCED IN ANY OTHER FORM WITHOUT EXPRESS PERMISSION OF DUMASIA DESAI NANDANI ARCHITECTS

B. SPECIAL NOTES

01 ALL PROJECTIONS TO BE CHECKED WITH ARCHITECTS DRAWING AND TO BE VERIFIED OR ADJUSTED ON SITE IN CONJUNCTION WITH THE STRUCTURAL DRAWINGS.

02 THIS DRAWING IS TO BE READ IN CONJUCTION WITH THE R.C.C. CONSULTANTS DRAWING. DRG. NO.061030-B-111-COL-FTG

C. REVISIONS

REV. NO.	DESCRIPTION	DATE	SIGN
R1	CHANGE IN LVL. OF LIFT MACH. RM. FLOOR SLAB	3-9-07	
R2			
R3			

PROJECT :
PROPOSED INFORMATION TECHNOLOGY BUILDING KNOWN AS 'FLEXCEL-PARK', ON PLOT BEARING C.T.S. NO. 217/1 TO 7 S.V. ROAD, JOGESHWARI(WEST), MUMBAI 400102


FOR M/S EXCEL INDUSTRIES LTD.

TITLE
TERRACE FLOOR PLAN

I N D E X

JOB : EXCEL	DRG NO. WD/EXC/REAR/06
SCALE : 1 = 50	
DATE : 01-06-07	CADFILE :-
DRN : PRANAV	PRANAV/DDN/BANDIVALI/WD/PLAN.DWG
CHKD : P N D	LOCATION :

DUMASIA DESAI NANDANI ARCHITECTS
ARCHITECTS ENGINEERS & VALUERS
402, SAI CHAMBERS,OPP.RLY.STN.
NEHRU ROAD,SANTACRUZ (E),
MUMBAI-400 055

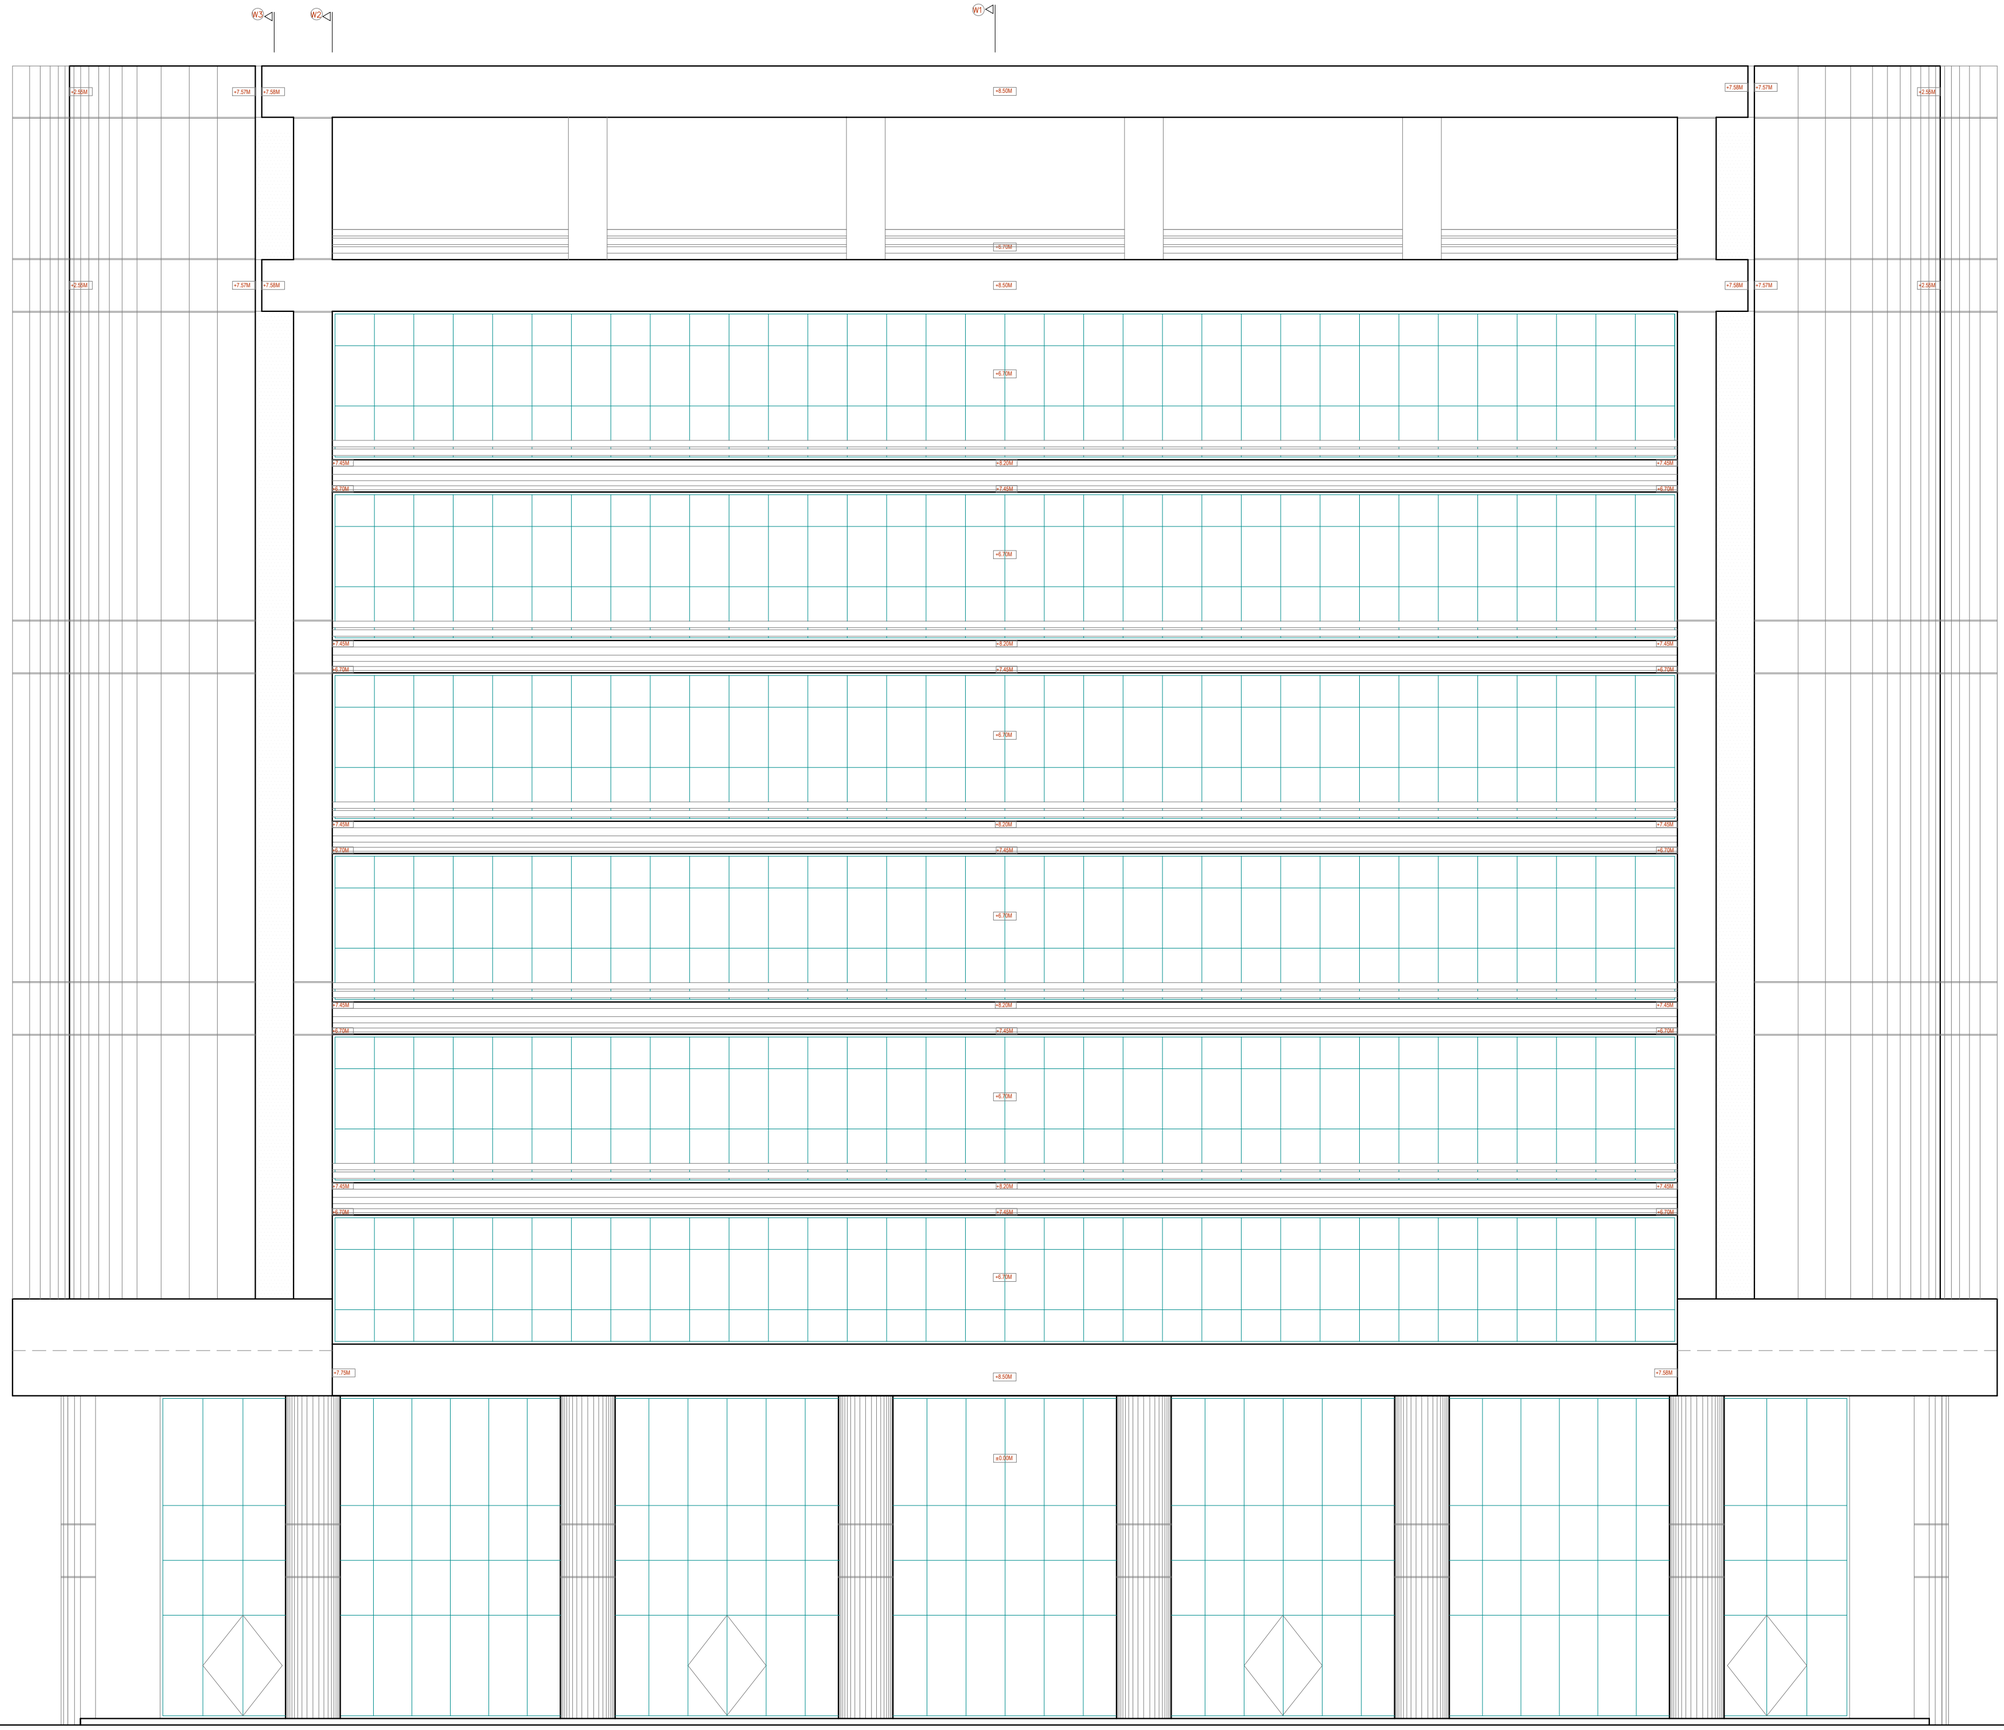

WEST SIDE ELEVATION(FRONT SIDE)

A. GENERAL NOTES

01 ALL DIMENSIONS ARE IN MTS. & MM UNLESS SPECIFIED OTHERWISE.

02 ALL DIMENSIONS AND LEVELS ARE TO BE CHECKED AND VERIFIED BY THE SITE ENG. BEFORE EXECUTION.

03 ALL THE WORK SHOULD BE CARRIED OUT AS PER SPECIFICATIONS AND INSTRUCTIONS GIVEN BY THE ARCHITECTS.

04 ANY DESCRIPANCY IN THIS DRAWING SHOULD BE BROUGHT TO THE IMMEDIATE NOTICE OF THE ARCHITECTS OR STRUCTURAL ENGINEERS.

05 ALL INTERNAL WALLS ARE 115MM THICK EXCLUDING PLASTERING AND EXTERNAL WALLS 125MM THK EXCLUDING PLASTER.

06 THIS DRAWING IS A COPYRIGHT AND MUST NOT BE USED OR DISCLOSED OR REPRODUCED IN ANY OTHER FORM WITHOUT EXPRESS PERMISSION OF DUMASIA DESAI NANDANI ARCHITECTS

B. SPECIAL NOTES

01 ALL PROJECTIONS TO BE CHECKED WITH ARCHITECTS DRAWING AND TO BE VERIFIED OR ADJUSTED ON SITE IN CONJUNCTION WITH THE STRUCTURAL DRAWINGS.

02 THIS DRAWING IS TO BE READ IN CONJUCTION WITH THE R.C.C. CONSULTANTS DRAWING. DRG. NO.061030-B-111-COL-FTG

C. REVISIONS

REV. NO.	DESCRIPTION	DATE	SIGN
R1			
R2			
R3			

PROJECT :
PROPOSED INFORMATION TECHNOLOGY BUILDING KNOWN AS "FLEXCEL-PARK", ON PLOT BEARING C.T.S. NO. 217/1 TO 7 S.V. ROAD, JOGESHWAR(WEST), MUMBAI 400102


FOR M/S EXCEL INDUSTRIES LTD.

TITLE
WEST SIDE ELEVATION

I N D E X

JOB : EXCEL	DRG NO. WD/EXC/REAR/08
SCALE : 1 = 50	
DATE : 19-09-06	CADFILE :- PRANAV/DDN/BANDIVALI/WD/PLAN.DWG
DRN : PRANAV	
CHKD : P N D	LOCATION :

DUMASIA DESAI NANDANI ARCHITECTS
ARCHITECTS ENGINEERS & VALUERS
402, SAI CHAMBERS,OPP.RLY.STN.
NEHRU ROAD,SANTACRUZ (E),
MUMBAI-400 055

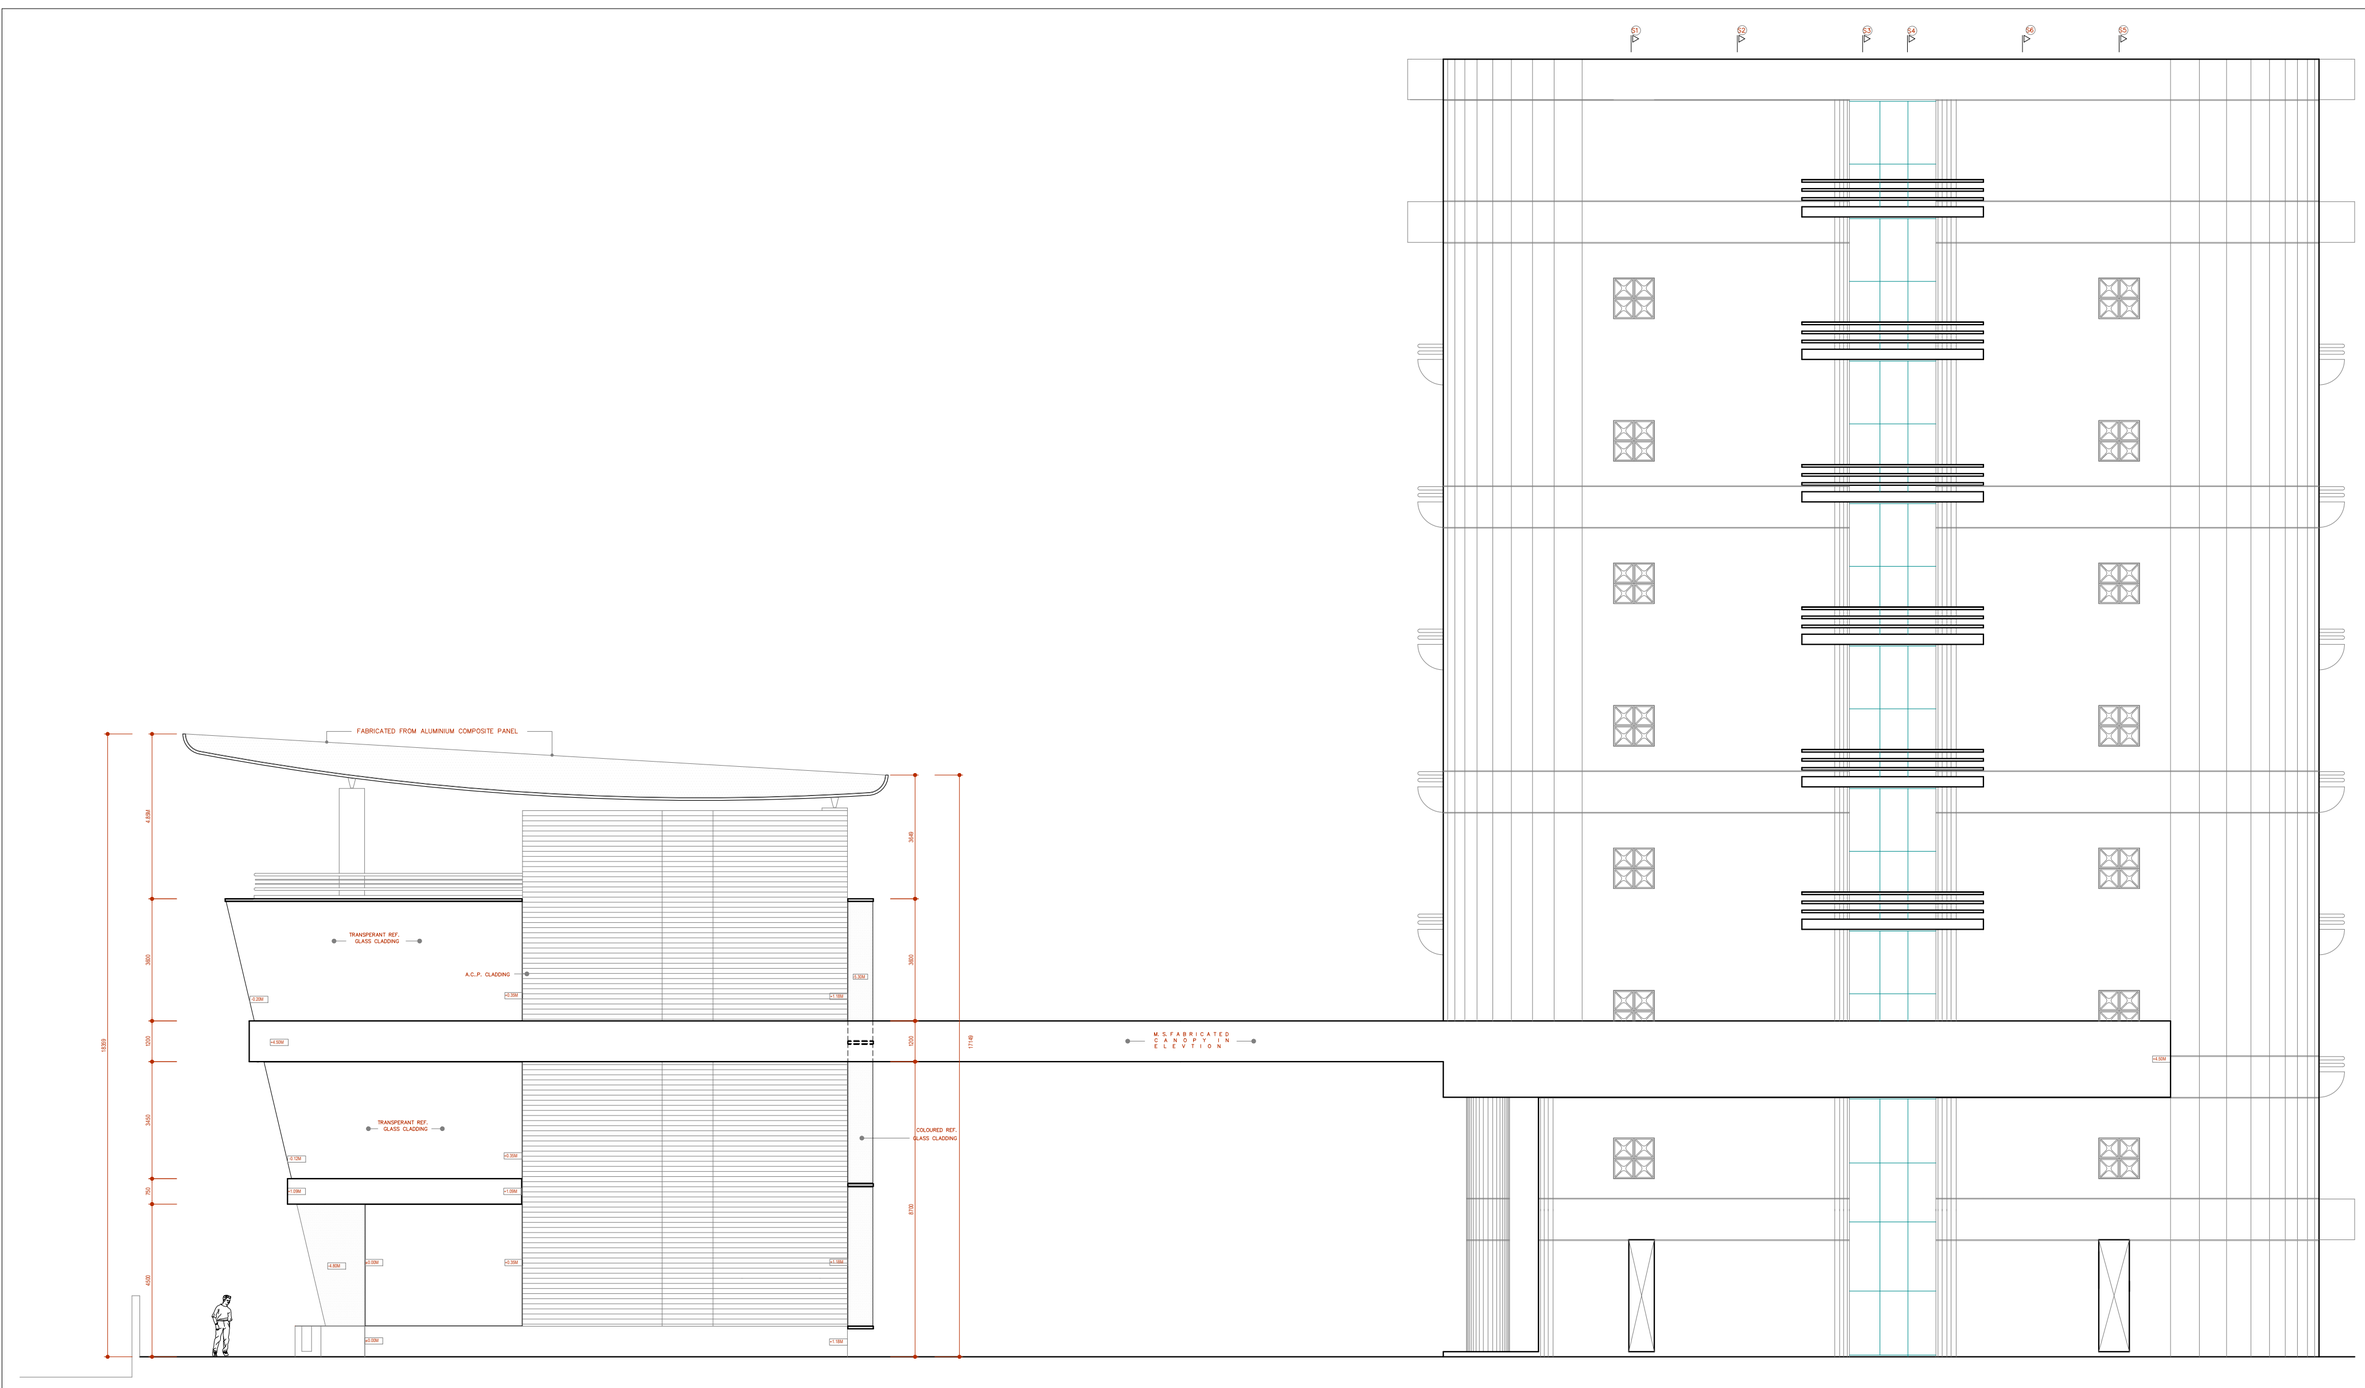

SIDE ELEVATION(SOUTH SIDE)

SCALE:- 1:50

A. GENERAL NOTES

01 ALL DIMENSIONS ARE IN METER UNLESS SPECIFIED OTHERWISE.

02 ALL DIMENSIONS AND LEVELS ARE TO BE CHECKED AND VERIFIED BY THE SITE ENG. BEFORE EXECUTION.

03 ALL THE WORK SHOULD BE CARRIED OUT AS PER SPECIFICATIONS AND INSTRUCTIONS GIVEN BY THE ARCHITECTS.

04 ANY DISCRIPANCY IN THIS DRAWING SHOULD BE BROUGHT TO THE IMMEDIATE NOTICE OF THE ARCHITECTS OR STRUCTURAL ENGINEERS.

05 ALL INTERNAL WALLS ARE 115MM THICK EXCLUDING PLASTERING AND EXTERNAL WALLS 125MM THK EXCLUDING PLASTER.

06 THIS DRAWING IS A COPYRIGHT AND MUST NOT BE USED OR DISCLOSED OR REPRODUCED IN ANY OTHER FORM WITHOUT EXPRESS PERMISSION OF DUMASIA DESAI NANDANI ARCHITECTS

B. SPECIAL NOTES

01 ALL PROJECTIONS TO BE CHECKED WITH ARCHITECTS DRAWING AND TO BE VERIFIED OR ADJUSTED ON SITE IN CONJUNCTION WITH THE STRUCTURAL DRAWINGS.

02 THIS DRAWING IS TO BE READ IN CONJUCTION WITH THE R.C.C. CONSULTANTS DRAWING.

C. REVISIONS

REC. NO.	DESCRIPTION	DATE	SIGN
R1			
R2			
R3			


PROJECT :
PROPOSED INFORMATION TECHNOLOGY BUILDING KNOWN AS "EXCEL-PARK", ON PLOT BEARING C.T.S. NO. 217/1 TO 7 S.V. ROAD, JOGESHWARI(WEST), MUMBAI 400102
FOR M/S EXCEL INDUSTRIES LTD.

TITLE
SIDE ELEVATION(SOUTH SIDE)

INDEX

JOB :- EXCEL	DRG NO.
SCALE:- 1 = 50	WD/EXC/REAR/11
DATE :- 19-09-06	CADFILE :-
DRN :- PRANAV	PRANAV/DDN/BHANVAL/WD/PLAN.DWG
CHKD :- P N D	LOCATION :-

DUMASIA DESAI NANDANI ARCHITECTS
ARCHITECTS, ENGINEERS & VALUERS
402, SAI CHAMBERS,OPP.MLY.STN.
NEHRU ROAD,SANTACRUZ (E),
MUMBAI-400 055

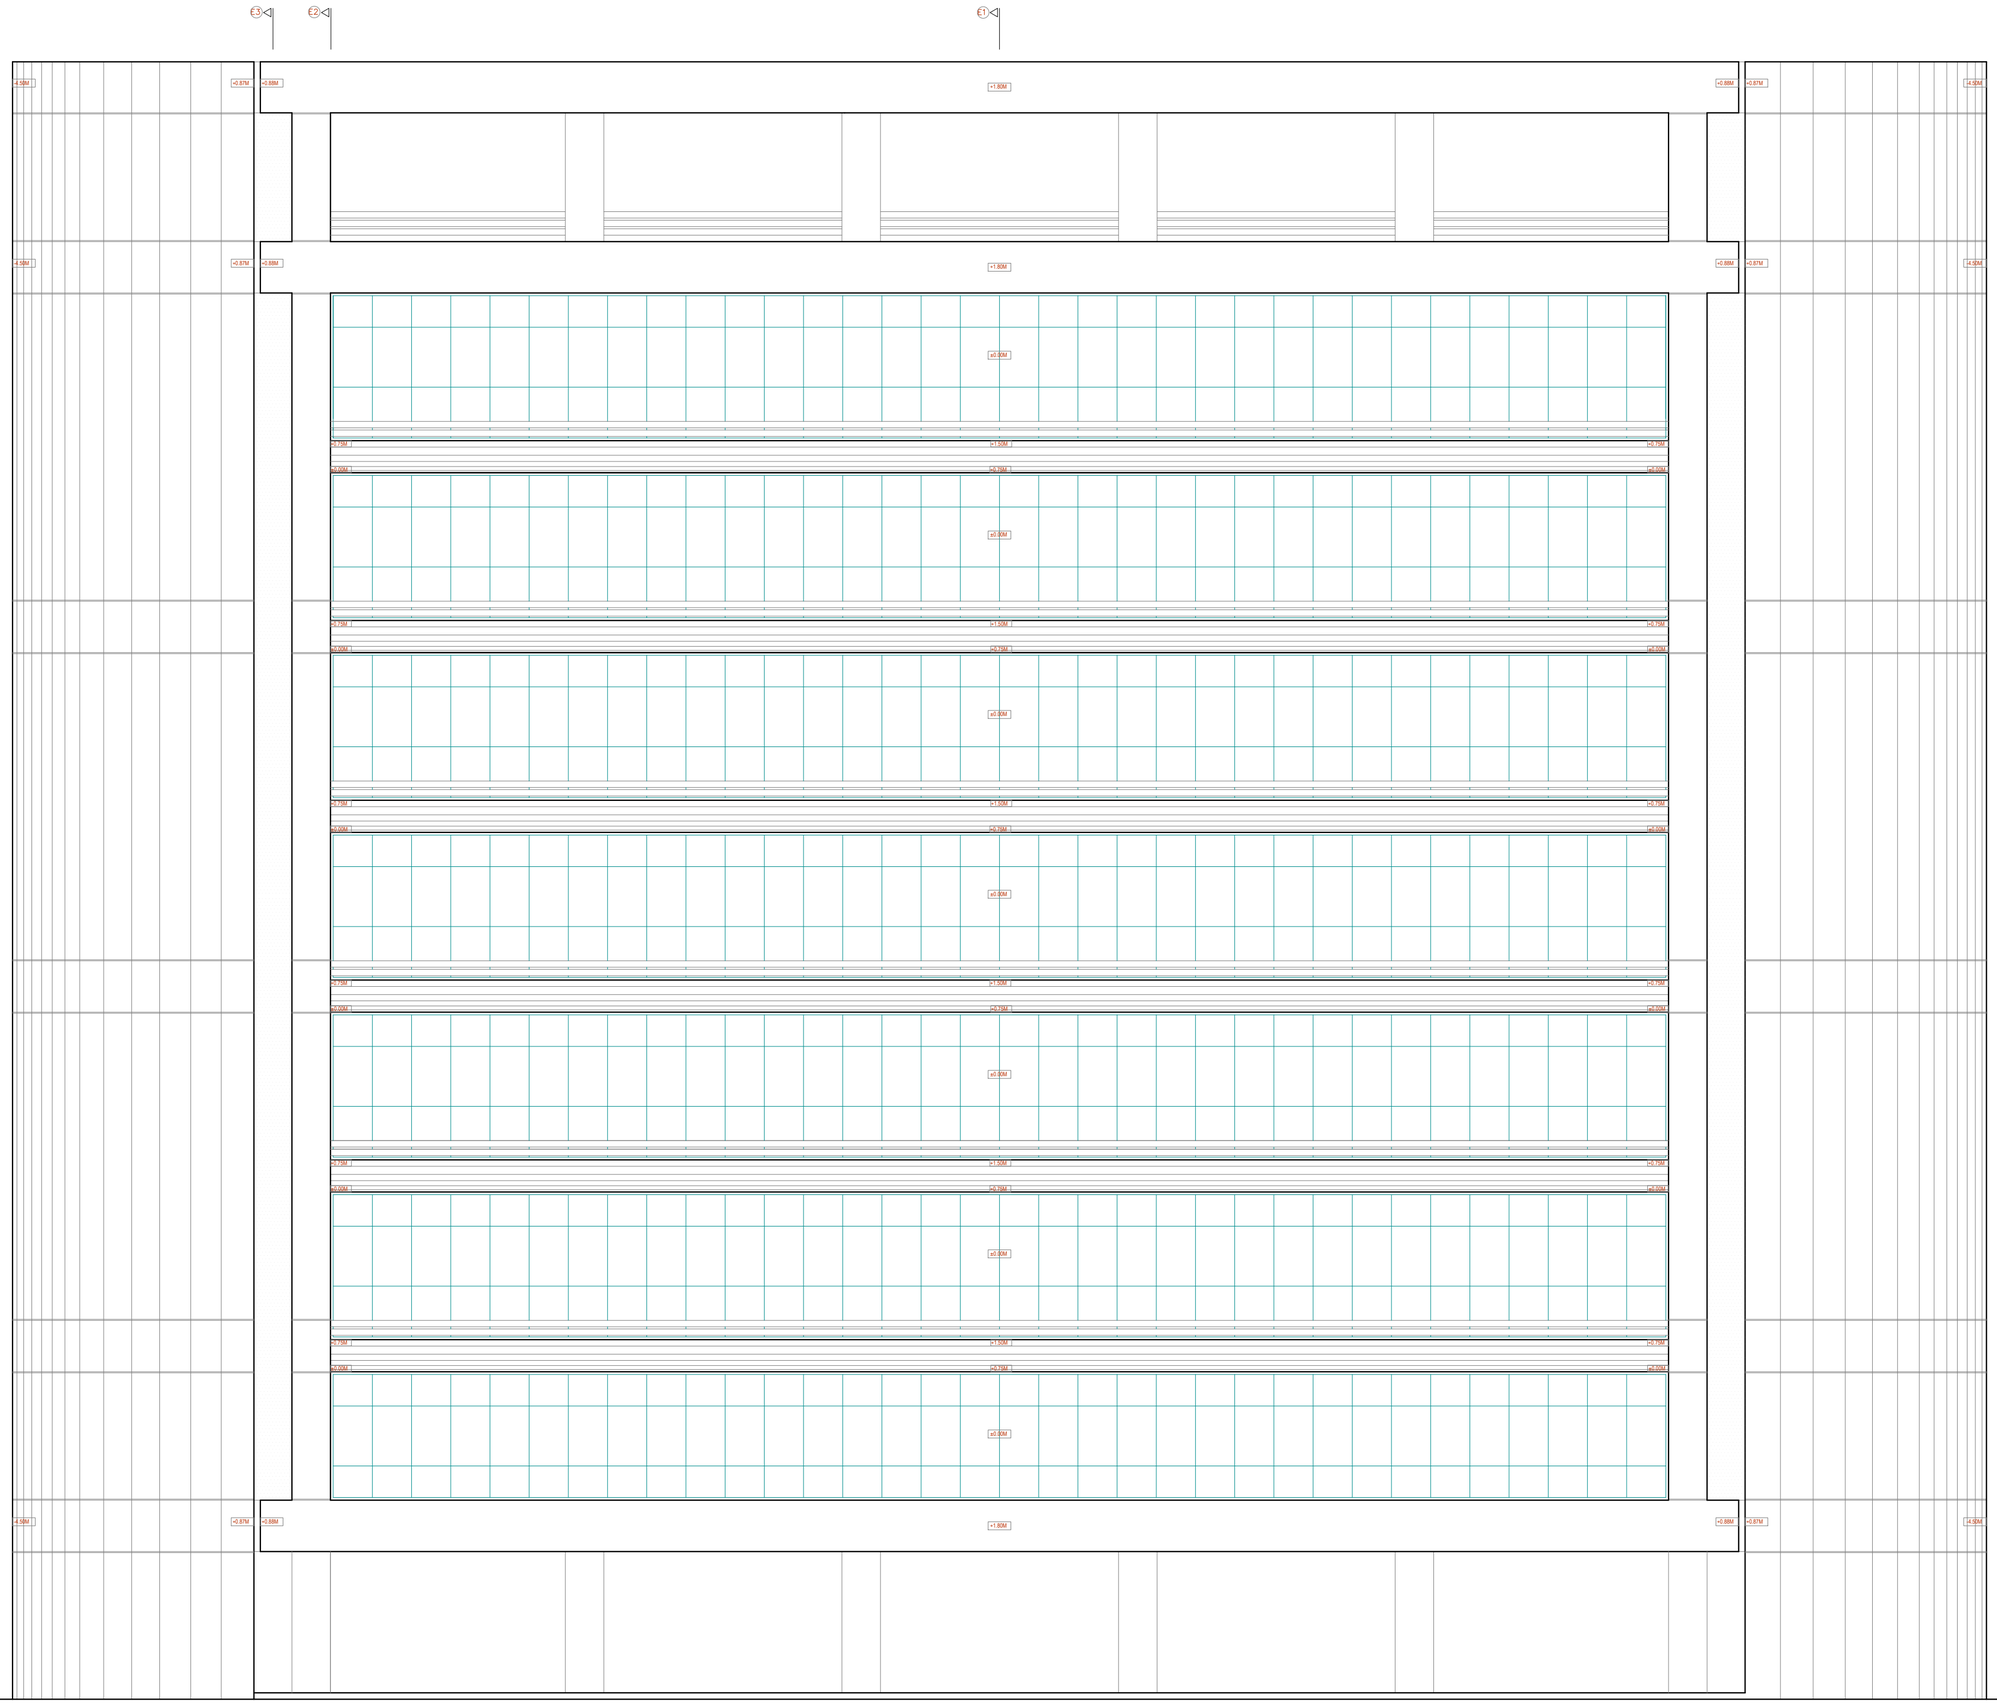

EAST SIDE ELEVATION

SCALE:- 1:50

A. GENERAL NOTES

01 ALL DIMENSIONS ARE IN MTS. & MM UNLESS SPECIFIED OTHERWISE.

02 ALL DIMENSIONS AND LEVELS ARE TO BE CHECKED AND VERIFIED BY THE SITE ENG. BEFORE EXECUTION.

03 ALL THE WORK SHOULD BE CARRIED OUT AS PER SPECIFICATIONS AND INSTRUCTIONS GIVEN BY THE ARCHITECTS.

04 ANY DESCRIPANCY IN THIS DRAWING SHOULD BE BROUGHT TO THE IMMEDIATE NOTICE OF THE ARCHITECTS OR STRUCTURAL ENGINEERS.

05 ALL INTERNAL WALLS ARE 115MM THICK EXCLUDING PLASTERING AND EXTERNAL WALLS 125MM THK EXCLUDING PLASTER.

06 THIS DRAWING IS A COPYRIGHT AND MUST NOT BE USED OR DISCLOSED OR REPRODUCED IN ANY OTHER FORM WITHOUT EXPRESS PERMISSION OF DUMASIA DESAI NANDANI ARCHITECTS

B. SPECIAL NOTES

01 ALL PROJECTIONS TO BE CHECKED WITH ARCHITECTS DRAWING AND TO BE VERIFIED OR ADJUSTED ON SITE IN CONJUNCTION WITH THE STRUCTURAL DRAWINGS.

02 THIS DRAWING IS TO BE READ IN CONJUCTION WITH THE R.C.C. CONSULTANTS DRAWING. DRG. NO.061030-B-111-COL-FTG

C. REVISIONS

REV. NO.	DESCRIPTION	DATE	SIGN
R1			
R2			
R3			

PROJECT :
PROPOSED INFORMATION TECHNOLOGY BUILDING KNOWN AS 'FLEXCEL-PARK', ON PLOT BEARING C.T.S. NO. 217/1 TO 7 S.V. ROAD, JOGESHWARI(WEST), MUMBAI 400102


FOR M/S EXCEL INDUSTRIES LTD.

TITLE
EAST SIDE ELEVATION

I N D E X

JOB : EXCEL	DRG NO. WD/EXC/REAR/10
SCALE : 1 = 50	
DATE : 19-09-06	CADFILE :- PRANAV/DDN/BANDIVALI/WD/PLAN.DWG
DRN : PRANAV	
CHKD: P N D	LOCATION :

DUMASIA DESAI NANDANI ARCHITECTS
ARCHITECTS ENGINEERS & VALUERS
402, SAI CHAMBERS,OPP.RLY.STN.
NEHRU ROAD,SANTACRUZ (E),
MUMBAI-400 055

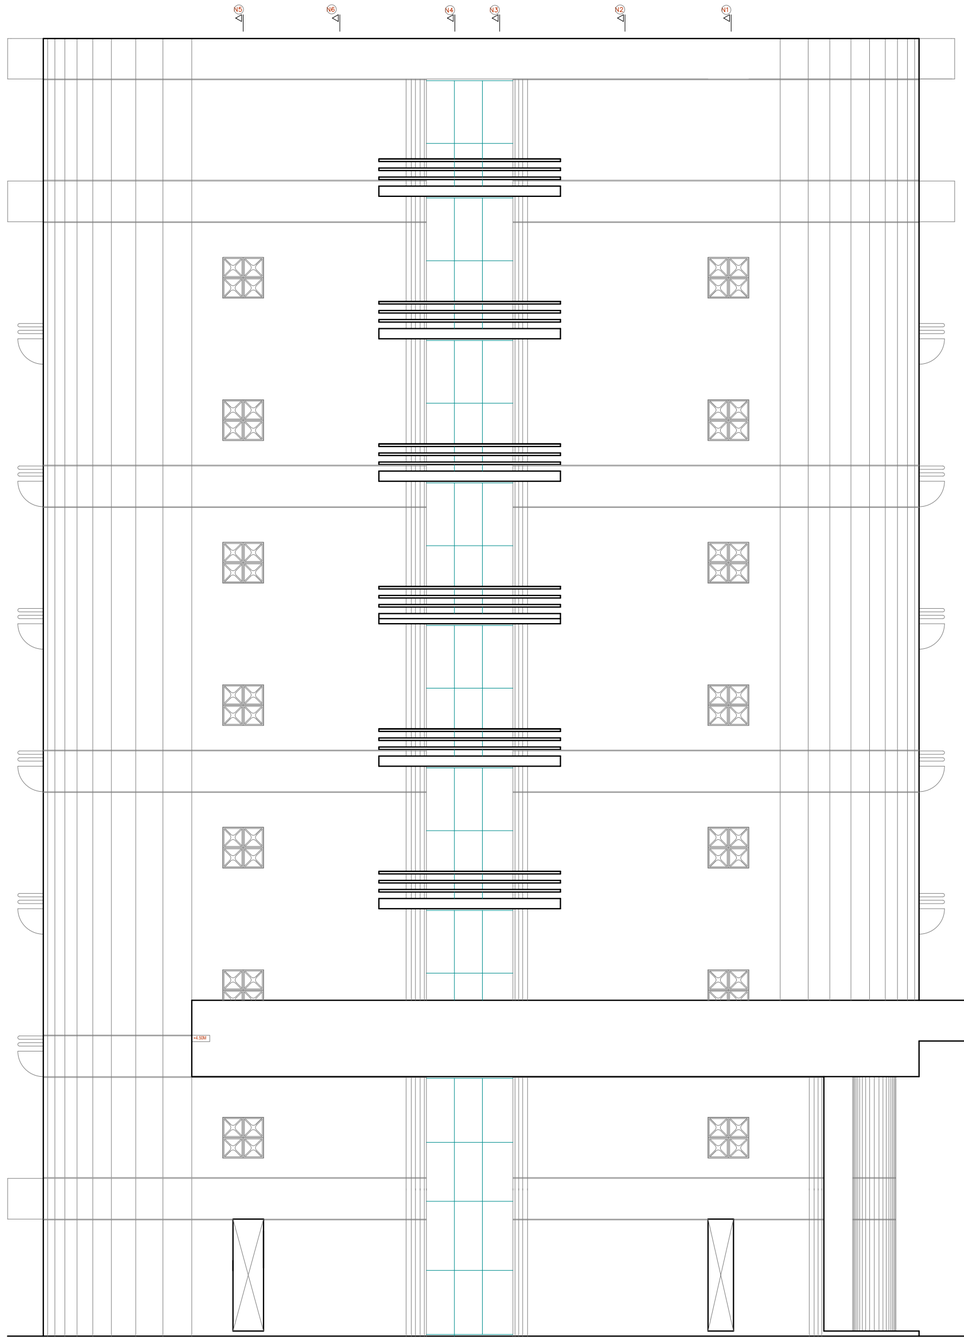

A. GENERAL NOTES

01 ALL DIMENSIONS ARE IN METER UNLESS SPECIFIED OTHERWISE.

02 ALL DIMENSIONS AND LEVELS ARE TO BE CHECKED AND VERIFIED BY THE SITE ENG. BEFORE EXECUTION.

03 ALL THE WORK SHOULD BE CARRIED OUT AS PER SPECIFICATIONS AND INSTRUCTIONS GIVEN BY THE ARCHITECTS.

04 ANY DESCRIPANCY IN THIS DRAWING SHOULD BE BROUGHT TO THE IMMEDIATE NOTICE OF THE ARCHITECTS OR STRUCTURAL ENGINEERS.

05 ALL INTERNAL WALLS ARE 115MM THICK EXCLUDING PLASTERING AND EXTERNAL WALLS 125MM THK EXCLUDING PLASTER.

06 THIS DRAWING IS A COPYRIGHT AND MUST NOT BE USED OR DISCLOSED OR REPRODUCED IN ANY OTHER FORM WITHOUT EXPRESS PERMISSION OF DUMASIA DESAI NANDANI ARCHITECTS

B. SPECIAL NOTES

01 ALL PROJECTIONS TO BE CHECKED WITH ARCHITECTS DRAWING AND TO BE VERIFIED OR ADJUSTED ON SITE IN CONJUNCTION WITH THE STRUCTURAL DRAWINGS.

02 . THIS DRAWING IS TO BE READ IN CONJUCTION WITH THE R.C.C. CONSULTANTS DRAWING.

C. REVISIONS

REV. NO.	DESCRIPTION	DATE	SIGN.
R1			
R2			
R3			

PROJECT :
PROPOSED INFORMATION TECHNOLOGY BUILDING KNOWN AS "EXCEL-I-PARK", ON PLOT BEARING C.T.S. NO. 217/1 TO 7 S.V. ROAD, JOGESHWARI(WEST), MUMBAI 400102

FOR M/S EXCEL INDUSTRIES LTD.


TITLE
SIDE ELEVATION(NORTH SIDE)

I N D E X


JOB : EXCEL	DRG NO.
SCALE: 1 = 50	WD/EXC/REAR/09
DATE : 19-09-06	CADFILE :-
DRN : PRANAV	PRANAV/DDN/BHANDALI/WD/PLANDWG
CHKD : P N D	LOCATION :

DUMASIA DESAI NANDANI ARCHITECTS
ARCHITECTS-ENGINEERS & VALUERS
A-WING, 4TH FLOOR, OPP.M.T.NL.
NEHRU ROAD,SANTACRUZ (E),
MUMBAI-400 055


SIDE ELEVATION(NORTH SIDE)
SCALE:- 1:50

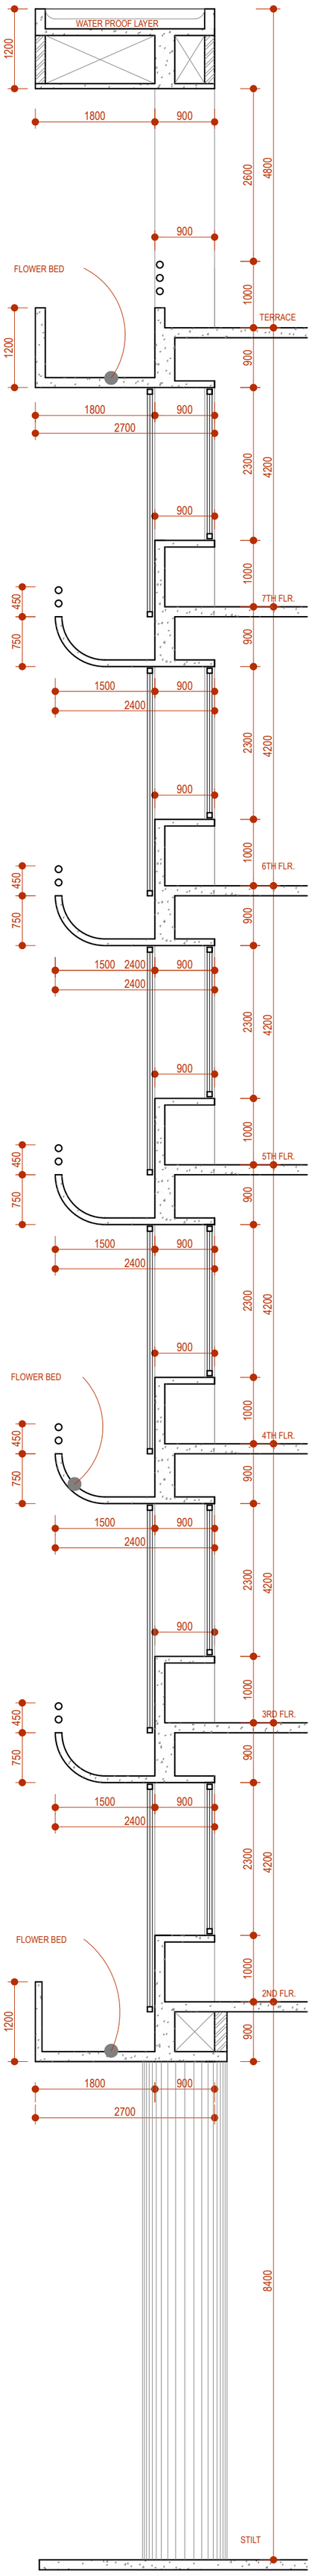

SECTION – W1

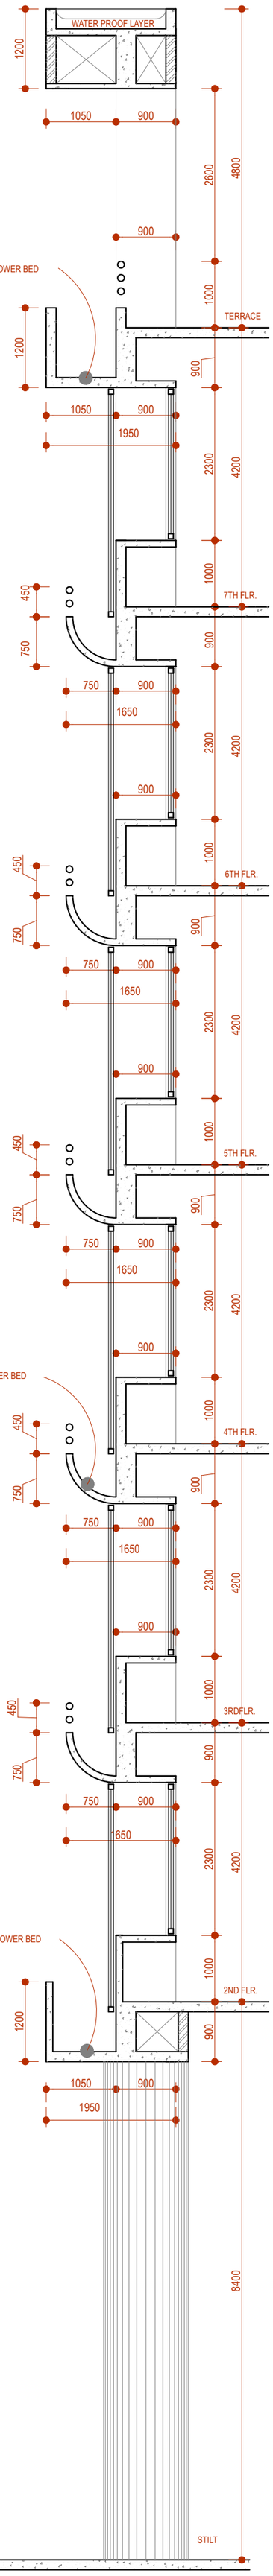

SECTION – W2

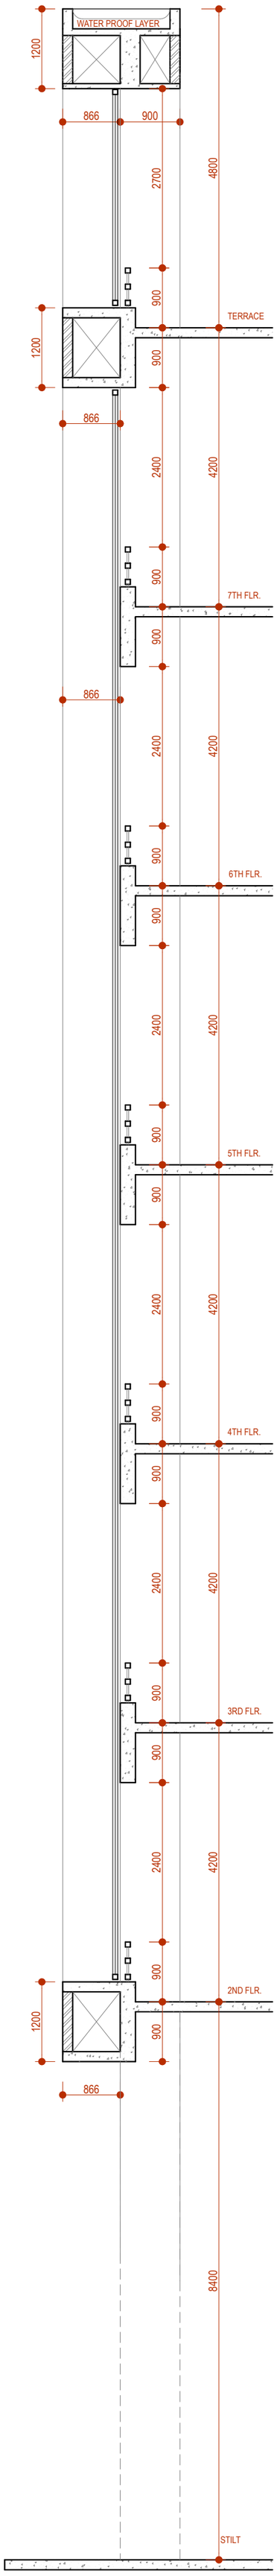

SECTION – W3

A. GENERAL NOTES

01 ALL DIMENSIONS ARE IN MTS. & MM UNLESS SPECIFIED OTHERWISE.

02 ALL DIMENSIONS AND LEVELS ARE TO BE CHECKED AND VERIFIED BY THE SITE ENG. BEFORE EXECUTION.

03 ALL THE WORK SHOULD BE CARRIED OUT AS PER SPECIFICATIONS AND INSTRUCTIONS GIVEN BY THE ARCHITECTS.

04 ANY DESCRIPANCY IN THIS DRAWING SHOULD BE BROUGHT TO THE IMMEDIATE NOTICE OF THE ARCHITECTS OR STRUCTURAL ENGINEERS.

05 ALL INTERNAL WALLS ARE 115MM THICK EXCLUDING PLASTERING AND EXTERNAL WALLS 125MM THK EXCLUDING PLASTER.

06 THIS DRAWING IS A COPYRIGHT AND MUST NOT BE USED OR DISCLOSED OR REPRODUCED IN ANY OTHER FORM WITHOUT EXPRESS PERMISSION OF DUMASIA DESAI NANDANI ARCHITECTS

B. SPECIAL NOTES

01 ALL PROJECTIONS TO BE CHECKED WITH ARCHITECTS DRAWING AND TO BE VERIFIED OR ADJUSTED ON SITE IN CONJUNCTION WITH THE STRUCTURAL DRAWINGS.

02 . THIS DRAWING IS TO BE READ IN CONJUCTION WITH THE R.C.C. CONSULTANTS DRAWING. DRG. NO. 061030–B–111–COL–FTG

C. REVISIONS

REV. NO.	DESCRIPTION	DATE	SIGN
R1			
R2			
R3			

PROJECT :
PROPOSED INFORMATION TECHNOLOGY BUILDING KNOWN AS 'FLEXCEL–PARK', ON PLOT BEARING C.T.S. NO. 217/1 TO 7 S.V. ROAD, JOGESHWARI(WEST), MUMBAI 400102


FOR M/S EXCEL INDUSTRIES LTD.

TITLE
WALL SECTIONS W1 TO W3(WEST SIDE)


I N D E X

JOB : EXCEL	DRG NO. : WD/EXC/REAR/12
SCALE : 1 = 50	
DATE : 28/08/07	CADFILE :– PRANAV/DDN/BANDIVALI/WD/PLAN.DWG
DRN : PRANAV	
CHKD : P N D	LOCATION :


DUMASIA DESAI NANDANI
ARCHITECTS
ARCHITECTS ENGINEERS & VALUERS
402, SAI CHAMBERS,OPP.RLY.STN.
NEHRU ROAD,SANTACRUZ (E),
MUMBAI–400 055

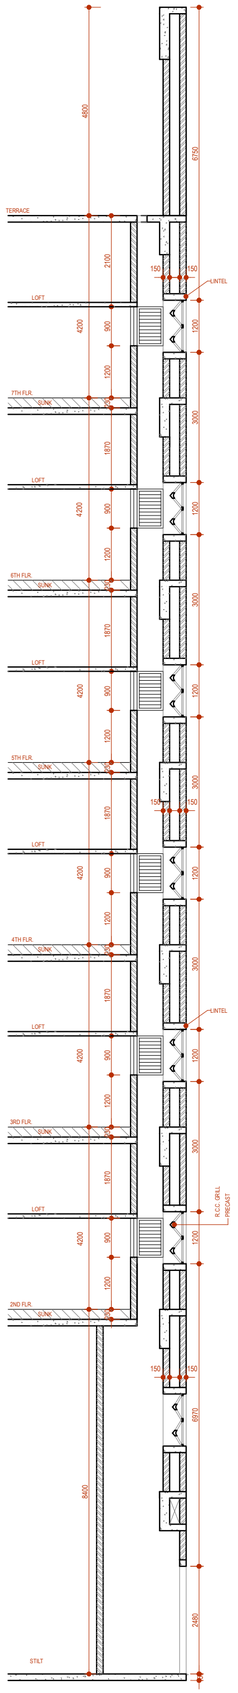


SECTION–S1

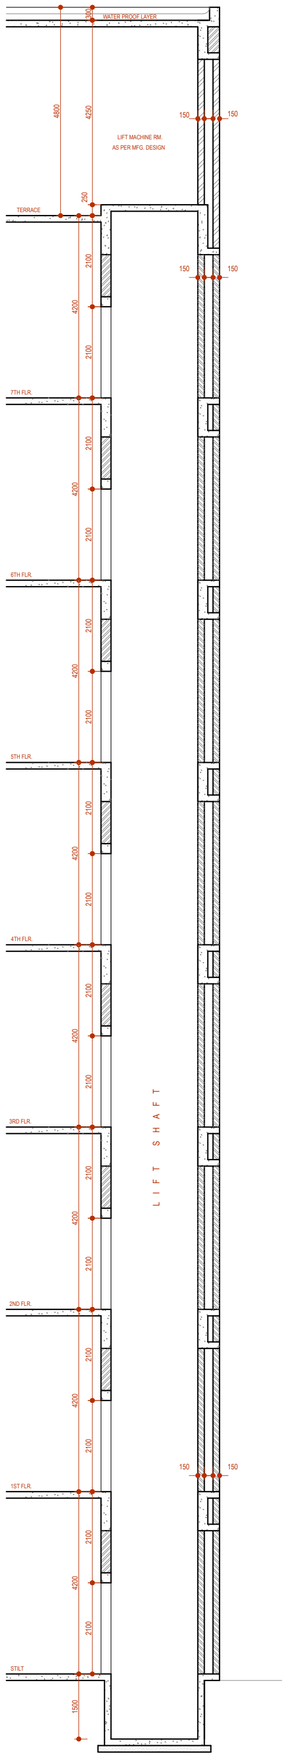


SECTION–S2

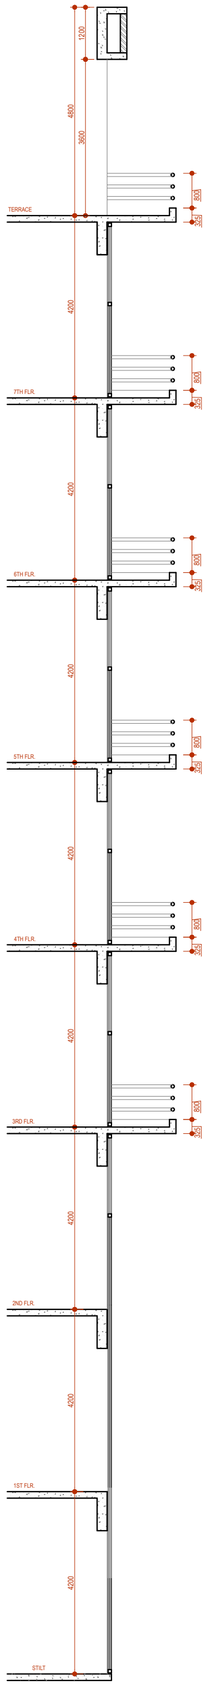


SECTION–S3

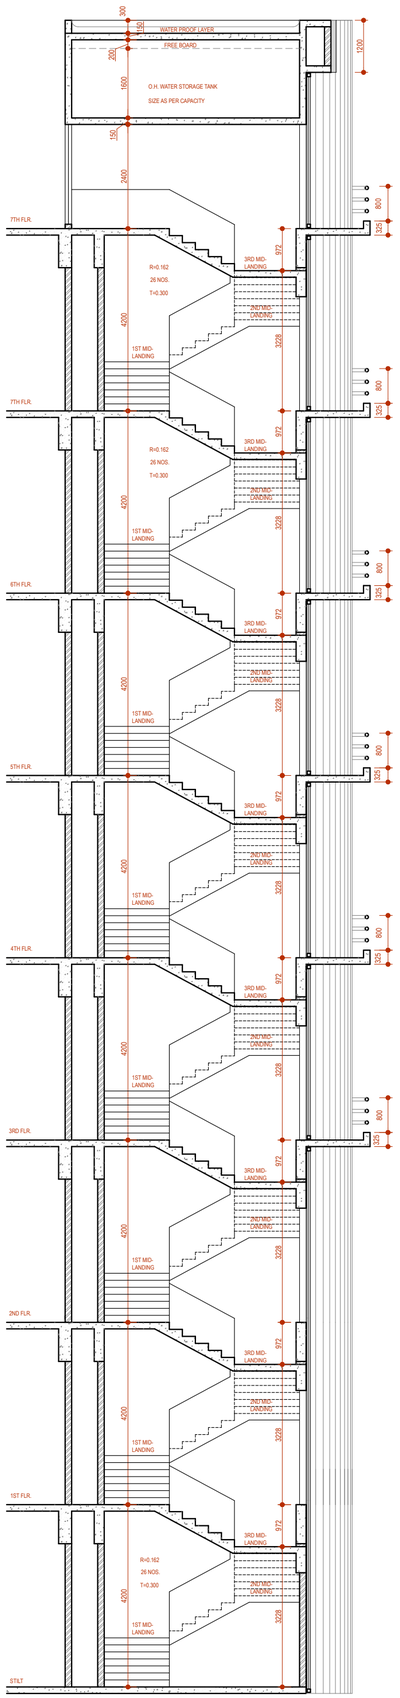

SECTION–S4

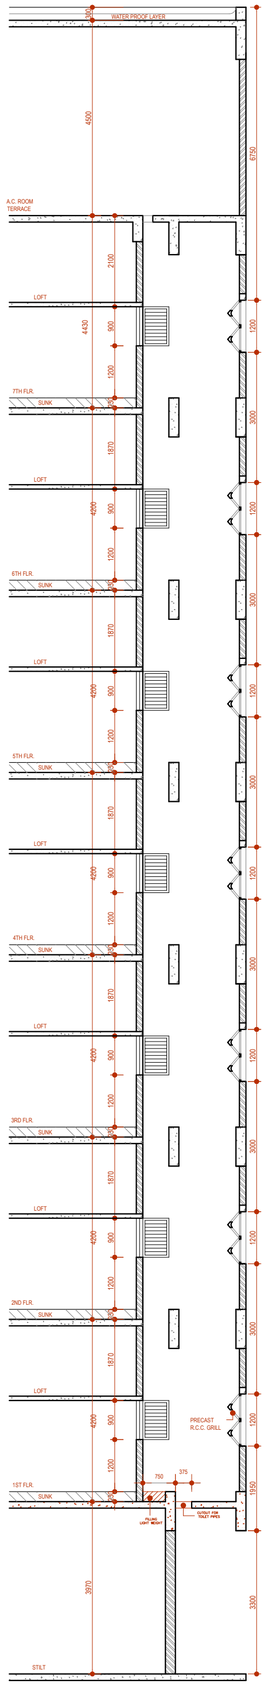

SECTION–S5

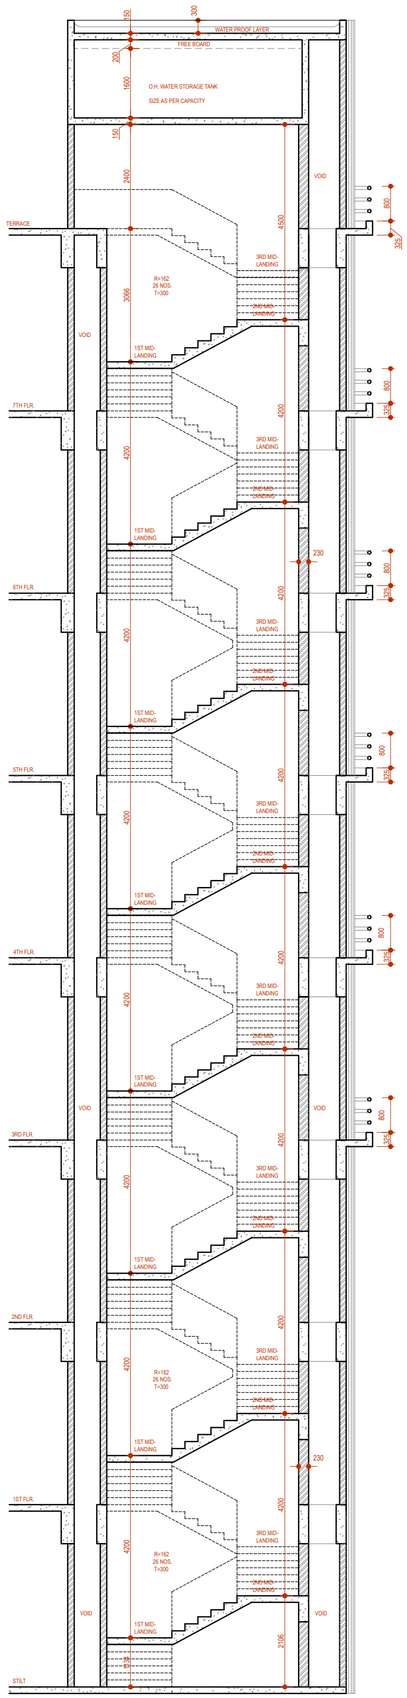

SECTION–S6

A. GENERAL NOTES

01 ALL DIMENSIONS ARE IN MTS. & MM UNLESS SPECIFIED OTHERWISE.

02 ALL DIMENSIONS AND LEVELS ARE TO BE CHECKED AND VERIFIED BY THE SITE ENG. BEFORE EXECUTION.

03 ALL THE WORK SHOULD BE CARRIED OUT AS PER SPECIFICATIONS AND INSTRUCTIONS GIVEN BY THE ARCHITECTS.

04 ANY DESCRIPANCY IN THIS DRAWING SHOULD BE BROUGHT TO THE IMMEDIATE NOTICE OF THE ARCHITECTS OR STRUCTURAL ENGINEERS.

05 ALL INTERNAL WALLS ARE 115MM THICK EXCLUDING PLASTERING AND EXTERNAL WALLS 125MM THK EXCLUDING PLASTER.

06 THIS DRAWING IS A COPYRIGHT AND MUST NOT BE USED OR DISCLOSED OR REPRODUCED IN ANY OTHER FORM WITHOUT EXPRESS PERMISSION OF DUMASIA DESAI NANDANI ARCHITECTS

B. SPECIAL NOTES

01 ALL PROJECTIONS TO BE CHECKED WITH ARCHITECTS DRAWING AND TO BE VERIFIED OR ADJUSTED ON SITE IN CONJUNCTION WITH THE STRUCTURAL DRAWINGS.

02 . THIS DRAWING IS TO BE READ IN CONJUCTION WITH THE R.C.C. CONSULTANTS DRAWING. DRG. NO.061030–B–111–COL–FTG

C. REVISIONS

REV. NO.	DESCRIPTION	DATE	SIGN
R1			
R2			
R3			

PROJECT :
PROPOSED INFORMATION TECHNOLOGY BUILDING KNOWN AS 'FLEXCEL–PARK', ON PLOT BEARING C.T.S. NO. 217/1 TO 7 S.V. ROAD, JOGESHWARI(WEST), MUMBAI 400102


FOR M/S EXCEL INDUSTRIES LTD.

TITLE
WALL SECTIONS S1 TO S6(SOUTH SIDE)


INDEX

JOB : EXCEL	DRG NO. WD/EXC/REAR/15
SCALE : 1 = 50	
DATE : 27/08/07	CADFILE :– PRANAV/DDN/BANDVALI/WD/PLAN.DWG
DRN : PRANAV	
CHKD : P N D	LOCATION :


DUMASIA DESAI NANDANI ARCHITECTS
ARCHITECTS ENGINEERS & VALUERS
402, SAI CHAMBERS,OPP.RLY.STN.
NEHRU ROAD,SANTACRUZ (E).
MUMBAI–400 055

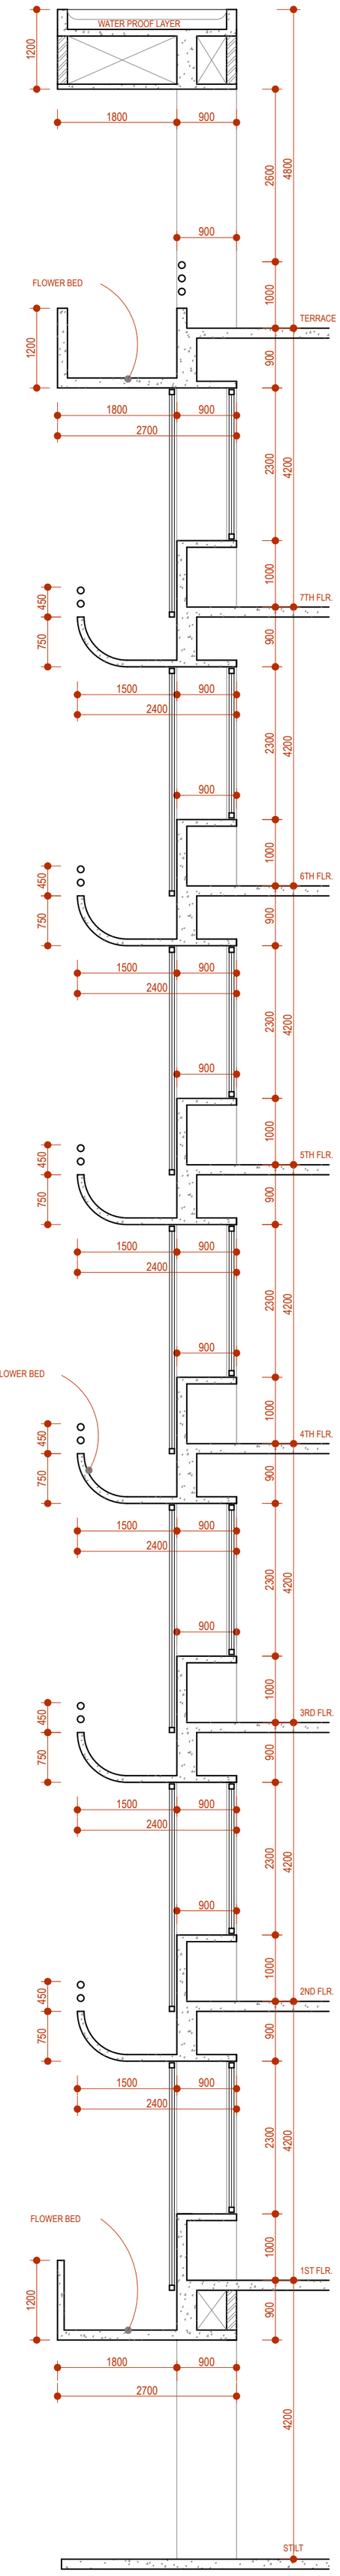

SECTION–E1

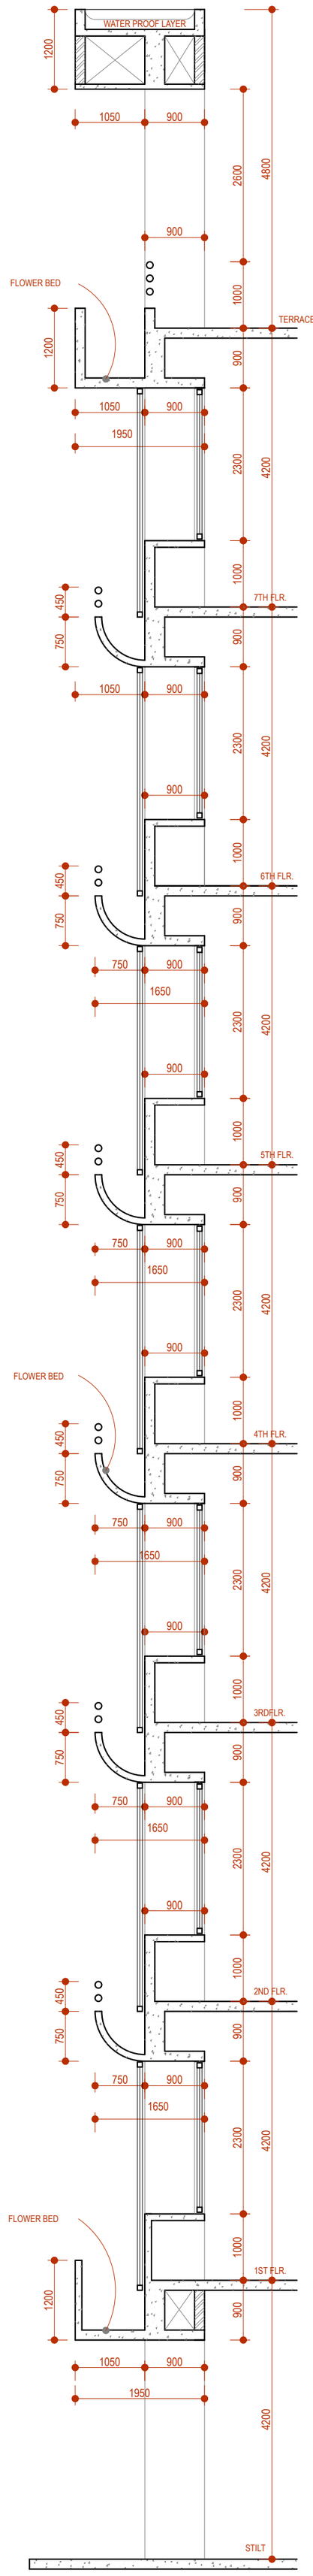

SECTION–E2

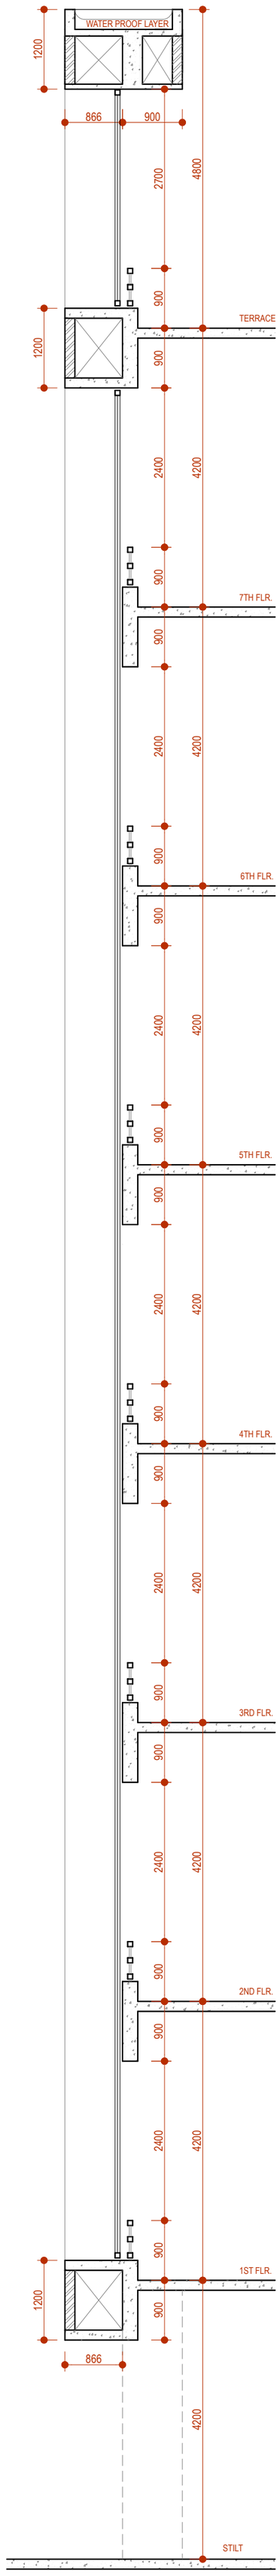

SECTION–E3

A. GENERAL NOTES

01 ALL DIMENSIONS ARE IN MTS. & MM UNLESS SPECIFIED OTHERWISE.

02 ALL DIMENSIONS AND LEVELS ARE TO BE CHECKED AND VERIFIED BY THE SITE ENG. BEFORE EXECUTION.

03 ALL THE WORK SHOULD BE CARRIED OUT AS PER SPECIFICATIONS AND INSTRUCTIONS GIVEN BY THE ARCHITECTS.

04 ANY DESCRIPANCY IN THIS DRAWING SHOULD BE BROUGHT TO THE IMMEDIATE NOTICE OF THE ARCHITECTS OR STRUCTURAL ENGINEERS.

05 ALL INTERNAL WALLS ARE 115MM THICK EXCLUDING PLASTERING AND EXTERNAL WALLS 125MM THK EXCLUDING PLASTER.

06 THIS DRAWING IS A COPYRIGHT AND MUST NOT BE USED OR DISCLOSED OR REPRODUCED IN ANY OTHER FORM WITHOUT EXPRESS PERMISSION OF DUMASIA DESAI NANDANI ARCHITECTS

B. SPECIAL NOTES

01 ALL PROJECTIONS TO BE CHECKED WITH ARCHITECTS DRAWING AND TO BE VERIFIED OR ADJUSTED ON SITE IN CONJUNCTION WITH THE STRUCTURAL DRAWINGS.

02 . THIS DRAWING IS TO BE READ IN CONJUCTION WITH THE R.C.C. CONSULTANTS DRAWING. DRG. NO.061030–B–111–COL–FTG

C. REVISIONS

REV. NO.	DESCRIPTION	DATE	SIGN
R1			
R2			
R3			

PROJECT :
PROPOSED INFORMATION TECHNOLOGY BUILDING KNOWN AS 'FLEXCEL–PARK', ON PLOT BEARING C.T.S. NO. 217/1 TO 7 S.V. ROAD, JOGESHWARI(WEST), MUMBAI 400102


FOR M/S EXCEL INDUSTRIES LTD.

TITLE
WALL SECTIONS E1 TO E3(EAST SIDE)


I N D E X

JOB : EXCEL	DRG NO. WD/EXC/REAR/14
SCALE : 1 = 50	
DATE : 28/08/07	CADFILE :– PRANAV/DDN/BANDIVALI/WD/PLAN.DWG
DRN : PRANAV	
CHKD : P N D	LOCATION :


DUMASIA DESAI NANDANI ARCHITECTS
ARCHITECTS ENGINEERS & VALUERS
402, SAI CHAMBERS,OPP.RLY.STN.
NEHRU ROAD,SANTACRUZ (E),
MUMBAI–400 055

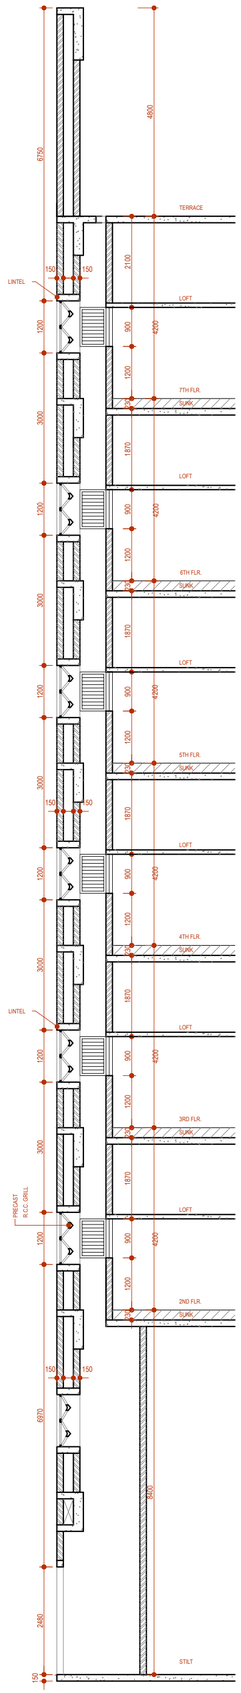


SECTION–N1

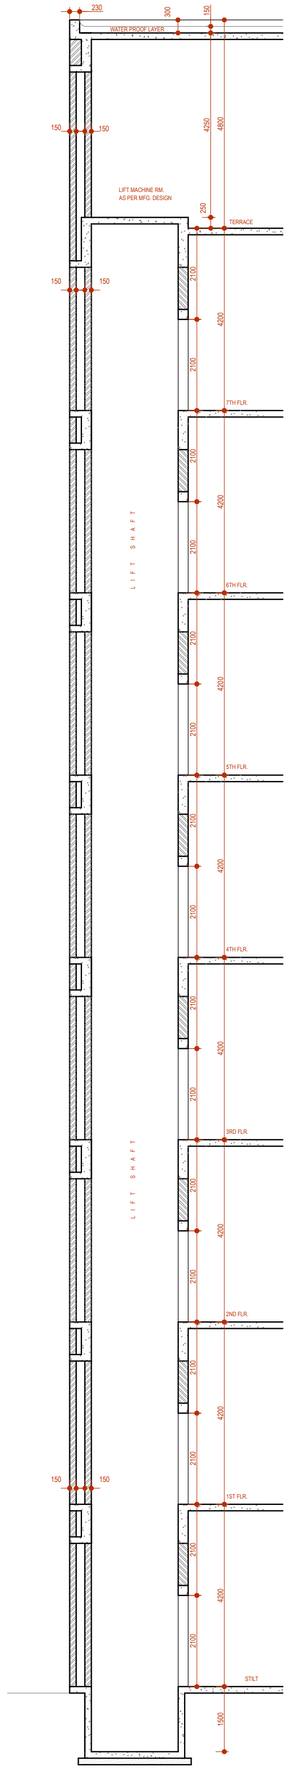


SECTION–N2

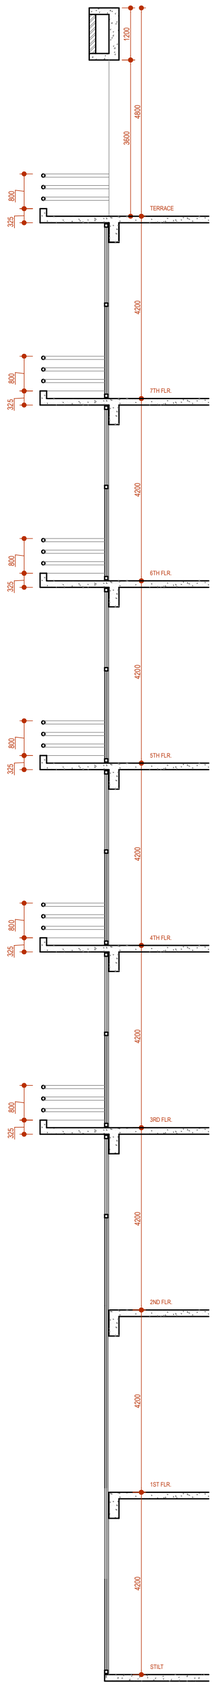


SECTION–N3

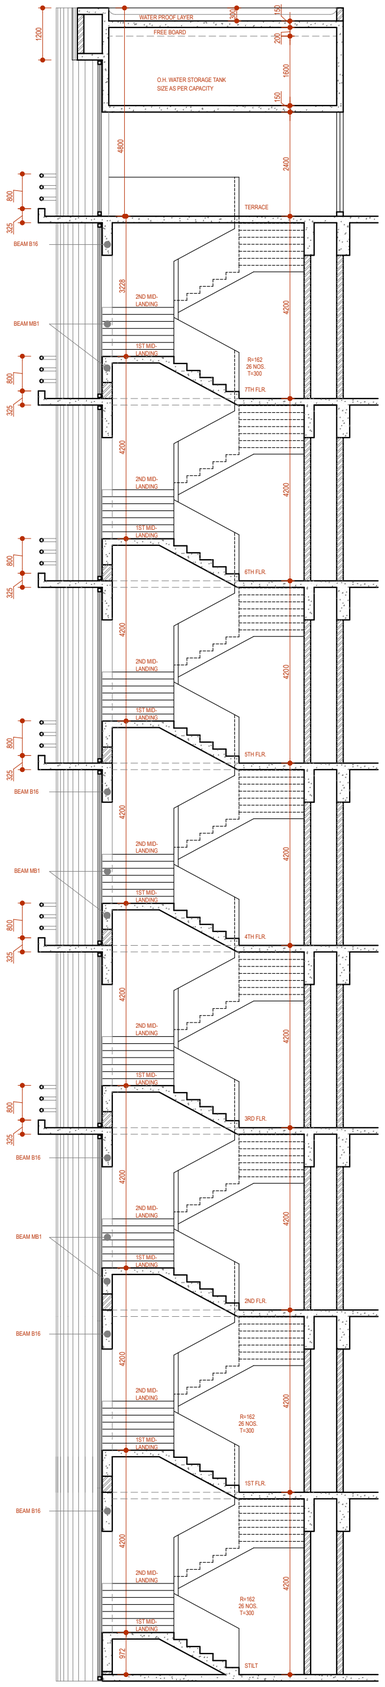

SECTION–N4

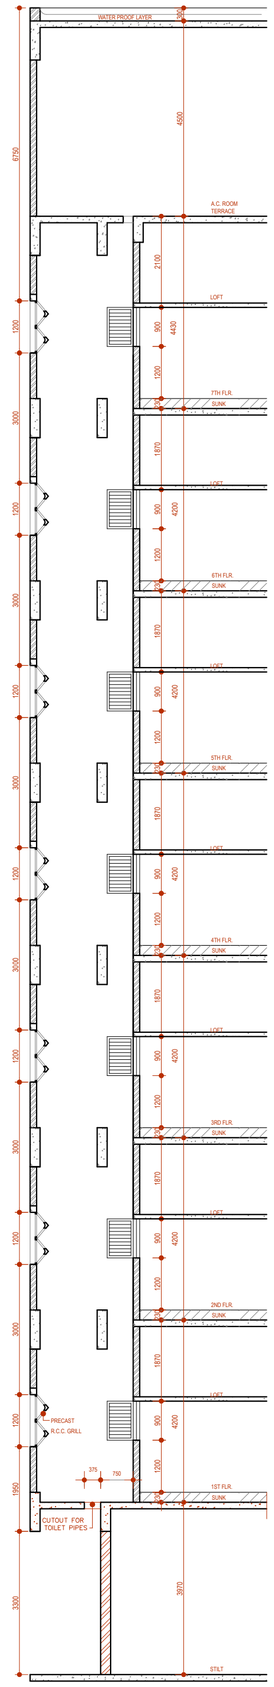

SECTION–N5

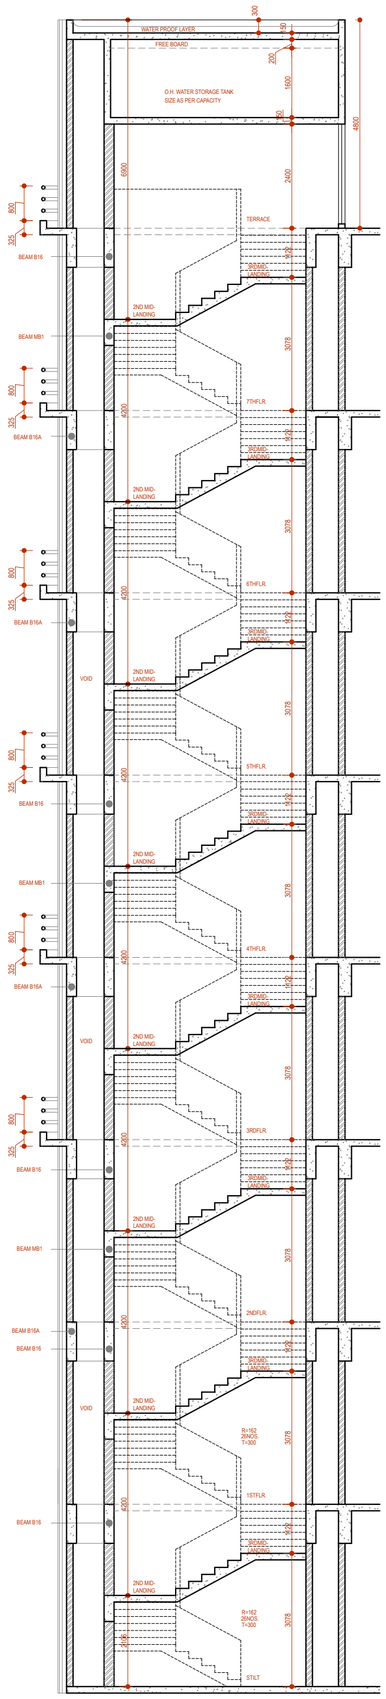

SECTION–N6

A. GENERAL NOTES

01 ALL DIMENSIONS ARE IN MTS. & MM UNLESS SPECIFIED OTHERWISE.

02 ALL DIMENSIONS AND LEVELS ARE TO BE CHECKED AND VERIFIED BY THE SITE ENG. BEFORE EXECUTION.

03 ALL THE WORK SHOULD BE CARRIED OUT AS PER SPECIFICATIONS AND INSTRUCTIONS GIVEN BY THE ARCHITECTS.

04 ANY DESCRIPANCY IN THIS DRAWING SHOULD BE BROUGHT TO THE IMMEDIATE NOTICE OF THE ARCHITECTS OR STRUCTURAL ENGINEERS.

05 ALL INTERNAL WALLS ARE 115MM THICK EXCLUDING PLASTERING AND EXTERNAL WALLS 125MM THK EXCLUDING PLASTER.

06 THIS DRAWING IS A COPYRIGHT AND MUST NOT BE USED OR DISCLOSED OR REPRODUCED IN ANY OTHER FORM WITHOUT EXPRESS PERMISSION OF DUMASIA DESAI NANDANI ARCHITECTS

B. SPECIAL NOTES

01 ALL PROJECTIONS TO BE CHECKED WITH ARCHITECTS DRAWING AND TO BE VERIFIED OR ADJUSTED ON SITE IN CONJUNCTION WITH THE STRUCTURAL DRAWINGS.

02 , THIS DRAWING IS TO BE READ IN CONJUCTION WITH THE R.C.C. CONSULTANTS DRAWING. DRG. NO.061030-B-111-COL-FTG

C. REVISIONS

REV. NO.	DESCRIPTION	DATE	SIGN
R1			
R2			
R3			

PROJECT :
PROPOSED INFORMATION TECHNOLOGY BUILDING KNOWN AS 'FLEXCEL–PARK', ON PLOT BEARING C.T.S. NO. 217/1 TO 7 S.V. ROAD, JOGESHWARI(WEST), MUMBAI 400102

FOR M/S EXCEL INDUSTRIES LTD.

TITLE
WALL SECTIONS N1 TO N6(NORTH SIDE)

I N D E X

JOB : EXCEL	DRG NO. WD/EXC/REAR/13
SCALE : 1 = 50	
DATE : 28/08/07	CADFILE :– PRANAV/DDN/BANDIVALI/WD/PLAN.DWG
DRN : PRANAV	
CHKD: P N D	LOCATION :

DUMASIA DESAI NANDANI ARCHITECTS
ARCHITECTS ENGINEERS & VALUERS
402, SAI CHAMBERS,OPP.RLY.STN.
NEHRU ROAD,SANTACRUZ (E),
MUMBAI–400 055