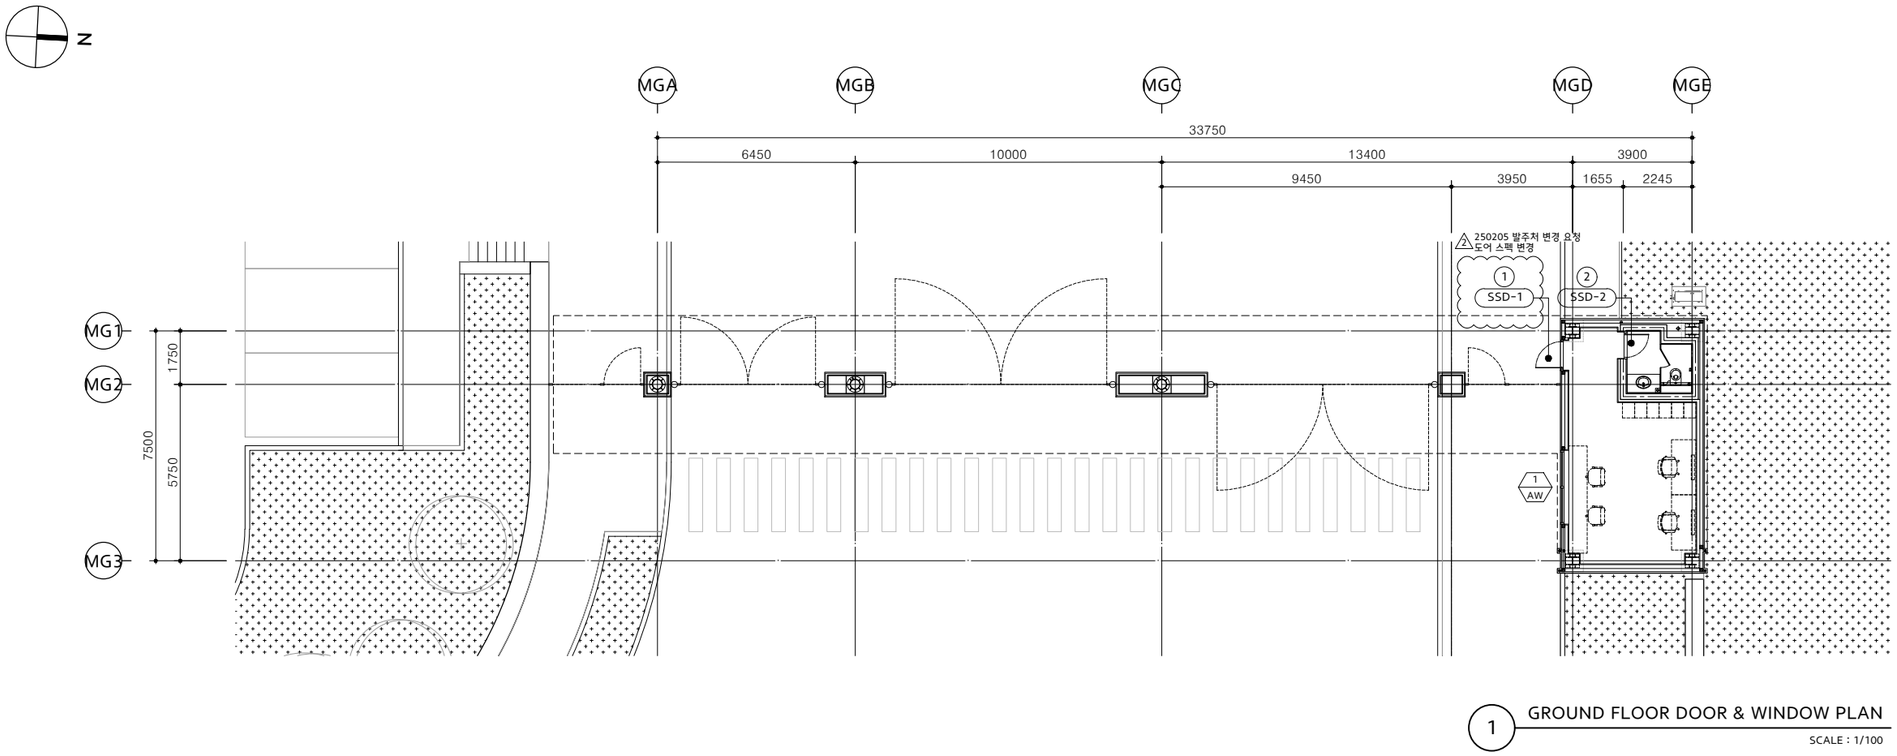



1 GROUND FLOOR DOOR & WINDOW PLAN

SCALE : 1/100


DOOR SHAPE & LEGEND

1 GENERAL NOTE

DOOR SYMBOL

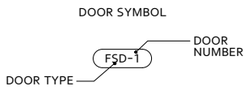


WINDOW SYMBOL

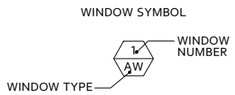


2 DOOR & WINDOW TYPE

SD	STEEL DOOR	OHD	OVERHEAD DOOR
FSD	FIRE STEEL DOOR	RS	ROOL-UP SHUTTER
SSD	S' STEEL DOOR	RRS	RAPID ROOL-UP SHUTTER
SFD	S' STEEL FOLDING DOOR	AW	ALUMINUM WINDOW
ASD	AUTO SLIDING DOOR	SSW	S' STEEL WINDOW
SLID	SLID DOOR	AG	ALUMINUM GRILL


3 DOOR SHAPE : SINGLE DOOR

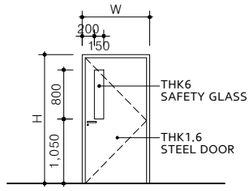

DOOR SHAPE - S1

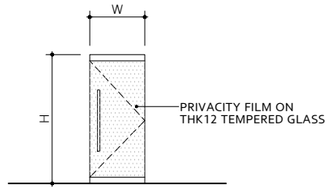

DOOR SHAPE - S2

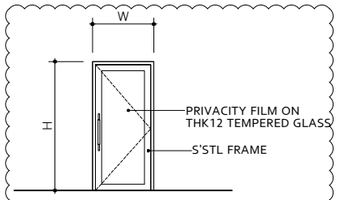


DOOR SHAPE - S3

2 250205 발주처 변경 요청
도어 스펙 변경

DOOR SCHEDULE

FLOOR NO.	NO.	DOOR NO.	MATERIAL		DOOR SIZE			SHAPE	MATERIAL			FIRE	KEY SET	HW SET	REMARKS
			DOOR	FRAME	THK	WIDTH	HEIGHT		HEAD	JAMB	SILL				
1F	1	SSD-1	GLASS	S'STL	-	1,000	2,100	S3	-	-	-	-	-	521	2 250205 발주처 변경 요청 도어 스펙 변경
	2	SSD-2	GLASS	S'STL	-	900	2,100	S2	-	-	-	-	-	501	

WINDOW SCHEDULE

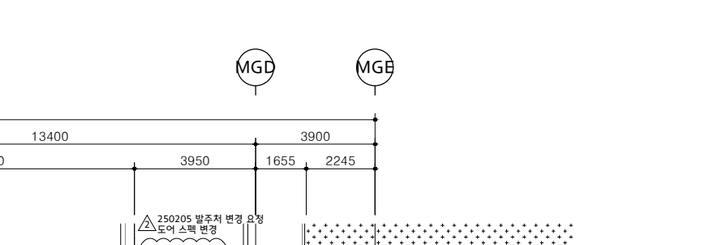

ID	1 AW ALUMINUM WINDOW	QT'Y	1 EA
GLAZING	THK18 PAIR GLASS		
FRAME	AL.BAR / ELECTROSTATIC POWDER COATING		
HARDWARE	-		

ID	-	QT'Y	-
GLAZING	-		
FRAME	-		
HARDWARE	-		

KEY PLAN

NOTE

REV.	DESCRIPTION	DRAWN	DATE
2	CD Rev.2	OH.J.S	2025.02.14
1	CD Rev.1	OH.J.S	2024.10.18
0	CONSTRUCTION DRAWING	OH.J.S	2024.07.30
B	DD Rev.B	OH.J.S	2024.06.28
A	DESIGN DEVELOPMENT	OH.J.S	2024.04.15

CLIENT

HYUNDAI

ARCHITECTS & ENGINEERS

JUNGLIM ARCHITECTURE

PROJECT TITLE

PUNE HMI PROJECT

DRAWING TITLE

[MAIN GATE]
DOOR, WINDOW PLAN & SCHEDULE

SCALE	DRAWN	CHECKED	REVIEWED	APPROVED	APPROVED
A1:1/100 A3:1/200	OH.J.S	HONG.G.D	LEE.S.L	HEC INDIA	PARK.T.S
DATE 14 FEB,2025					

MAIN CONTRACTOR

HEC KOREA LLP

DRAWING NO. WA-IPB-640-A-6101

REV. 2

A1 SIZE (841mm x 594mm)