

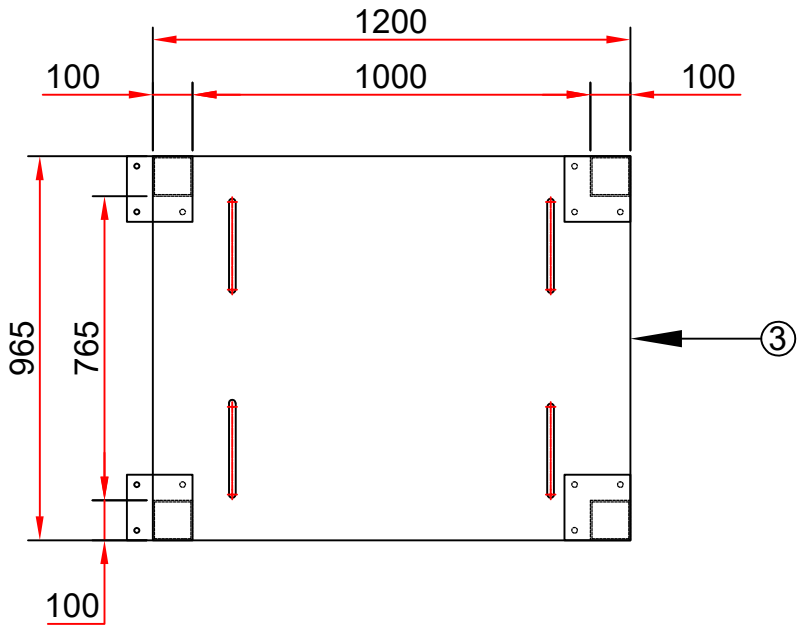


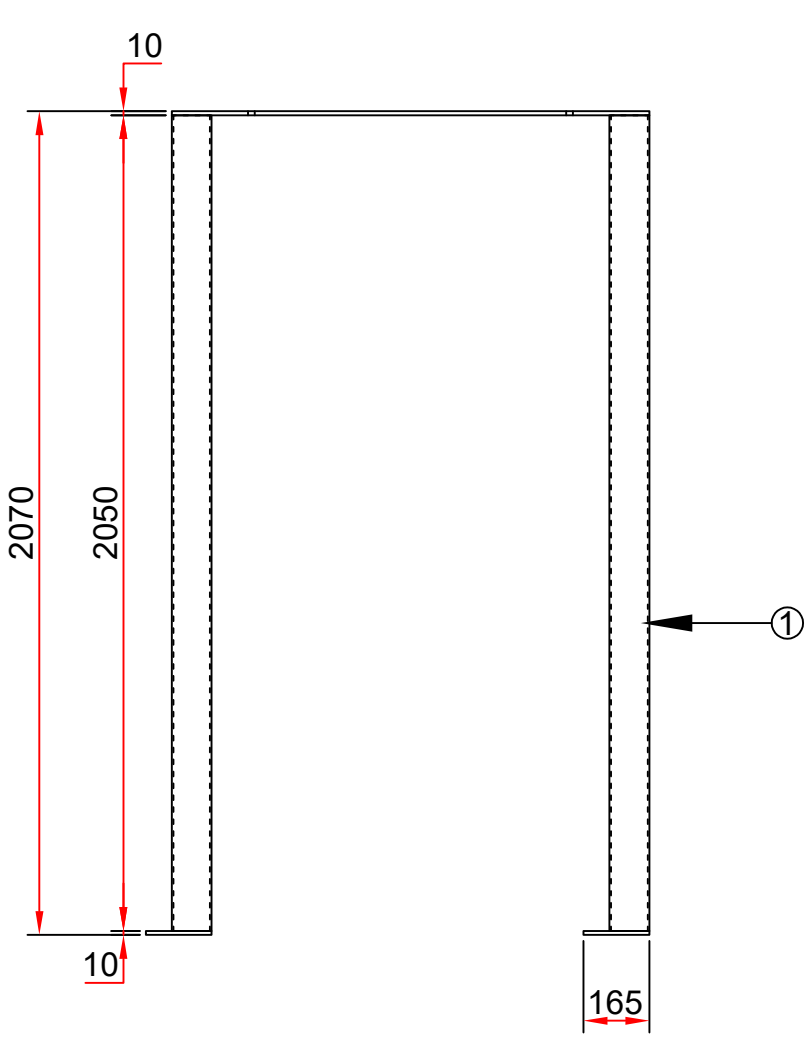

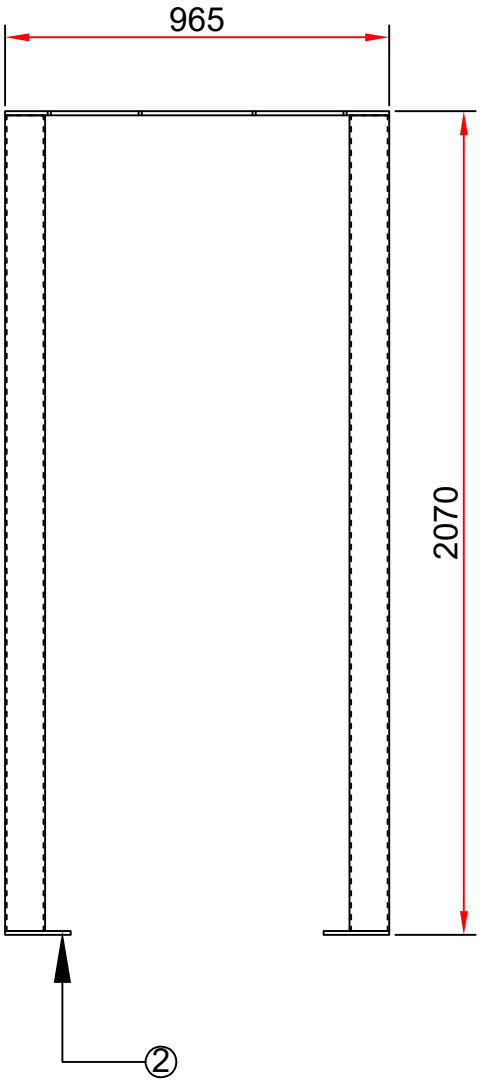

BOM FOR POST			
SL NO.	DESCRIPTION	SPECIFICATION	QTY
1	MS SQ. TUBE	100X100X4X2050L	4NOS
2	POST SUPPORT PLATE	165X165X10THK	4NOS
3	ROLLER SUPPORT PLATE	1200X965X10THK	1NO

Rev No.	Revision	Date	Revised By

This drawing & design is the property of NIHVA TECHNOLOGIES. Not to be sold or copied to any other concern.

TITLE:- POST

	NAME	DATE	SIGN
DRAWN	SUJATA	20/07/2022	
CHECK	M.S	20/07/2022	
APPRD.	A.K	20/07/2022	

If any queries contact : design@nihva.com

ALL DIMENSION ARE IN mm

NIHVA TECHNOLOGIES PVT. LTD.

NIHVA TECHNOLOGIES PVT. LTD. PUNE
Tel : 020 66304033
Email:- info@nihva.com
Website:- www.nihva.com

CLIENT - OC Specialities

LOCATION - Solapur

PRODUCT - | QTY:-1 NO

DWG NO:-NIHVA/22-23/MFG/0039 | REV- 0

SCALE: NTS | SCALE:-- 1:1 | SHEET: 01 OF 01