ASSA ABLOY

Installation documents

GMR Aero Technic Hyderabad (5-part)

Project No. 84800

Installation Manual

Project handover, installation checklist, Installation report,

Daily field report, changes during installation 1

Shall always be filled out and sent back to AAES Skellefteå.

Interface drawing, main assembly drawings 2

Sub assembly drawings 3

Load diagram 4

Electrical installation diagram 5

Fabric folding instruction 6

Project Hand Over

84800 GMR Aero Technic Hyderabad (5-part)

Project description: ***Megadoor in size 79014 mm X 2300/14000 mm acc. to assembly drawing No. 77800***

Contract/file: *ASSA ABLOY quotation 221129*

Installation: ***Done in accordance to "Installation manual" and with Megadoor certified supervisor.***

Actual project is hereby approved and accepted for hand over to the Purchaser: ***Nihva Technologies***

Warranty period for material: ***12 months from Project Hand Over***

For ASSA ABLOY (Supplier)	For: Nihva Technologies (Purchaser)
……	……..
Date:	Date:

ASSAABLOY Entrance System
Servicegatan 6
SE- 931 76 Skellefteå

Tel: + 46 (0)10 47 47 190
Fax : + 46 (0)910 166 20
www.assaabloyentrance.com

Org. No: 556059-9523
Vat. No: SE55605995230

Project Hand Over

84800 GMR Aero Technic Hyderabad (5-part)

Project description: ***Megadoor in size 79014 mm X 2300/14000 mm acc. to assembly drawing No. 77800***

Contract/file: *ASSA ABLOY quotation 221129*

Installation: ***Done in accordance to "Installation manual" and with Megadoor certified supervisor.***

Actual project is hereby approved and accepted for hand over to the Purchaser: ***Nihva Technologies***

Warranty period for material: ***12 months from Project Hand Over***

For ASSA ABLOY (Supplier)	For: Nihva Technologies (Purchaser)
……	……..
Date:	Date:

ASSAABLOY Entrance System
Servicegatan 6
SE- 931 76 Skellefteå

Tel: + 46 (0)10 47 47 190
Fax : + 46 (0)910 166 20
www.assaabloyentrance.com

Org. No: 556059-9523
Vat. No: SE55605995230

ASSA ABLOY
AAES Production Skellefteå AB
Servicegatan 6
931 76 Skellefteå
Sweden
www.megadoor.com

INSTALLATION CHECK LIST MEGADOOR PROJECTS

Project Name:	Project Number:	Engineers on site:
	Sheet Number:	

	Check list pre-installation	OK	NOT OK	N/A
1	**Documentation**			
1.1	- Installation documentation has been studied and understood	☐	☐	☐
1.2	- Deviations from documentation have been reported and approved	☐	☐	☐
2	**Building**			
2.1	- Has appropriate stability	☐	☐	☐
2.2	- Has been load tested	☐	☐	☐
2.3	- Measurements are in accordance with agreements	☐	☐	☐
	Check during installation			
3	**Door machinery**			
3.1	- Belts intact, not chafing or twisted	☐	☐	☐
3.2	- Belt loops have sewn flap facing toward TW	☐	☐	☐
3.3	- Belt drum segments and belt rotate in correct direction	☐	☐	☐
3.4	- Adjustable roller holders are adjusted and locked	☐	☐	☐
3.5	- Wire rope fleet angle within 4 degrees	☐	☐	☐
3.6	- Wire rope lubricated correctly	☐	☐	☐
3.7	- Hoist and sheave grooves lubricated correctly	☐	☐	☐
4	**Chain hoist**			
4.1	- Chain secured, exit stop fitted	☐	☐	☐
4.2	- Chain intact, not twisted	☐	☐	☐
4.3	- Enough slack at lower position	☐	☐	☐
4.4	- Hoist free to swing	☐	☐	☐
4.5	- Hoist is directly above lifting pipe	☐	☐	☐
4.6	- Chain lubricated correctly	☐	☐	☐
5	**Gear motors**			
5.1	- Air plug fitted	☐	☐	☐
5.2	- Motor brake working	☐	☐	☐
5.3	- Crank interlock working	☐	☐	☐
5.4	- Crank and brake lever correct size	☐	☐	☐
6	**Guiderail and Side Seal Angles**			
6.1	- Joints are even, tight, and dressed	☐	☐	☐
6.2	- Roll pins are in place, in both guiderail and seal angles	☐	☐	☐

6.3	- Pieces are aligned at mullion hinge joint	☐	☐	☐
6.4	- Arresters and guide blocks are not chafing	☐	☐	☐
6.5	- Guide blocks are adjusted with correct gap to guiderail	☐	☐	☐
7	**Safety Arresters**			
7.1	- Actuates freely without binding	☐	☐	☐
7.2	- Catching function works	☐	☐	☐
7.3	- Wind locks correctly positioned and re-verified after door has hung	☐	☐	☐

	Check during installation	OK	NOT OK	N/A
7.4	- Axial guide rollers adjusted with correct gap to guiderail	☐	☐	☐
7.5				
8	**Seals**			
8.1	- Installed, trimmed, and effective	☐	☐	☐
8.2	- Bottom rubber seal isolated from fabric to prevent out-gassing mark	☐	☐	☐
9	**Mullion**			
9.1	- Mullion swings up under door leaf	☐	☐	☐
9.2	- Pivot joint actuates smoothly	☐	☐	☐
9.3	- Pillow blocks greased	☐	☐	☐
9.4	- Pivot joint actuates smoothly	☐	☐	☐
9.5	**At normally loaded building:**			
9.6	- Floor pin centered and running easily in guide	☐	☐	☐
9.7	- Correct clearance between mullion end and floor	☐	☐	☐
9.8	- Pit covers fit and operate correctly	☐	☐	☐
10	**Door leaf**			
10.1	- Door leaf built with correct pitch	☐	☐	☐
10.2	- Fabric intact and clean	☐	☐	☐
10.3	- Fabric tensioned well at last few feet on each edge of door for tight seal	☐	☐	☐
10.4	- Fabric trimmed at sides, flush with batten strips	☐	☐	☐
10.5	- All fabric screws fitted	☐	☐	☐
10.6	- Batten strips not bent	☐	☐	☐
10.7	- Batten strips do not press against side seal angles	☐	☐	☐
10.8	- Batten strips trimmed with correct gap to TW	☐	☐	☐
10.9	- Top beam batten strip screwed into side seal at last hole location	☐	☐	☐
10.10	- Header box sheet metal installed and clean	☐	☐	☐
10.11	- Beam clamps have correct engagement onto support steel	☐	☐	☐
10.12	- Wooden blocks or shipping supports removed from door leaf / top beam	☐	☐	☐
10.13	- End of header box closed off with sheet metal if exposed	☐	☐	☐

11	**Joints**			
11.1	- Screws tightened with correct torque	☐	☐	☐
11.2	- Welds professionally done	☐	☐	☐
11.3	- Primer applied / touched up	☐	☐	☐
12	**Electric equipment**			
12.1	- Permanent power is connected	☐	☐	☐
12.2	- Control panel disconnect functions correctly	☐	☐	☐

	Check during installation	**OK**	**NOT OK**	**N/A**
12.3	- E-stops function correctly	☐	☐	☐
12.4	- Pushbuttons do not stick	☐	☐	☐
12.5	- Phase monitor adjusted	☐	☐	☐
12.6	- Current monitors adjusted	☐	☐	☐
12.7	- Audible/visual alarm functioning	☐	☐	☐
12.8	- No loose connections in panels	☐	☐	☐
13	**Limit switches**			
13.1	- Door and mullion limits adjusted and actuating correctly	☐	☐	☐
13.2	- Slack wire rope limit assembly adjusted and locked	☐	☐	☐
13.3	- Limit plunger extensions installed	☐	☐	☐
13.4	- 3-phase limit plungers correctly adjusted	☐	☐	☐
14	**Function**			
14.1	- Door is working in accordance with function description	☐	☐	☐
14.2	- Doors and mullions reach intended positions	☐	☐	☐
14.3	- Interlocks work as planned	☐	☐	☐
14.4	- Door has been operated through at least two complete cycles	☐	☐	☐
15	**Labelling**			
15.1	- Warning labels fitted	☐	☐	☐
15.2	- Instruction labels fitted	☐	☐	☐
15.3	- Instruction labels fitted	☐	☐	☐
16	**General**			
16.1	- User informed about door functions	☐	☐	☐
16.2	- User informed about six-inch-stop door closing procedure	☐	☐	☐
16.3	- Installation report approved and signed	☐	☐	☐
16.4	- Rental equipment return called in (record conformation numbers below)	☐	☐	☐
16.5	- Ship as-built prints to office within two days	☐	☐	☐
16.6	- Returned Material Form filled out if shipping any material back to Megadoor	☐	☐	☐

Notes, observations not previously recorded, customer comments.

Place: .....

Date: .....

Sign: .....

Name: .....

Supervisor

Date: .....

Sign: .....

Name: .....

Purchaser representative

Date: .....

Sign: .....

Name: .....

Third party representative

Address: Servicegatan 6
931 76 Skellefteå, Sweden
Tel: +46 10 47 47 190 Fax: +46 910 166 20

Project name:
Project number:
Supervisor:

Installation report

Date/Day	Weather impact on inst?	Supervisor: hours worked	Helpers: hours worked	Installation progress	Problems: Daily field report no.

Megadoor AB

Address: Servicegatan 6
931 76 Skellefteå, Sweden
Tel: +46 10 47 47 190 Fax: +46 910 166 20

Changes during installation

The installation has been completed; the following changes need to be implemented on Megadoor AB's documentation:

No changes ☐

Drawing # / Change

-

-

-

-

-

-

-

-

-

-

-

-

Date:_____

Signature:_____

Name in printing/Organization:_____

ASSA ABLOY

DAILY FIELD REPORT no:1

Job Name:		Date / Day:			
Job Number:		Weather / Temp:			
Lead Installer:		Hours Worked: from		to	
Helpers / Hours Worked:					

Anticipated or Current Delays: (Mark applicable item and explain)
Due to: ☐ dwg, ☐ mat'l, ☐ equipment, ☐ subcontractor, ☐ GC, ☐ other

Subjects discussed with GC today: (Mark applicable item and explain)
☐ progress/schedule, ☐ extra work, ☐ manpower, ☐ other

Installation Highlights: (Mark applicable item and explain)
☐ work completed, ☐ significant scope of work change, ☐ mat'l/equip problems,
☐ safety violations, ☐ anticipated construction problems, ☐ visitors

Attest by GC/Customer: _____

Revision		Date	By
A	Corrected mullion hoist positions, floor pits altered	2022-09-02	EB
B	New measurements, doors redrawn	2022-10-11	EB

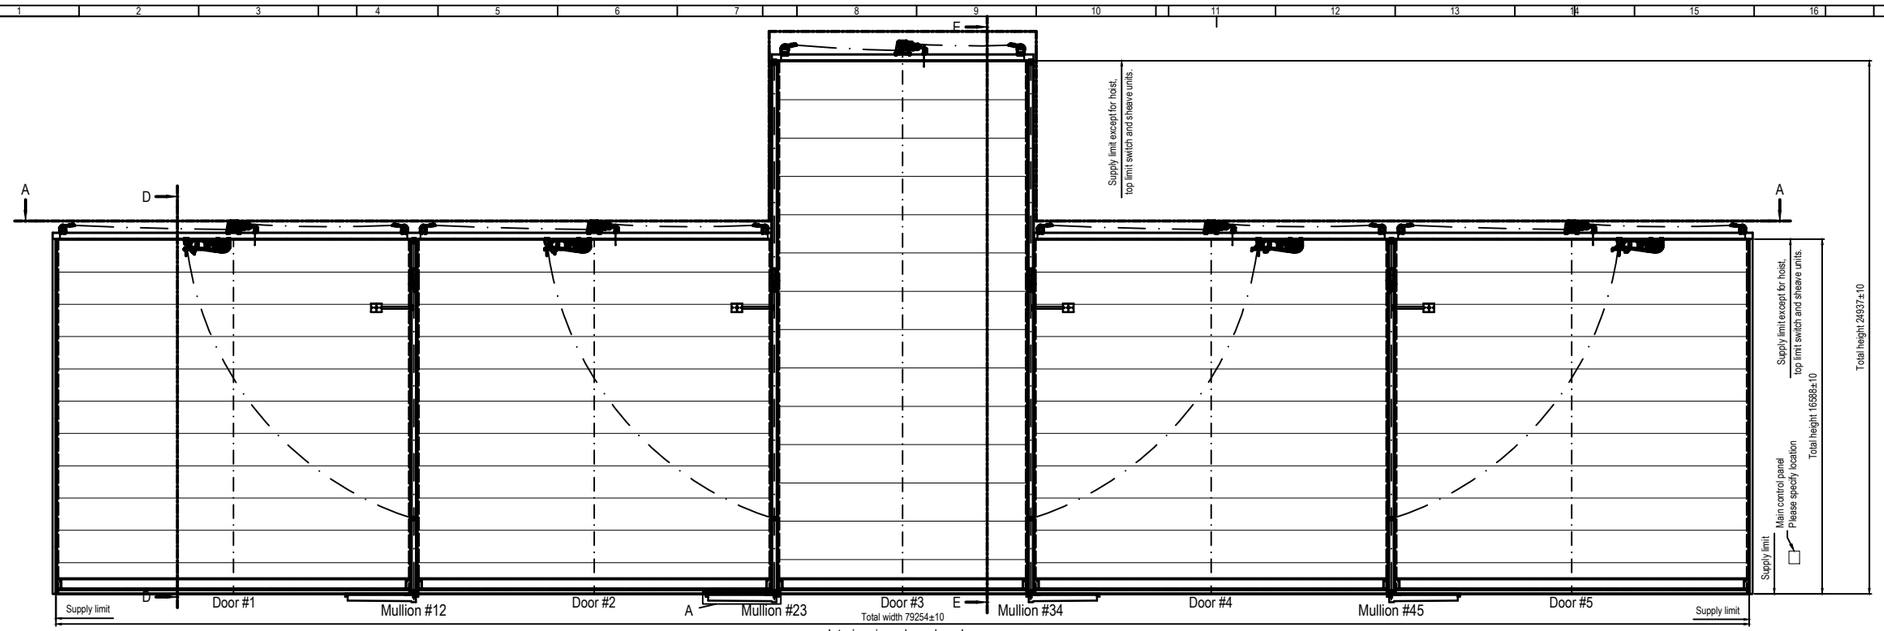

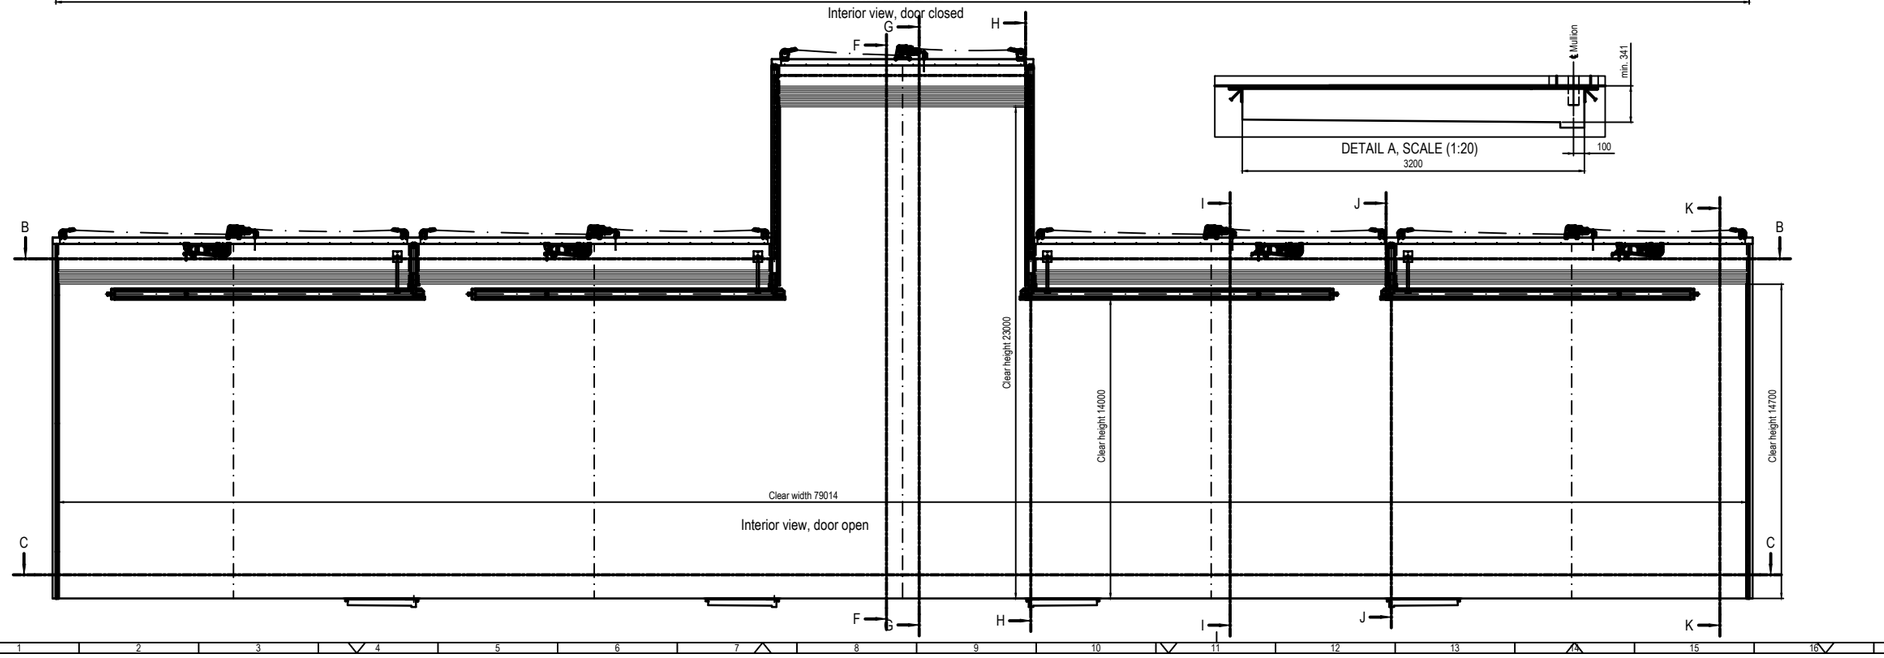

5.9T/27 Door #3

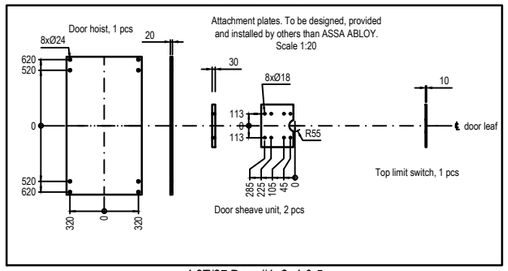

4.9T/27 Door #1, 2, 4 & 5

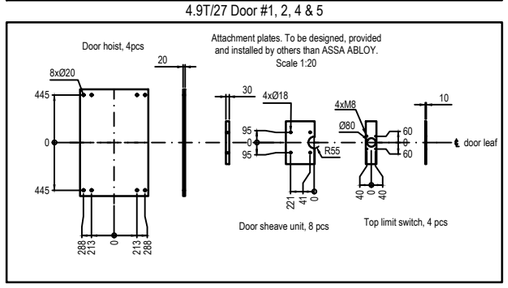

DOOR IDENTITY NUMBER: 84800001

LOAD DIAGRAM & NOTES, ref. to drwng. no. 77446

INTERFACE, SECTIONS ref. to drwng. no. 77445

INTERFACE, PLAN VIEWS ref. to drwng. no. 77444

DESIGNED: EB	SIZE: A1F	SCALE: 1:100	GMR Aero Technic Hangar1
CODE: 84800	If not otherwise stated: Tolerances ISO 2768-m EN ISO 13920-B		India
ITEM NO:	Drafting class ISO 9013-442		Megadoor 79014x23000/14000
DATE: 2022-08-23	Weld class ISO 5817-C		Interface, Elevation
ASSA ABLOY	Surface finish Smooth raw surface	DRAWING NO: 77443	REVISION: B

This document is the property of ASSA ABLOY Entrance Systems AB and shall not without our written permission be copied, imported to a third party country or by any other means misused.

Revision		Date	By
A	Corrected mullion hoist positions, floor pits altered	2022-09-02	EB
B	New measurements, doors redrawn	2022-10-11	EB

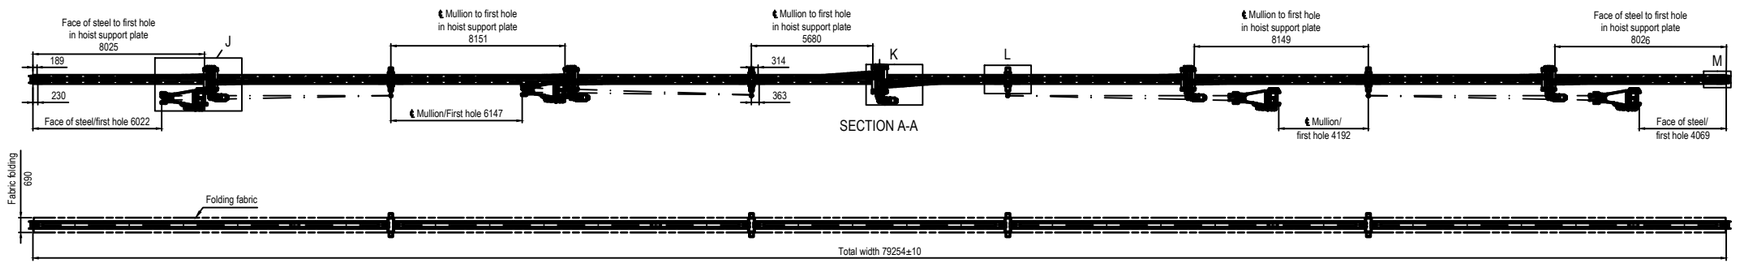

SECTION A-A

SECTION B-B

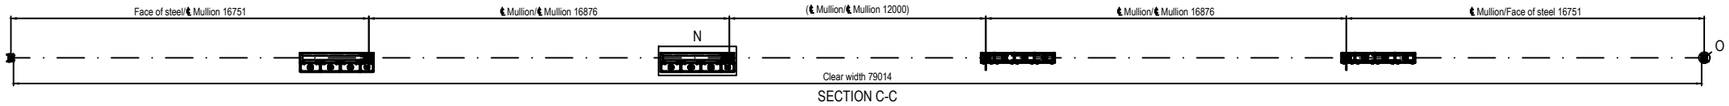

SECTION C-C

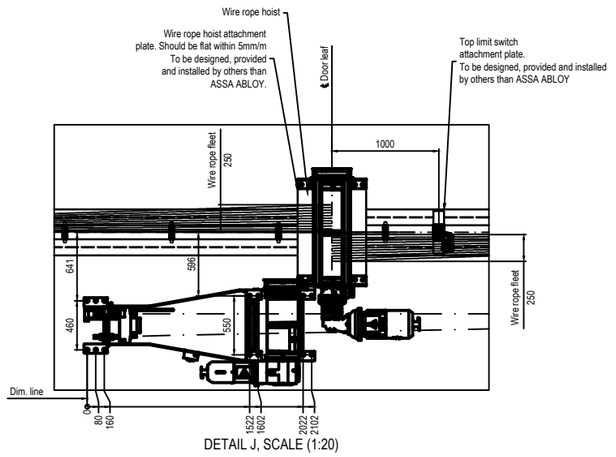

DETAIL J, SCALE (1:20)

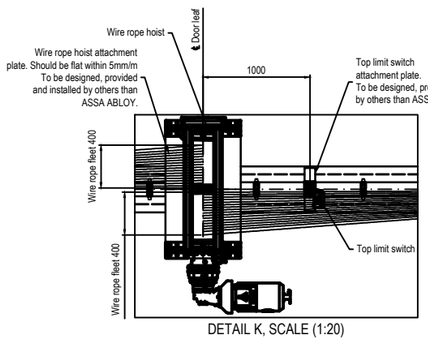

DETAIL K, SCALE (1:20)

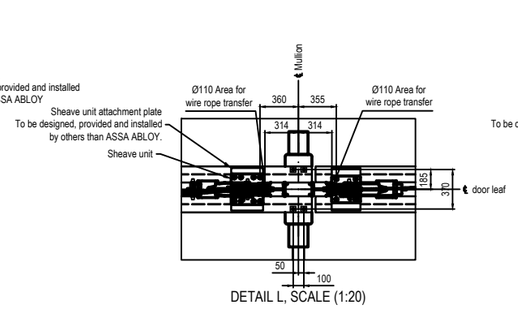

DETAIL L, SCALE (1:20)

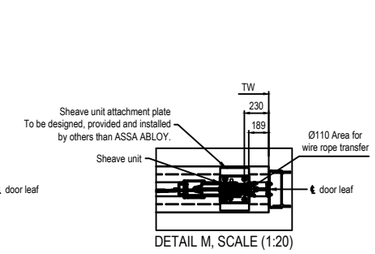

DETAIL M, SCALE (1:20)

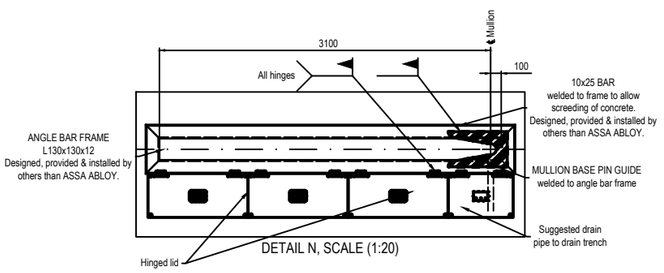

DETAIL N, SCALE (1:20)

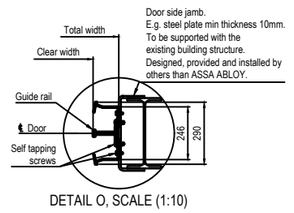

DETAIL O, SCALE (1:10)

DOOR IDENTITY NUMBER: 84800001

LOAD DIAGRAM & NOTES, ref. to drwng. no. 77446

INTERFACE, SECTIONS ref. to drwng. no. 77445

INTERFACE, ELEVATION ref. to drwng. no. 77443

DESIGNED EB	SIZE A1F	SCALE 1:100	GMR Aero Technic Hangar1
CODE 84800	If not otherwise stated: Tolerances ISO 2768-m EN ISO 1302-B		India
ITEM NO	Drafting class ISO 9013-4D		Megadoor 84000x23000/14000
DATE 2022-08-23	Weld class ISO 5817-C		Interface, Plan views
ASSA ABLOY	Surface finish Smooth raw surface	DRAWING NO 77444	REVISION B

PDF/DXF

The document is the property of ASSA ABLOY Entrance Systems AB and shall not without our written permission be copied, reported to a third party or used in any other unauthorized manner.

Revision		Date	By
A	Corrected mullion hoist positions, floor pits altered	2022-09-02	EB
B	New measurements, doors redrawn	2022-10-12	EB

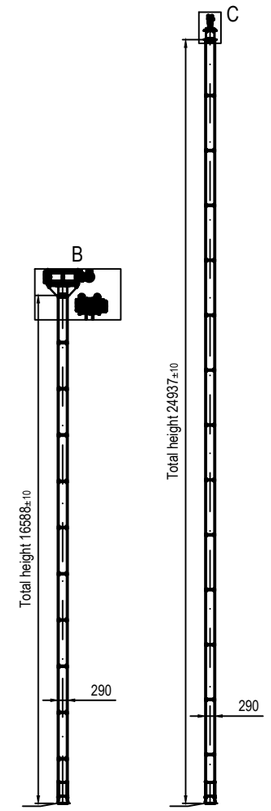

SECTION D-D SECTION E-E

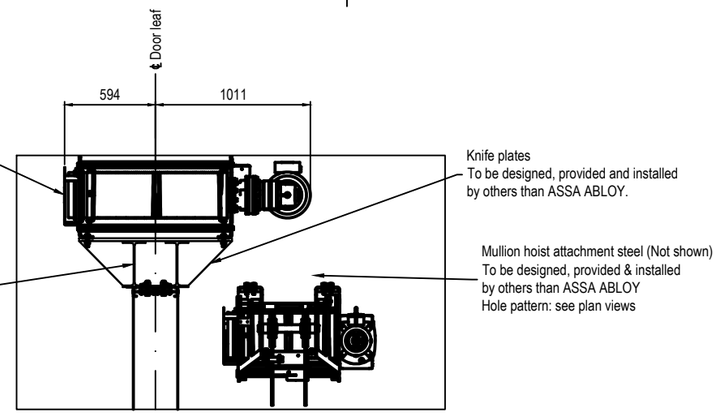

DETAIL B, SCALE (1:20)

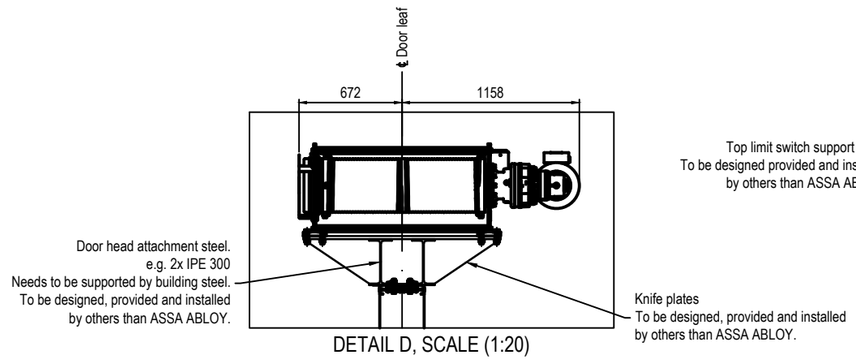

DETAIL D, SCALE (1:20)

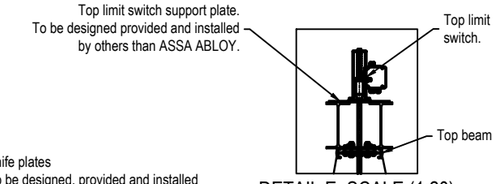

DETAIL E, SCALE (1:20)

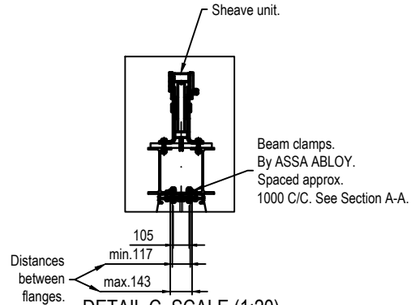

DETAIL C, SCALE (1:20)

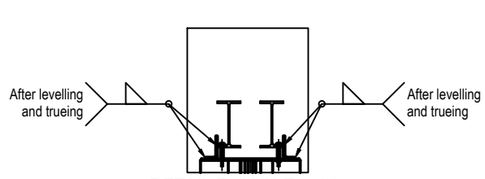

DETAIL F, SCALE (1:20)

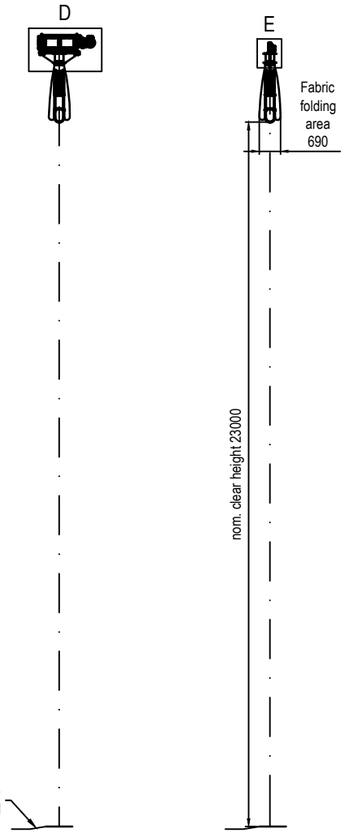

SECTION F-F

SECTION G-G

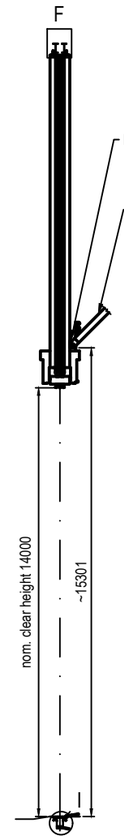

SECTION H-H

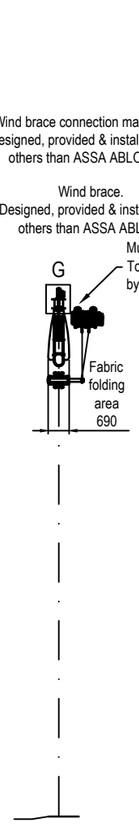

SECTION I-I

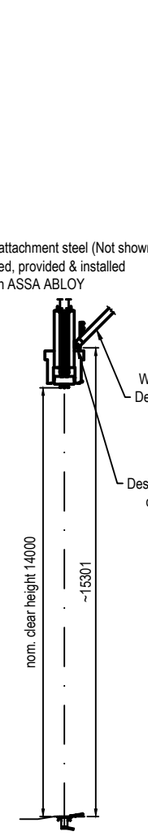

SECTION J-J

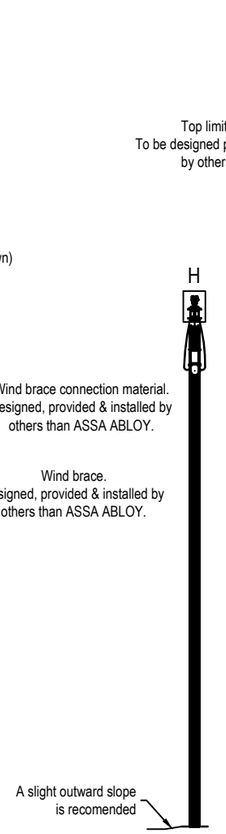

SECTION K-K

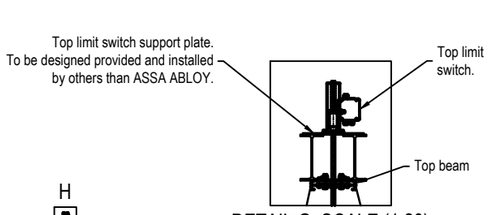

DETAIL G, SCALE (1:20)

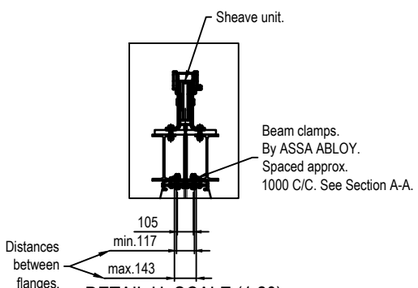

DETAIL H, SCALE (1:20)

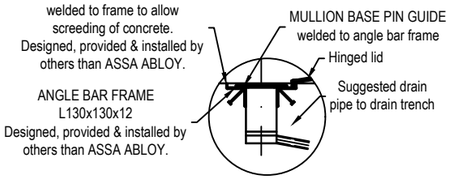

DETAIL I, SCALE (1:20)

DOOR IDENTITY NUMBER: 84800001

LOAD DIAGRAM & NOTES, ref. to drwng. no. 77446

INTERFACE, PLAN VIEWS ref. to drwng. no. 77444

INTERFACE, ELEVATION ref. to drwng. no. 77443

DESIGNED EB	SIZE A1	SCALE 1:100	GMR Aero Technic Hangar1
CODE 84800	If not otherwise stated:		India
ITEM NO	Tolerances ISO 2768-m EN ISO 13920-B		Megadoor 79014x23000/14000
DATE 2022-08-23	Cutting class ISO 9013-442		Interface, sections
ASSA ABLOY	Weld class ISO 5817-C	DRAWING NO 77445	REVISION B
	Surface finish Smooth raw surface		

P.O.T DATE

This document is the property of ASSA ABLOY Entrance Systems AB and shall not be reproduced, disclosed or copied, nor used in part, to a third party or used for any other unauthorised purpose.

Installation

98	1	Installation manual					
97							

Electrical

96							
95	1	Electrical cable set					
94	1	Control panel					

Side jamb related

93							
92							
91							
90	20	Washer	HB 200	BRB 10.5x22		19200200	0,0046
89	20	Screw	Cl. 8.8	M6S 10x50		19200435	0,038
88	20	Locking lug				19113128	0,57
87	12	Parallel pin	SMS 2374	CP 5x40 A2		19200363	
86	8	Tension pin	SMS 1663	FRP 6x10 A2		19200373	
85	84	Screw		M6SF-GF 8x20 zib		19200233	0,035
84	92	Screw		M6SF-GF 10x30 zib		19200455	0,065
83	1	Set of guide rails				77828	388

Swing up mullion related

82							
81							
80							
79	3	Touch up paint (Megadoor std.)			Light Grey (RAL 7047)	19204692	
78	1	Primer				19204693	
77							
76	4	Closing weight		10 Counter weight plates.	Assembled on site	39500	243
75	4	Lifting pipe		Ø100 mm, L=1120 mm.	Assembled on site	19139284	53
74							
73	4	3-Phase limit switch trigger		Rope 8 & 10 mm		19134555	
72							
71							
70							
69	56	Nut		M16 DIN 985 A2		19203435	0,03
68	112	Washer		BRB 17x30x3 fzv		19200356	0,01
67	56	Screw		M6S 16x 70h fzv		19204296	0,13
66	16	Shim	Stainless steel	220x76x2	for 1T2/17TB-1.75T2/19TB	19146488	
65	32	Shim	Stainless steel	140x86x2	for 1T2/17TB-1.75T2/19TB	19146588	
64							
63	8	Shackle		Gunnebo straight type A M12	art. no. A831312	19203154	0,2
62	8	Thimble & ferrule			For wire rope Ø10 mm	19204554	
61	8	Wire rope Ø10 mm		L=25000 mm	Max. load 69,8 kN	19203953	12,0
60	4	Mullion hoist		Lidan 1,75T2/19 TB	For wire Ø10 mm	19205123	327
59							
58	4	Mullion hoist		Lidan 1,75T2/19 TB	Type 1	19151187	19,5
57							
56	12	Floor pit cover, Large				77826	21
55							
54	4	Floor pit cover, Small		For pin Ø80-100 mm		19163824	23
53							
52	4	Mullion floor guide		For Ø100 mm:s pin		19115986	8,6
51	16	Washer		BRB 17x30x3 fzv		19200356	0,0
50	16	Adjustment screw		M6S 16x140h fzv		19203971	0,2
49	8	Angle bar		150x75x10	L = 200mm	19136594	3,3
48	1	Swing up mullion #45				77820	2171
47	1	Swing up mullion #34				77819	3025
46	1	Swing up mullion #23				77818	3025
45	1	Swing up mullion #12				77817	2171

Hoist related

44							
43	10	Screw		MRT - GF 5x16		19200263	
42	5	Main switch attachment plate		for KF325/11		19150710	0,5
41	5	Clutch arm bracket		d=28 & 38 for 3.4-12.5T		19151303	0,53
40	80	Nut		M6M 16 ISO 4032-8 fzv		19203289	0,04
39	160	Washer		BRB 17x30x3 fzv		19200356	0,01
38	32	Screw		M6S 16x 70h fzv		19204296	0,13
37	48	Screw		M6S 16x 80 fzv		19200254	0,15
36	8	Nut		M6M 20 ISO 4032-8 fzv		19201687	0,07
35	16	Washer		BRB 21x36x3 fzv		19200202	0,02
34	8	Screw		M6S 20x 80 fzv		19200294	0,26
33	5	Top limit breaker		Push rod L=925mm	25A	19150851	18,3
32	2	Thimble & ferrule			For wire rope Ø16 mm	19204557	
31	2	Wire rope Ø16 mm		L= 37000mm	Max. load 179 kN	19203955	46
30	8	Thimble & ferrule			For wire rope Ø12 mm	19204555	
29	8	Wire rope Ø12 mm		L= 37000mm	Max. load 100 kN	19203954	25,6
28							
27	1	Sheave unit, Right		For wire Ø16 mm	With slack wire breaker	19129467	49
26	1	Sheave unit, Left		For wire Ø16 mm	With slack wire breaker	19129211	49
25	4	Sheave unit, Right		For wire Ø12 mm	With slack wire breaker	19129468	34
24	4	Sheave unit, Left		For wire Ø12 mm	With slack wire breaker	19129447	34
23							
22	8	Shim	Stainless steel	215x140x2	for 5.9T2/27-8T2/27-12.5T2/37	19146486	
21	32	Shim	Stainless steel		for 3.4T2/21- 4.9T2/27	19146484	
20	5	Label set				19125704	
19							
18	1	Wire rope hoist		LIDAN 5.9T2/27	For wire Ø16 mm,	19205265	503
17	4	Wire rope hoist		LIDAN 4,9T2/27	For wire Ø12 mm,	19205259	339

Bottom beam

16							
15							
14							
13	1	Bottom beam #3				77814	716
12	4	Bottom beam #1, 2, 4 & 5				77807	999

Door leaf related

11							
10							
9							
8	172	Washer		50x55x5 d=14		19124902	0,06
7	172	Beam clamp	Lindapter	B 12P3777 M12		19203066	0,14
6	172	Washer	HB200	BRB 13x24x2,5 fzv		19200333	
5	172	Screw	Cl. 8.8	M6S 12x120h fzv		19203623	0,11
4							
3							
2	1	Door leaf #3				77810	1865
1	4	Door leaf #1, 2, 4 & 5				77803	2455
item	**qty / door**	**description**	**material**	**dimension**	**remarks**	**drwng.no /art.no**	**weight kg/pc.**

GMR Aero Technic Hangar1
India
Megadoor 79014x23000/14000
Parts list no.: 77800.xls
Ref. to assembly drawing no. 77800-77802.dwg

Date: 2022-11-03
Project no: 84800
Designed by: EB
Revision: --

Total weight (kg): 32983

Door identity number: 84800001
Quantity of equal doors: 1

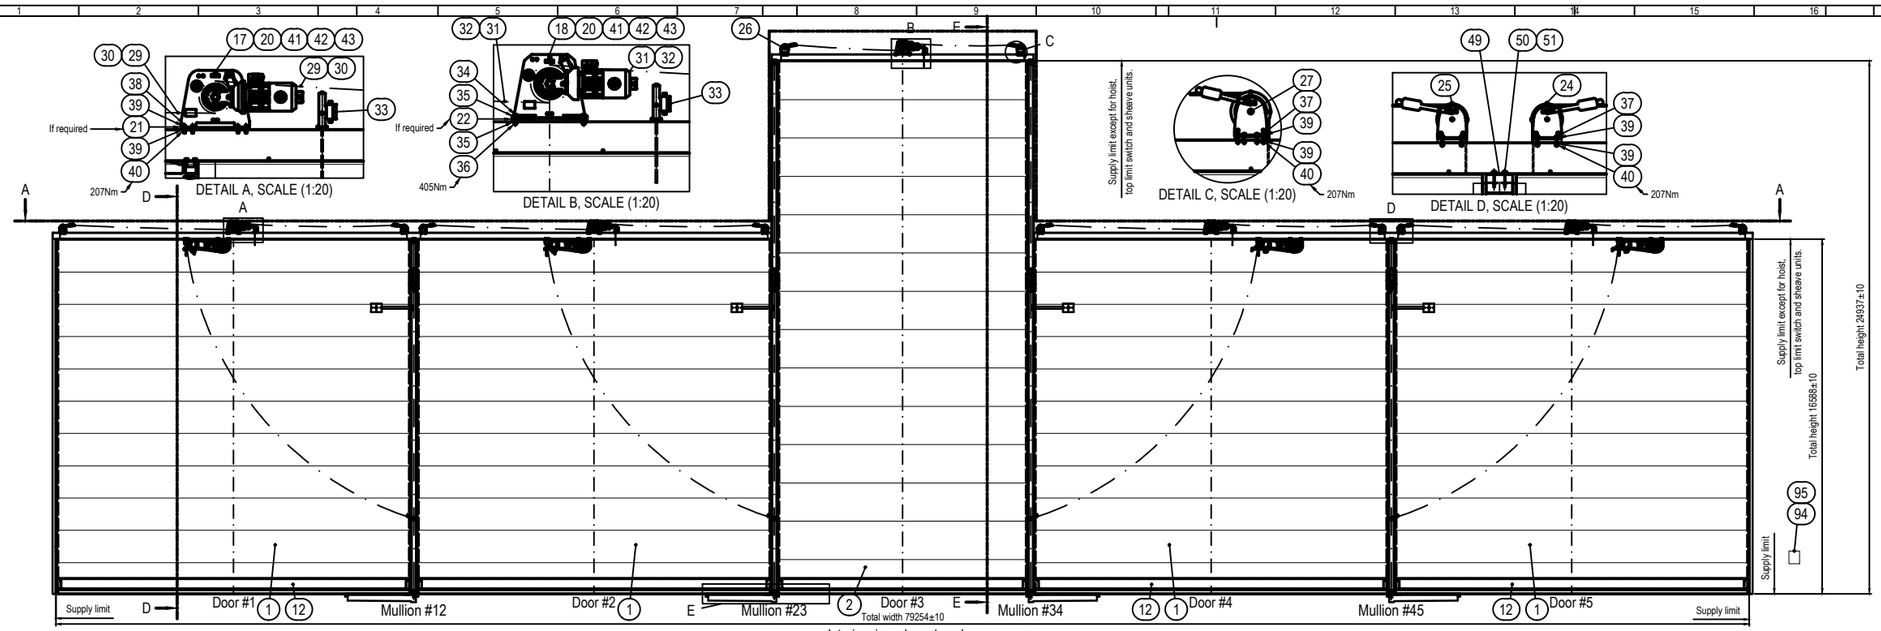

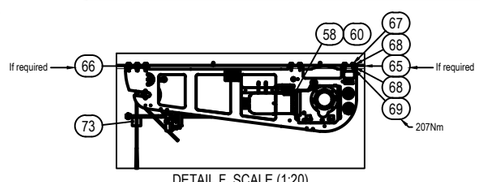

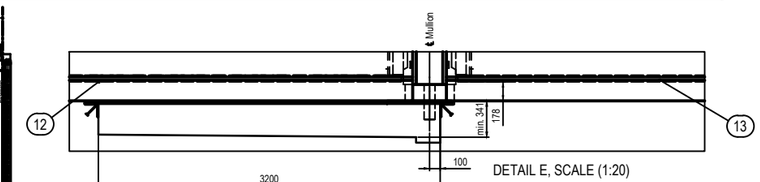

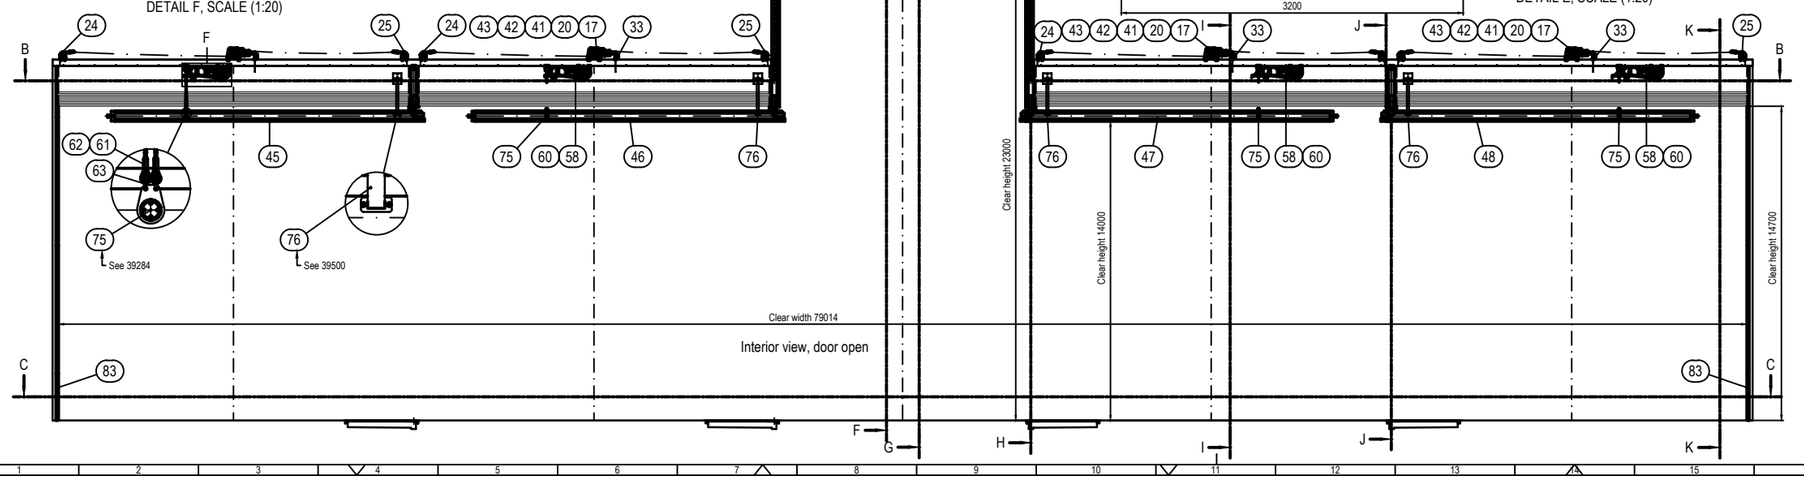

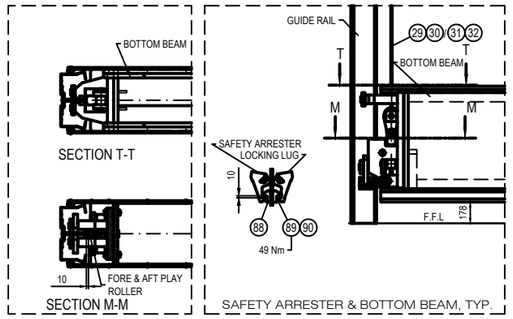

DOOR IDENTITY NUMBER: 84800001

LOAD DIAGRAM & NOTES, ref. to drwng. no. 77446

PARTS LIST ref. to no. 77800.xls

ASSEMBLY, SECTIONS ref. to drwng. no. 77802

ASSEMBLY, PLAN VIEWS ref. to drwng. no. 77801

Stated tightening torque refers to dry screw and nut, unless noted otherwise, and a torque wrench with max. tolerance of ±5%. At re-check, the tightening torque must be within ±25% of stated torque.

DESIGNED: EB	SIZE: A1F	SCALE: 1:100	GMR Aero Technic Hangar1
CODE: 84800	If not otherwise stated: Tolerances ISO 2768-m, EN ISO 13920-B		India
ITEM NO:	Cutting class ISO 9013-442		Megadoor 79014x23000/14000
DATE: 2022-11-03	Weld class ISO 5817-C		Assembly, elevation
ASSA ABLOY	Surface finish Smooth raw surface	DRAWING NO: 77800	REVISION: --

This document is the property of ASSA ABLOY Entrance Systems AB and shall not without our written permission be copied, imported to a third party or used in any manner detrimental thereto.

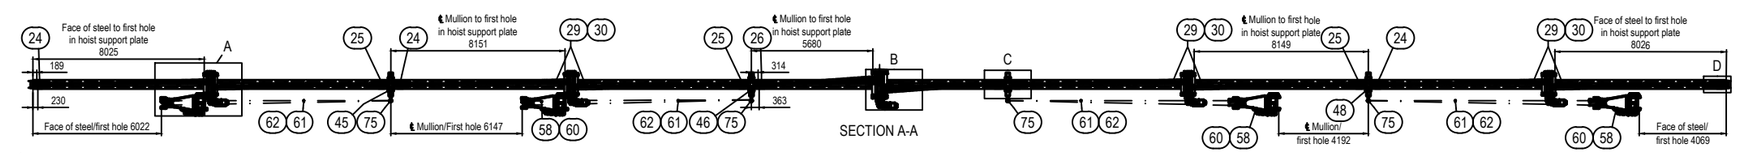

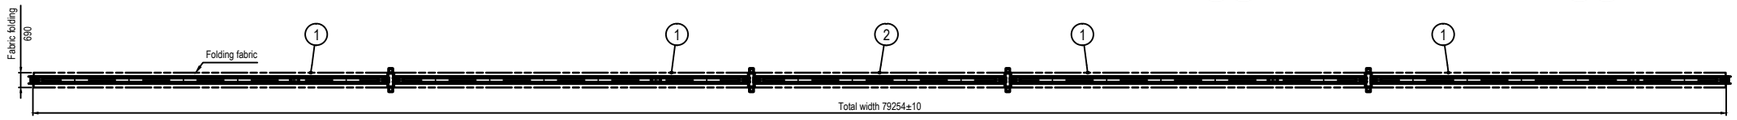

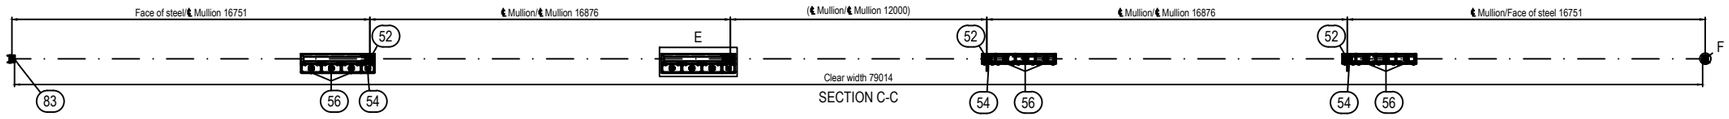

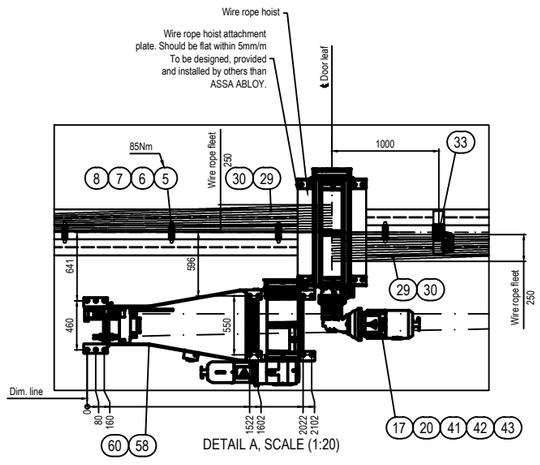

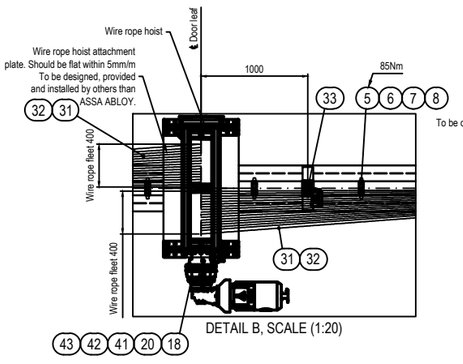

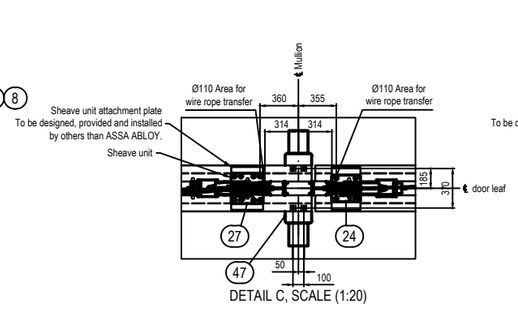

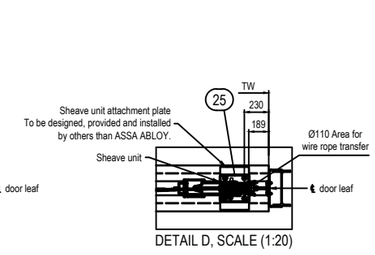

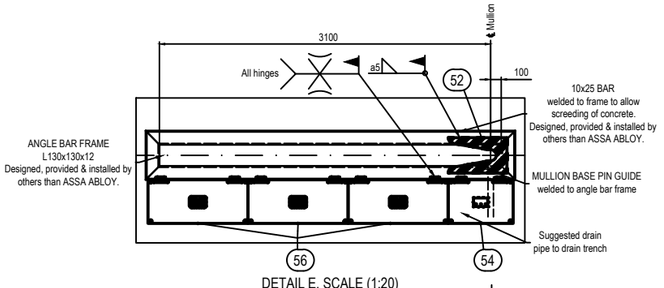

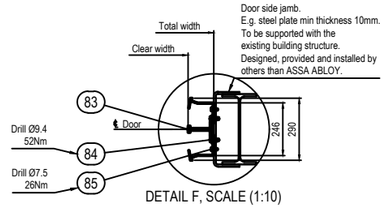

Stated tightening torque refers to dry screw and nut, unless noted otherwise, and a torque wrench with max. tolerance of ±5%. At re-check, the tightening torque must be within ±25% of stated torque.

DOOR IDENTITY NUMBER: 84800001

LOAD DIAGRAM & NOTES, ref. to drwng. no. 77446

PARTS LIST ref. to no. 77800.xls

ASSEMBLY, SECTIONS ref. to drwng. no. 77802

ASSEMBLY, ELEVATION ref. to drwng. no. 77800

DESIGNED: EB	SIZE: A1F	SCALE: 1:100	GMR Aero Technic Hangar1
CODE: 84800	Tolerances ISO 2768-mK EN ISO 13920-B		India
ITEM NO	Coating class ISO 9013-442		Megadoor 79014x23000/14000
DATE: 2022-11-03	Paint class ISO 5817-C		Assembly, plan views
ASSA ABLOY	Surface finish Smooth raw surface	DRAWING NO: 77801	REVISION: --

This document is the property of ASSA ABLOY Entrance Systems AB and may not without our written permission be copied, imported to a third party or used in any manner not authorized by us.

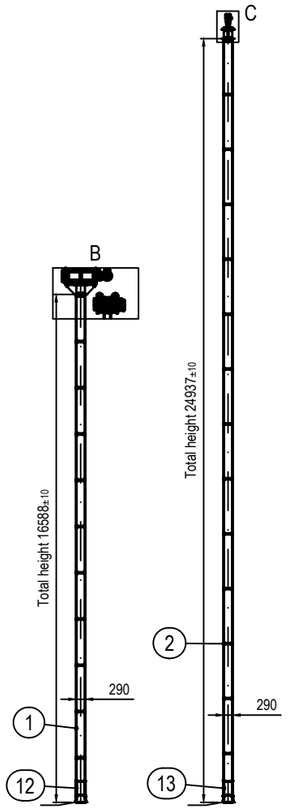

SECTION D-D

SECTION E-E

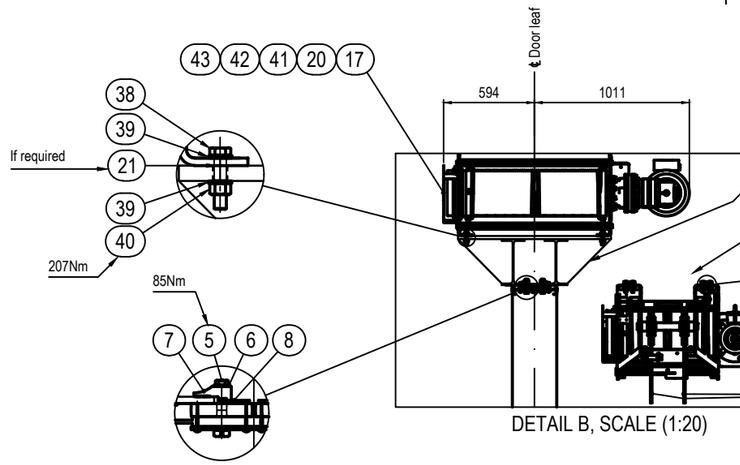

DETAIL B, SCALE (1:20)

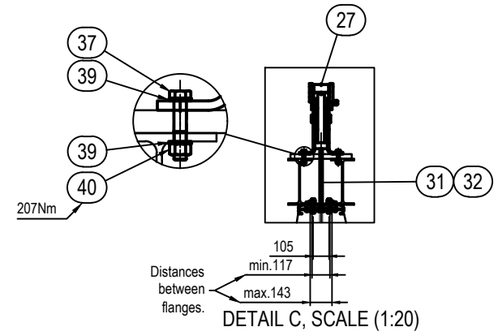

DETAIL C, SCALE (1:20)

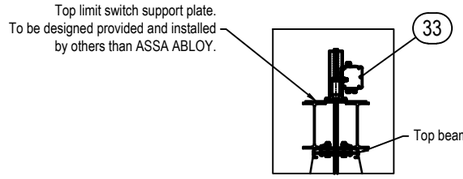

DETAIL E, SCALE (1:20)

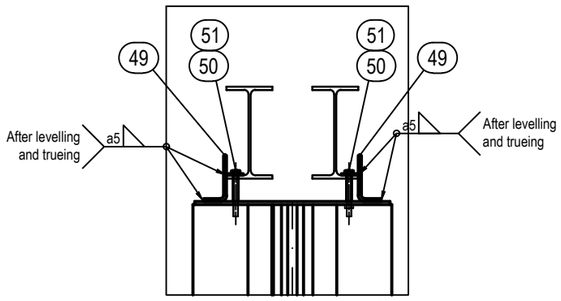

DETAIL F, SCALE (1:10)

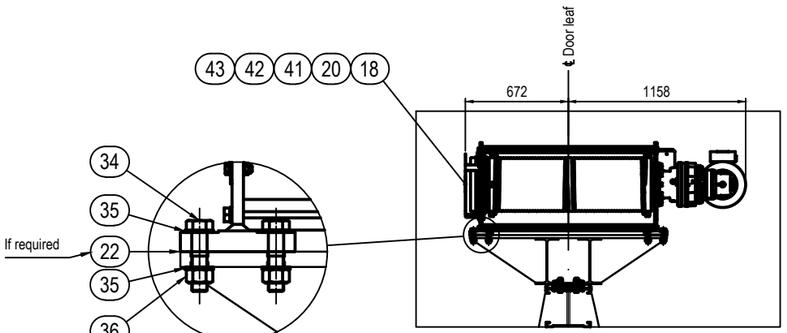

DETAIL D, SCALE (1:20)

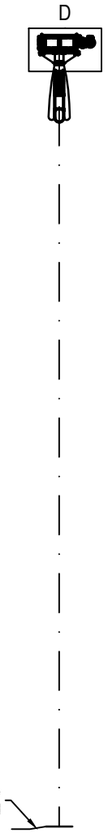

SECTION F-F

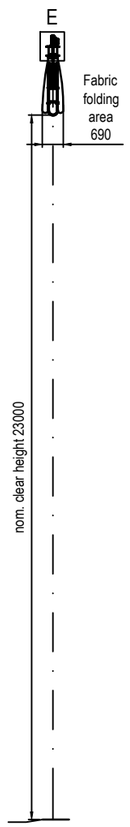

SECTION G-G

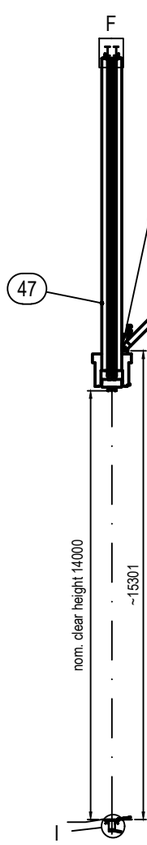

SECTION H-H

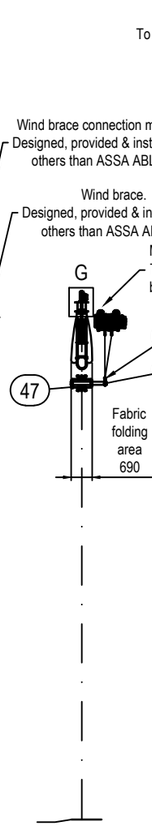

SECTION I-I

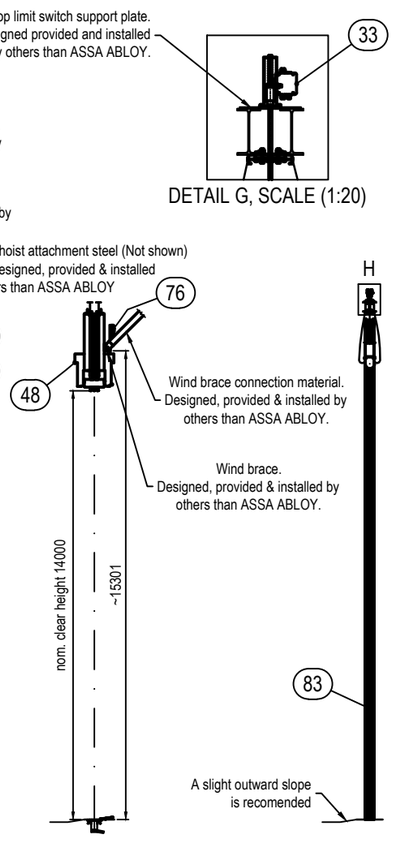

SECTION J-J

SECTION K-K

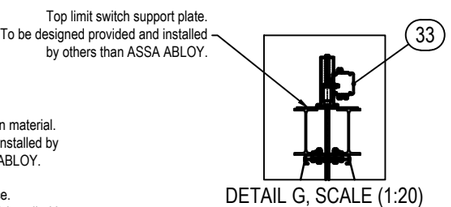

DETAIL G, SCALE (1:20)

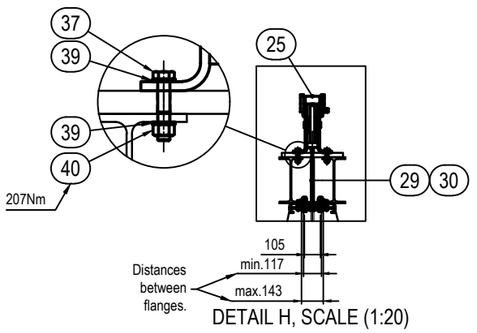

DETAIL H, SCALE (1:20)

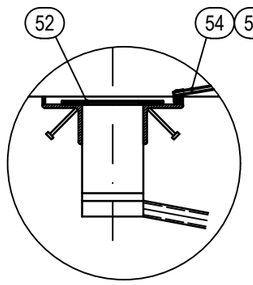

DETAIL I, SCALE (1:10)

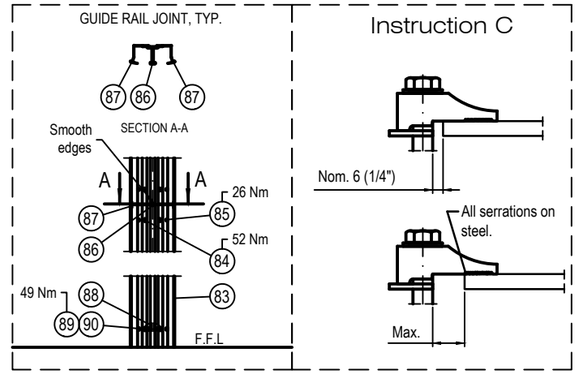

DOOR IDENTITY NUMBER: 84800001

LOAD DIAGRAM & NOTES, ref. to drwng. no. 77446

PARTS LIST ref. to no. 77800.xls

ASSEMBLY, PLAN VIEWS ref. to drwng. no. 77801

ASSEMBLY, ELEVATION ref. to drwng. no. 77800

Stated tightening torque refers to dry screw and nut, unless noted otherwise, and a torque wrench with max. tolerance of ±5%. At re-check, the tightening torque must be within ±25% of stated torque.

DESIGNED EB		SIZE A1	SCALE 1:100
CODE 84800		If not otherwise stated: Tolerances ISO 2768-m EN ISO 13920-B	
ITEM NO		Cutting class ISO 9013-442	
DATE 2022-11-03		Weld class ISO 5817-C	
ASSA ABLOY		Surface finish Smooth raw surface	

GMR Aero Technic Hangar1
India
Megadoor 79014x23000/14000
Assembly, sections

DRAWING NO 77802

REVISION --

PLOT DATE

This document is the property of ASSA ABLOY Entrance Systems AB and shall not be reproduced or otherwise disclosed to third party or used for any other unauthorized purpose.

29							
28							
27							
26	13	Painted Clamp strip Alt. 2		L= 4558	White (RAL9016)	51120	1,3
25	26	Painted Clamp strip Alt. 2		L= 6000	White (RAL9016)	51120	1,7
24							
23							
22							
21	44	Screw		RTS TX 4.8x13		19200242	0,00
20	1	Door leaf signs		Placed as shown on drawing A2-23486		19123486	
19	80	Screw	ZIB	MRT-GF 5x16	Mount on site	19200263	
18	21	Splice plate	AA 6005-T6	440x266		19162369	4,3
17	416	Washer	HB200	BRB 13x24		19200333	0,005
16	80	Nut	BH8	M12 DIN 985		19203172	0,017
15	176	Nut	BH 8	M6M 12		19200225	0,016
14							
13	160	Screw	Cl. 8.8	M6S 12x50		19201681	0,055
12	80	Screw	Cl. 8.8	M6S 12x45		19203177	0,051
11	16	Screw	Cl. 8.8	M6S 12x35		19200812	0,051
10	2430	Screw	Cl. 8.8	RTS TX5.5x16		19204942	0,00
9							
8	9	Painted Clamp strip Alt. 2		L= 4558	Antracite grey (RAL7016)	51124	1,3
7	18	Painted Clamp strip Alt. 2		L= 6000	Antracite grey (RAL7016)	51124	1,7
6	1	Door fabric	(W=16618 L=34000) Ordering dimension	W=16558 L=33466 Finished dimension		77806	408
5	44	Protective stud		Dia.20x10		19100902	
4	20	Intermediate beam guide		For 15mm Guide rail		19149918	12
3							
2	10	Intermediate beam		290x75	L=16071	77805	147
1	1	Top beam		290x60	L=16356	77804	116
Item	**Qty**	**Description**	**Material**	**Dimension**	**Remarks**	**Drawing/ art.no.**	**Weight kg/pc.**

GMR Aero Technic Hangar1
India
Megadoor 79014x23000/14000
Door leaf assembly #1, 2, 4 & 5
Parts list no. 77803.xls
Ref. to assembly drawing no. 77803

Date: 2022-11-02
Project no: 84800
Designed by: EB
Revision: ---

Total weight (kg): **2455**

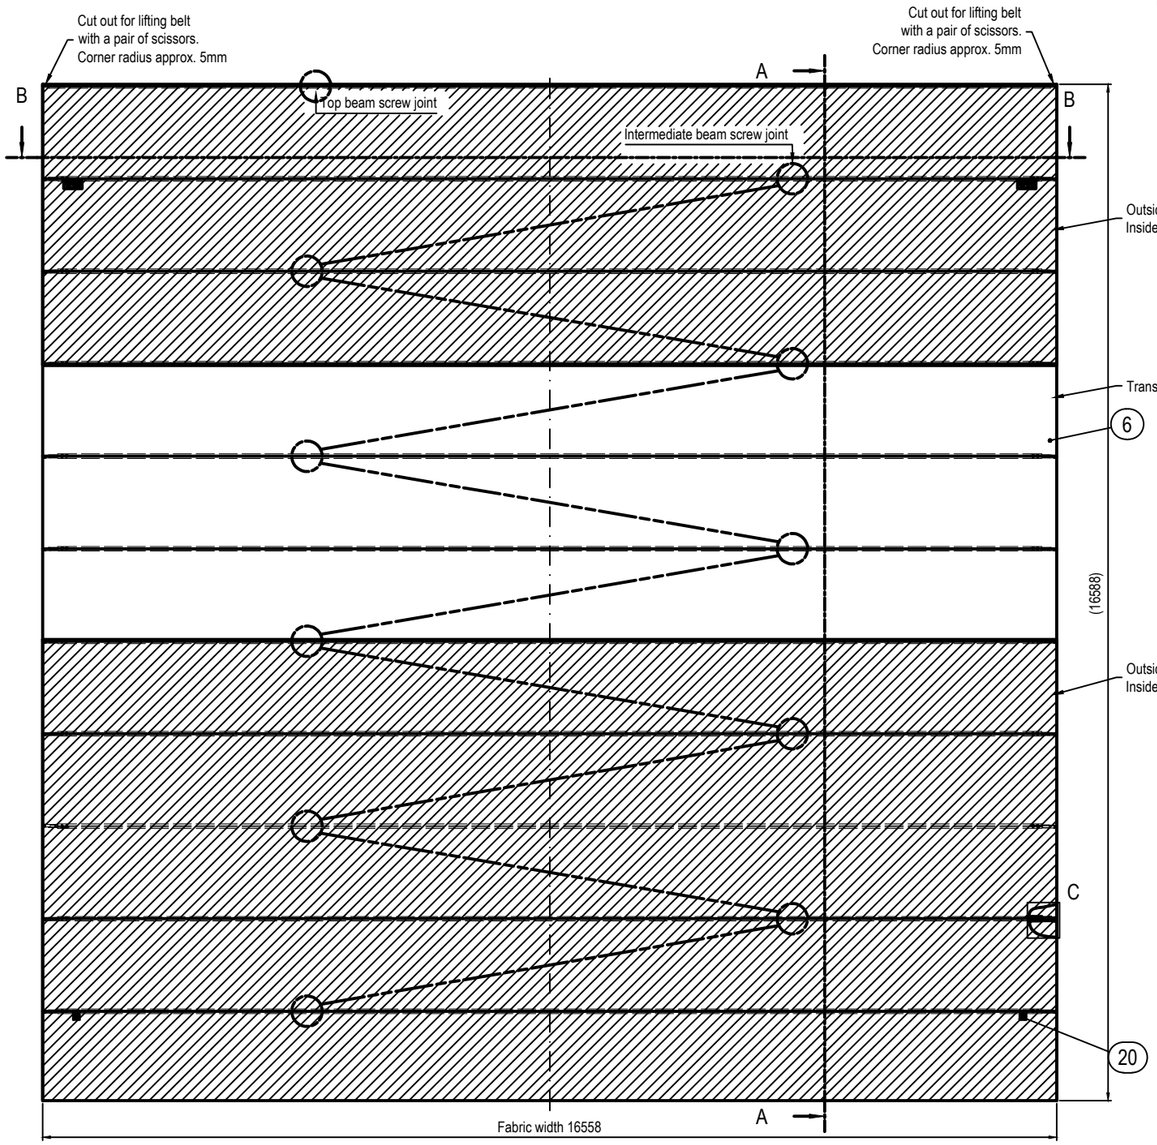

View from exterior side

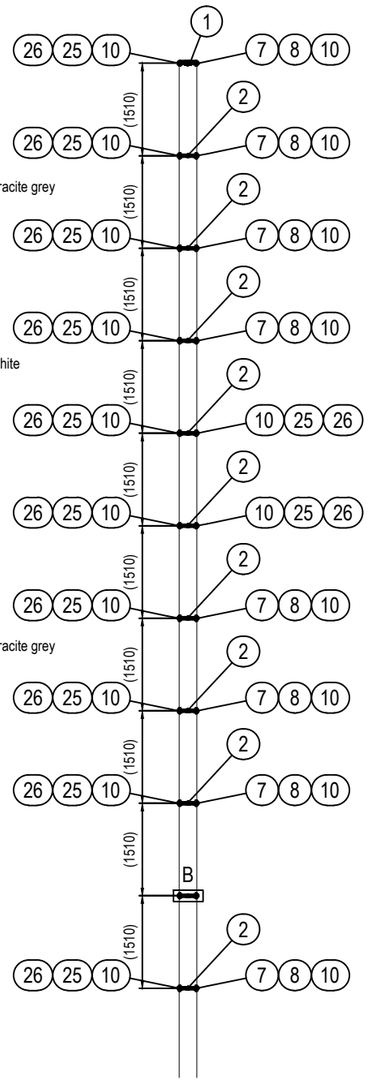

SECTION A-A

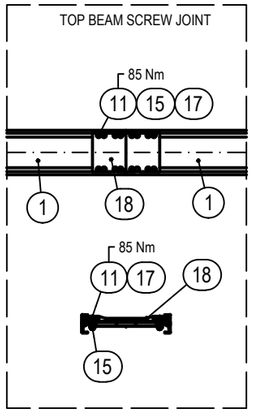

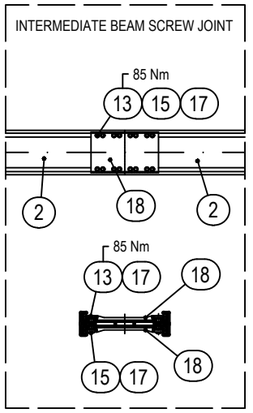

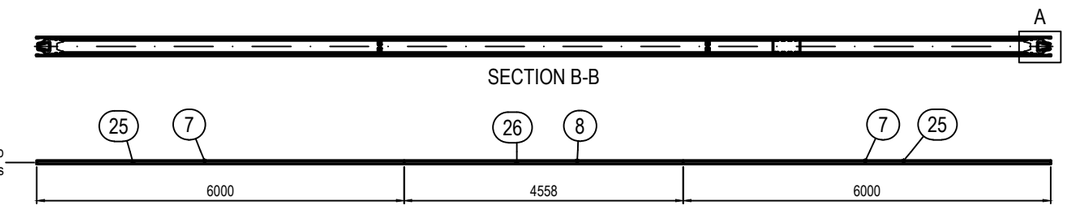

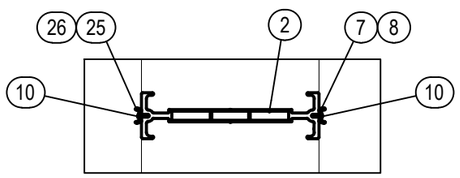

DETAIL B, SCALE (1:5)

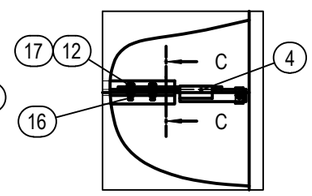

DETAIL C, SCALE (1:10)

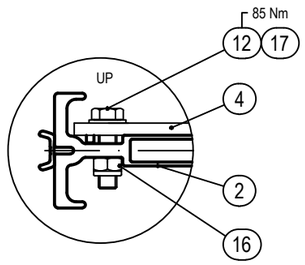

SECTION C-C

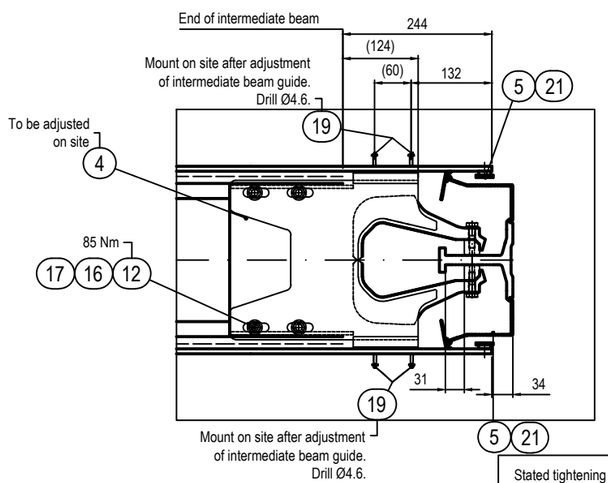

DETAIL A, SCALE (1:5)

Cut out in door fabric at each end of top beam for guide rail and belt penetration.

All cuts must be done with scissors.

Make sure cut outs have radius corners as shown.

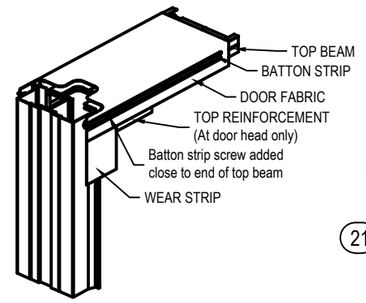

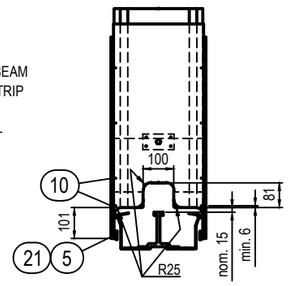

PARTS LIST, ref. to drwng 77803. XLS

Stated tightening torque refers to dry screw and nut, unless noted otherwise, and a torque wrench with max. tolerance of ±5%. At re-check, the tightening torque must be within ±25% of stated torque.

DESIGNED	EB	SIZE	A1
		SCALE	1:50
CODE	84800	If not otherwise stated:	
ITEM NO		Tolerances	ISO 2768-m EN ISO 13920-B
DATE	2022-11-02	Cutting class	ISO 9013-442
		Weld class	ISO 5817-C
ASSA ABLOY		Surface finish	Smooth raw surface

GMR Aero Technic Hangar1
India
Megadoor 79014x23000/14000
Door leaf assembly #1, 2, 4 & 5

DRAWING NO 77803

REVISION --

PLOT DATE

This document is the property of ASSA ABLOY Entrance Systems AB and shall not be copied or otherwise reproduced to a third party or used for any other unauthorized purpose.

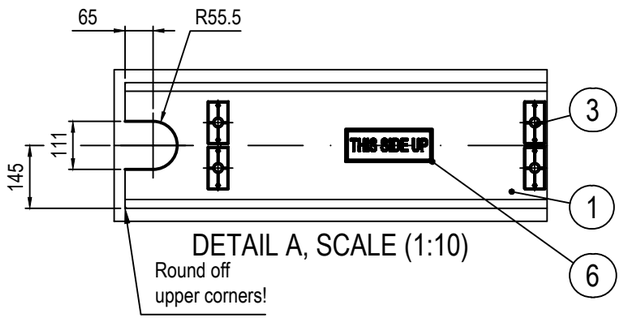

DETAIL A, SCALE (1:10)

Round off
upper corners!

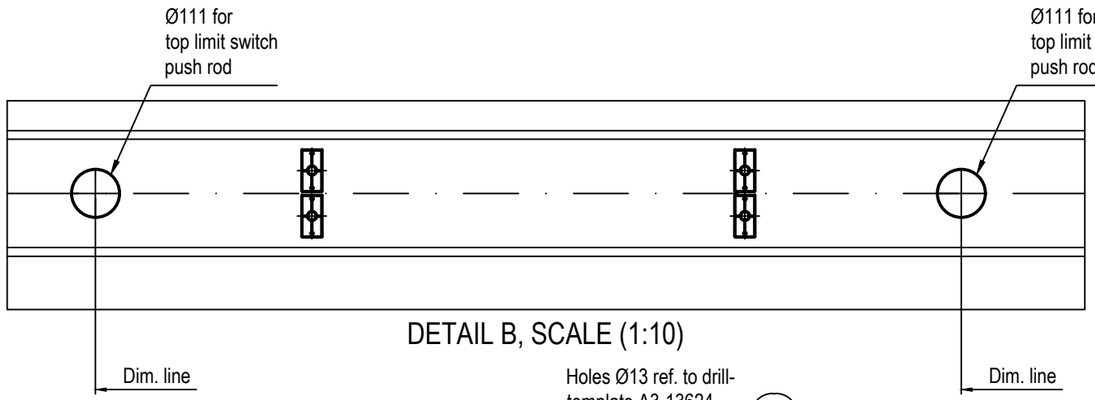

DETAIL B, SCALE (1:10)

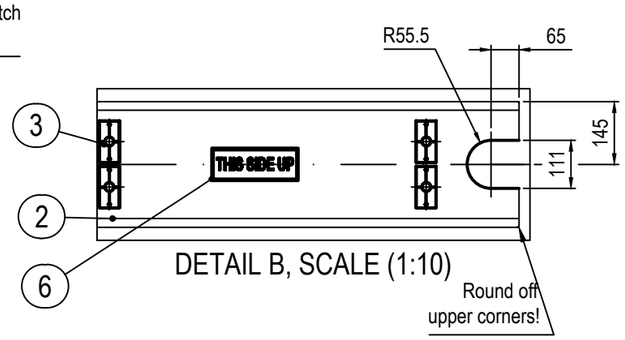

DETAIL B, SCALE (1:10)

Round off
upper corners!

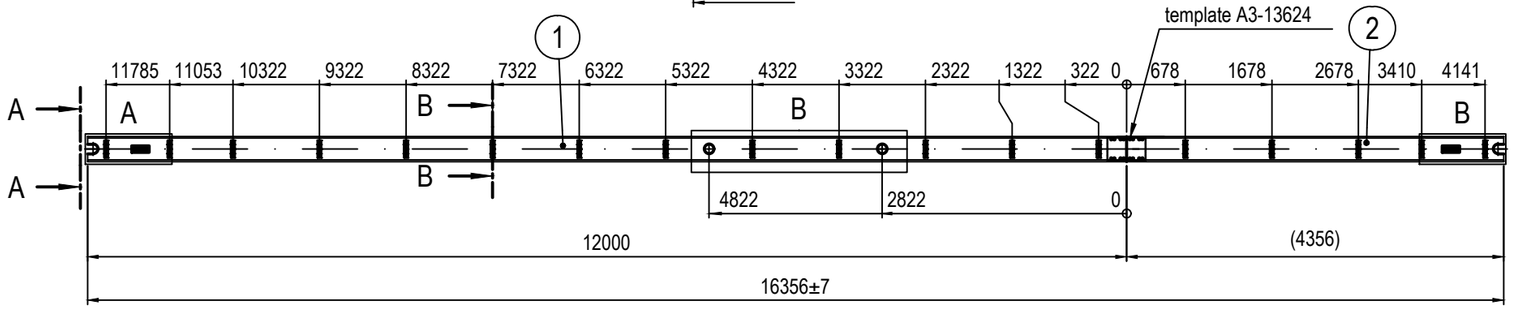

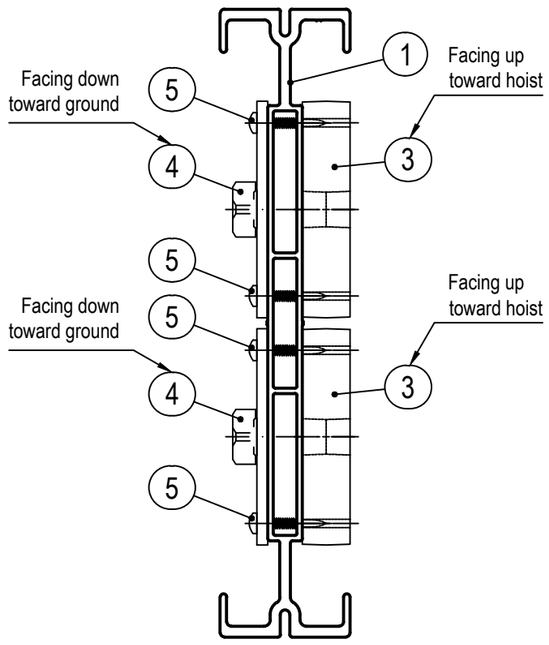

A - A Scale 1:2

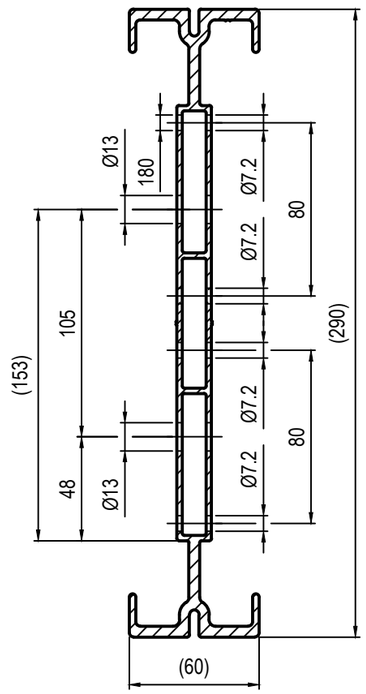

B - B Scale 1:2
Hole drilling typ. @ all
spacers & nut plates

Weight: 116 kg.

ITEM	QTY	DESCRIPTION	DIMENSION	MATERIAL	REMARKS	kg/pc
6	2	Sign	200 x 75		19150987	
5	72	Screw	RTS TX 4,8x38		19203815	
4	36	Nut plate			19113194	0.3
3	36	Spacer			19123449	
2	1	Profile 290x60	L= 4356	6005-T6	19162359	27.9
1	1	Profile 290x60	L= 12000	6005-T6	19162359	76.9

DESIGNED: EB
SIZE: A2
SCALE: 1:50
CODE: 84800
ITEM NO:
DATE: 2022-11-02
If not otherwise stated:
Tolerances ISO 2768-m EN ISO 13920-B
Cutting class ISO 9013-442
Weld class ISO 5817-C
Surface finish Smooth raw surface
ASSA ABLOY

GMR Aero Technic Hangar1

India

Megadoor 79014x23000/14000

Top beam #1, 2, 4 & 5

PLOT DATE

DRAWING NO: 77804

REVISION: --

This document is the property of ASSA ABLOY Entrance Systems AB and shall not without our written permission be copied, imparted to a third party or used for any other unauthorized purpose.

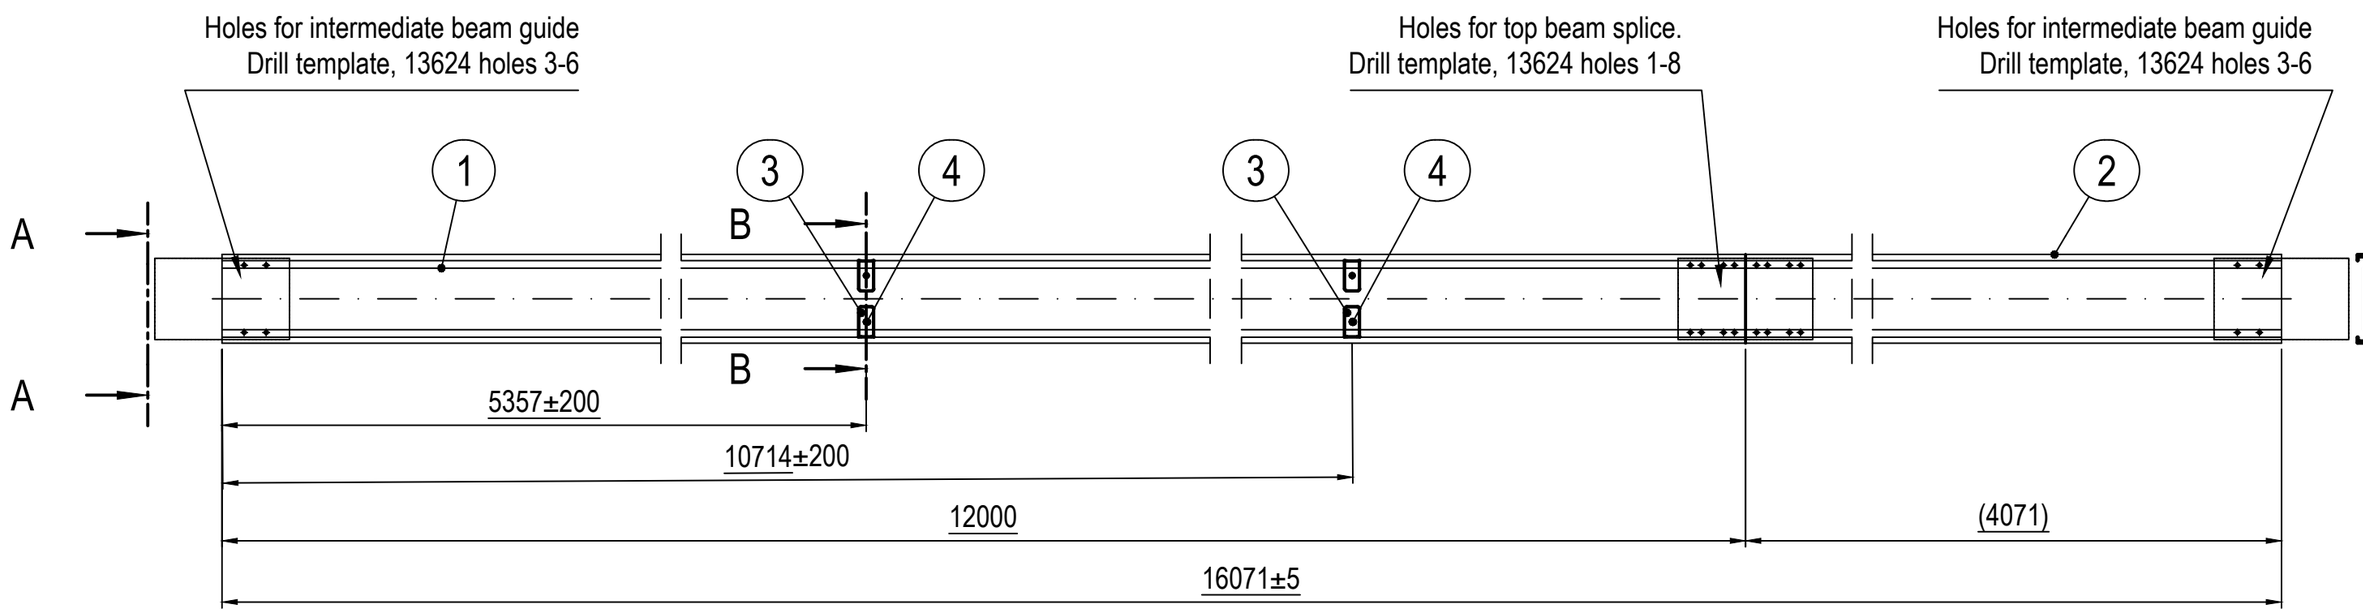

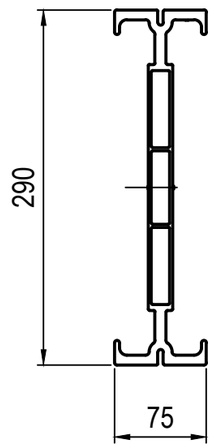

A - A Scale 1:5

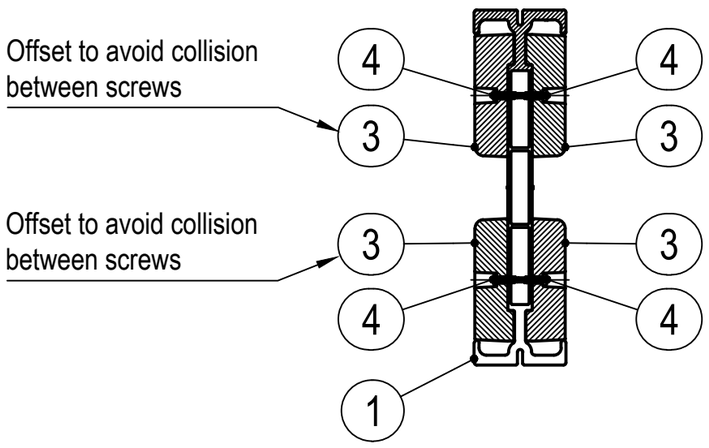

B - B Scale 1:5

Weight= 147 (kg)
Weight= 9.115 (kg/m)

ITEM	QTY	DESCRIPTION	DIMENSION	MATERIAL	REMARKS	kg/pc
4	8	Screw	RTB ST4.8x22		19202674	
3	8	Spacer			19134314	0.1
2	1	Profile 290x75	L= 4071	6005-T6	19162360	37.1
1	1	Profile 290x75	L= 12000	6005-T6	19162360	109.4

DESIGNED: EB
SIZE: A3
SCALE: 1:20
CODE: 84800
ITEM NO:
DATE: 2022-11-02

If not otherwise stated:
Tolerances
ISO 2768-m
EN ISO 13920-B
Cutting class
ISO 9013-442
Weld class
ISO 5817-C
Surface finish
Smooth raw surface

ASSA ABLOY

GMR Aero Technic Hangar1

India

Megadoor 79014x23000/14000

Intermediate beam #1, 2, 4 & 5

PLOT DATE

DRAWING NO: 77805

REVISION: --

This document is the property of ASSA ABLOY Entrance Systems AB and shall not without our written permission be copied, imparted to a third party or used for any other unauthorized purpose.

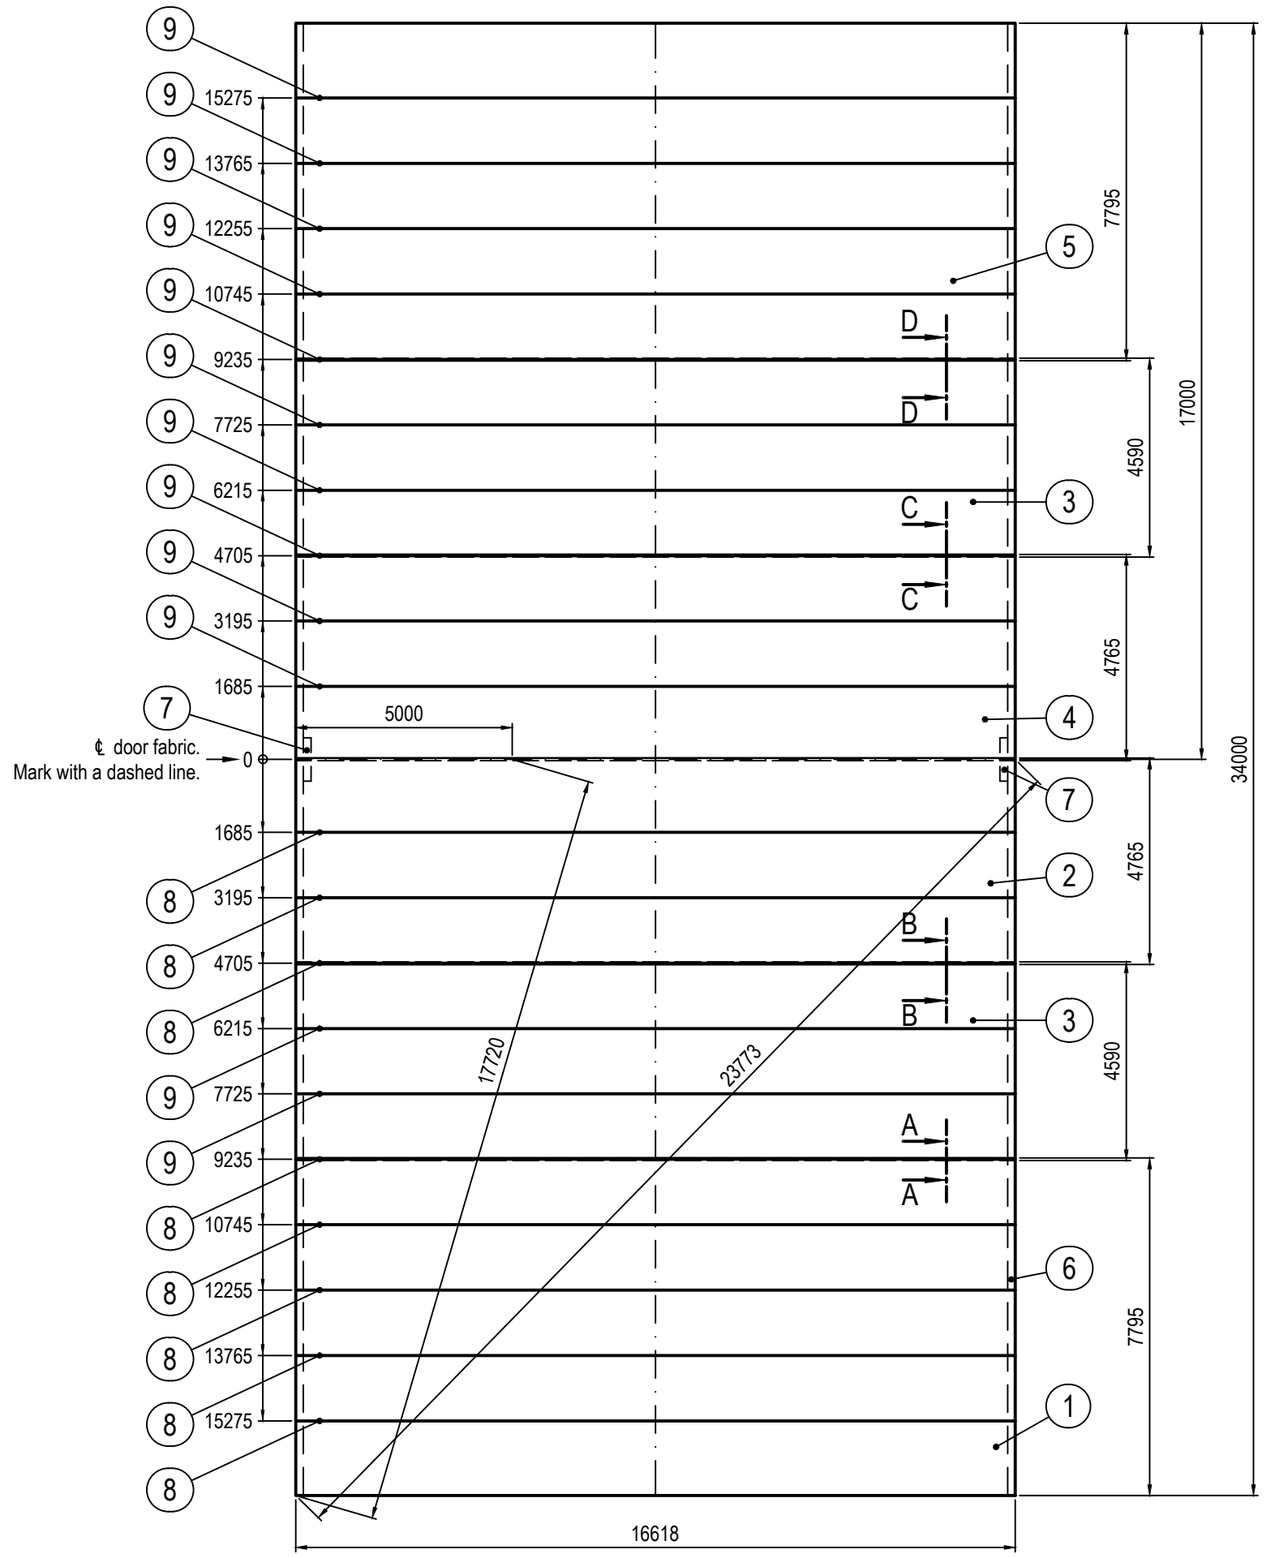

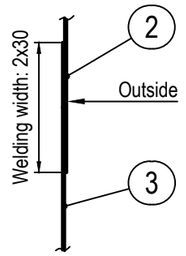

SECTION B-B. SCALE (1:1)

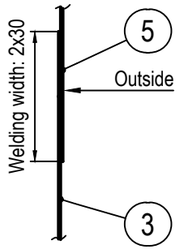

SECTION D-D. SCALE (1:1)

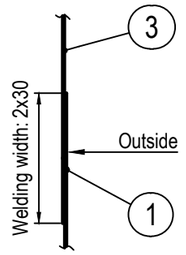

SECTION A-A. SCALE (1:1)

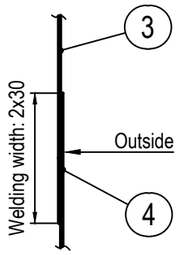

SECTION C-C. SCALE (1:1)

Top reinforcement and wear strip welding acc. to A3-19944

Weight: 408kg

App. lengths

ITEM	QTY	DESCRIPTION	DIMENSION	MATERIAL	REMARKS	kg/pc
9	12	Scribe line	L=16618		19204697, tape & ink	
8	8	Scribe line	L=16618		19203659 Crayon	
7	2	Top reinforcement	W= 175 x L= 1000			0.1
6	2	Wear strip	W= 175 x L= 34000			4.2
5	1	Door Fabric	W= 16618 x L= 7795		Color: White	90.7
4	1	Door Fabric	W= 16618 x L= 4765		Color: White	55.4
3	2	Door Fabric	W= 16618 x L= 4590		Color: Translucent white	53.4
2	1	Door Fabric	W= 16618 x L= 4765		Color: Anthracite grey	55.4
1	1	Door Fabric	W= 16618 x L= 7795		Color: Anthracite grey	90.7

DESIGNED: EB
SIZE: A2
SCALE: 1:100
CODE: 84800
ITEM NO:
DATE: 2022-11-01
If not otherwise stated:
Tolerances ISO 2768-m EN ISO 13920-B
Cutting class ISO 9013-442
Weld class ISO 5817-C
Surface finish Smooth raw surface
ASSA ABLOY

GMR Aero Technic Hangar1

India

Megadoor 79014x23000/14000

Door fabric #1, 2, 4 & 5

PLOT DATE

DRAWING NO: 77806
REVISION: --

This document is the property of ASSA ABLOY Entrance Systems AB and shall not without our written permission be: copied, imparted to a third party or used for any other unauthorized purpose.

Attachment profile related

54	6	Int. Beam support				19162433	0,08
53	6	Screw		MRT-GF 6x20		19200324	0,0066
52	74	Washer		RB 6,4 x 18 x 1,5		19203203	0,0015
51	6	Washer, rubber				19130893	0.0014
50	68	Screw		MRT-GF 6x16		19200452	0,006
49	62	Screw set				19143478	0,0
48							
47	1	Set of clamp strip attachment profiles				77809	78
46							

Bottom seal related

45							
44	222	Screw		RTS TX 5.5x19	Geomet	19204943	0,00
43							
42	2	Clamp strip		30x6 #2	L= 4558	19151078	1,3
41	4	Clamp strip		30x6 #2	L= 6000	19151078	1,7
40	1	Rubber seal	900 EPDM Grey	4x900	L= 16558 Finished Dimension	19203302	84,6

Bottom beam related

39							
38							
37							
36							
35							
34	1	Painted Clamp strip Alt. 2	Antracite grey (RAL7	30x6 #2	L= 4558	51124	1,3
33	2	Painted Clamp strip Alt. 2	Antracite grey (RAL7	30x6 #2	L= 6000	51124	1,7
32	1	Shims for bottom beam screw joint				19128506	
31	2	Nut	Class 8.8	M6M 20		19201687	0,053
30	4	Nut	Class 8.8	M6M 24		19203273	0,073
29	4	Washer	HB 200	21x36 t=3		19200202	0,011
28	8	Washer	HB 200	25x45 t=4		19203274	0,016
27	2	Screw	Class 8.8	M6S 20x70		19203191	0,22
26	4	Screw	Class 8.8	M6S 24x75		19203422	0,3
25	8	Washer		TBRSUB 13x36		19200211	0,041
24	8	Screw	Class 8.8	M6S 12x50		19201681	0,055
23							
22							
21							
20							
19	222	Screw		RTS TX 5.5x19		19204943	0,00
18	222	Screw		KFTS 5.5x16		19204944	0,00
17	222	Screw		RTS TX 5.5x16		19204942	0,00
16	12	Protective stud		Dia.20x10		19100902	
15	4	Screw		RTS TX 4.8x13		19200242	0,00
14	8	Screw		RTS TX 4.8x16		19200320	0,00
13							
12	2	Clamp strip		30x6 #3	L= 4558	19151079	1,3
11	4	Clamp strip		30x6 #3	L= 6000	19151079	1,7
10							
9	1	Painted Clamp strip Alt. 2	White (RAL9016)	30x6 #2	L= 4558	51120	1,3
8	2	Painted Clamp strip Alt. 2	White (RAL9016)	30x6 #2	L= 6000	51120	1,7
7							
6	2	Clamp strip		15x3 #1	L= 4558	19151077	0,6
5	4	Clamp strip		15x3 #1	L= 6000	19151077	0,7
4	2	Link			11&12 mm	19122913	7
3	2	Safety arrester				19149915	50
2							
1	2	Bottom beam half		L= 8065	290x450	77808	342
Item	**Qty**	**Description**	**Material**	**Dimension**	**Remarks**	**Drawing/ art.no.**	**Weight kg/pc.**

GMR Aero Technic Hangar1
India
Megadoor 79014x23000/14000
Bottom beam assembly #1, 2, 4 & 5
Parts list no. 77807.xls
Ref. to assembly drawing no. 77807

Date: 2022-10-31
Project no: 84800
Designed by: EB
Revision: ---

Total weight (kg): **999**

DETAIL 3, SCALE (1:4)

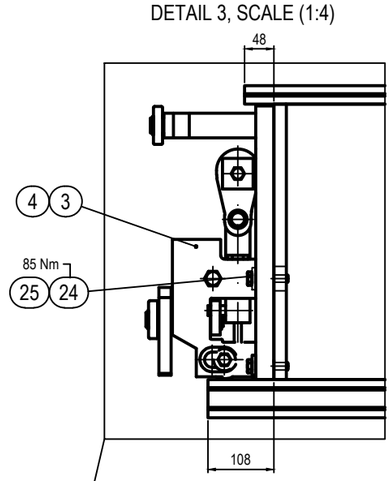

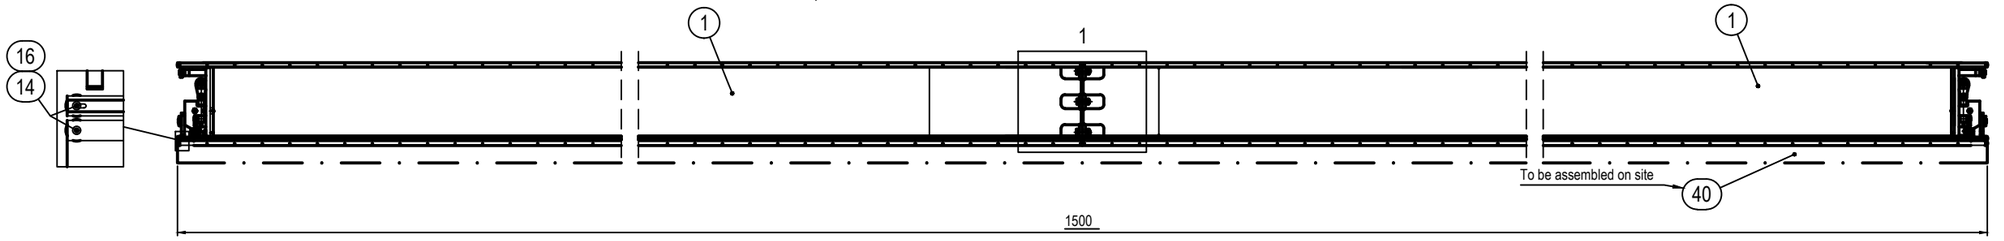

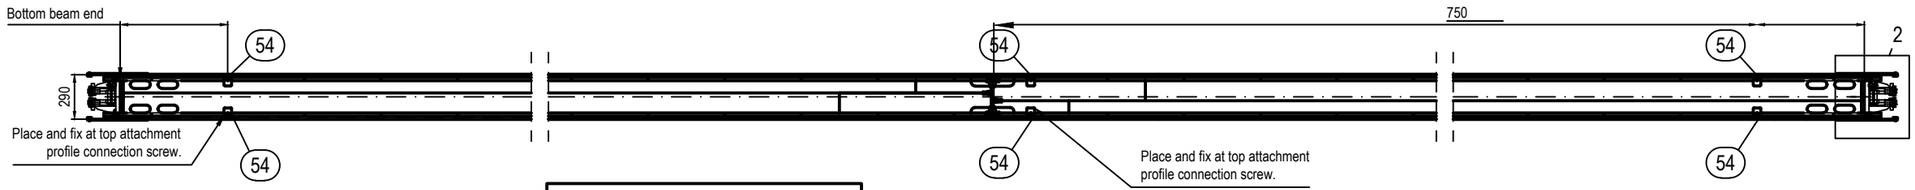

DRILL INSTRUCTIONS
Drill additional holes Ø5.5 thru attachment profiles into bottom beam if distance between bottom beam splice & 1st predrilled hole exceeds 250mm. Drill holes close to joint.

3

BOTTOM BEAM PREPARED FOR TRANSPORTATION
SCALE 1:10

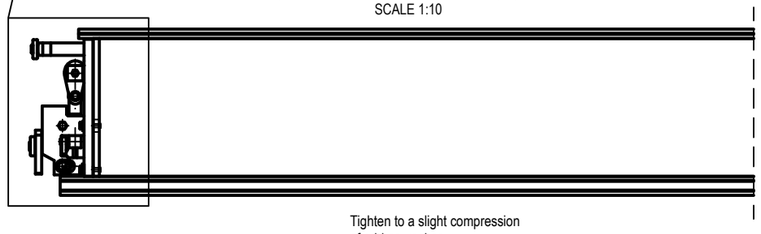

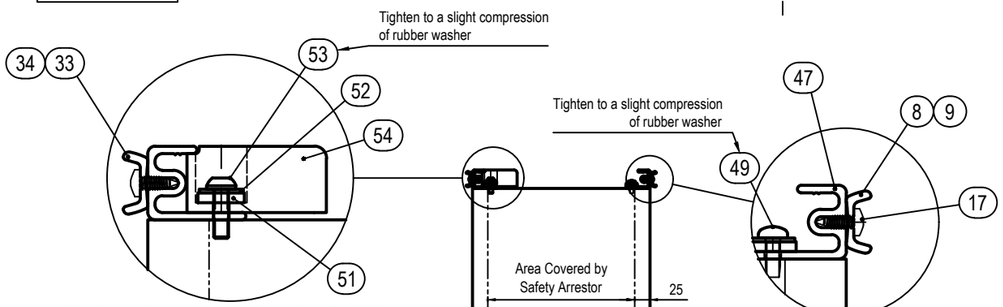

NOTE:DETAIL ONLY AT INTERMEDIATE BEAM SUPPORT

VIEW A-A,SCALE 1:5

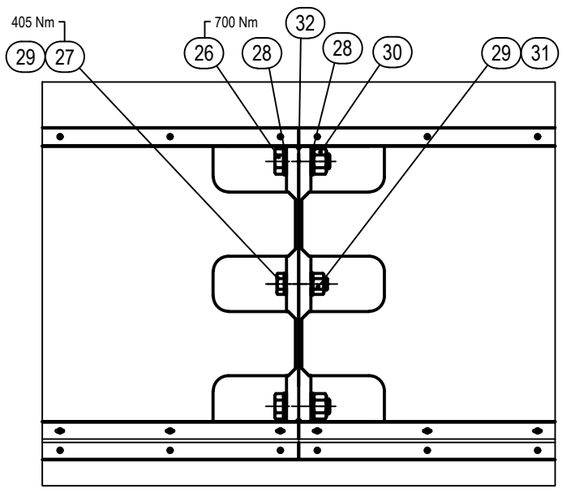

DETAIL 1, SCALE (1:5)

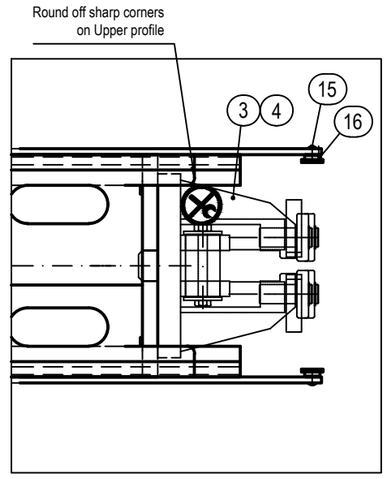

DETAIL 2, SCALE (1:4)

Beam length= 1500

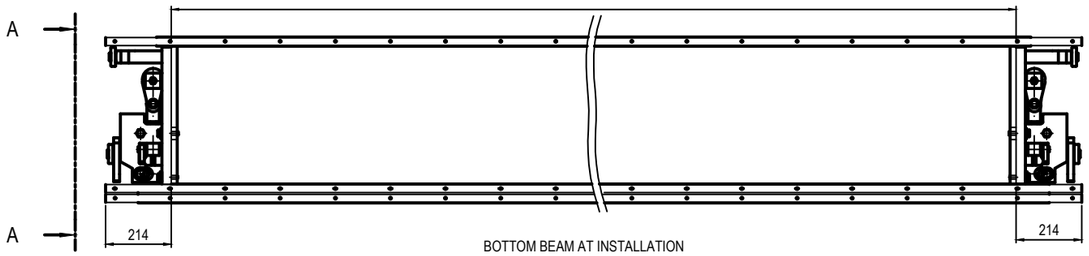

BOTTOM BEAM AT INSTALLATION
Interior view
SCALE 1:10

TITLE - MEGA DOOR				NIHVA TECHNOLOGIES PVT.LTD.PUNE
DWG NO -			QTY - 1	NIHVA Technologies Pvt. Ltd. Website - www.nihva.com
	NAME	SIGNATURE	DATE	PROJECT NO -
DRAWN	S.W		17-07-2025	PRODUCT -
CHK'D	P.M.		17-72025	SITE LOCATION -
APPV'D	V.T.		17-07-2025	
if any queries contact - supportautomation@nihva.com				REVISION -
ALL DIMENSION ARE IN mm		A3		SCALE - SHEET 1 OF 1

This document is the property of ASSA ABLOY Entrance Systems AB and shall not be reproduced or disclosed to a third party or used for any other unauthorized purpose.

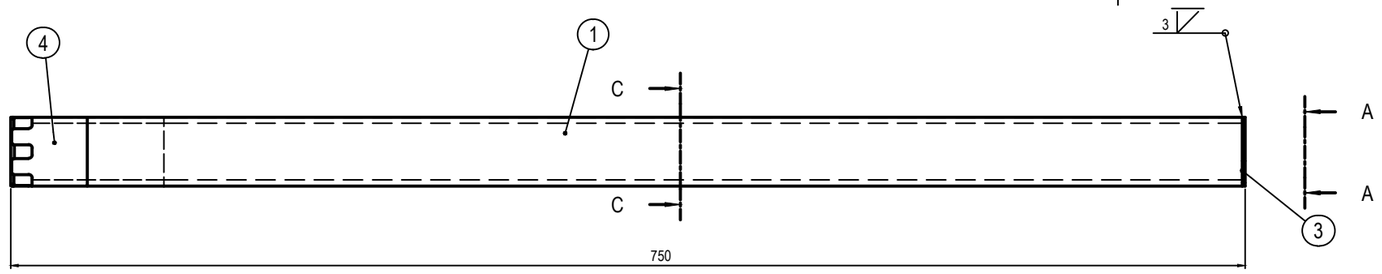

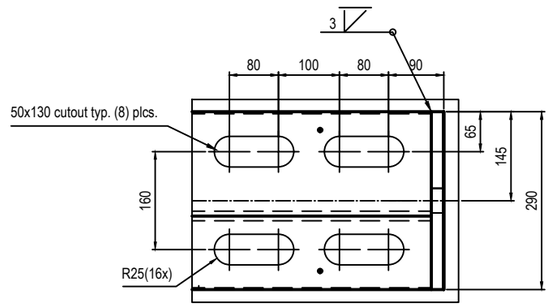

DETAIL A, SCALE (1:5)

HOLE TEMPLATE
Top of Bottom beam

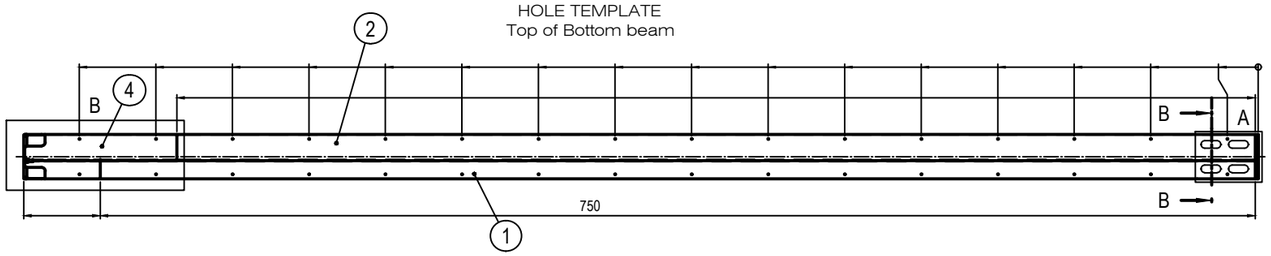

HOLE TEMPLATE
Bottom of Bottom beam

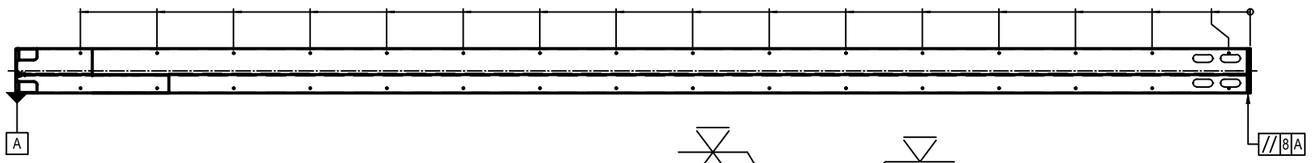

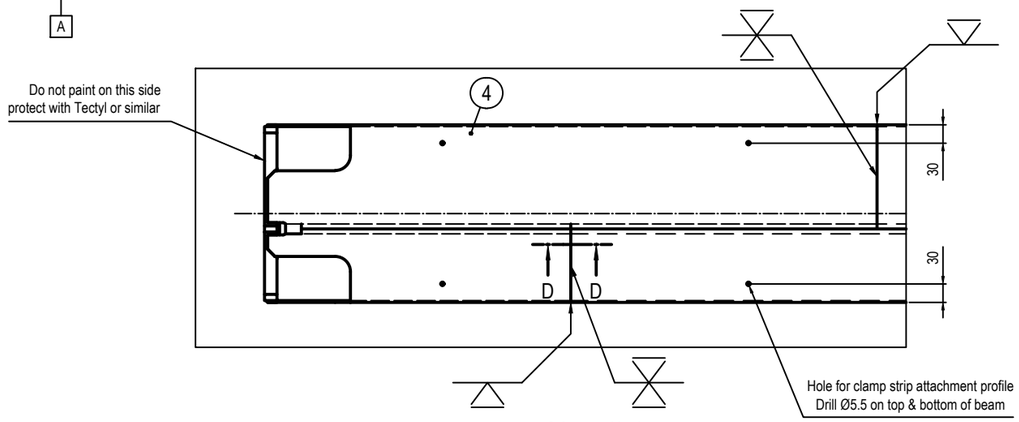

DETAIL B, SCALE (1:5)

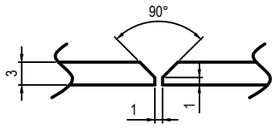

SECTION D-D, SCALE 1:1. Weld prep.

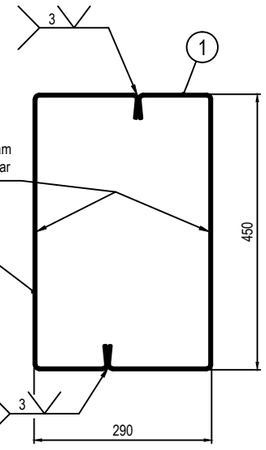

Section C-C
Scale 1:5

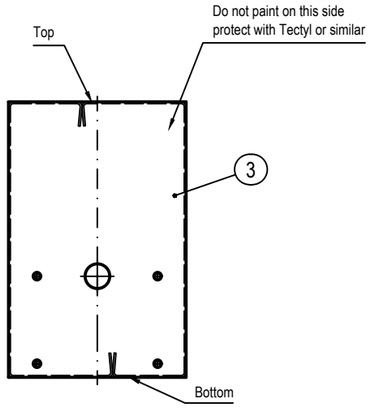

View A-A Scale 1:5

Section B-B
Scale 1:5

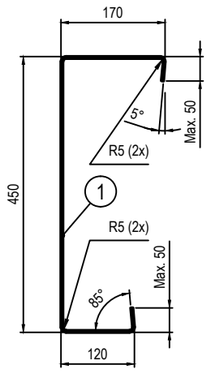

Pos 1 forming layout
Scale 1:5

Surface treatment: A4-1500 Standard Color: Light grey (RAL 7047).
Surface treatment area: 1198 dm² Surface treatment area/m: 148.5 dm² Perimeter: 1480 mm Cross section area: 4776 mm² Weight: 342 kg
Wx = 660 cm3 Wy = 460 cm3 Zx = 806 cm3 Zy = - cm3 Ix = 14959 cm4 Iy = 6668 cm4
Grind all sharp edges and welding sparks after welding. This to prevent fabric wear.

TITLE - MEGA DOOR				NIHVA TECHNOLOGIES PVT.LTD.PUNE
DWG NO -			QTY - 1	Website - www.nihva.com
	NAME	SIGNATURE	DATE	PROJECT NO -
DRAWN	S.W		17-07-2025	PRODUCT -
CHK'D	P.M.		17-72025	SITE LOCATION -
APPV'D	V.T.		17-07-2025	
if any queries contact - supportautomation@nihva.com				REVISION -
ALL DIMENSION ARE IN mm			A3	SCALE - SHEET 1 OF 1

This document is the property of ASSA ABLOY Entrance Systems AB and shall not be reproduced or otherwise disclosed to a third party or used for any other unauthorized purpose.

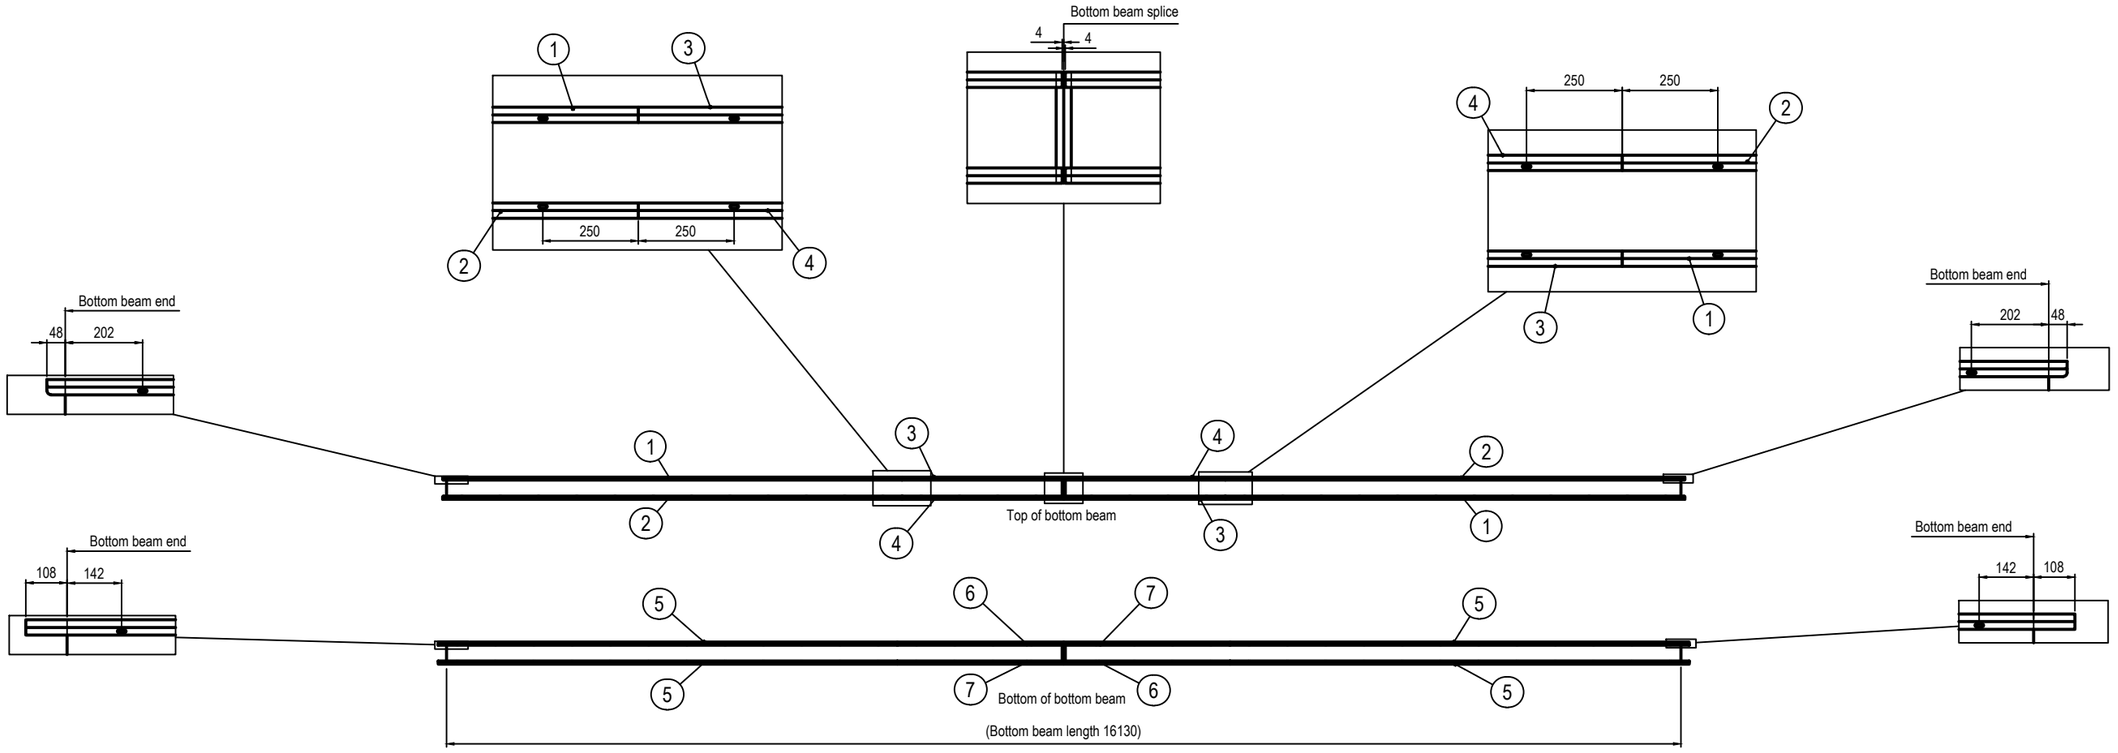

Positioning of clamp strip attachment profiles
Scale 1:40

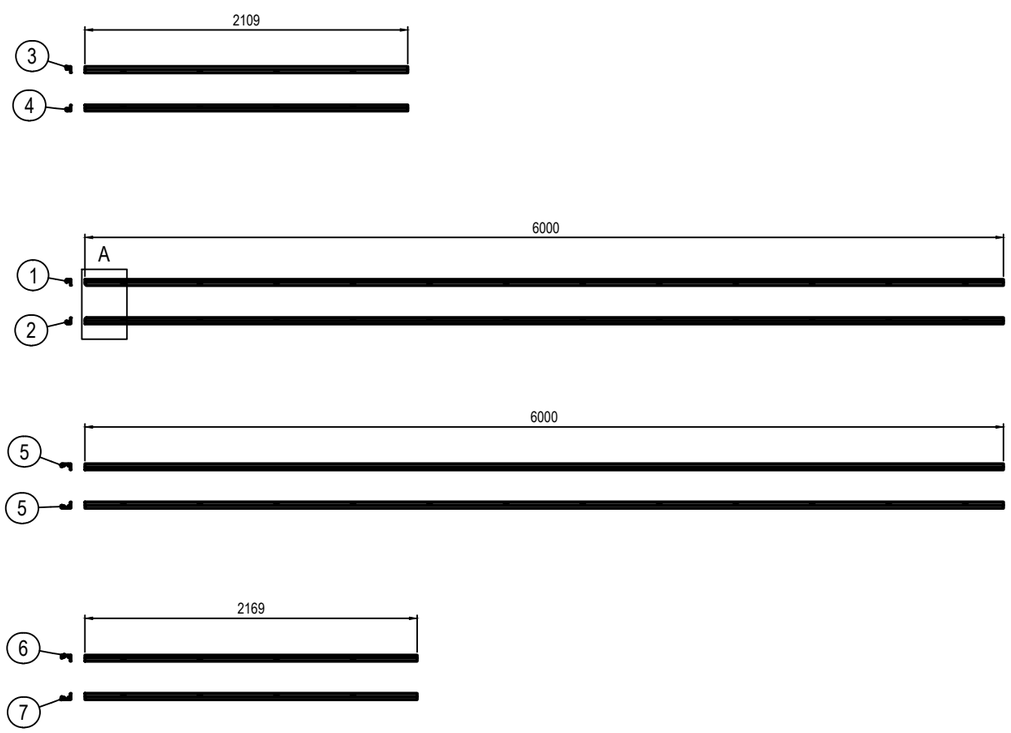

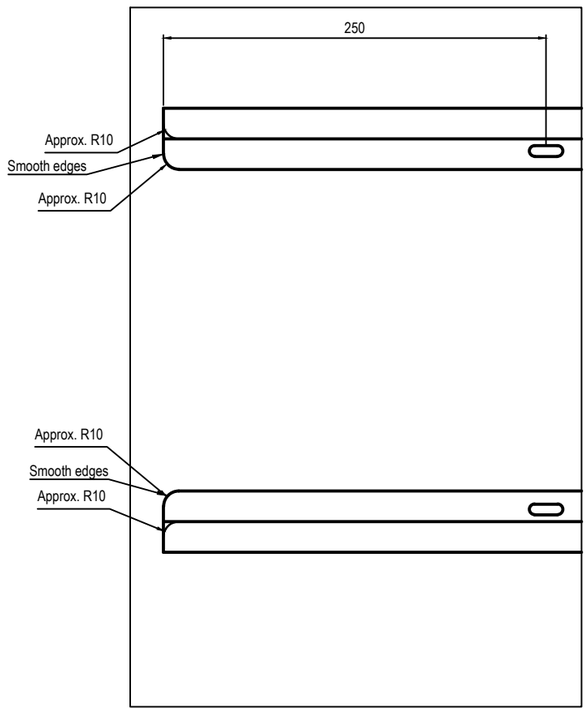

DETAIL A, SCALE (1:2)
Upper profile only
Only one side per profile

Weight: 78 kg

ITEM	QTY	DESCRIPTION	DIMENSION	MATERIAL	REMARKS	kg/pc
7	2	Clamp strip attachment profile, lower	L= 2169		19162431	3.3
6	2	Clamp strip attachment profile, lower	L= 2169		19162431	3.3
5	4	Clamp strip attachment profile, lower	L= 6000		19162431	9.1
4	2	Clamp strip attachment profile, upper	L= 2109		19162430	1.8
3	2	Clamp strip attachment profile, upper	L= 2109		19162430	1.8
2	2	Clamp strip attachment profile, upper	L= 6000		19162430	5.2
1	2	Clamp strip attachment profile, upper	L= 6000		19162430	5.2

DESIGNED: EB
SIZE: A1
SCALE: 1:20
CODE: 84800
ITEM NO
DATE: 2022-10-31
If not otherwise stated:
Tolerances: ISO 2768-m, EN ISO 13920-B
Cutting class: ISO 9013-442
Weld class: ISO 5817-C
Surface finish: Smooth raw surface

GMR Aero Technic Hangar1

India

Megadoor 79014x23000/14000

Clamp strip attachment profiles #1, 2, 4 & 5

DRAWING NO: 77809
REVISION: --
PLOT DATE

This document is the property of ASSA ABLOY Entrance Systems AB and shall not be reproduced or handed over to a third party or used for any other unauthorized purpose.

29							
28							
27							
26	17	Painted Clamp strip Alt. 2		L= 5682	White (RAL9016)	51120	1,6
25	17	Painted Clamp strip Alt. 2		L= 6000	White (RAL9016)	51120	1,7
24							
23							
22							
21							
20	1	Door leaf signs		Placed as shown on drawing A2-23486		19123486	
19	104	Screw	ZIB	MRT-GF 5x16	Mount on site	19200263	
18							
17	104	Washer	HB200	BRB 13x24		19200333	0,005
16	104	Nut	BH8	M12 DIN 985		19203172	0,017
15							
14							
13							
12	104	Screw	Cl. 8.8	M6S 12x45		19203177	0,051
11							
10	2180	Screw	Cl. 8.8	RTS TX5.5x16		19204942	0,00
9							
8	11	Painted Clamp strip Alt. 2		L= 5682	Antracite grey (RAL7016)	51124	1,6
7	11	Painted Clamp strip Alt. 2		L= 6000	Antracite grey (RAL7016)	51124	1,7
6	1	Door fabric	(W=11742 L=51000) Ordering dimension	W=11682 L=50164 Finished dimension		77813	432
5	56	Protective stud		Dia.20x10		19100902	
4	26	Intermediate beam guide		For 15mm Guide rail		19149918	12
3							
2	13	Intermediate beam		290x60	L=11195	77812	72
1	1	Top beam		290x60	L=11480	77811	82
Item	**Qty**	**Description**	**Material**	**Dimension**	**Remarks**	**Drawing/ art.no.**	**Weight kg/pc.**

GMR Aero Technic Hangar1
India
Megadoor 79014x23000/14000
Door leaf assembly #3
Parts list no. 77810.xls
Ref. to assembly drawing no. 77810

Date: 2022-11-01
Project no: 84800
Designed by: EB
Revision: ---

Total weight (kg): **1865**

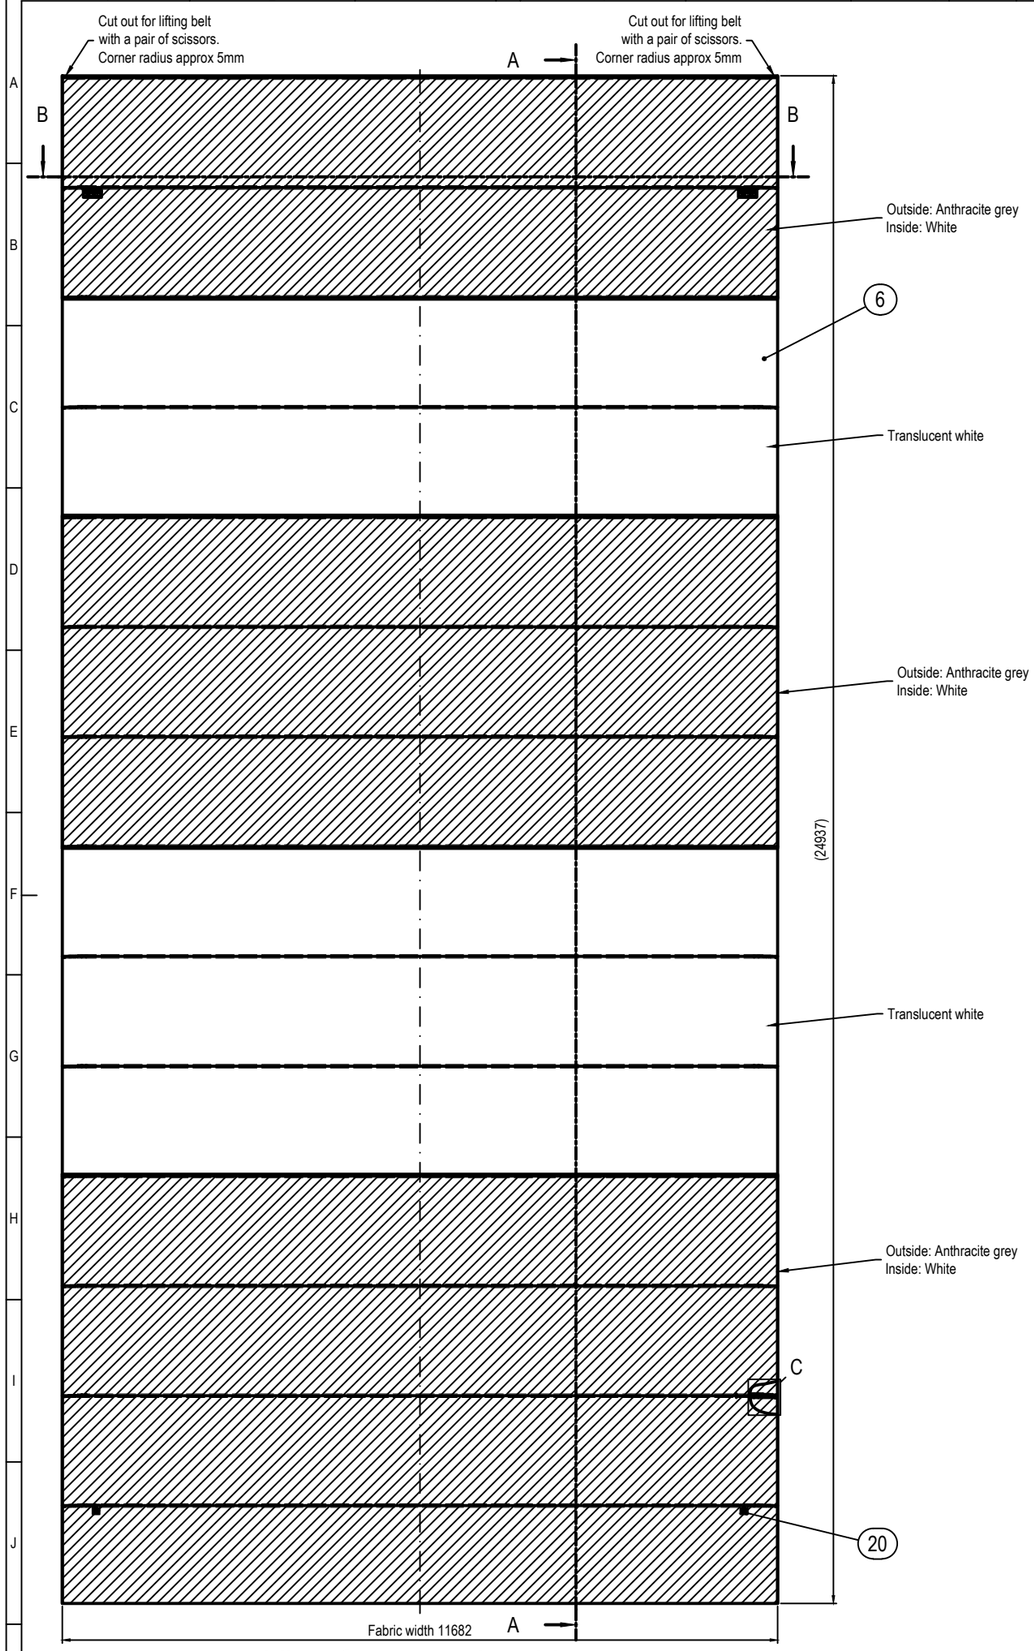

View from exterior side

SECTION B-B

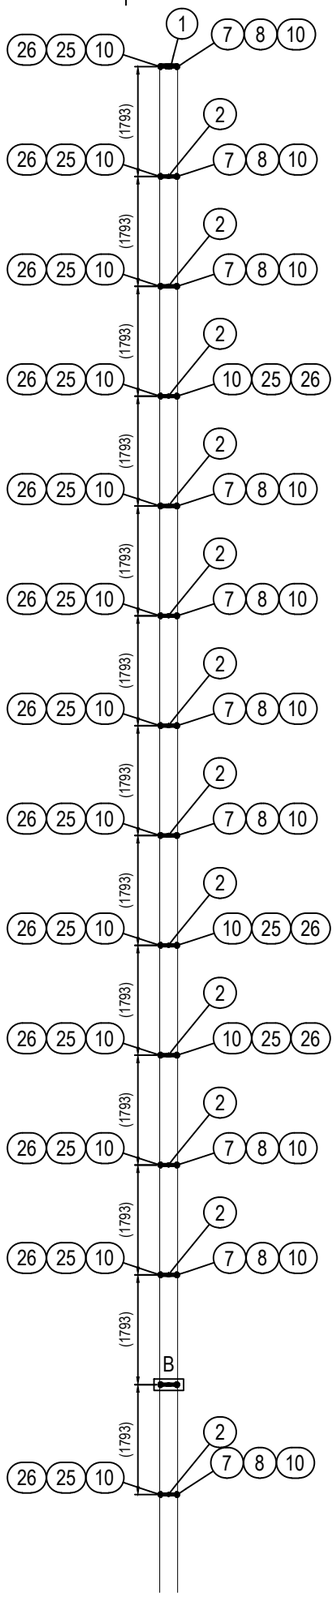

SECTION A-A

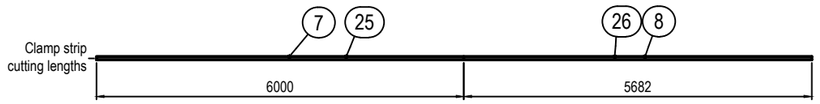

Cut out in door fabric at each end of top beam for guide rail and belt penetration.

All cuts must be done with scissors.

Make sure cut outs have radius corners as shown.

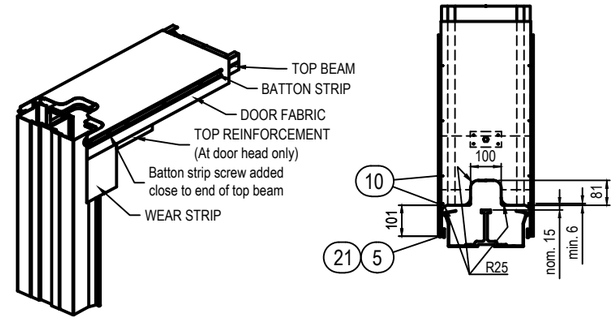

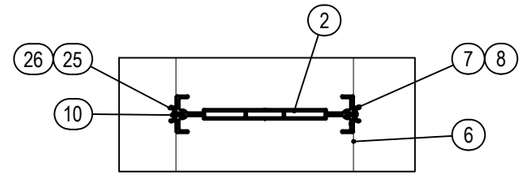

DETAIL B, SCALE (1:5)

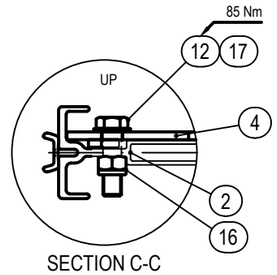

SECTION C-C

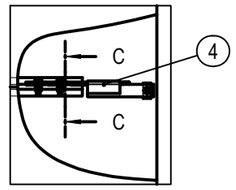

DETAIL C, SCALE (1:10)

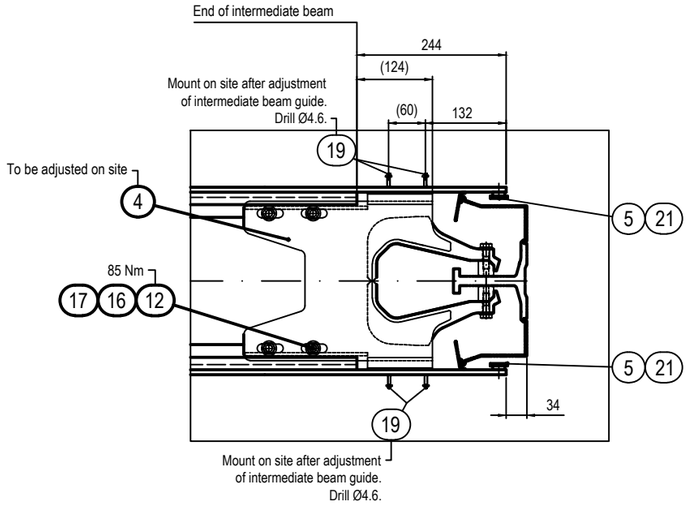

DETAIL A, SCALE (1:5)

PARTS LIST, ref. to drwng 77810.XLS

Stated tightening torque refers to dry screw and nut, unless noted otherwise, and a torque wrench with max. tolerance of ±5%. At re-check, the tightening torque must be within ±25% of stated torque.

DESIGNED EB		SIZE A1	SCALE 1:50
CODE 84800		If not otherwise stated:	
ITEM NO		Tolerances ISO 2768-m EN ISO 13920-B	
DATE 2022-11-01		Cutting class ISO 9013-442	
ASSA ABLOY		Weld class ISO 5817-C	
		Surface finish Smooth raw surface	

GMR Aero Technic Hangar1
India
Megadoor 79014x23000/14000
Door leaf assembly #3

DRAWING NO 77810

REVISION --

PLOT DATE

This document is the property of ASSA ABLOY Entrance Systems AB and shall not be reproduced, disclosed or used without permission, nor reproduced to a third party or used for any other unauthorized purpose.

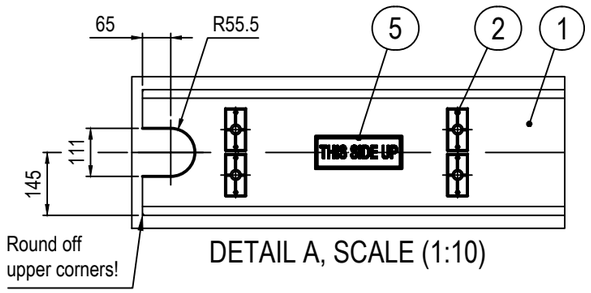

DETAIL A, SCALE (1:10)

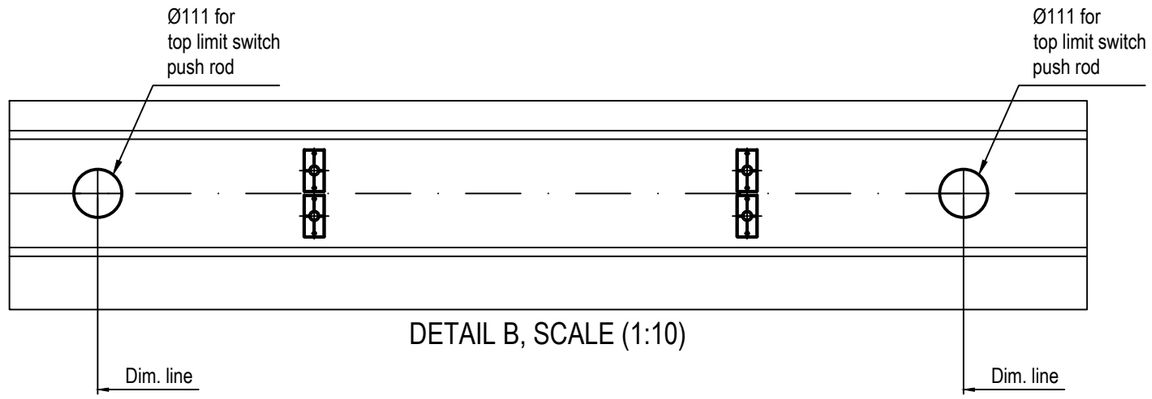

DETAIL B, SCALE (1:10)

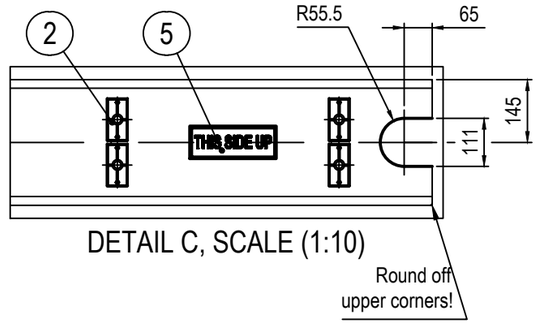

DETAIL C, SCALE (1:10)

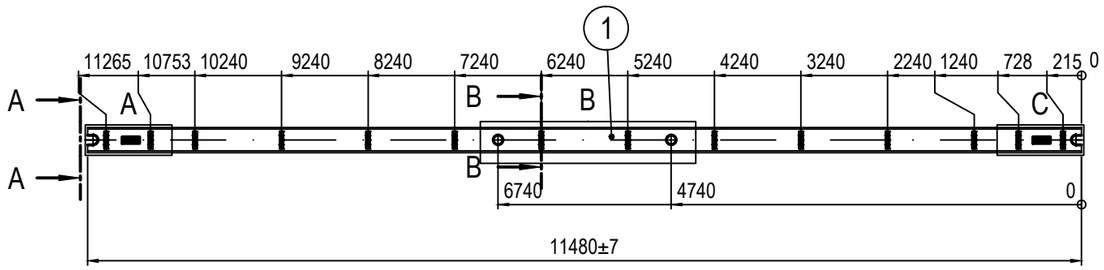

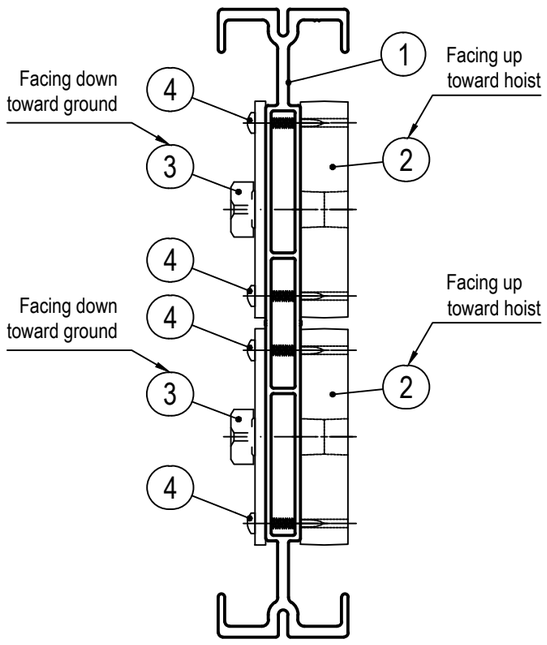

A - A Scale 1:2

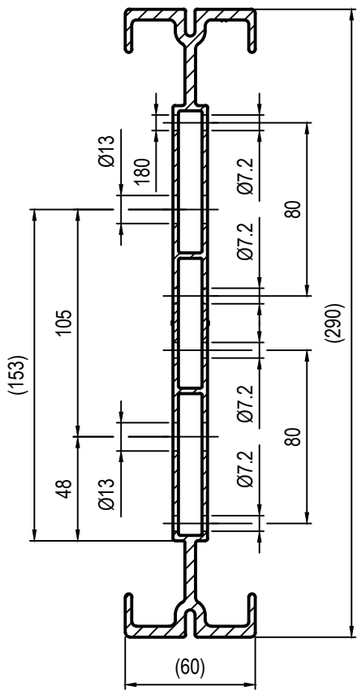

B - B Scale 1:2
Hole drilling typ. @ all
spacers & nut plates

Weight: 82kg.

ITEM	QTY	DESCRIPTION	DIMENSION	MATERIAL	REMARKS	kg/pc
5	2	Sign	200 x 75		19150987	
4	56	Screw	RTS TX 4,8x38		19203815	
3	28	Nut plate			19113194	0.3
2	28	Spacer			19123449	
1	1	Profile 290x60	L= 11480	6005-T6	19162359	73.6

DESIGNED: EB
SIZE: A2
SCALE: 1:50
CODE: 84800
ITEM NO:
DATE: 2022-11-01
If not otherwise stated:
Tolerances ISO 2768-m EN ISO 13920-B
Cutting class ISO 9013-442
Weld class ISO 5817-C
Surface finish Smooth raw surface
ASSA ABLOY

GMR Aero Technic Hangar1

India

Megadoor 79014x23000/14000

Top beam #3

PLOT DATE

DRAWING NO: 77811

REVISION: --

This document is the property of ASSA ABLOY Entrance Systems AB and shall not without our written permission be copied, imparted to a third party or used for any other unauthorized purpose.

Holes for intermediate beam guide
Drill template, 13624 holes 3-6

Holes for intermediate beam guide
Drill template, 13624 holes 3-6

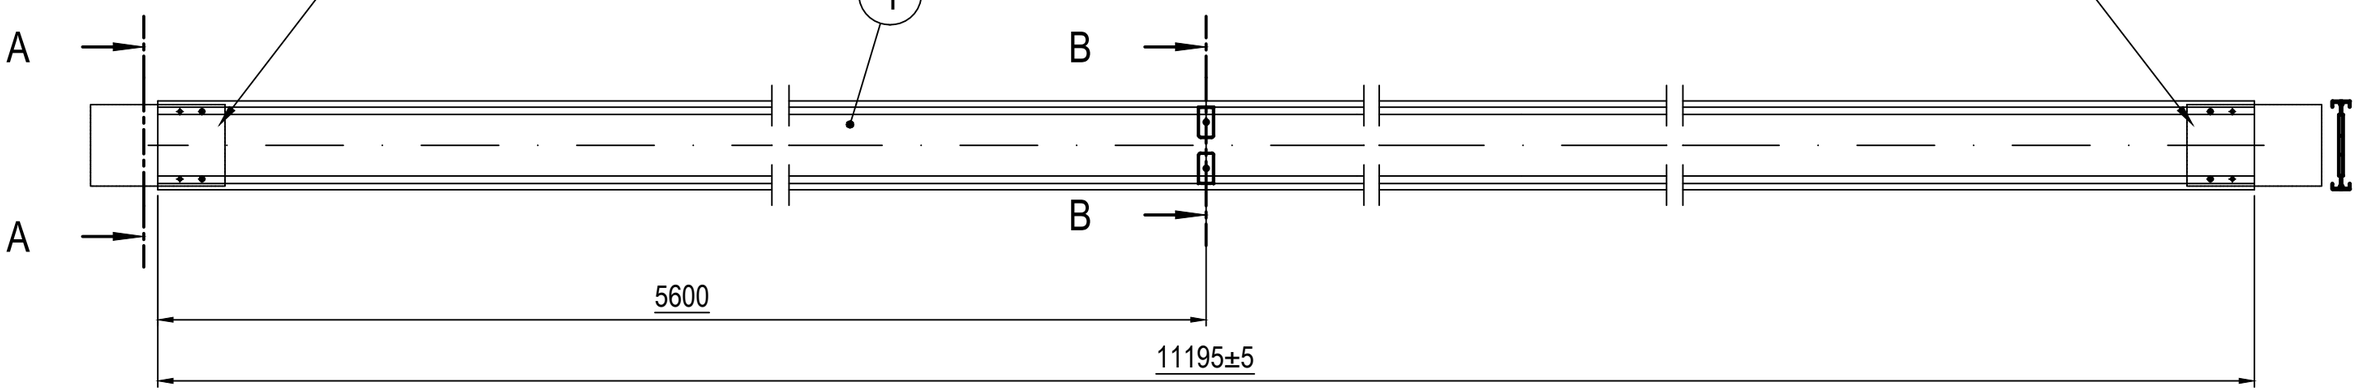

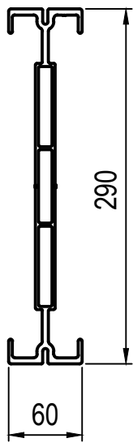

A - A Scale 1:5

Offset to avoid collision
between screws

Offset to avoid collision
between screws

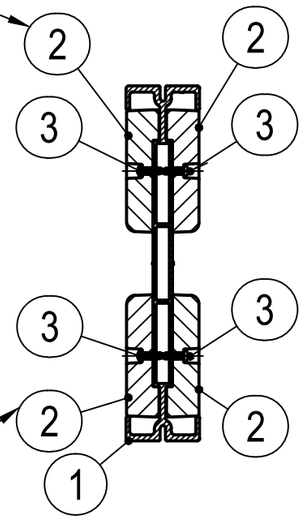

B - B Scale 1:5

Weight = 72 kg
Weight = 6.41 kg/m

ITEM	QTY	DESCRIPTION	DIMENSION	MATERIAL	REMARKS	kg/pc
3	4	Screw	RTB ST 4.8x22		19202674	
2	4	Spacer			19134313	0.0
1	1	Profile 290 x 60	L= 11195	6005-T6	19162359	71.8

DESIGNED EB

SIZE A3

SCALE 1:20

CODE 84800

ITEM NO

DATE 2022-11-01

ASSA ABLOY

If not otherwise stated:
Tolerances
ISO 2768-m
EN ISO 13920-B
Cutting class
ISO 9013-442
Weld class
ISO 5817-C
Surface finish
Smooth raw surface

GMR Aero Technic Hangar1

India

Megadoor 79014x23000/14000

Intermediate beam #3

PLOT DATE

DRAWING NO 77812

REVISION --

This document is the property of ASSA ABLOY Entrance Systems AB and shall not without our written permission be copied, imparted to a third party or used for any other unauthorized purpose.

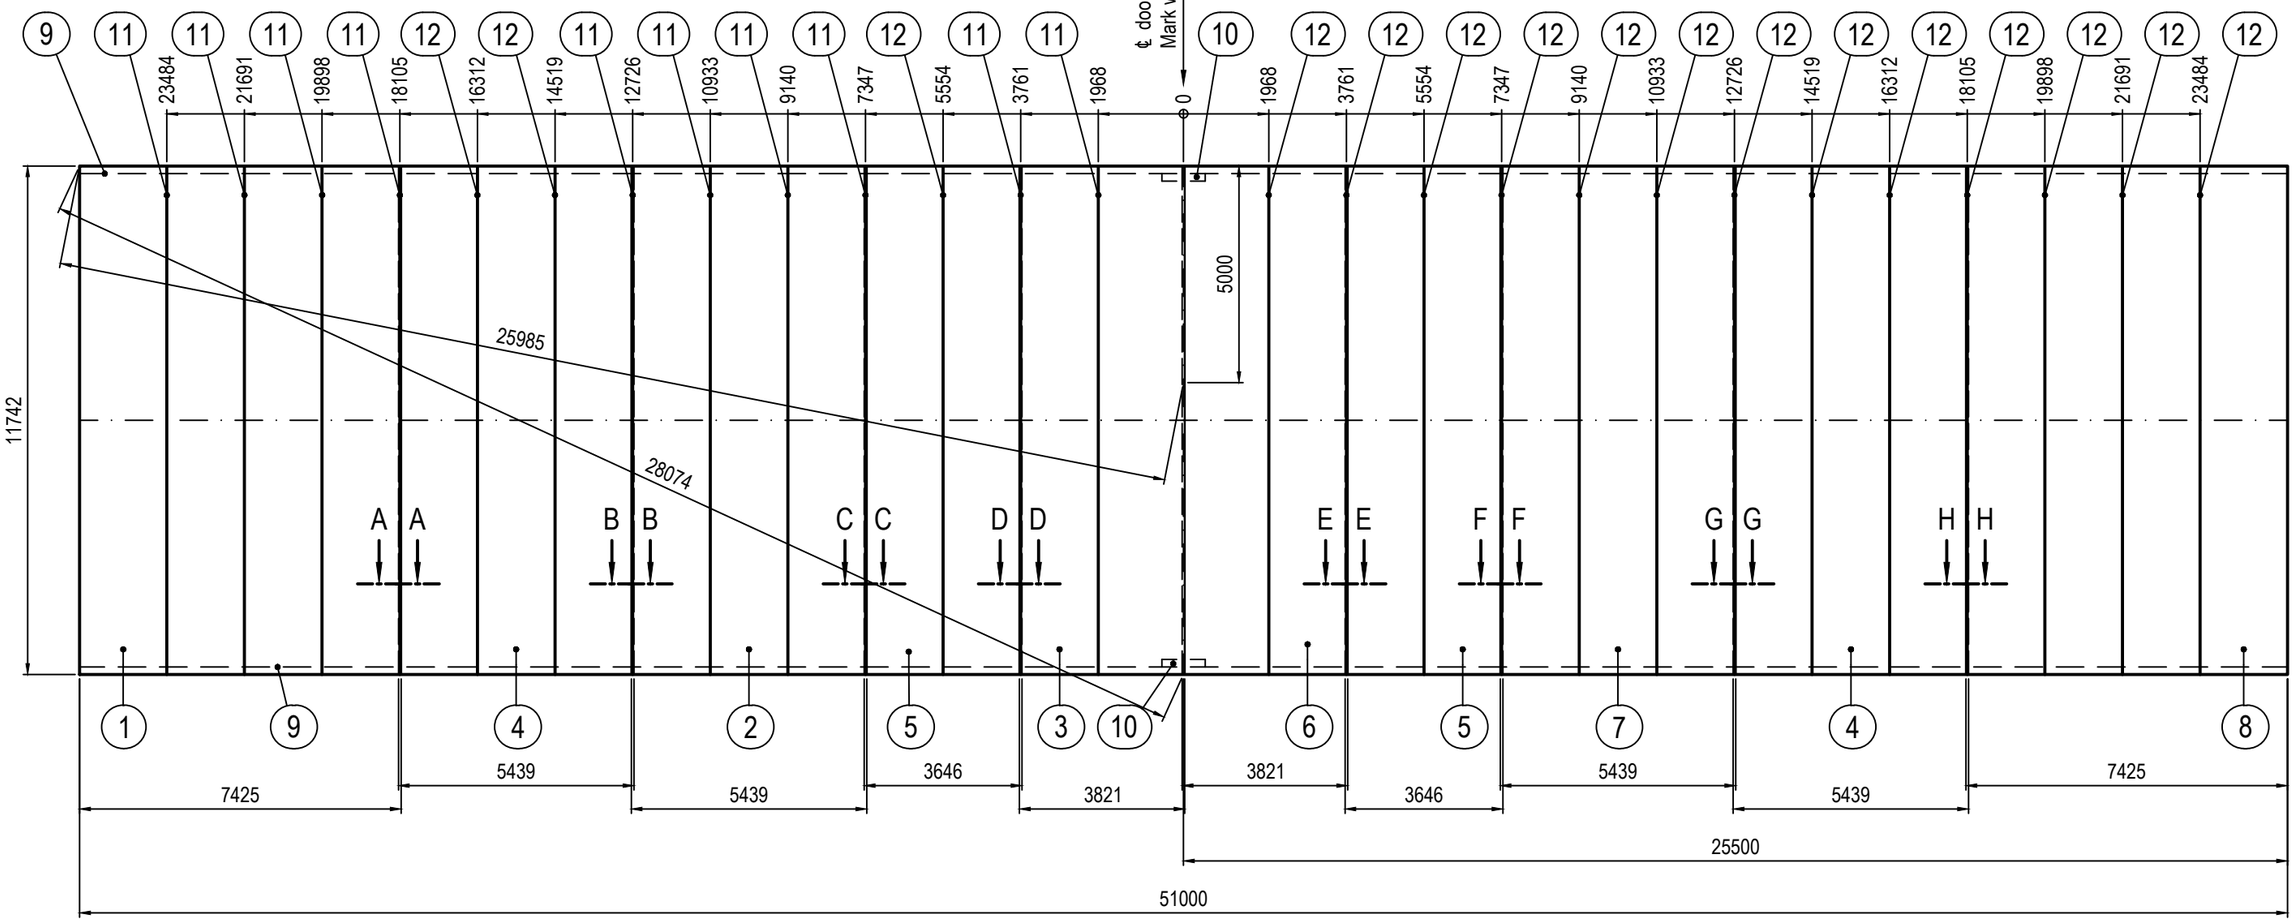

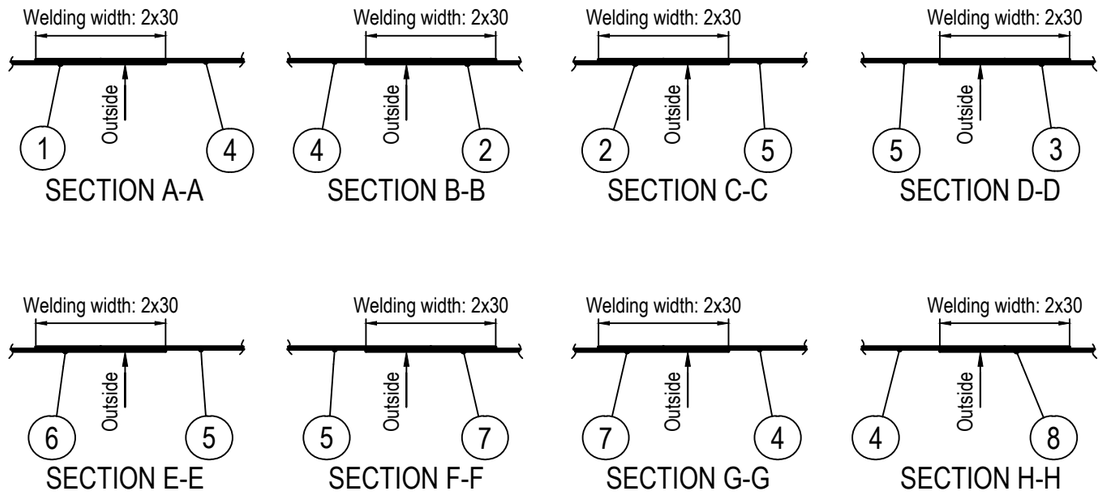

Top reinforcement and wear strip welding acc. to A3-19944

Weight: 432kg

App. lengths

ITEM	QTY	DESCRIPTION	DIMENSION	MATERIAL	REMARKS	kg/pc
12	16	Scribe line	L=11742		19204697, tape & ink	
11	10	Scribe line	L=11742		19203659 Crayon	
10	2	Top reinforcement	W= 175 x L= 1000			0.1
9	2	Wear strip	W= 175 x L= 34000			4.2
8	1	Door Fabric	W= 11742 x L= 7425		Color: White	61.0
7	1	Door Fabric	W= 11742 x L= 5439		Color: White	44.7
6	1	Door Fabric	W= 11742 x L= 3821		Color: White	31.4
5	2	Door Fabric	W= 11742 x L= 3646		Color: Translucent white	30.0
4	2	Door Fabric	W= 11742 x L= 5439		Color: Translucent white	44.7
3	1	Door Fabric	W= 11742 x L= 3821		Color: Anthracite grey	31.4
2	1	Door Fabric	W= 11742 x L= 5439		Color: Anthracite grey	44.7
1	1	Door Fabric	W= 11742 x L= 7425		Color: Anthracite grey	61.0

DESIGNED EB | SIZE A2 | SCALE 1:100

CODE 84800

ITEM NO

DATE 2022-11-01

If not otherwise stated:
Tolerances ISO 2768-m EN ISO 13920-B
Cutting class ISO 9013-442
Weld class ISO 5817-C
Surface finish Smooth raw surface

ASSA ABLOY

GMR Aero Technic Hangar1

India

Megadoor 79014x23000/14000

Door fabric #3

PLOT DATE

DRAWING NO 77813

REVISION --

This document is the property of ASSA ABLOY Entrance Systems AB and shall not without our written permission be copied, imparted to a third party or used for any other unauthorized purpose.

DETAIL 3, SCALE (1:4)

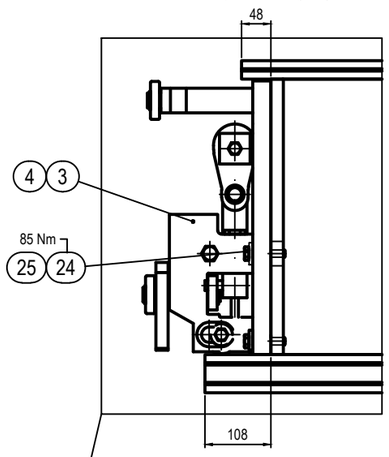

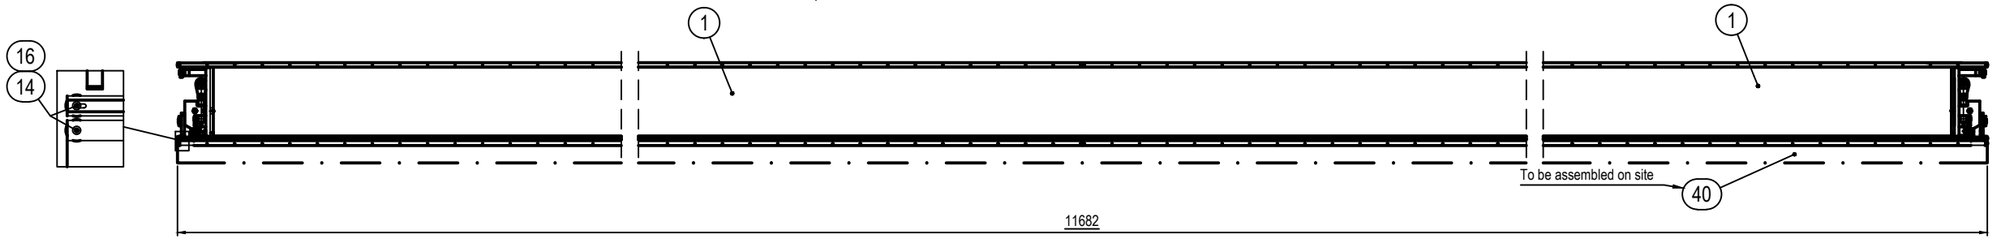

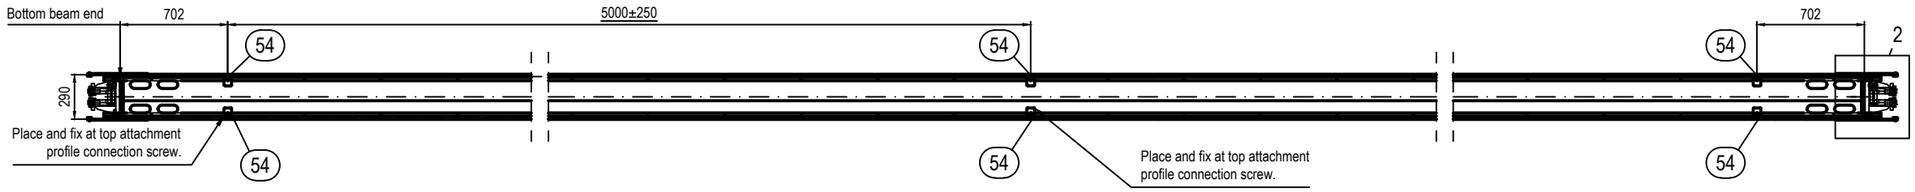

3

BOTTOM BEAM PREPARED FOR TRANSPORTATION
SCALE 1:10

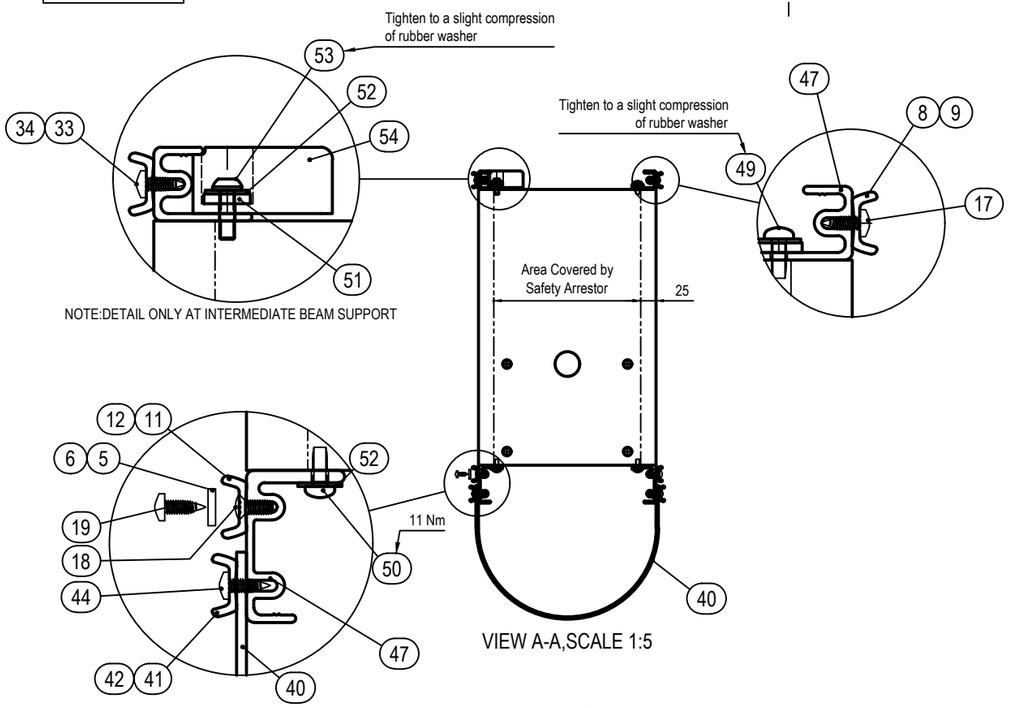

NOTE:DETAIL ONLY AT INTERMEDIATE BEAM SUPPORT

VIEW A-A,SCALE 1:5

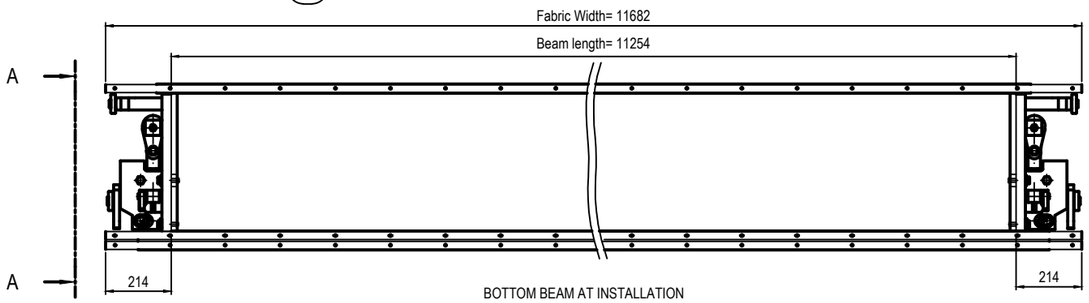

BOTTOM BEAM AT INSTALLATION
Interior view
SCALE 1:10

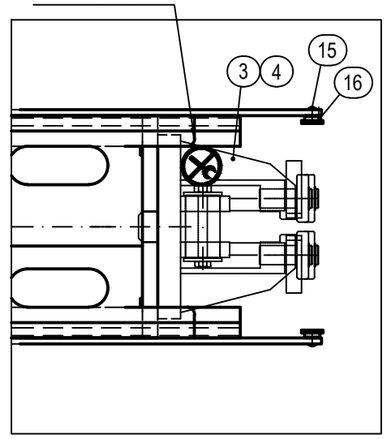

DETAIL 2, SCALE (1:4)

PARTS LIST, ref. to drwng 77814.XLS

Total weight:716kg

Stated tightening torque refers to dry screw and nut, unless noted otherwise, and a torque wrench with max. tolerance of ±5%. At re-check, the tightening torque must be within ±25% of stated torque.

DESIGNED	EB
CODE	84800
ITEM NO	
DATE	2022-10-31
SIZE	A1
SCALE	1:20
If not otherwise stated:	
Tolerances	ISO 2768-m EN ISO 13920-B
Cutting class	ISO 9013:442
Weld class	ISO 5817-C
Surface finish	Smooth raw surface

ASSA ABLOY

GMR Aero Technic Hangar1

India

Megadoor 79014x23000/14000

Bottom beam assembly #3

DRAWING NO 77814

REVISION --

PLOT DATE

This document is the property of ASSA ABLOY Entrance Systems AB and shall not be reproduced or disclosed to a third party or used for any other unauthorized purpose.

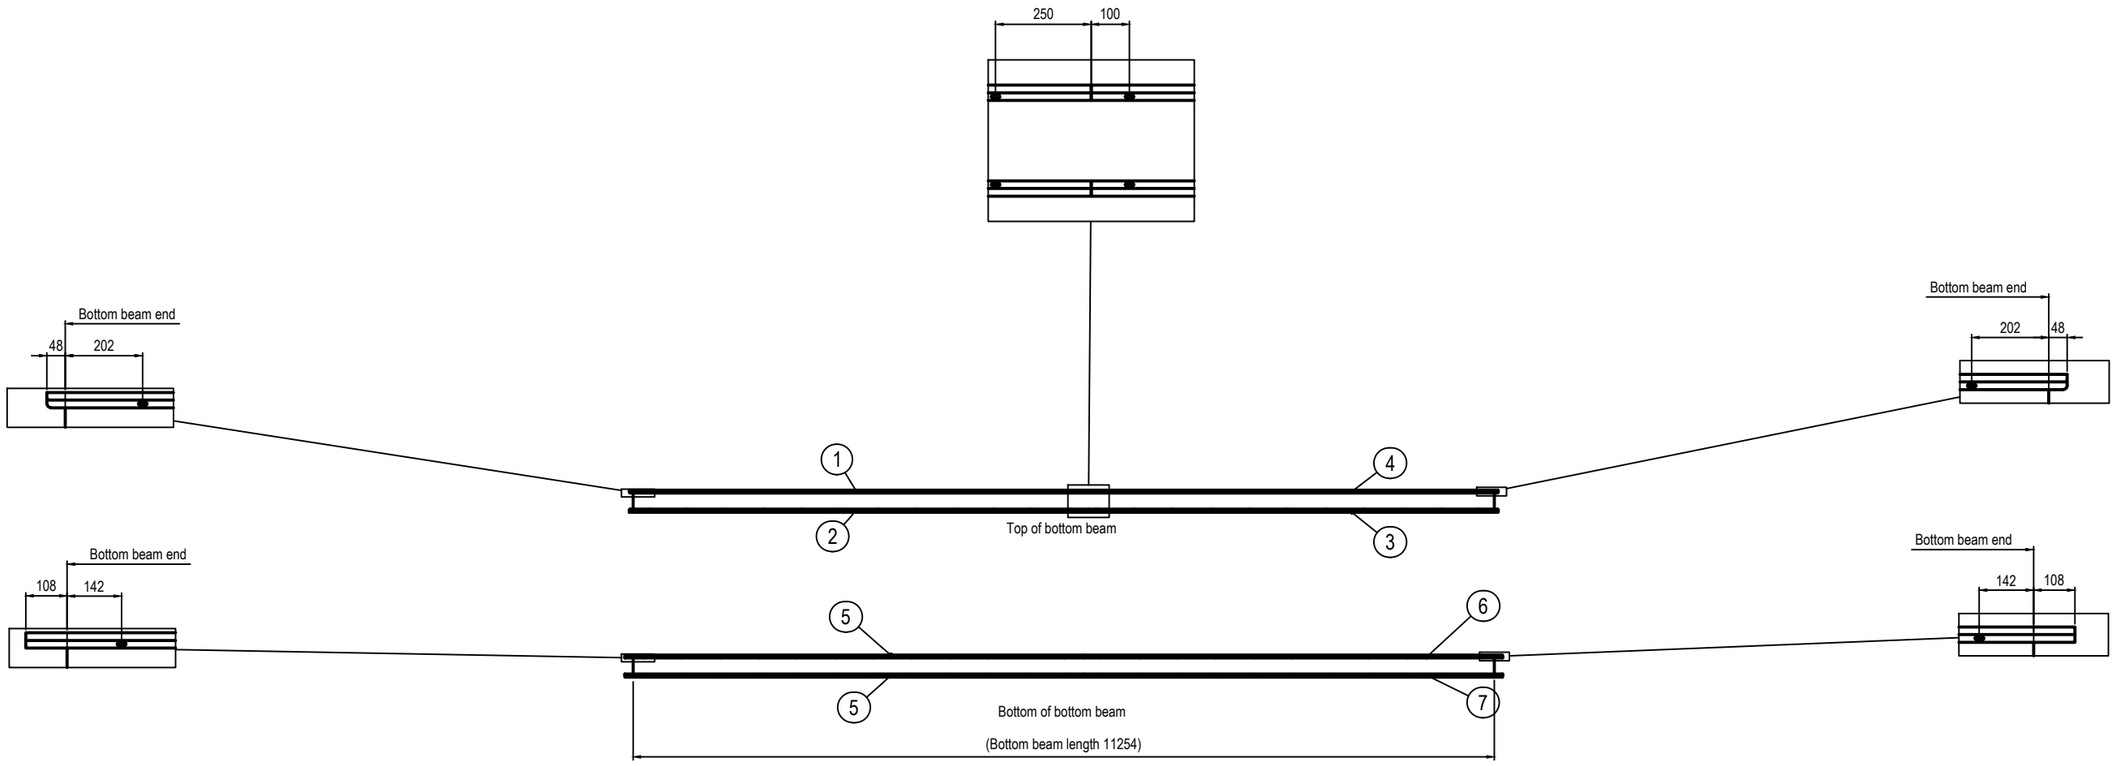

Positioning of
clamp strip
attachment profiles
Scale 1:40

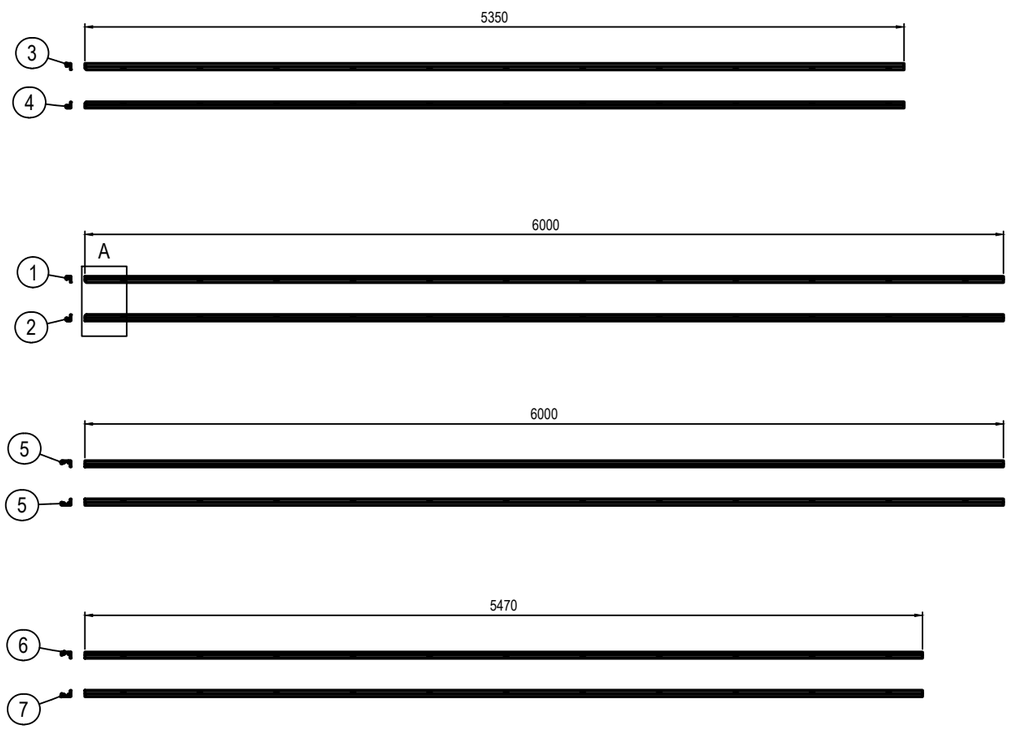

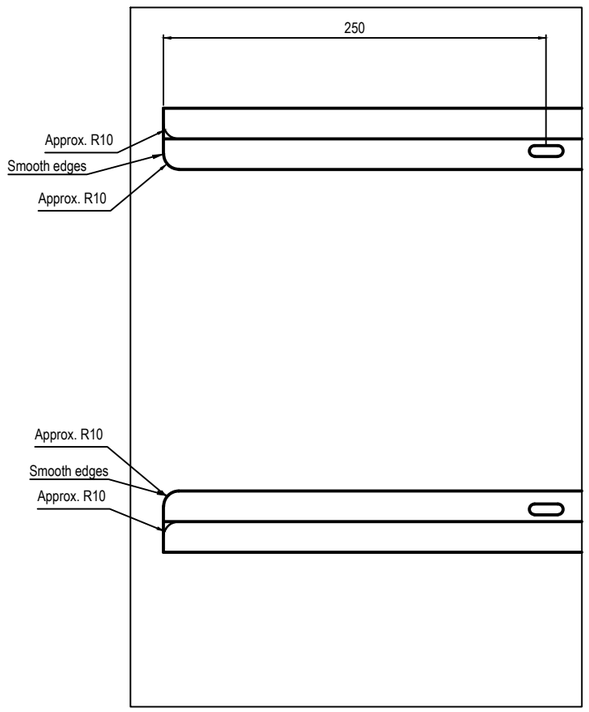

DETAIL A, SCALE (1:2)
Upper profile only
Only one side per profile
Other side mirror image

Weight: 54 kg

ITEM	QTY	DESCRIPTION	DIMENSION	MATERIAL	REMARKS	kg/pc
7	1	Clamp strip attachment profile, lower	L= 5470		19162431	8.3
6	1	Clamp strip attachment profile, lower	L= 5470		19162431	8.3
5	2	Clamp strip attachment profile, lower	L= 6000		19162431	9.1
4	1	Clamp strip attachment profile, upper	L= 5350		19162430	4.6
3	1	Clamp strip attachment profile, upper	L= 5350		19162430	4.6
2	1	Clamp strip attachment profile, upper	L= 6000		19162430	5.2
1	1	Clamp strip attachment profile, upper	L= 6000		19162430	5.2

DESIGNED: EB
SIZE: A1
SCALE: 1:20
CODE: 84800
ITEM NO:
DATE: 2022-10-31
If not otherwise stated:
Tolerances: ISO 2768-m, EN ISO 13920-B
Cutting class: ISO 9013-442
Weld class: ISO 5817-C
Surface finish: Smooth raw surface

GMR Aero Technic Hangar1

India

Megadoor 79014x23000/14000

Clamp strip attachment profiles #3

DRAWING NO: 77816
REVISION: --
PLOT DATE:

This document is the property of ASSA ABLOY Entrance Systems AB and shall not be reproduced, disclosed or used in whole or in part for any other unauthorized purpose. It shall not be lent or delivered to a third party or used for any other unauthorized purpose.

Installation preparation, ref. to drawing no. A2-23869

41	2	Screw	cl 10.9	MF6S 12x30		19204118	
40	2	Fork pin washer				19141235	0,17
39	1	Set of guide rails				77824	385
38	4	Bottom seal clamp		L=84	Pos 2	62713	
37	2	Bottom seal clamp		L=210	Pos 1	62713	
36	2	Rubber fabric	EPDM	4x900x400		19203296	0,5
35	12	Parallel pin	SMS 2374	CP 5x40		19200363	
34	4	Tension pin	SMS 1663	FRP 6x30		19200972	
33	10	Tension pin	SMS 1663	FRP 6x10		19200373	
32	2	Tension pin	SMS 1663	FRP 4x10		19201678	
31	2	Nut	Cl. 8	M6M 20		19201687	0,073
30	2	Washer	HB 200	BRB 21x36		19200202	0,016
29	16	Washer	HB 200	BRB 13x24		19200333	0,005
28	1	Washer	HB 200	BRB 8.4x16		19200397	0,0017
27	2	Screw	Cl. 8.8	M6S 16x40		19200246	0,09
26	16	Screw	Cl. 8.8	M6S 12x50		19201681	0,055
25	104	Screw		M6SF-GF 10x30		19200455	0,028
24	88	Screw		M6SF-GF 8x20		19200233	0,014
23	1	Screw	Cl. 8.8	M6S 8x16		19203617	0,011
22	2	Screw	Cl. 8.8	M6SF-GF 5x16		19201978	0,0063
21	8	Screw		RTS TX 4.8x19		19200327	0,0027
20	16	Screw		RTS TX 4.8x13		19200242	0,0022
19	1	Bearing assembly				19123485	10
18	1	Bearing assembly				19123484	10
17	1	Suspension unit				19125059	10
16	2	Brush strip	Nylon 0.25	L=238	B=5, H=60 (51060)	19203460	
15	2	Brush strip bracket		L=238	F90° B=5, L=2000 (55590)	19203461	
14	1	Limit switch attachment plate				19143997	
13	1	Limit switch		IGS232		43998	
12	1	Trigger arm			L=350	43996	0,2
11	1	Fork pin				19141934	3,8
10	1	Set screw				19113946	0,48
9	1	Leaf spring				19113945	8,5
8	1	Hinge pin				19119857	36
7	1	Mullion				77823	1373
6	4	Shaft nut		M40x1.5	KM8	19201148	0,078
5	4	Thrust washer			GLY.PXG 527802 A	19201700	
4	2	Washer				19112647	0,3
3							
2	1	Fork				19123489	137
1	1	Mullion extension				77821	189
item	**qty**	**description**	**material**	**dimension**	**remarks**	**art.no/ drwng.no.**	**weight kg/pc.**

GMR Aero Technic Hangar1 **Total weight (kg): 2171**

India

Megadoor 79014x23000/14000 Date: 2022-11-02

Swing-up mullion #12 **Project no.** 84800

Parts list. 77817.xls Designed: EB

Ref. to assembly drawing no. 77817.dwg Revision: --

Stated tightening torque refers to dry screw and nut, unless noted otherwise, and a torque wrench with max. tolerance of ±5%. At re-check, the tightening torque must be within ±25% of stated torque.

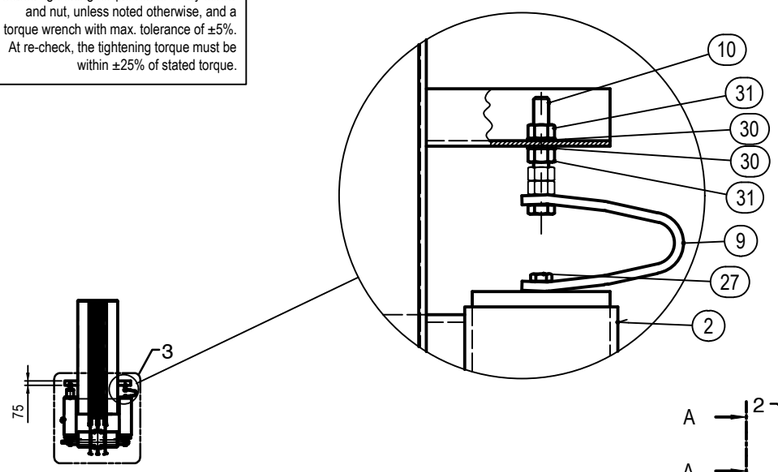

NOTE!
Max. allowed compression of spring is 10mm

Springs should be set to a minimum of compression when mullion is hanging straight in vertical position. Adjust set screws simultaneously when adjustment is required to ensure a positive fit of base pin in floor guide.

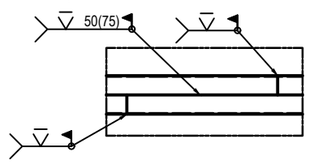

Mullion weld joint, scale 1:20

Electrode: ESAB OK48
Filarc 88S
Maxeta 22
Lincoln 7018
Hyundai SM-70
or similar.

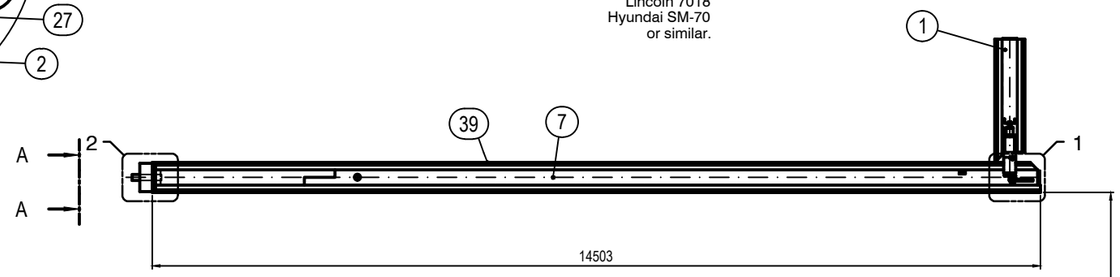

View from inside building

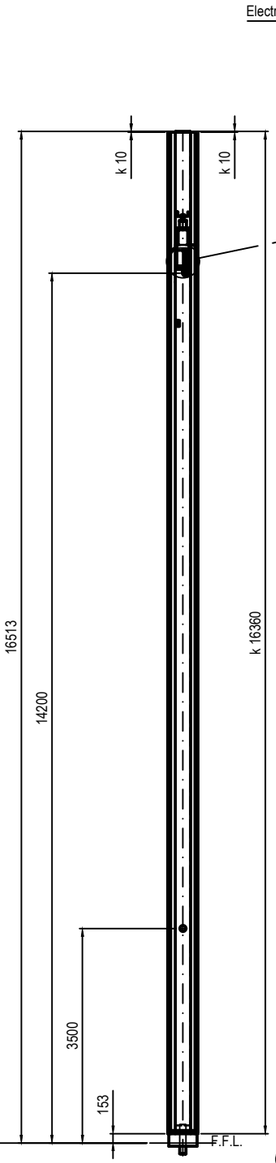

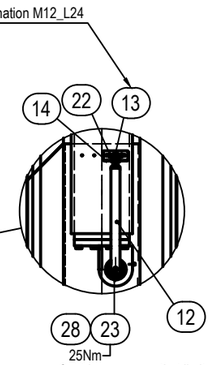

Set trigger arm so that limit switch is activated when mullion is in vertical position. Drill Ø5x10 hole in shaft for tension pin.

Section B -- B

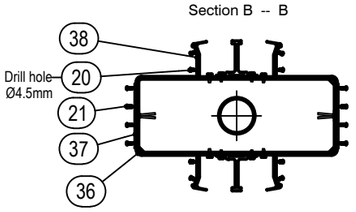

View A -- A, scale 1:10

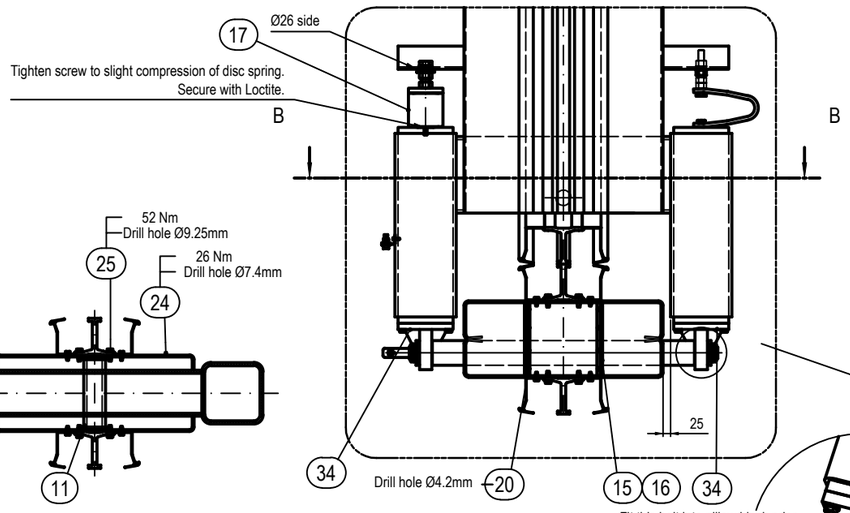

Detail 3, scale 1:10

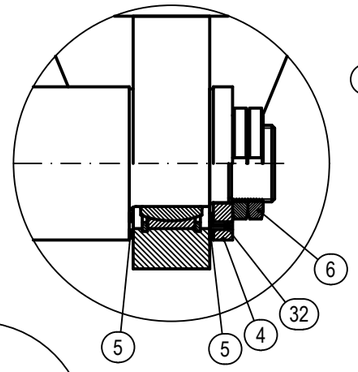

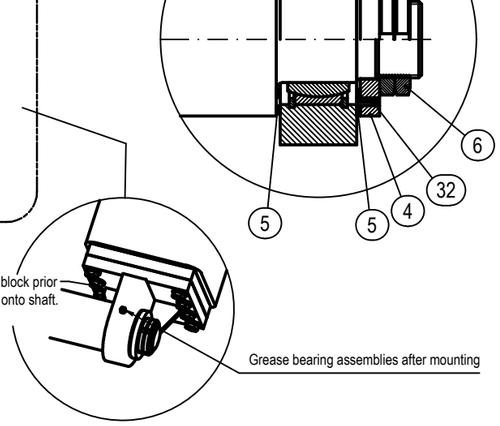

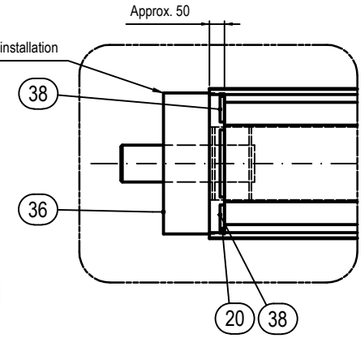

Detail 2, scale 1:10

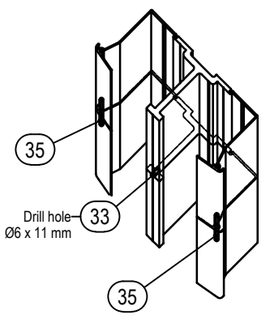

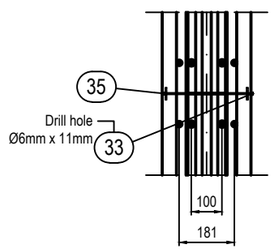

Detail @ System 1500
Guide Rail Joint, typ.

Welding of shaft at layout with hinge assembly, typ.

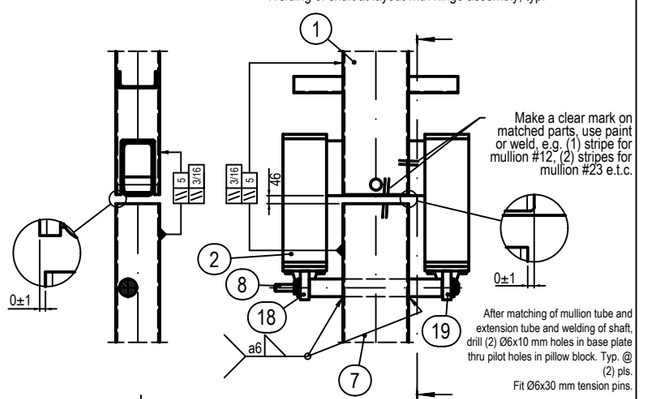

Make a clear mark on matched parts, use paint or weld, e.g. (1) stripe for mullion #12, (2) stripes for mullion #23 e.t.c.

After matching of mullion tube and extension tube and welding of shaft, drill (2) Ø6x10 mm holes in base plate thru pilot holes in pillow block. Typ. @ (2) pls.
Fit Ø6x30 mm tension pins.

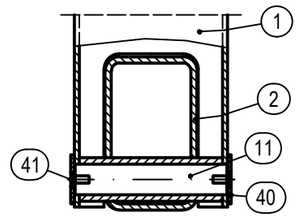

Section through
Mullion Extension Joint, typ.

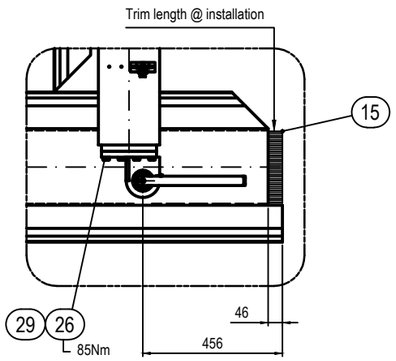

Detail 1, scale 1:10

Painting instructions acc. to 44626.dwg

Weight: 2171 kg

PARTS LIST, ref. to. drwng. no. 77817.XLS

DESIGNED EB	APPROVED	SIZE A1	SCALE 1:50
CODE 84800		If not otherwise stated: Tolerances ISO 2768-m EN ISO 13920-B	
ITEM NO		Cutting class ISO 9013-442	
DATE 2022-11-02		Weld class ISO 5817-C	
ASSA ABLOY		Surface finish Smooth raw surface	

GMR Aero Technic Hangar1
India
Megadoor 79014x23000/14000
Swing-up mullion assembly #12

DRAWING NO 77817
REVISION --
PLOT DATE

This document is the property of ASSA ABLOY Entrance Systems AB and shall not be reproduced or disclosed to any third party or used for any other unauthorized purpose.

Installation preparation, ref. to drawing no. A2-23869

41	2	Screw	cl 10.9	MF6S 12x30		19204118	
40	2	Fork pin washer				19141235	0,17
39	1	Set of guide rails				77825	483
38	4	Bottom seal clamp		L=84	Pos 2	62713	
37	2	Bottom seal clamp		L=210	Pos 1	62713	
36	2	Rubber fabric	EPDM	4x900x400		19203296	0,5
35	14	Parallel pin	SMS 2374	CP 5x40		19200363	
34	4	Tension pin	SMS 1663	FRP 6x30		19200972	
33	11	Tension pin	SMS 1663	FRP 6x10		19200373	
32	2	Tension pin	SMS 1663	FRP 4x10		19201678	
31	2	Nut	Cl. 8	M6M 20		19201687	0,073
30	2	Washer	HB 200	BRB 21x36		19200202	0,016
29	16	Washer	HB 200	BRB 13x24		19200333	0,005
28	1	Washer	HB 200	BRB 8.4x16		19200397	0,0017
27	2	Screw	Cl. 8.8	M6S 16x40		19200246	0,09
26	16	Screw	Cl. 8.8	M6S 12x50		19201681	0,055
25	122	Screw		M6SF-GF 10x30		19200455	0,028
24	106	Screw		M6SF-GF 8x20		19200233	0,014
23	1	Screw	Cl. 8.8	M6S 8x16		19203617	0,011
22	2	Screw	Cl. 8.8	M6SF-GF 5x16		19201978	0,0063
21	8	Screw		RTS TX 4.8x19		19200327	0,0027
20	16	Screw		RTS TX 4.8x13		19200242	0,0022
19	1	Bearing assembly				19123485	10
18	1	Bearing assembly				19123484	10
17	1	Suspension unit				19125059	10
16	2	Brush strip	Nylon 0.25	L=238	B=5, H=60 (51060)	19203460	
15	2	Brush strip bracket		L=238	F90° B=5, L=2000 (55590)	19203461	
14	1	Limit switch attachment plate				19143997	
13	1	Limit switch		IGS232		43998	
12	1	Trigger arm			L=350	43996	0,2
11	1	Fork pin				19141934	3,8
10	1	Set screw				19113946	0,48
9	1	Leaf spring				19113945	8,5
8	1	Hinge pin				19119857	36
7	1	Mullion				77823	1373
6	4	Shaft nut		M40x1.5	KM8	19201148	0,078
5	4	Thrust washer			GLY.PXG 527802 A	19201700	
4	2	Washer				19112647	0,3
3							
2	1	Fork				19123489	137
1	1	Mullion extension				77822	944
item	**qty**	**description**	**material**	**dimension**	**remarks**	**art.no/ drwng.no.**	**weight kg/pc.**

GMR Aero Technic Hangar1 **Total weight (kg): 3025**

India

Megadoor 79014x23000/14000 Date: 2022-11-02

Swing-up mullion #23 **Project no.** 84800

Parts list. 77818.xls Designed: EB

Ref. to assembly drawing no. 77818.dwg Revision: --

NOTE!
Max. allowed compression of spring is 10mm

Springs should be set to a minimum of compression when mullion is hanging straight in vertical position. Adjust set screws simultaneously when adjustment is required to ensure a positive fit of base pin in floor guide.

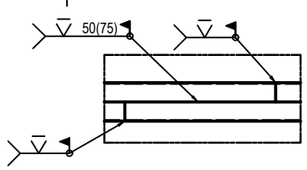

Mullion weld joint, scale 1:20

Electrode: ESAB OK48
Filarc 88S
Maxeta 22
Lincoln 7018
Hyundai SM-70
or similar.

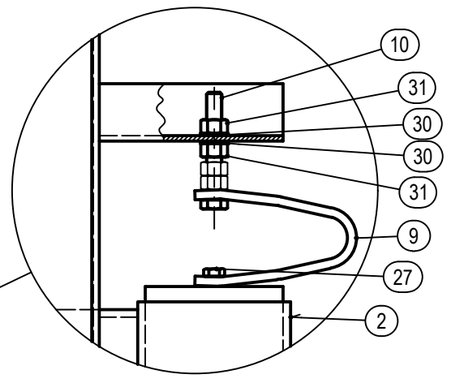

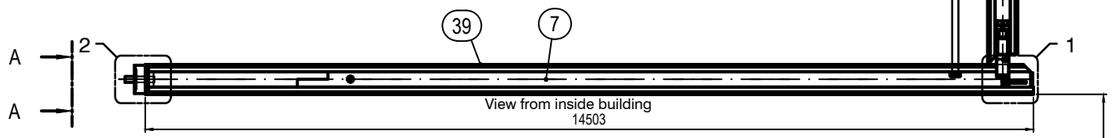

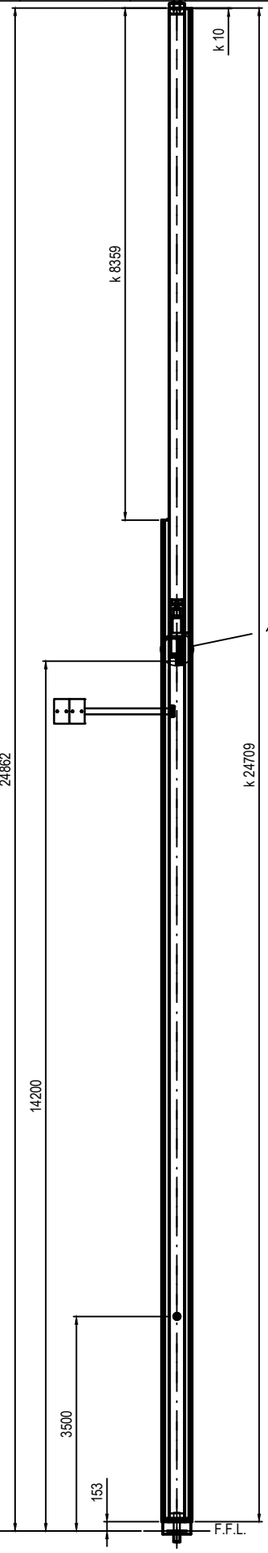

Stated tightening torque refers to dry screw and nut, unless noted otherwise, and a torque wrench with max. tolerance of ±5%. At re-check, the tightening torque must be within ±25% of stated torque.

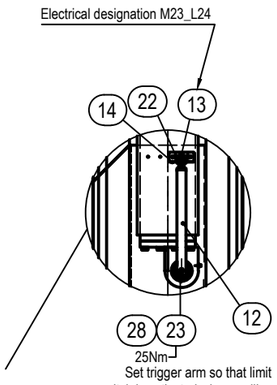

Set trigger arm so that limit switch is activated when mullion is in vertical position. Drill Ø5x10 hole in shaft for tension pin.

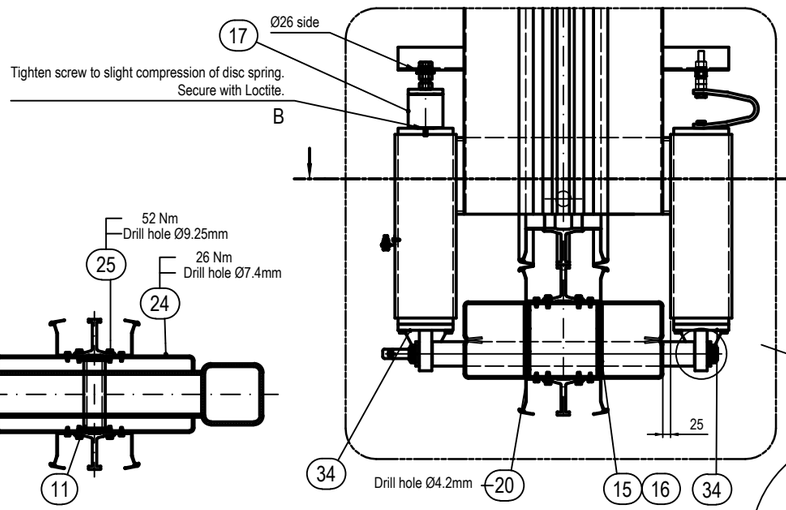

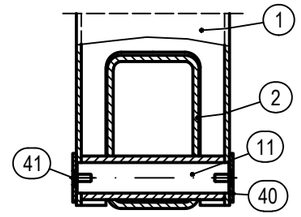

Section through
Mullion Extension Joint, typ.

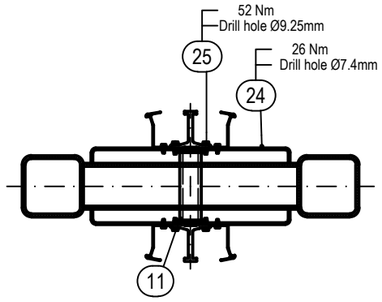

Section B -- B

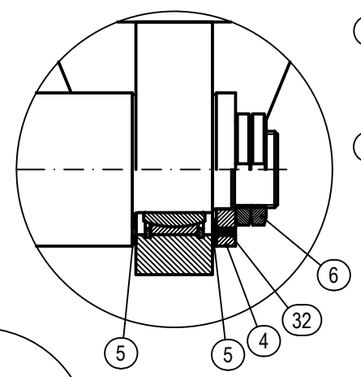

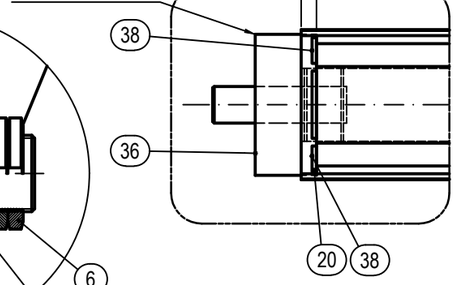

Detail 2, scale 1:10

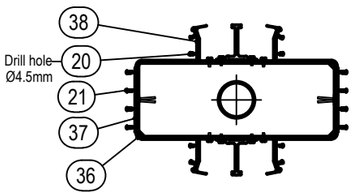

View A -- A, scale 1:10

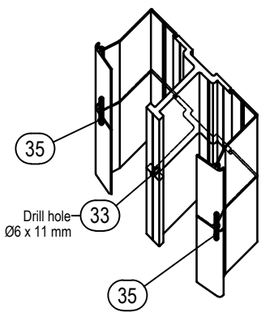

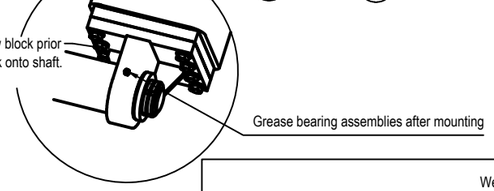

Detail 3, scale 1:10

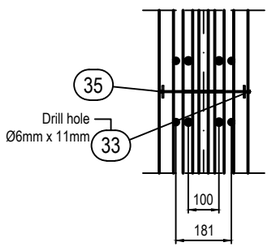

Detail @ System 1500
Guide Rail Joint, typ.

Welding of shaft at layout with hinge assembly, typ.

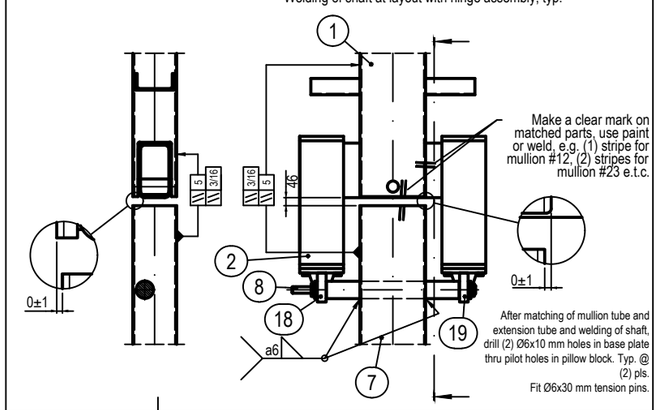

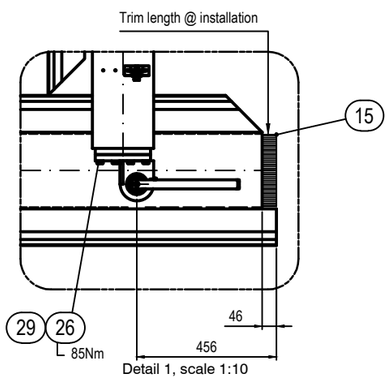

Detail 1, scale 1:10

Painting instructions acc. to 44626.dwg

Weight: 3025 kg

PARTS LIST, ref. to. drwng. no. 77818.XLS

DESIGNED EB	APPROVED	SIZE A1	SCALE 1:50
CODE 84800		If not otherwise stated:	
ITEM NO		Tolerances ISO 2768-m EN ISO 13920-B	
DATE 2022-11-02		Cutting class ISO 9013-442	
ASSA ABLOY		Weld class ISO 5817-C	
		Surface finish Smooth raw surface	

GMR Aero Technic Hangar1
India
Megadoor 79014x23000/14000
Swing-up mullion assembly #23

DRAWING NO 77818
REVISION --
PLOT DATE

This document is the property of ASSA ABLOY Entrance Systems AB and shall not be reproduced or copied without permission. It is not to be communicated to a third party or used for any other unauthorized purpose.

Installation preparation, ref. to drawing no. A2-23869

41	2	Screw	cl 10.9	MF6S 12x30		19204118	
40	2	Fork pin washer				19141235	0,17
39	1	Set of guide rails				77825	483
38	4	Bottom seal clamp		L=84	Pos 2	62713	
37	2	Bottom seal clamp		L=210	Pos 1	62713	
36	2	Rubber fabric	EPDM	4x900x400		19203296	0,5
35	14	Parallel pin	SMS 2374	CP 5x40		19200363	
34	4	Tension pin	SMS 1663	FRP 6x30		19200972	
33	11	Tension pin	SMS 1663	FRP 6x10		19200373	
32	2	Tension pin	SMS 1663	FRP 4x10		19201678	
31	2	Nut	Cl. 8	M6M 20		19201687	0,073
30	2	Washer	HB 200	BRB 21x36		19200202	0,016
29	16	Washer	HB 200	BRB 13x24		19200333	0,005
28	1	Washer	HB 200	BRB 8.4x16		19200397	0,0017
27	2	Screw	Cl. 8.8	M6S 16x40		19200246	0,09
26	16	Screw	Cl. 8.8	M6S 12x50		19201681	0,055
25	122	Screw		M6SF-GF 10x30		19200455	0,028
24	106	Screw		M6SF-GF 8x20		19200233	0,014
23	1	Screw	Cl. 8.8	M6S 8x16		19203617	0,011
22	2	Screw	Cl. 8.8	M6SF-GF 5x16		19201978	0,0063
21	8	Screw		RTS TX 4.8x19		19200327	0,0027
20	16	Screw		RTS TX 4.8x13		19200242	0,0022
19	1	Bearing assembly				19123485	10
18	1	Bearing assembly				19123484	10
17	1	Suspension unit				19125059	10
16	2	Brush strip	Nylon 0.25	L=238	B=5, H=60 (51060)	19203460	
15	2	Brush strip bracket		L=238	F90° B=5, L=2000 (55590)	19203461	
14	1	Limit switch attachment plate				19143997	
13	1	Limit switch		IGS232		43998	
12	1	Trigger arm			L=350	43996	0,2
11	1	Fork pin				19141934	3,8
10	1	Set screw				19113946	0,48
9	1	Leaf spring				19113945	8,5
8	1	Hinge pin				19119857	36
7	1	Mullion				77823	1373
6	4	Shaft nut		M40x1.5	KM8	19201148	0,078
5	4	Thrust washer			GLY.PXG 527802 A	19201700	
4	2	Washer				19112647	0,3
3							
2	1	Fork				19123489	137
1	1	Mullion extension				77822	944
item	**qty**	**description**	**material**	**dimension**	**remarks**	**art.no/ drwng.no.**	**weight kg/pc.**

GMR Aero Technic Hangar1 **Total weight (kg): 3025**

India

Megadoor 79014x23000/14000 Date: 2022-11-02

Swing-up mullion #34 **Project no.** 84800

Parts list. 77819.xls Designed: EB

Ref. to assembly drawing no. 77819.dwg Revision: --

Electrical designation M34_L24

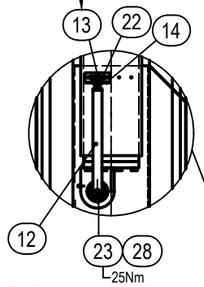

Set trigger arm so that limit switch is activated when mullion is in vertical position.
Drill Ø5x10 hole in shaft for tension pin.

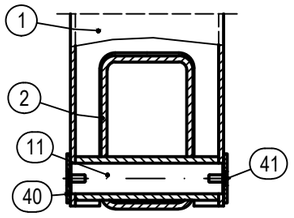

Section through
Mullion Extension Joint, typ.

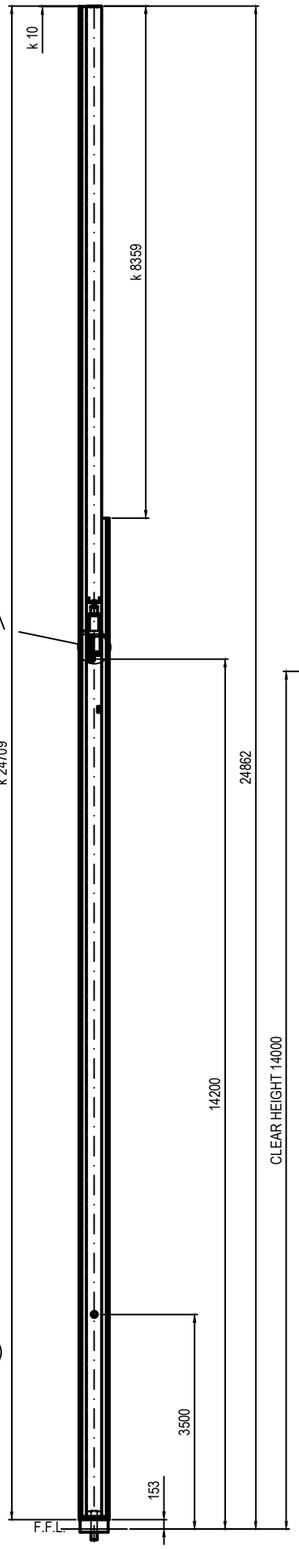

Welding of shaft at layout with hinge assembly, typ.

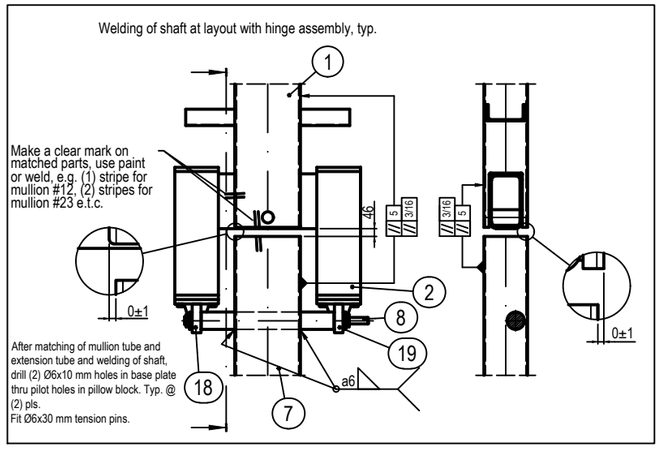

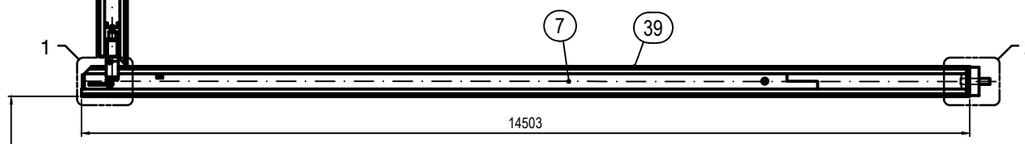

View from inside building

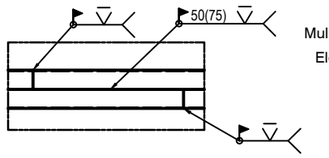

Mullion weld joint, scale 1:20

Electrode: ESAB OK48
Filarc 88S
Maxeta 22
Lincoln 7018
Hyundai SM-70
or similar.

NOTE!
Max. allowed compression of spring is 10mm

Springs should be set to a minimum of compression when mullion is hanging straight in vertical position. Adjust set screws simultaneously when adjustment is required to ensure a positive fit of base pin in floor guide.

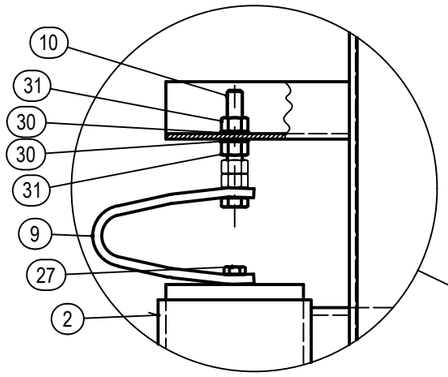

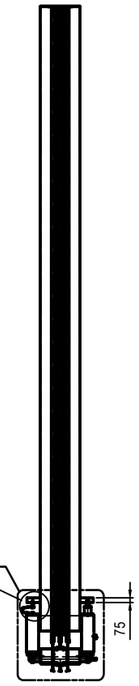

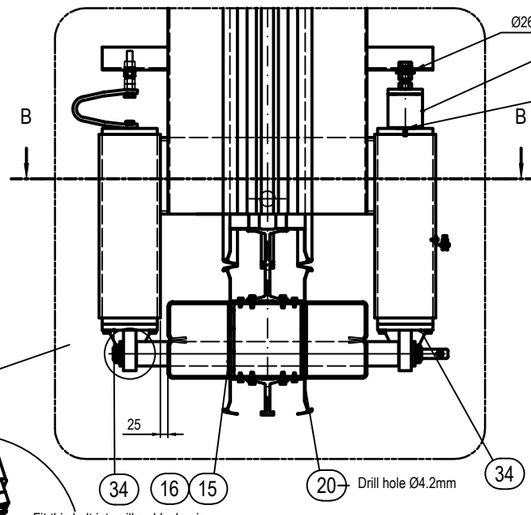

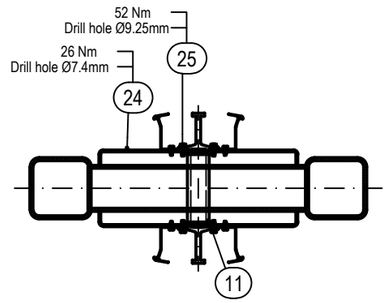

Section B -- B

Trim length @ installation

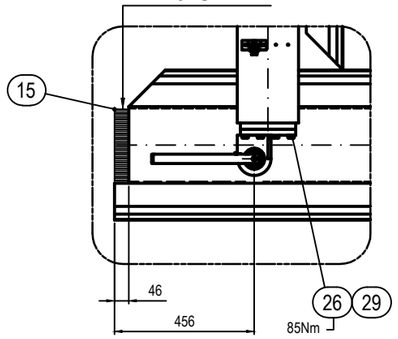

Detail 1, scale 1:10

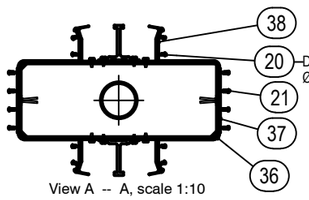

View A -- A, scale 1:10

Approx. 50

Trim length @ installation

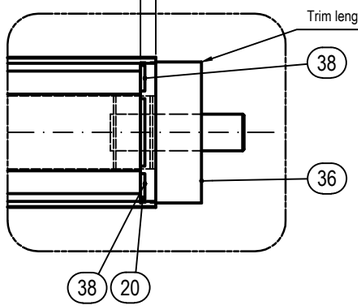

Detail 2, scale 1:10

Grease bearing assemblies after mounting

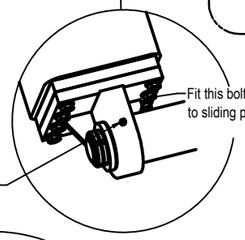

Fit this bolt into pillow block prior to sliding pillow block onto shaft.

Detail 3, scale 1:10

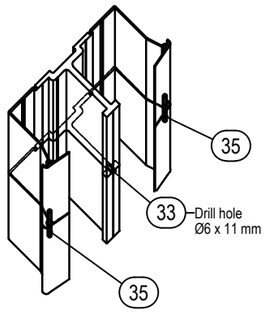

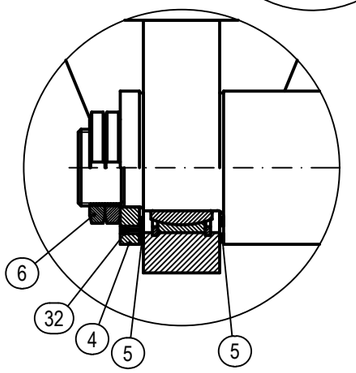

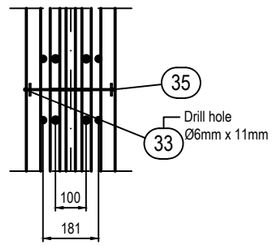

Detail @ System 1500
Guide Rail Joint, typ.

Painting instructions acc. to 44626.dwg

Weight: 3025 kg

PARTS LIST, ref. to. drwng. no. 77819.XLS

DESIGNED EB	APPROVED	SIZE A1	SCALE 1:50
CODE 84800		If not otherwise stated: Tolerances ISO 2768-m EN ISO 13920-B	
ITEM NO		Cutting class ISO 9013-442	
DATE 2022-11-03		Weld class ISO 5817-C	
ASSA ABLOY		Surface finish Smooth raw surface	

GMR Aero Technic Hangar1
India
Megadoor 79014x23000/14000
Swing-up mullion assembly #34

DRAWING NO 77819
REVISION --

PLOT DATE

Stated tightening torque refers to dry screw and nut, unless noted otherwise, and a torque wrench with max. tolerance of ±5%. At re-check, the tightening torque must be within ±25% of stated torque.

This document is the property of ASSA ABLOY Entrance Systems AB and shall not be copied or otherwise disclosed or reproduced to a third party or used for any other unauthorized purpose.

Installation preparation, ref. to drawing no. A2-23869

41	2	Screw	cl 10.9	MF6S 12x30		19204118	
40	2	Fork pin washer				19141235	0,17
39	1	Set of guide rails				77824	385
38	4	Bottom seal clamp		L=84	Pos 2	62713	
37	2	Bottom seal clamp		L=210	Pos 1	62713	
36	2	Rubber fabric	EPDM	4x900x400		19203296	0,5
35	12	Parallel pin	SMS 2374	CP 5x40		19200363	
34	4	Tension pin	SMS 1663	FRP 6x30		19200972	
33	10	Tension pin	SMS 1663	FRP 6x10		19200373	
32	2	Tension pin	SMS 1663	FRP 4x10		19201678	
31	2	Nut	Cl. 8	M6M 20		19201687	0,073
30	2	Washer	HB 200	BRB 21x36		19200202	0,016
29	16	Washer	HB 200	BRB 13x24		19200333	0,005
28	1	Washer	HB 200	BRB 8.4x16		19200397	0,0017
27	2	Screw	Cl. 8.8	M6S 16x40		19200246	0,09
26	16	Screw	Cl. 8.8	M6S 12x50		19201681	0,055
25	104	Screw		M6SF-GF 10x30		19200455	0,028
24	88	Screw		M6SF-GF 8x20		19200233	0,014
23	1	Screw	Cl. 8.8	M6S 8x16		19203617	0,011
22	2	Screw	Cl. 8.8	M6SF-GF 5x16		19201978	0,0063
21	8	Screw		RTS TX 4.8x19		19200327	0,0027
20	16	Screw		RTS TX 4.8x13		19200242	0,0022
19	1	Bearing assembly				19123485	10
18	1	Bearing assembly				19123484	10
17	1	Suspension unit				19125059	10
16	2	Brush strip	Nylon 0.25	L=238	B=5, H=60 (51060)	19203460	
15	2	Brush strip bracket		L=238	F90° B=5, L=2000 (55590)	19203461	
14	1	Limit switch attachment plate				19143997	
13	1	Limit switch		IGS232		43998	
12	1	Trigger arm			L=350	43996	0,2
11	1	Fork pin				19141934	3,8
10	1	Set screw				19113946	0,48
9	1	Leaf spring				19113945	8,5
8	1	Hinge pin				19119857	36
7	1	Mullion				77823	1373
6	4	Shaft nut		M40x1.5	KM8	19201148	0,078
5	4	Thrust washer			GLY.PXG 527802 A	19201700	
4	2	Washer				19112647	0,3
3							
2	1	Fork				19123489	137
1	1	Mullion extension				77821	189
item	**qty**	**description**	**material**	**dimension**	**remarks**	**art.no/ drwng.no.**	**weight kg/pc.**

GMR Aero Technic Hangar1 **Total weight (kg): 2171**

India

Megadoor 79014x23000/14000 Date: 2022-11-02

Swing-up mullion #45 **Project no.** 84800

Parts list. 77820.xls Designed: EB

Ref. to assembly drawing no. 77820.dwg Revision: --

Stated tightening torque refers to dry screw and nut, unless noted otherwise, and a torque wrench with max. tolerance of ±5%. At re-check, the tightening torque must be within ±25% of stated torque.

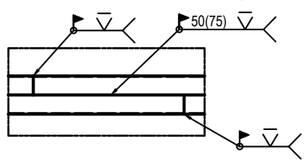

Mullion weld joint, scale 1:20

Electrode: ESAB OK48
Filarc 88S
Maxeta 22
Lincoln 7018
Hyundai SM-70
or similar.

NOTE!
Max. allowed compression of spring is 10mm

Springs should be set to a minimum of compression when mullion is hanging straight in vertical position. Adjust set screws simultaneously when adjustment is required to ensure a positive fit of base pin in floor guide.

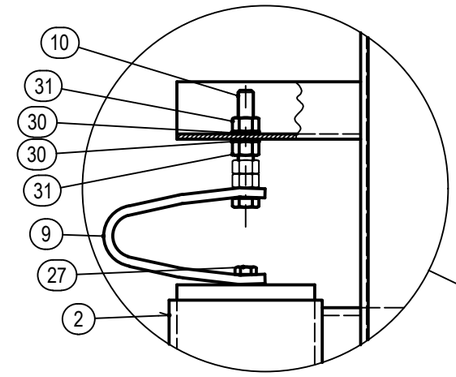

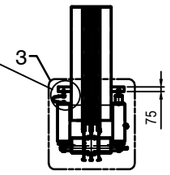

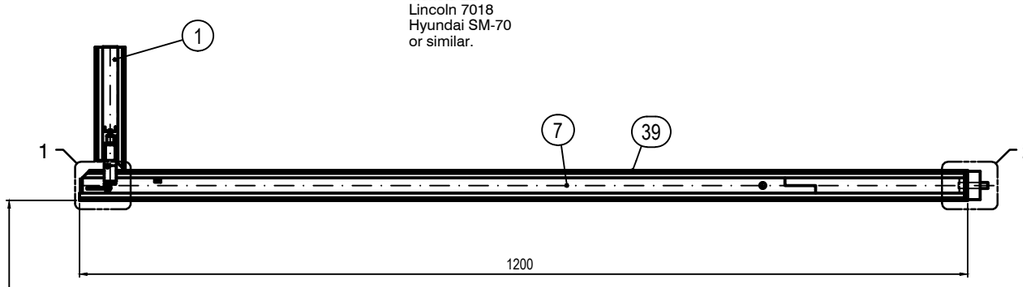

View from inside building

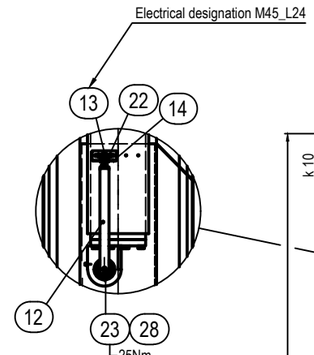

Set trigger arm so that limit switch is activated when mullion is in vertical position.
Drill Ø5x10 hole in shaft for tension pin.

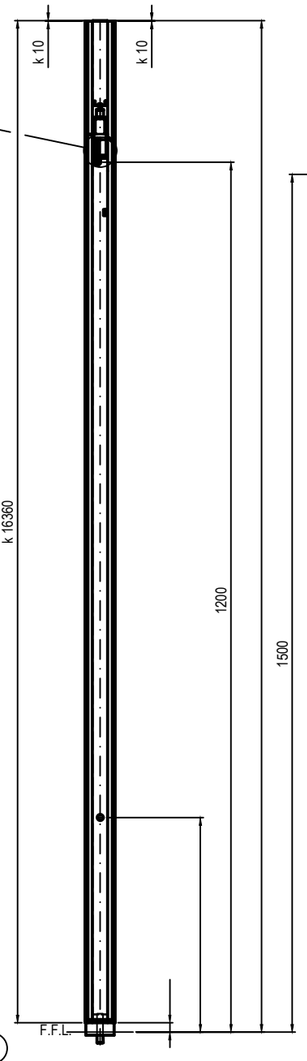

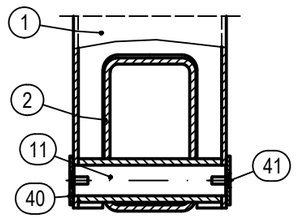

Section through
Mullion Extension Joint, typ.

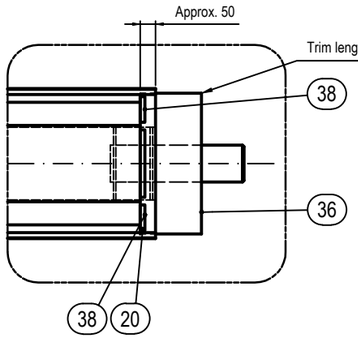

Detail 2, scale 1:10

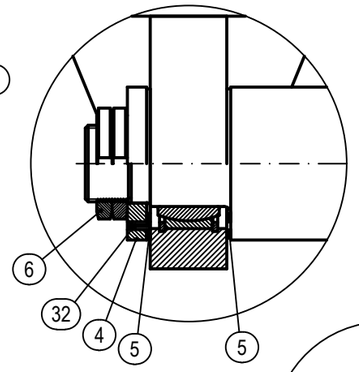

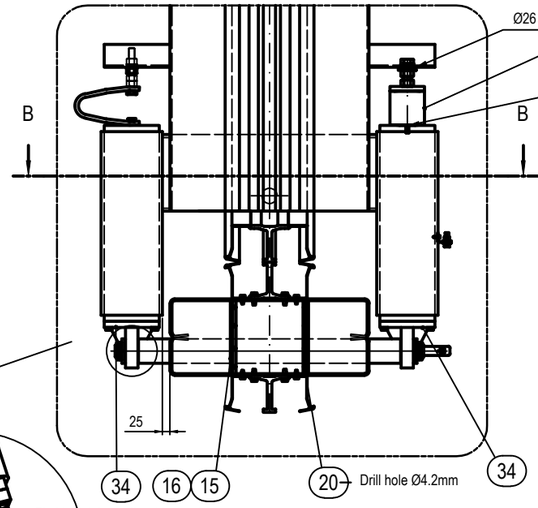

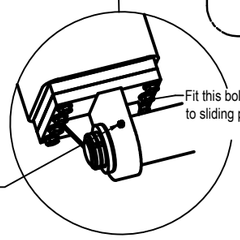

Grease bearing assemblies after mounting

Detail 3, scale 1:10

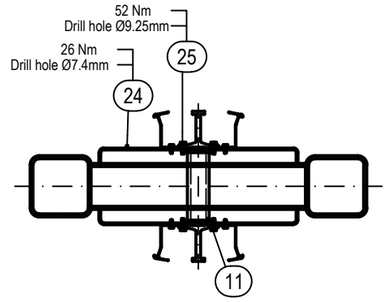

Section B -- B

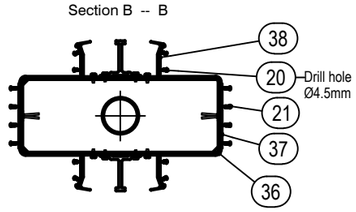

View A -- A, scale 1:10

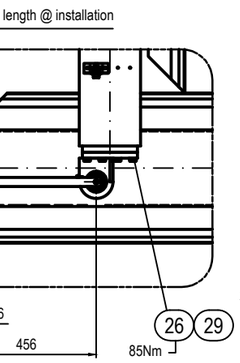

Detail 1, scale 1:10

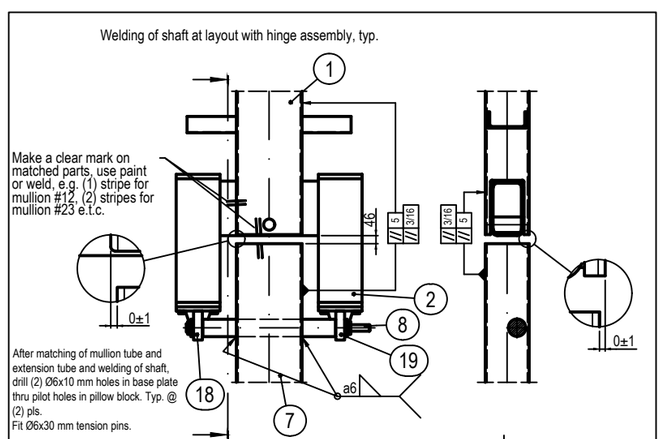

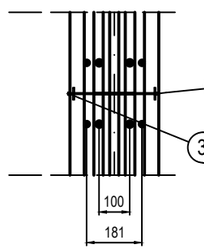

Detail @ System 1500
Guide Rail Joint, typ.

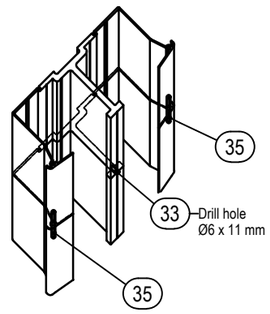

Painting instructions acc. to 44626.dwg

TITLE - MEGA DOOR				NIHVA Technologies Pvt. Ltd. — NIHVA TECHNOLOGIES PVT.LTD.PUNE — Website - www.nihva.com
DWG NO -			QTY - 1	
	NAME	SIGNATURE	DATE	PROJECT NO -
DRAWN	S.W		17-07-2025	PRODUCT -
CHK'D	P.M.		17-72025	SITE LOCATION -
APPV'D	V.T.		17-07-2025	
if any queries contact - supportautomation@nihva.com				REVISION -
ALL DIMENSION ARE IN mm		A3		SCALE - SHEET 1 OF 1

This document is the property of ASSA ABLOY Entrance Systems AB and shall not be used without permission, nor copied. It is not to be loaned to a third party or used for any other unauthorized purpose.

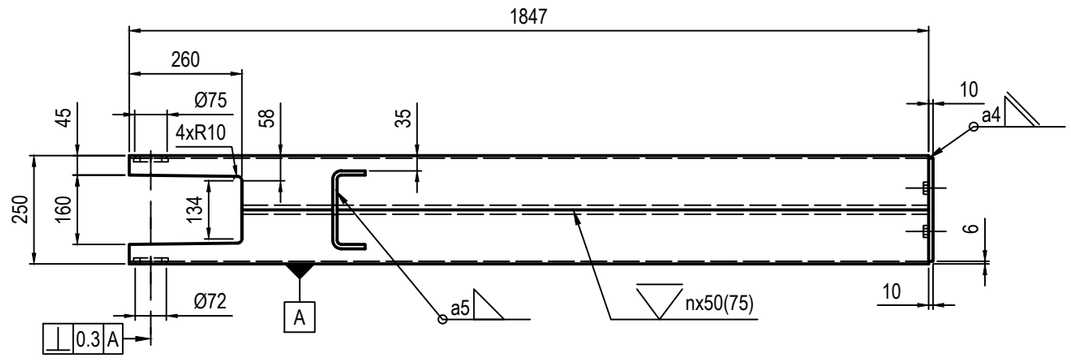

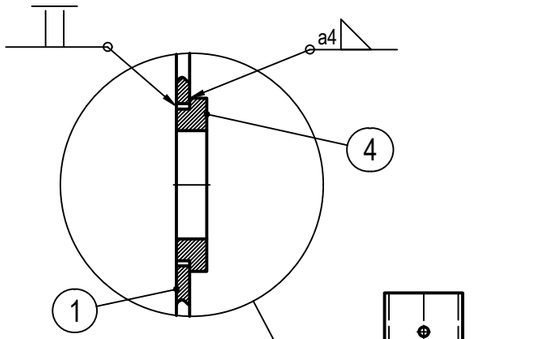

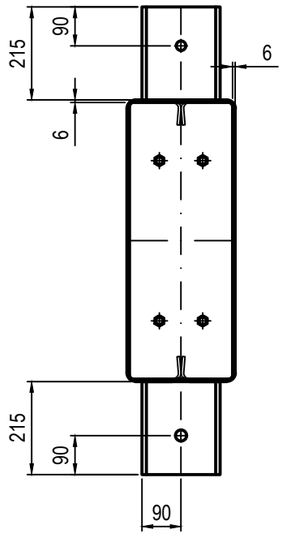

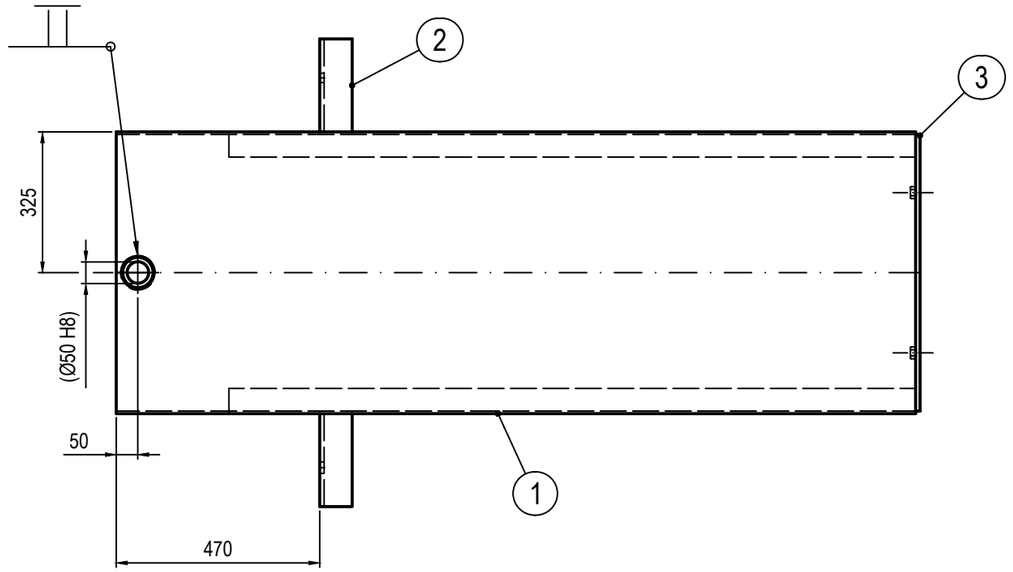

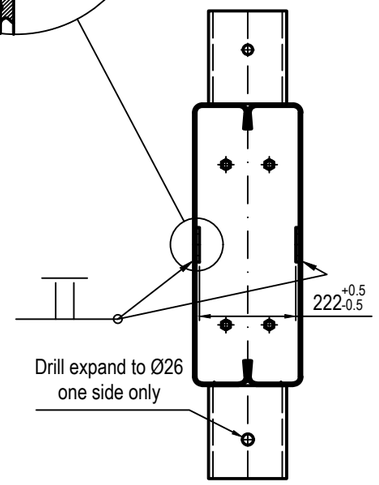

Painted colour light grey (RAL 7047). Standard acc. to A4-1500
Painting instructions acc. to 44626.dwg
Section area item #1= 5755 (mm^2)
Surface treatment area= 3.3 (m^2)
Weight= 189 (kg)

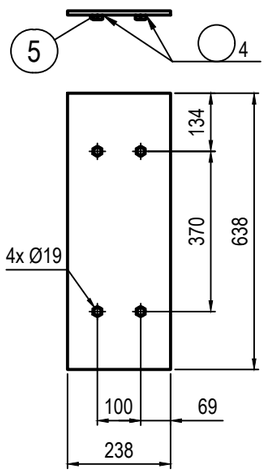

Item #3 & #5

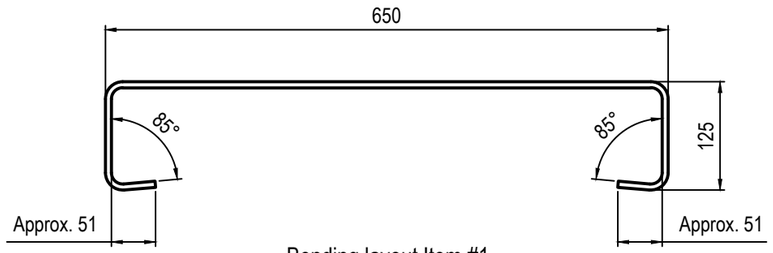

Bending layout Item #1,
scale1:5

TITLE - MEGA DOOR				NIHVA TECHNOLOGIES PVT.LTD.PUNE
DWG NO -			QTY - 1	Website - www.nihva.com
	NAME	SIGNATURE	DATE	PROJECT NO -
DRAWN	S.W		17-07-2025	PRODUCT -
CHK'D	P.M.		17-72025	SITE LOCATION -
APPV'D	V.T.		17-07-2025	
if any queries contact - supportautomation@nihva.com				REVISION -
ALL DIMENSION ARE IN mm			A3	SCALE - SHEET 1 OF 1

This document is the property of ASSA ABLOY Entrance Systems AB and shall not without our written permission be copied, imparted to a third party or used for any other unauthorized purpose.

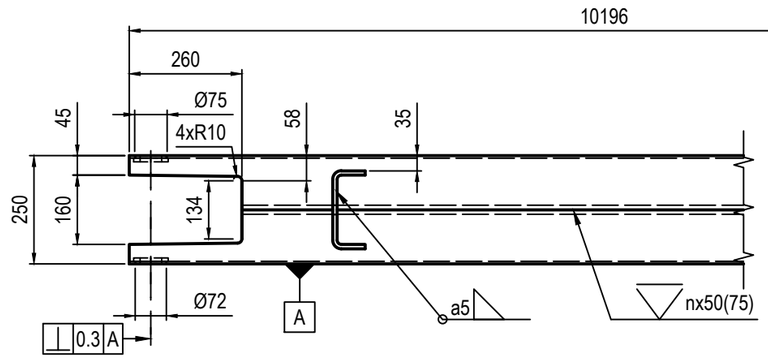

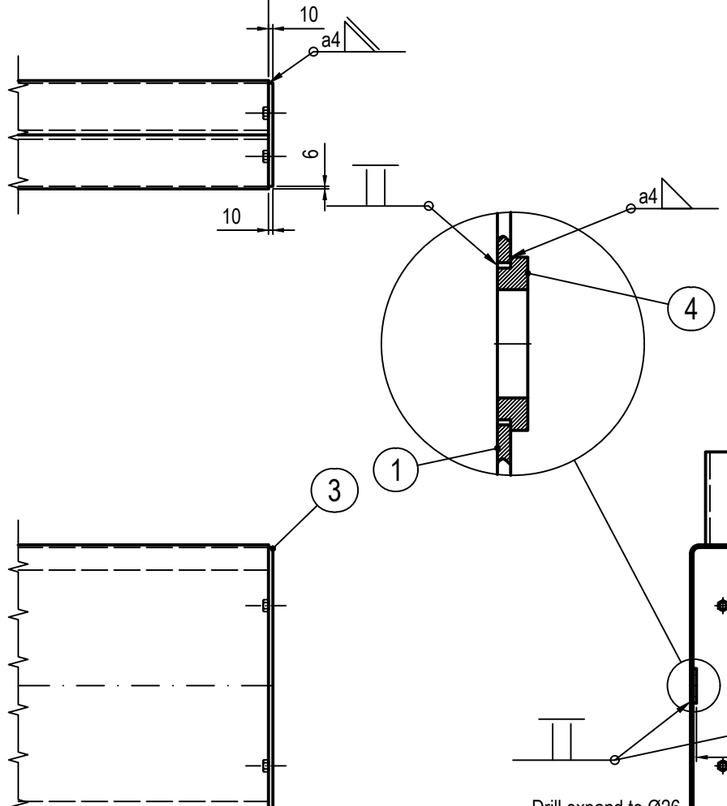

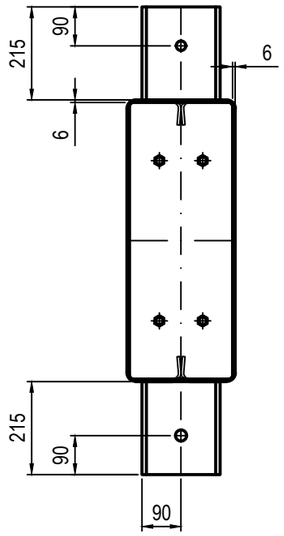

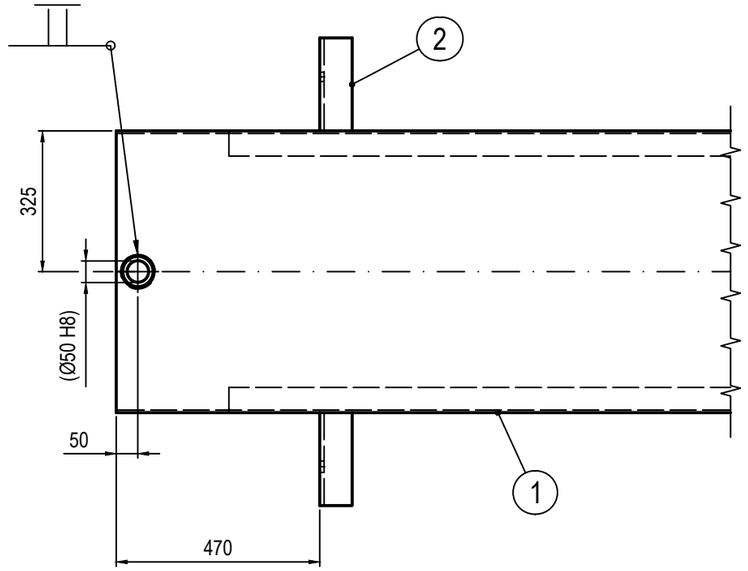

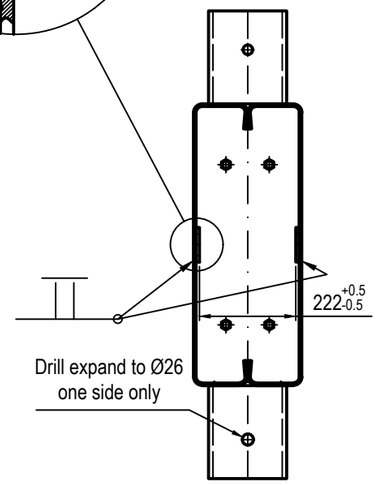

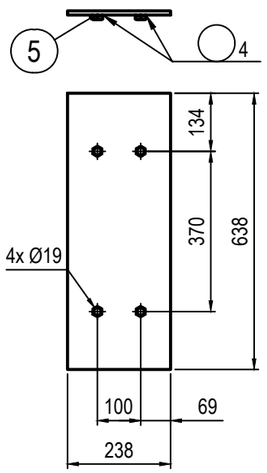

Item #3 & #5

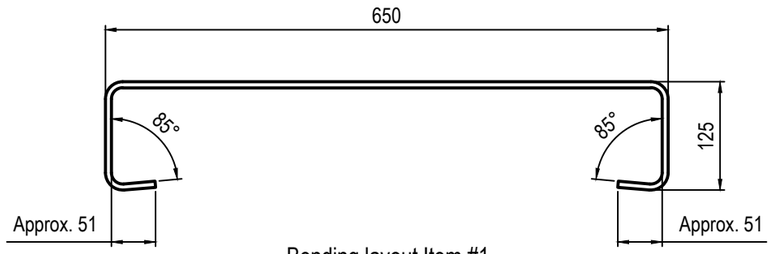

Bending layout Item #1,
scale1:5

Painted colour light grey (RAL 7047). Standard acc. to A4-1500
Painting instructions acc. to 44626.dwg
Section area item #1= 5755 (mm^2)
Surface treatment area= 18.4 (m^2)
Weight= 944 (kg)

TITLE - MEGA DOOR				NIHVA TECHNOLOGIES PVT.LTD.PUNE
DWG NO -			QTY - 1	Website - www.nihva.com
	NAME	SIGNATURE	DATE	PROJECT NO -
DRAWN	S.W		17-07-2025	PRODUCT -
CHK'D	P.M.		17-72025	SITE LOCATION -
APPV'D	V.T.		17-07-2025	
if any queries contact - supportautomation@nihva.com				REVISION -
ALL DIMENSION ARE IN mm			A3	SCALE - SHEET 1 OF 1

This document is the property of ASSA ABLOY Entrance Systems AB and shall not without our written permission be copied, imparted to a third party or used for any other unauthorized purpose.

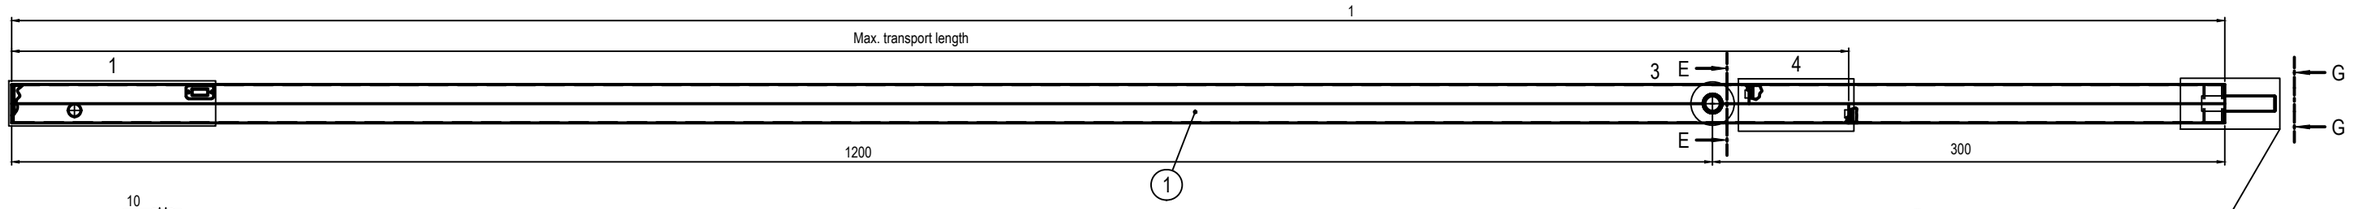

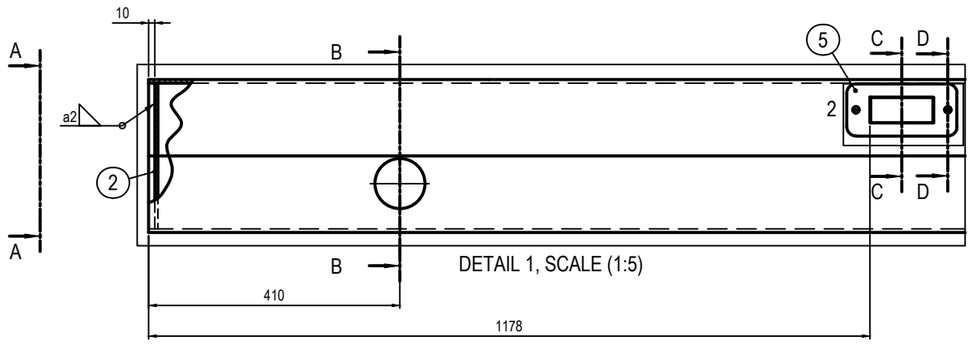

DETAIL 1, SCALE (1:5)

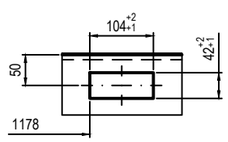

DETAIL 2, SCALE (1:5)
Item 5 not shown.

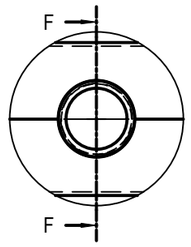

DETAIL 3, SCALE (1:5)

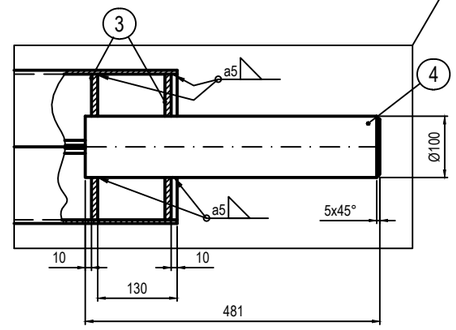

SCALE (1:5)

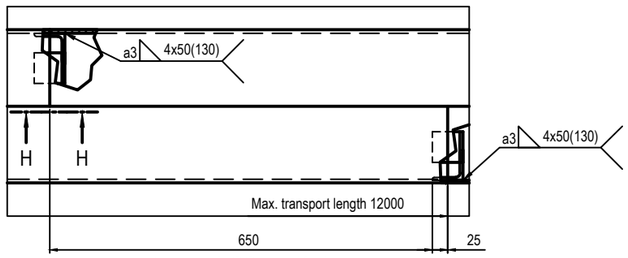

DETAIL 4, SCALE (1:5)
Splice method item #1.

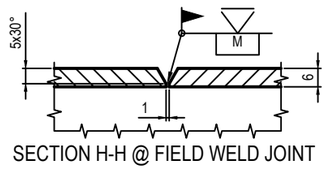

SECTION H-H @ FIELD WELD JOINT

ELECTRODES:
ESAB OK 48.00
Filarc 88S
Maxeta 22
Lincoln 7018
Hyundai SM-70
or similar.

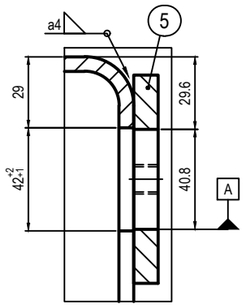

DETAIL 5, SCALE (1:5)

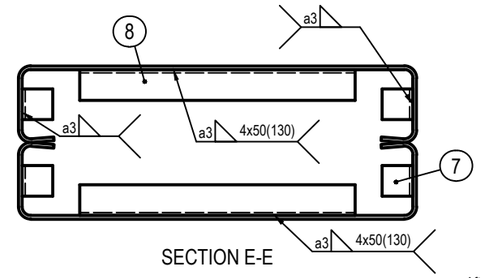

SECTION E-E

After welding item 5 to mullion tube,drill 4xØ10,2 and tap for M12 screw.

SECTION A-A (1:5)

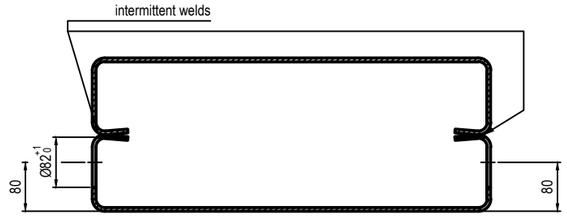

SECTION B-B(1:5)

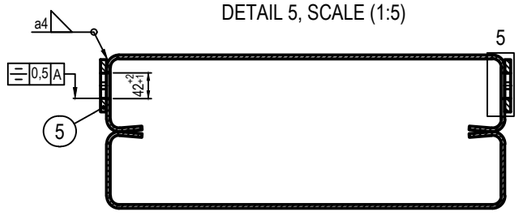

SECTION C-C (1:5)

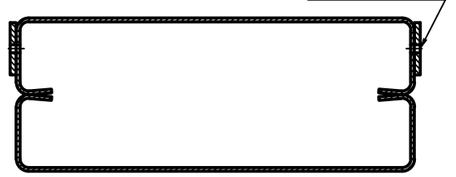

SECTION D-D

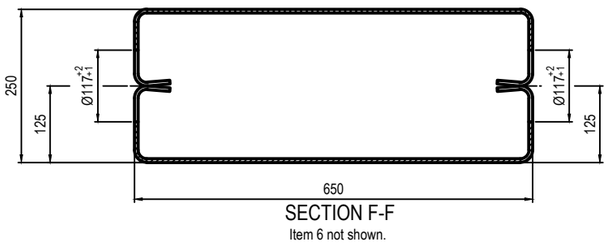

SECTION F-F
Item 6 not shown.

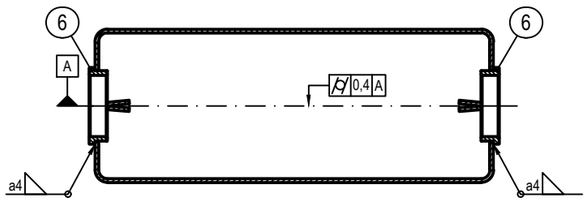

SECTION F-F'

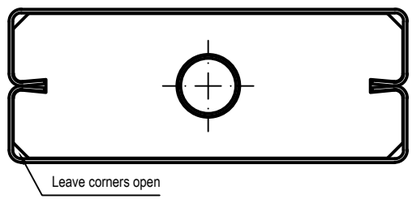

SECTION G-G

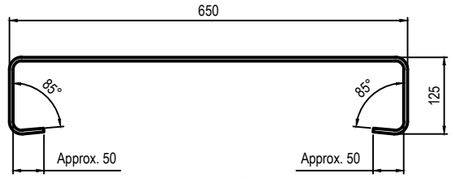

Bending layout item #1, scale 1:5

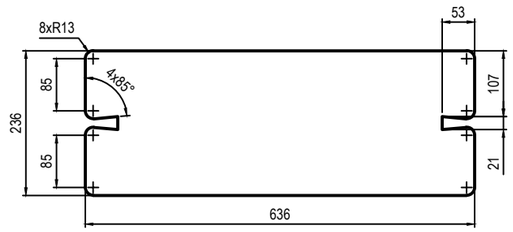

Item #2 (1:5)

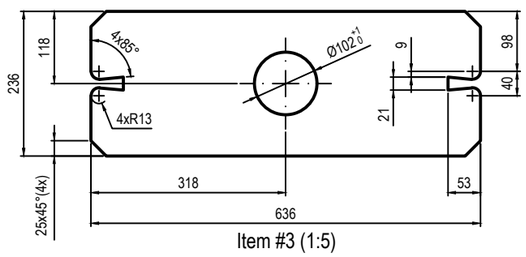

Item #3 (1:5)

TITLE - MEGA DOOR				NIHVA TECHNOLOGIES PVT.LTD.PUNE
DWG NO -			QTY - 1	NIHVA Technologies Pvt. Ltd. Website - www.nihva.com
	NAME	SIGNATURE	DATE	PROJECT NO -
DRAWN	S.W		17-07-2025	PRODUCT -
CHK'D	P.M.		17-72025	SITE LOCATION -
APPV'D	V.T.		17-07-2025	
if any queries contact - supportautomation@nihva.com				REVISION -
ALL DIMENSION ARE IN mm			A3	SCALE - SHEET 1 OF 1

This document is the property of ASSA ABLOY Entrance Systems AB and shall not be reproduced or used without permission, neither disclosed to a third party or used for any other unauthorized purpose.

100	1	Guide rail, fixed straight		500		51529	4,3
99	1	Guide rail, fixed angled		660		51530	4,7
81	1	Seal angle		1846		19114552	2,7
80	1	Seal angle		1846		19114552	2,7
71	1	Seal angle		962		19114552	1,4
70	1	Seal angle		962		19114552	1,4
61	1	Seal angle		2012		19114552	2,9
60	1	Seal angle		2012		19114552	2,9
51	1	Seal angle		916		19114552	1,3
50	1	Seal angle		916		19114552	1,3
41	2	Seal angle		5500		19114552	7,9
40	2	Seal angle		5500		19114552	7,9
31	2	Seal angle		6000		19114552	8,7
30	2	Seal angle		6000		19114552	8,7
11	2	Seal angle		2041		19114552	2,9
10	2	Seal angle		2041		19114552	2,9
8	1	Guide rail		1346		19149911	11,9
7	1	Guide rail		962		19149911	8,5
6	1	Guide rail		1352		19149911	12,0
5	1	Guide rail		916		19149911	8,1
4	2	Guide rail		5500		19149911	48,8
3	2	Guide rail		6000		19149911	53,2
2	2	Guide rail		642		19149911	5,7
1	2	Guide rail		1399		19149911	12,4
item	**qty**	**description**	**material**	**length**	**remarks**	**art.no.**	**weight kg/pc**

GMR Aero Technic Hangar1
India
Megadoor 79014x23000/14000
Swing-up Mullions, Guide rails #12 & 45
Parts list no. 77824.xls
Ref. to assy. Drwng. no. 77824.dwg

Date: 2022-11-02
Project no: 84800
Designed by: EB
Revision: ---

Total weight / mullion (kg): 385

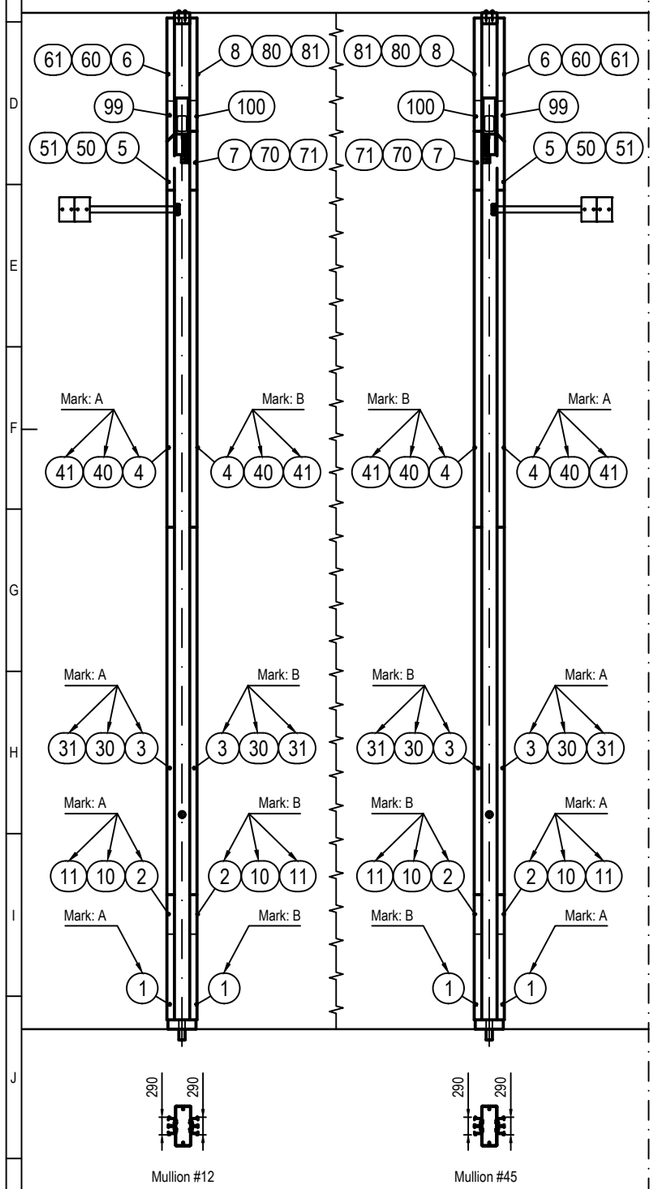

Guide rail location on mullion,
Interior view, scale 1:50

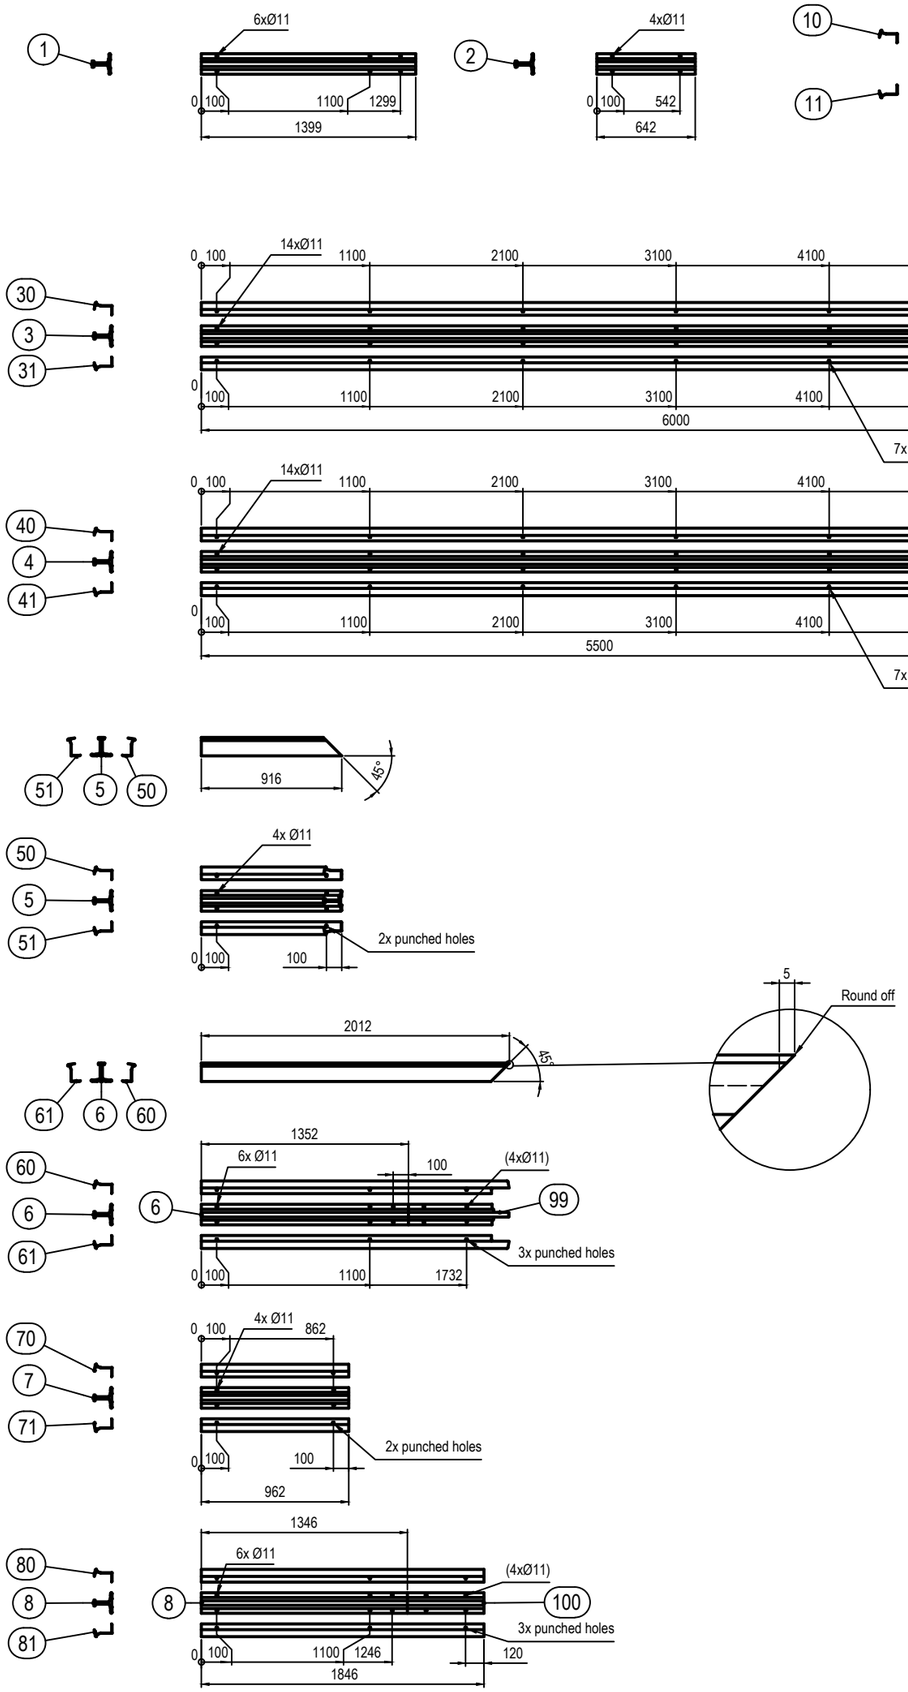

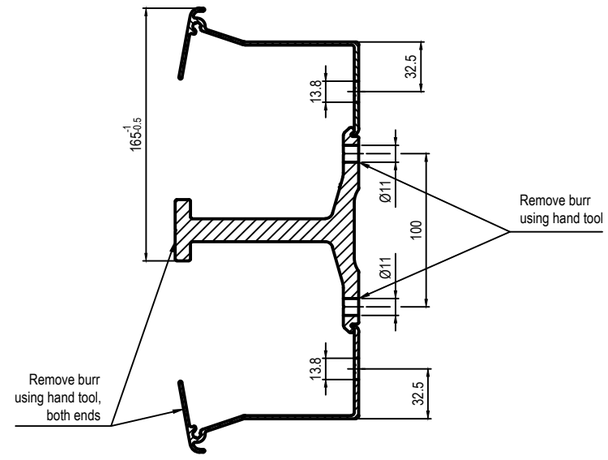

SECTION A-A, scale 1:2

Parts list, ref. to 77824.xls

Total rail weight: 385 kg

DESIGNED EB	SIZE A1	SCALE 1:20	GMR Aero Technic Hangar1
CODE 84800	If not otherwise stated: Tolerances ISO 2768-m EN ISO 13920-B		India
ITEM NO	Cutting class ISO 9013-442		Megadoor 79014x23000/14000
DATE 2022-11-02	Weld class ISO 5817-C		Guide rails mullion #12 & 45
ASSA ABLOY	Surface finish Smooth raw surface	DRAWING NO 77824	REVISION --

PLOT DATE

This document is the property of ASSA ABLOY Entrance Systems AB and shall not be reproduced or disclosed to a third party or used for any other unauthorized purpose.

100	1	Guide rail, fixed straight		500		51529	4,3
99	1	Guide rail, fixed angled		660		51530	4,7
81	1	Seal angle		4195		19114552	6,1
80	1	Seal angle		4195		19114552	6,1
71	1	Seal angle		962		19114552	1,4
70	1	Seal angle		962		19114552	1,4
61	1	Seal angle		2012		19114552	2,9
60	1	Seal angle		2012		19114552	2,9
51	1	Seal angle		916		19114552	1,3
50	1	Seal angle		916		19114552	1,3
41	2	Seal angle		5500		19114552	7,9
40	2	Seal angle		5500		19114552	7,9
31	3	Seal angle		6000		19114552	8,7
30	3	Seal angle		6000		19114552	8,7
11	2	Seal angle		2041		19114552	2,9
10	2	Seal angle		2041		19114552	2,9
8	1	Guide rail		3695		19149911	32,8
7	1	Guide rail		962		19149911	8,5
6	1	Guide rail		1352		19149911	12,0
5	1	Guide rail		916		19149911	8,1
4	2	Guide rail		5500		19149911	48,8
3	3	Guide rail		6000		19149911	53,2
2	2	Guide rail		642		19149911	5,7
1	2	Guide rail		1399		19149911	12,4
item	**qty**	**description**	**material**	**length**	**remarks**	**art.no.**	**weight kg/pc**

GMR Aero Technic Hangar1
India
Megadoor 79014x23000/14000
Swing-up Mullions, Guide rails #23 & 34
Parts list no. 77825.xls
Ref. to assy. Drwng. no. 77825.dwg

Date: 2022-11-02
Project no: 84800
Designed by: EB
Revision: ---

Total weight / mullion (kg): 483

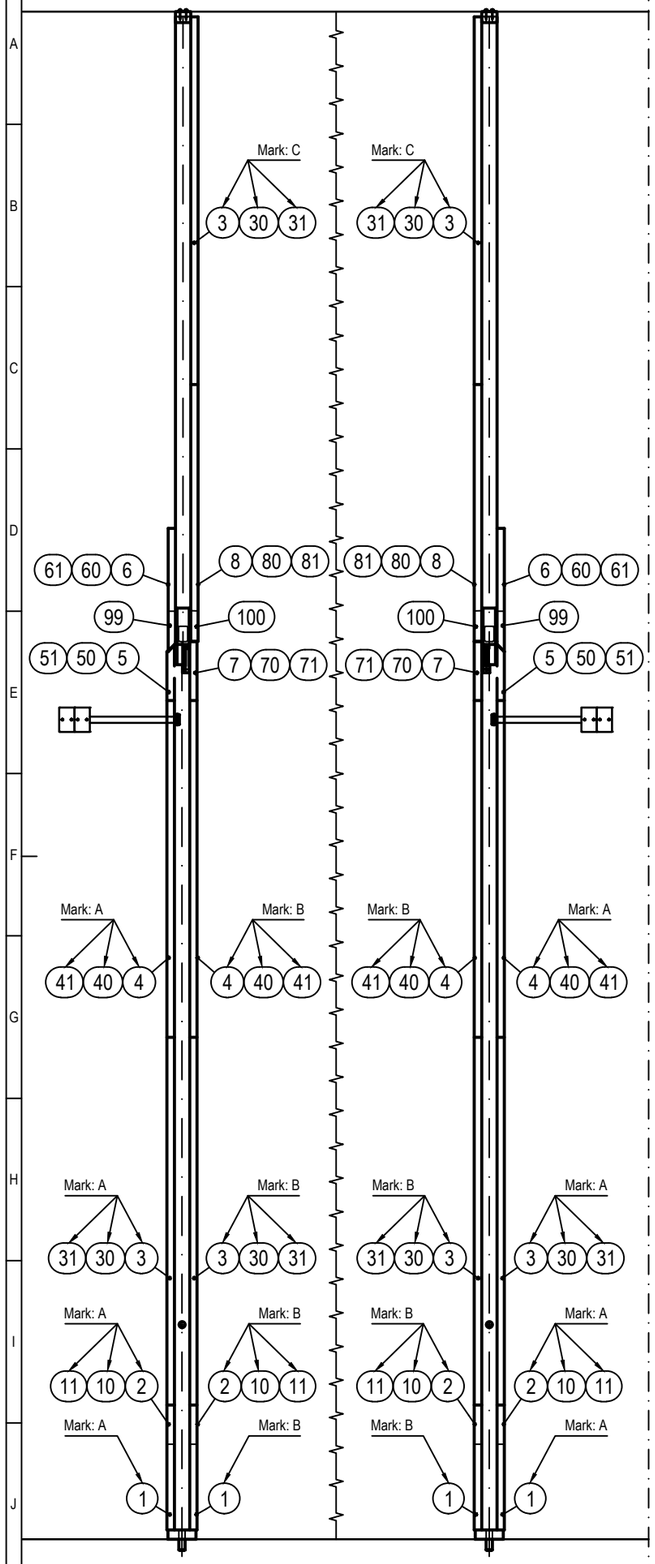

Mullion #23 Mullion #34

Guide rail location on mullion,
Interior view, scale 1:50

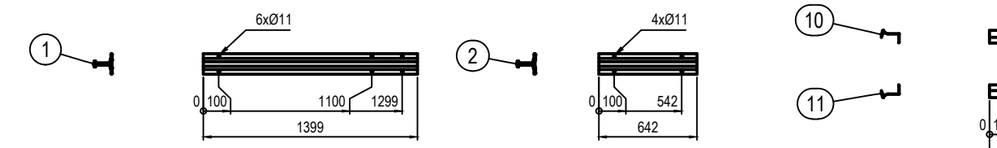

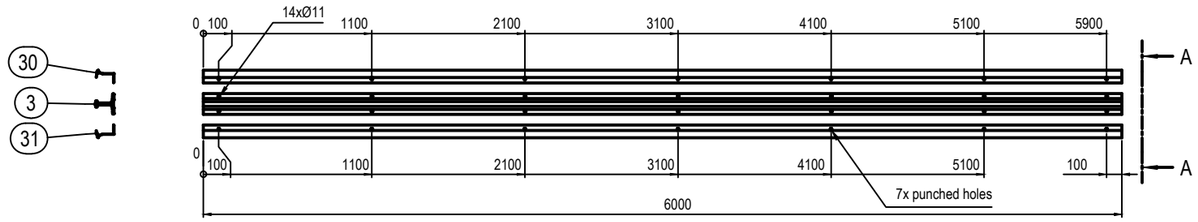

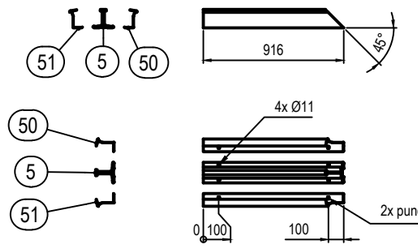

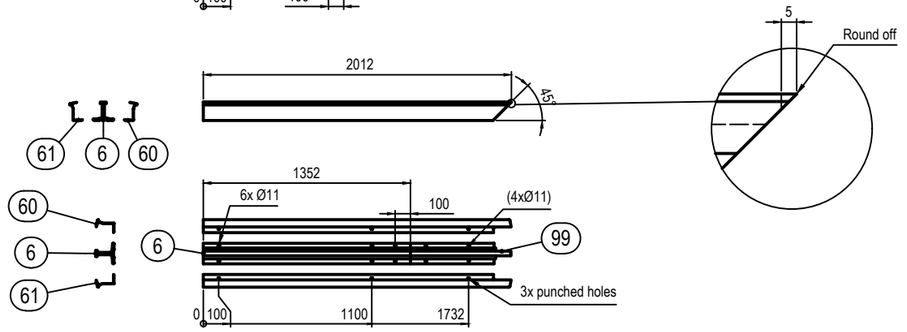

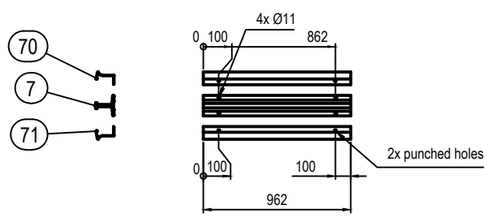

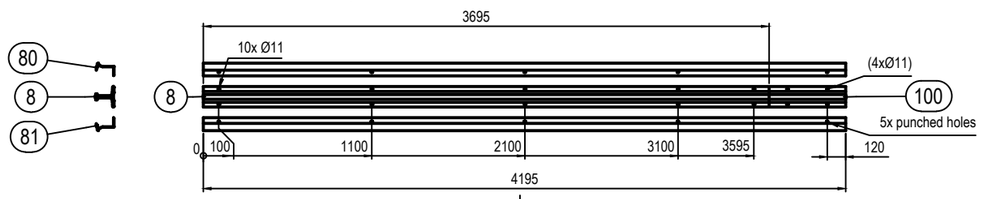

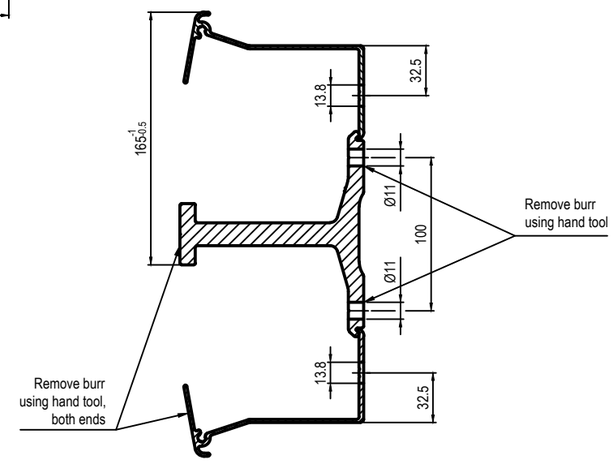

SECTION A-A, scale 1:2

Parts list, ref. to 77825.xls

Total rail weight: 483 kg

DESIGNED EB		SIZE A1	SCALE 1:20
CODE 84800	If not otherwise stated:		
ITEM NO	Tolerances ISO 2768-m EN ISO 13920-B		
DATE 2022-11-02	Cutting class ISO 9013-442		
ASSA ABLOY	Weld class ISO 5817-C		
	Surface finish Smooth raw surface		

GMR Aero Technic Hangar1
India
Megadoor 79014x23000/14000
Guide rails mullion #23 & 34

DRAWING NO 77825

REVISION --

PLOT DATE

This document is the property of ASSA ABLOY Entrance Systems AB and shall not be reproduced or disclosed to any third party or used for any other unauthorized purpose.

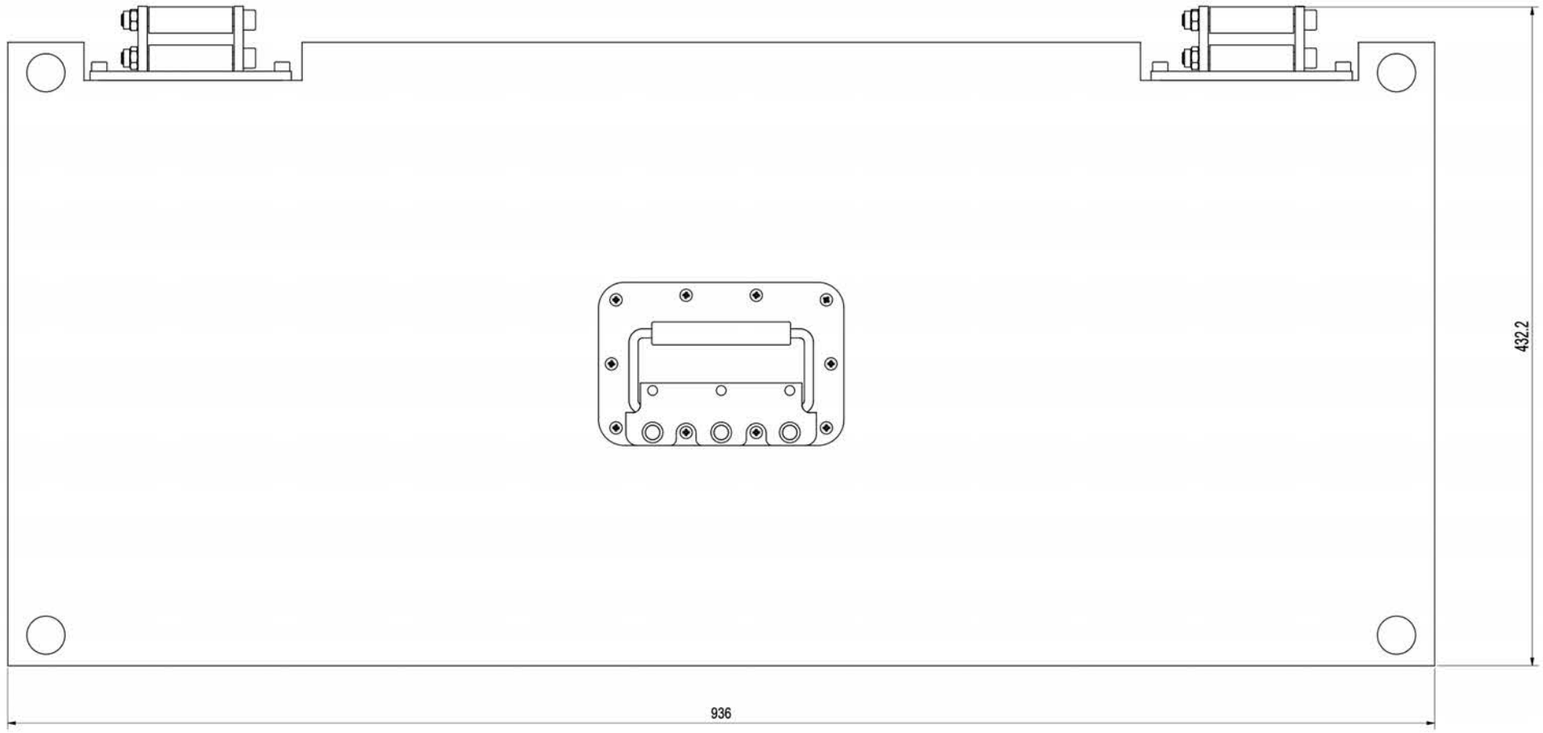

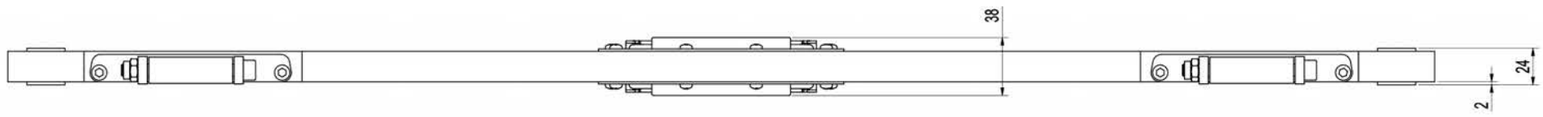

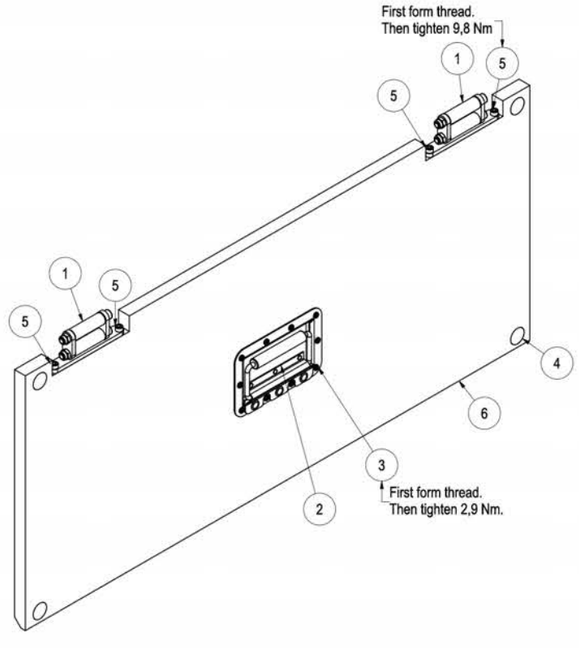

Total weight: 21 kg

ITEM	QTY	DESCRIPTION	DIMENSION	MATERIAL	REMARKS	kg/pc
6	1	Large floor pit cover			77827	19,5
5	4	Screw	MC6S-TT 6x30		19202367	0,0
4	4	Cell rubber string	Ø25, l=24 mm	EPDM	19203652	0,0
3	20	Screw	MRT-TT 4x8	8.8	19203200	0,0
2	2	Handle, Wiberger	Wiberger no. kh38-7151		19203653	0,5
1	2	Link, assembled			63828	0,4

DESIGNED: EB | APPROVED: | SIZE: A1 | SCALE: 1:2

CODE: 84800

ITEM NO:

DATE: 2022-11-02

If not otherwise stated:
Tolerances ISO 2768-m EN ISO 13920-B
Cutting class ISO 9013-442
Weld class ISO 5817-C
Surface finish Smooth raw surface

ASSA ABLOY

GMR Aero Technic Hangar1

India

Megadoor 79014x23000/14000

Large floor pit cover, assembly

DRAWING NO: 77826

REVISION: --

PLOT DATE

This document is the property of ASSA ABLOY Entrance Systems AB and shall not without our written permission be copied, imparted to a third party or used for any other unauthorized purpose.

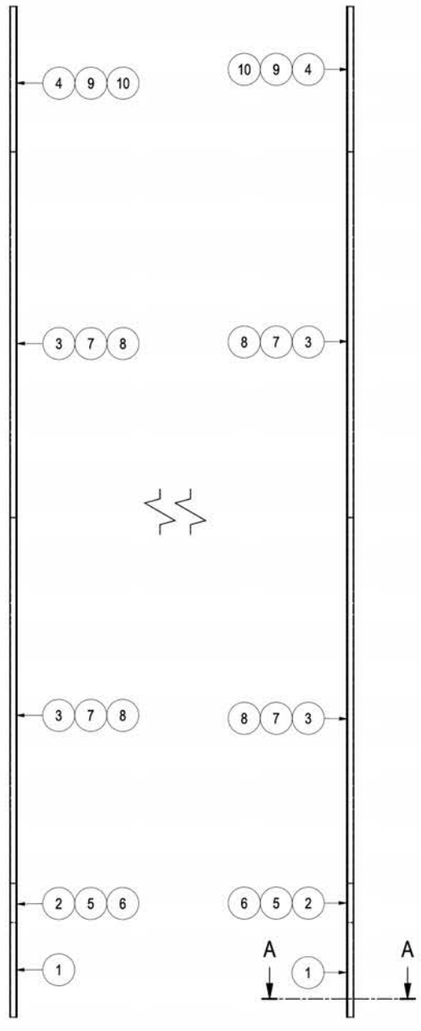

Guide rail location in building (1 : 50)

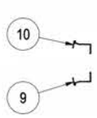

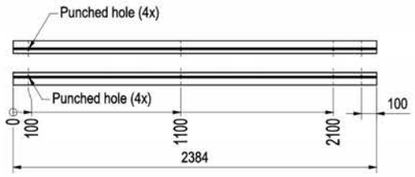

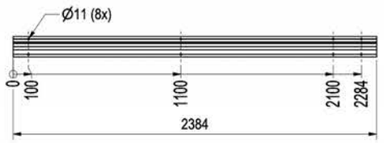

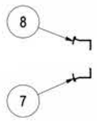

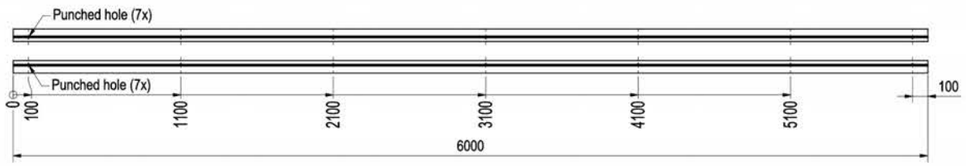

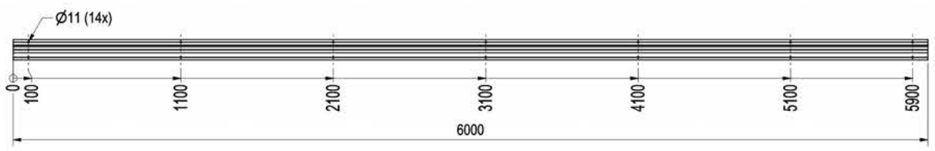

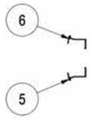

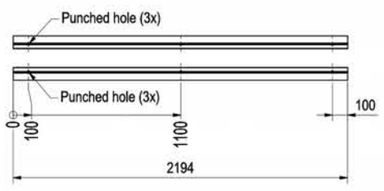

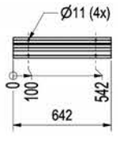

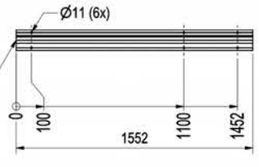

Place this side down.
All profiles.

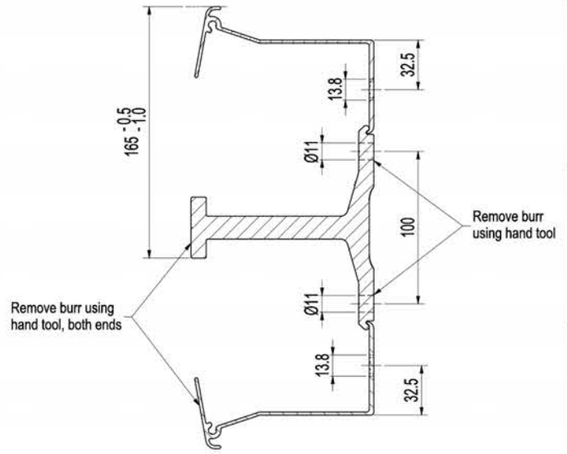

SECTION A-A (1 : 2)

ITEM	QTY	DESCRIPTION	DIMENSION	MATERIAL	REMARKS	kg/pc
10	2	Seal angle	L = 2384		19114552	3,4
9	2	Seal angle	L = 2384		19114552	3,4
8	4	Seal angle	L = 6000		19114552	8,7
7	4	Seal angle	L = 6000		19114552	8,7
6	2	Seal angle	L = 2194		19114552	3,2
5	2	Seal angle	L = 2194		19114552	3,2
4	2	Guide rail	L = 2384		19149911	21,0
3	4	Guide rail	L = 6000		19149911	53,0
2	2	Guide rail	L = 642		19149911	5,7
1	2	Guide rail	L = 1552		19149911	13,7

Total weight: 388 kg

DESIGNED: EB
SIZE: A1
SCALE: 1 : 50
CODE: 84800
ITEM NO:
DATE: 2021-12-17
If not otherwise stated:
Tolerances ISO 2768-m EN ISO 13920-B
Cutting class ISO 9013-442
Weld class ISO 5817-C
Surface finish Smooth raw surface

GMR Aero Technic Hangar1

India

Megadoor 79014x23000/14000

Guide rails

ASSA ABLOY

DRAWING NO: 77828

REVISION: --

PLOT DATE:

This document is the property of ASSA ABLOY Entrance Systems AB and shall not without our written permission be copied, imparted to a third party or used for any other unauthorized purpose.

Revision		Date	By
A	Corrected mullion hoist positions, floor pits altered	2022-09-02	EB
B	New measurements, doors redrawn, recalculated	2022-10-12	EB

LOAD DIAGRAM
Nominal static vertical loads are indicated. Value within brackets include dynamic surload factor 1.25 for door leaf loads in open position.
Includes items provided by ASSA ABLOY only.

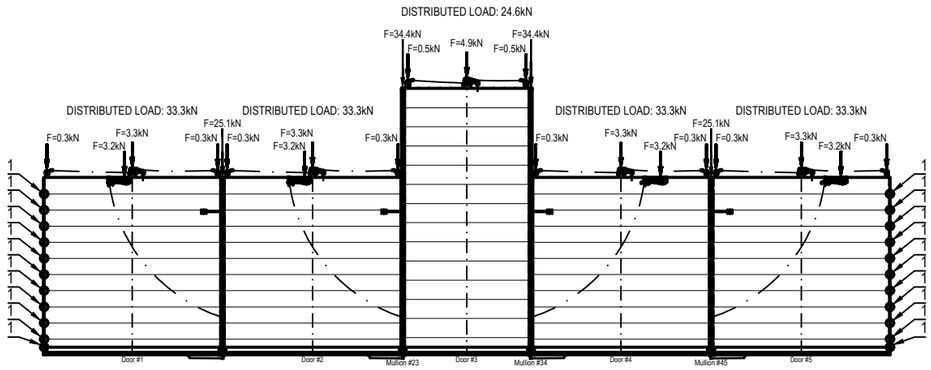

Interior view, door closed

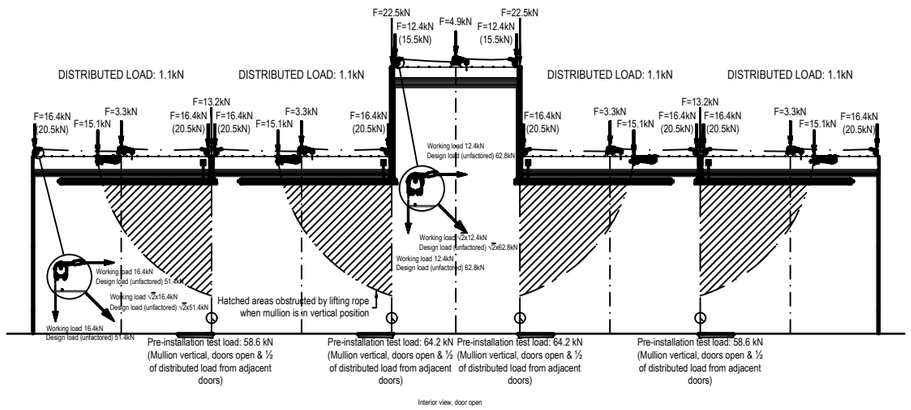

Interior view, door open

Steel building company in cooperation with door installing company must make a pre-installation load test on the structure, where the mullions are located, in order to simulate the vertical deflection of the structure that occurs when doors are installed. This vertical deflection figure will be used to determine the correct installation level of the mullions. Required material/equipment and personnel by others than ASSA ABLOY.

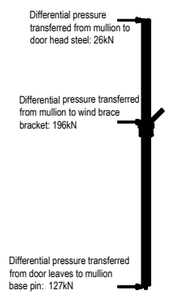

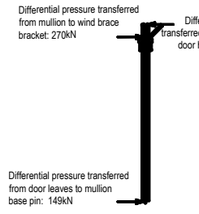

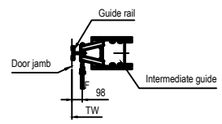

Force by differential pressure transferred to guide rail at each intermediate position. (located at pos 1)
F=14.8 kN

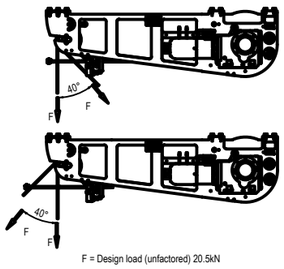

F = Design load (unfactored) 20.5kN

Force from mullion wire rope hoists
Scale 1:20

HOIST 4.9T

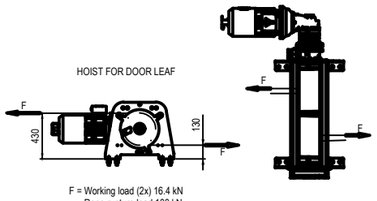

F = Working load (2x) 16.4 kN
Rope rupture load 100 kN

HOIST 5.9T

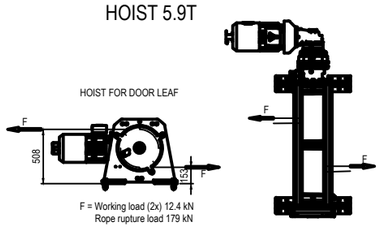

F = Working load (2x) 12.4 kN
Rope rupture load 179 kN

NOT INCLUDED IN DOOR SUPPLY:
1. Design and supply of all door supporting structural components.
2. Design and supply of all closure between door and adjacent steel.
3. Design and supply of coverage, such as roofing or enclosure, for door components at door head.
4. Door jambs adjustable for overall door width and true to plumb.
5. Paint job after completed door installation.
6. Any frameworks being provided by ASSA ABLOY will be clearly indicated as "by ASSA ABLOY".

REQUIREMENTS ON BUILDING:
7. Door head support must be straight within 1/600 of span in the in/out direction and free from protrusions of any kind.
8. For a single door leaf, door head support should be horizontal and straight within 1/600 of span at distributed full door load.
9. Door side jambs must be smooth, straight and parallel, out of plumb must not exceed 2mm/m (total deviation at full length 5 mm) in any direction.
10. Any footings at bottom of jamb columns must not interfere with installation of guide rails at floor level.
11. At time of installation, finished floor, free from obstructions, out to a distance of 2 m on each side of door centreline must be available.
12. Bracket/attachment plate for hoist should be flat within 5mm/m.

DOOR PROPERTIES:
13. The door is designed to withstand a differential pressure of 1.2kPa.
14. Mullions and mullion pits are designed to allow for 128mm of downward deflection and 128mm of upward deflection due to external loads such as wind.
15. Guide rails, top- and intermediate beams in extruded aluminium with natural finish.
16. Environmental category: Megadoor standard
17. Bottom beam in carbon steel painted: Light grey (RAL7047)
18. Colored clamp strips on both sides
19. The door fabric is a UV stabilized, flame retardant, self-extinguishing, PVC coated polyester fabric with fire technical properties Euroclass B-s2, d0 (according to EN 13501-1:2007).
Colour of fabric: TBC
RED (NCS S2070-R, RAL 3001)
BLUE (NCS S3560-R80B, RAL 5005)
GREY (NCS 3500, RAL 7004)
WHITE (NCS 0500, RAL 9016)
TAN (NCS 2010-Y40R, RAL 1001)
WHITE ALUMINUM (RAL 9006)
GREEN (NCS 8010-G10Y, RAL 6009)
ANTHRACITE GREY (NCS 8005-B20G, RAL 7016)
(Please specify)

ELECTRICAL:
20. One main control panel provided of PLC type.
21. One additional screen.
22. Control mode : Impulse up / Constant contact down.
23. Cables are included.
24. Back-up power socket & switch.
25. Audible & visual alarm.
26. Approx. size of main control panel: WxHxD (500x600x250 mm),
27. Location of main control panel: Please specify location.
28. Aux. Voltage 24VDC
29. Power supply: 400V /3Ph /50Hz
30. Power: 41.3kW
31. Nom. current: 97.7A
32. Start. current: 214.2A
33. (max. allowed voltage drop at start: 5%)

WIRE ROPE HOIST UNIT:
LIDAN 4.9T2/27(4x)
2x Ø12mm wire ropes. Rupture load 100kN/rope.

LIDAN 5.9T2/27(1x)
2x Ø16mm wire ropes. Rupture load 179kN/rope.

MULLION HOIST UNIT:
LIDAN 1.75T/1(4x)
2x Ø10mm wire ropes. Rupture load 69.8kN/rope.

DOOR IDENTITY NUMBER: 84800001

INTERFACE, SECTIONS ref. to drwng. no. 77445

INTERFACE, PLAN VIEWS ref. to drwng. no. 77444

INTERFACE, ELEVATION ref. to drwng. no. 77443

DESIGNED EB	SIZE A1F	SCALE 1:200	GMR Aero Technic Hangar1
CODE 84800	If not otherwise stated: Tolerances ISO 2768-m EN ISO 13920-B		India
ITEM NO	Cutting class ISO 9013-4.0		Megadoor 84000x23000/14000
DATE 2022-08-24	Weld class ISO 5817-C		Load diagram & Notes
ASSA ABLOY	Surface finish Smooth raw surface	DRAWING NO 77446	REVISION B

This document is the property of ASSA ABLOY Entrance Systems AB and shall not without our written permission be copied, reported to a third party or used for any other than intended purpose.

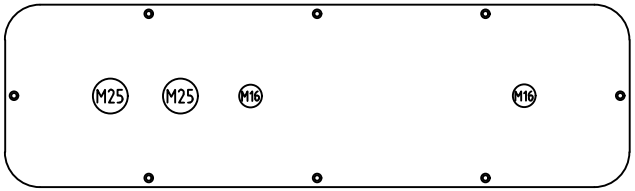

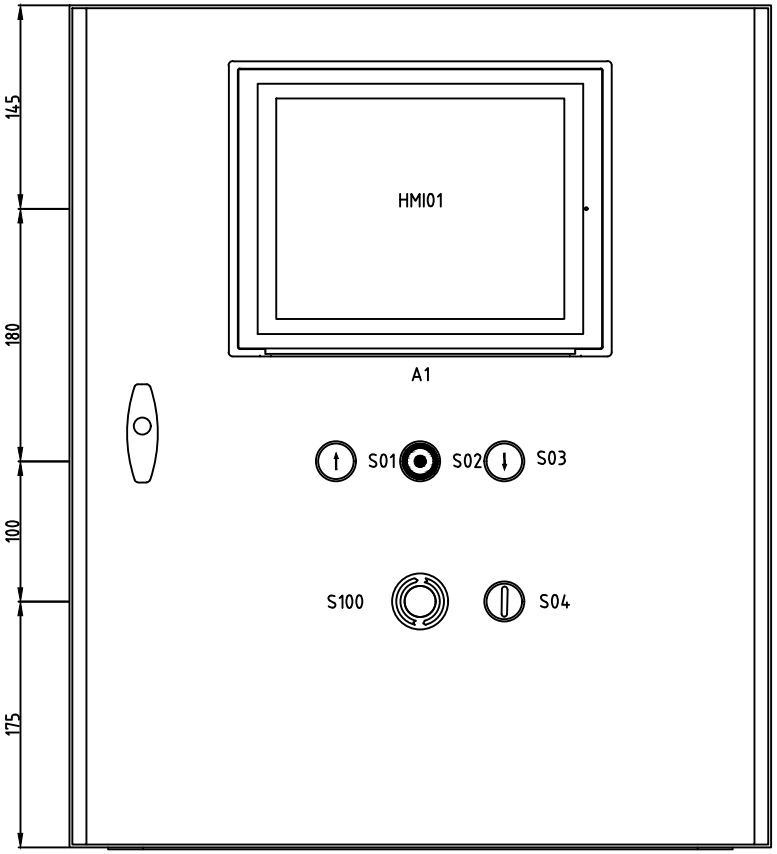

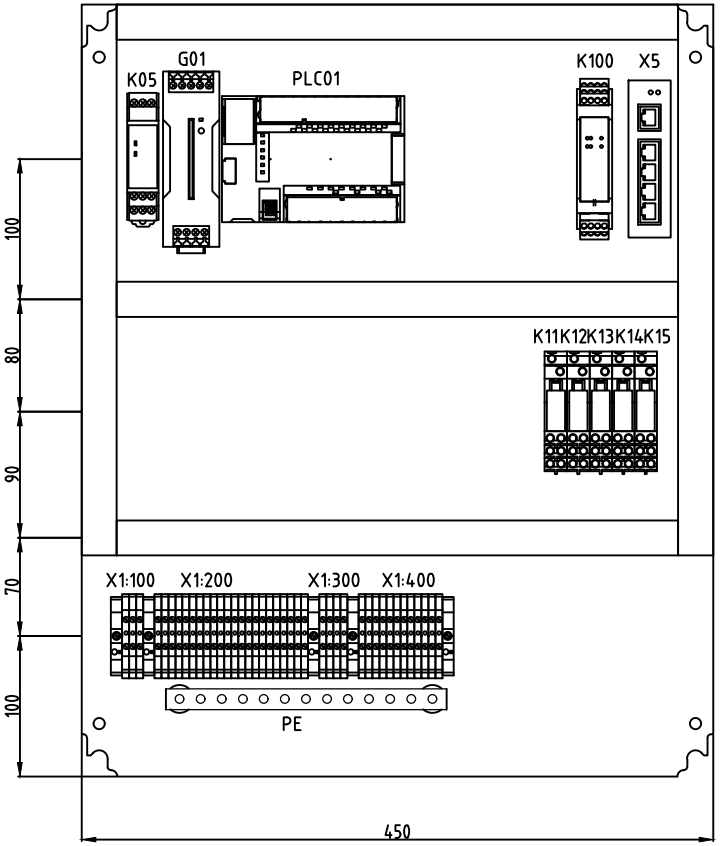

ASSA ABLOY

Property of ASSA ABLOY Entrance Systems AB and shall not without our written permission be copied, imparted to a third party or used for any other unauthorized purpose.

GMR Aero Technic Hyderabad

Direct drive | Single motor

Panel layout

Designed	Approved	Location	Code
MED	GO	+A1	84800001

Page	Date	Drawing No	Revision
1/45	221117	60109	--

ASSA ABLOY

Property of ASSA ABLOY Entrance Systems AB and shall not without our written permission be copied, imparted to a third party or used for any other unauthorized purpose.

GMR Aero Technic Hyderabad

Direct drive | Single motor

Wiring diagram

Designed	Approved	Location	Code
MED	GO	+A1	84800001

Page	2/45
Date	221117
Drawing No	60109
Revision	--

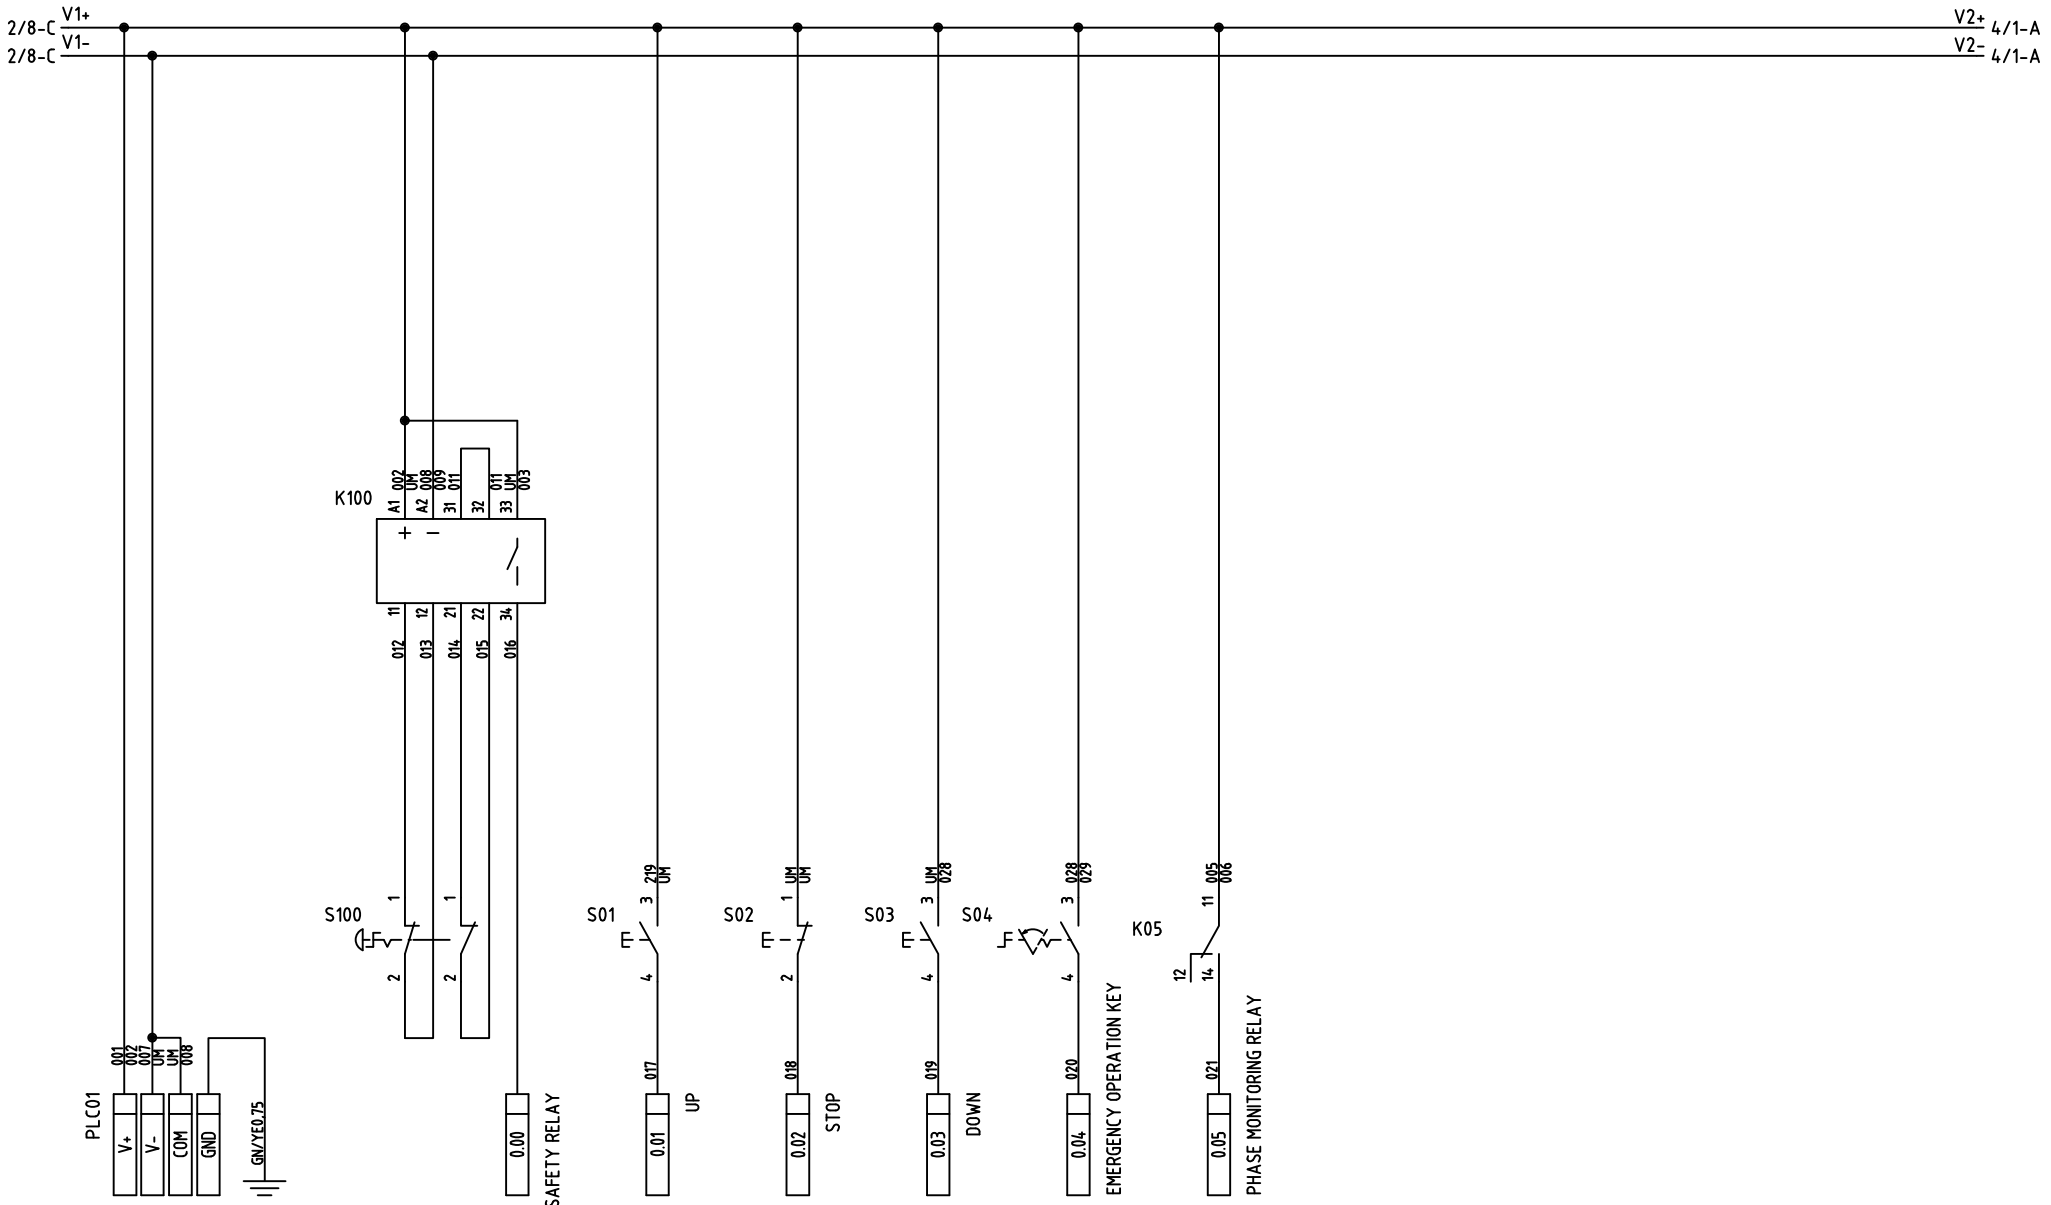

ASSA ABLOY

Property of ASSA ABLOY Entrance Systems AB and shall not without our written permission be copied, imparted to a third party or used for any other unauthorized purpose.

GMR Aero Technic Hyderabad

Direct drive | Single motor

Wiring diagram

Designed	Approved	Location	Code	Page	Date	Drawing No	Revision
MED	GO	+A1	84800001	3/45	221117	60109	--

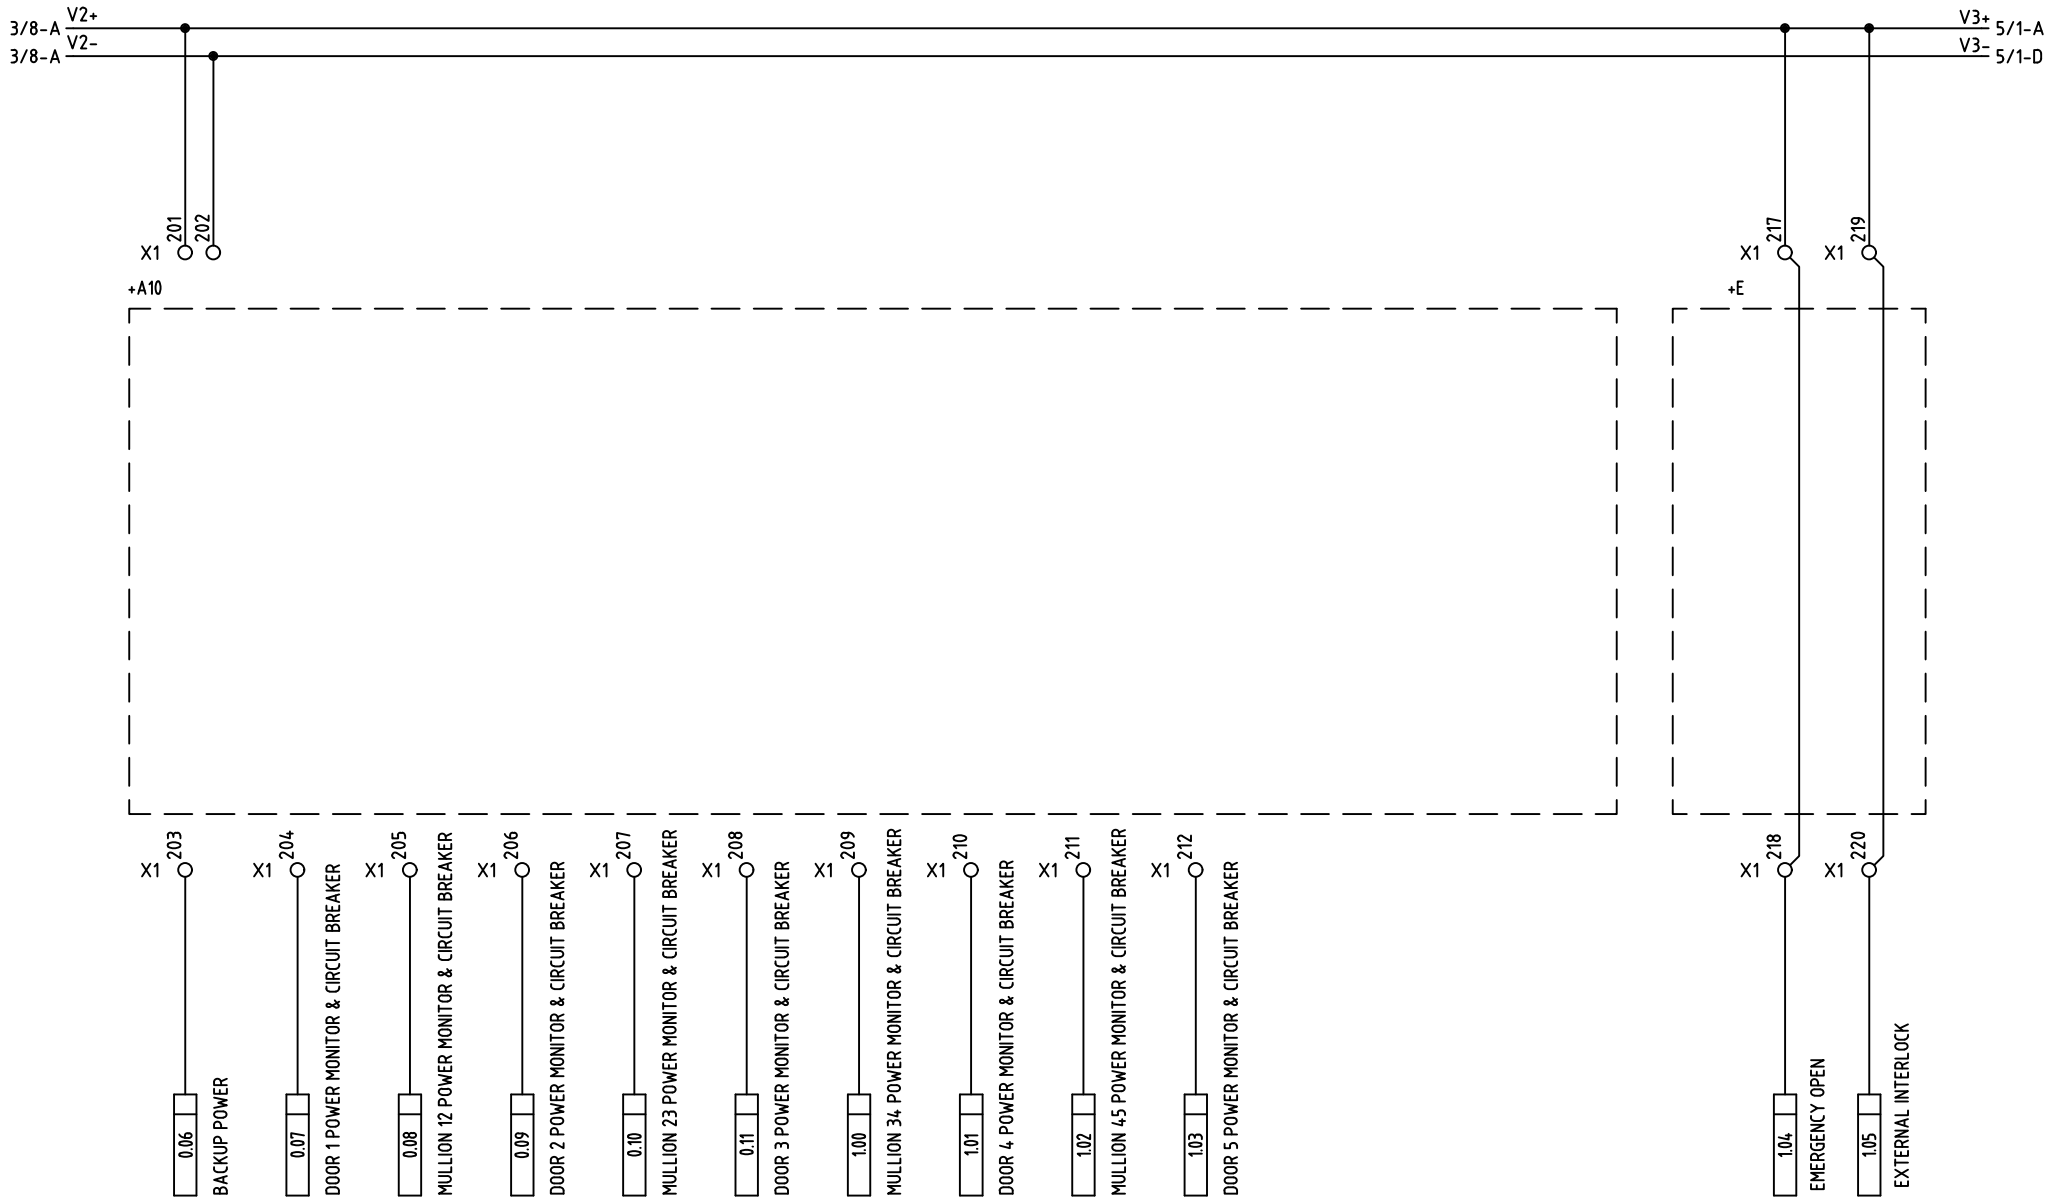

NO WIRE LABEL -> DBU0,75

ASSA ABLOY

Property of ASSA ABLOY Entrance Systems AB and shall not without our written permission be copied, imparted to a third party or used for any other unauthorized purpose.

GMR Aero Technic Hyderabad

Direct drive | Single motor

Wiring diagram

Designed	Approved	Location	Code
MED	GO	+A1	84800001

Page 4/45

Date 221117

Drawing No 60109

Revision --

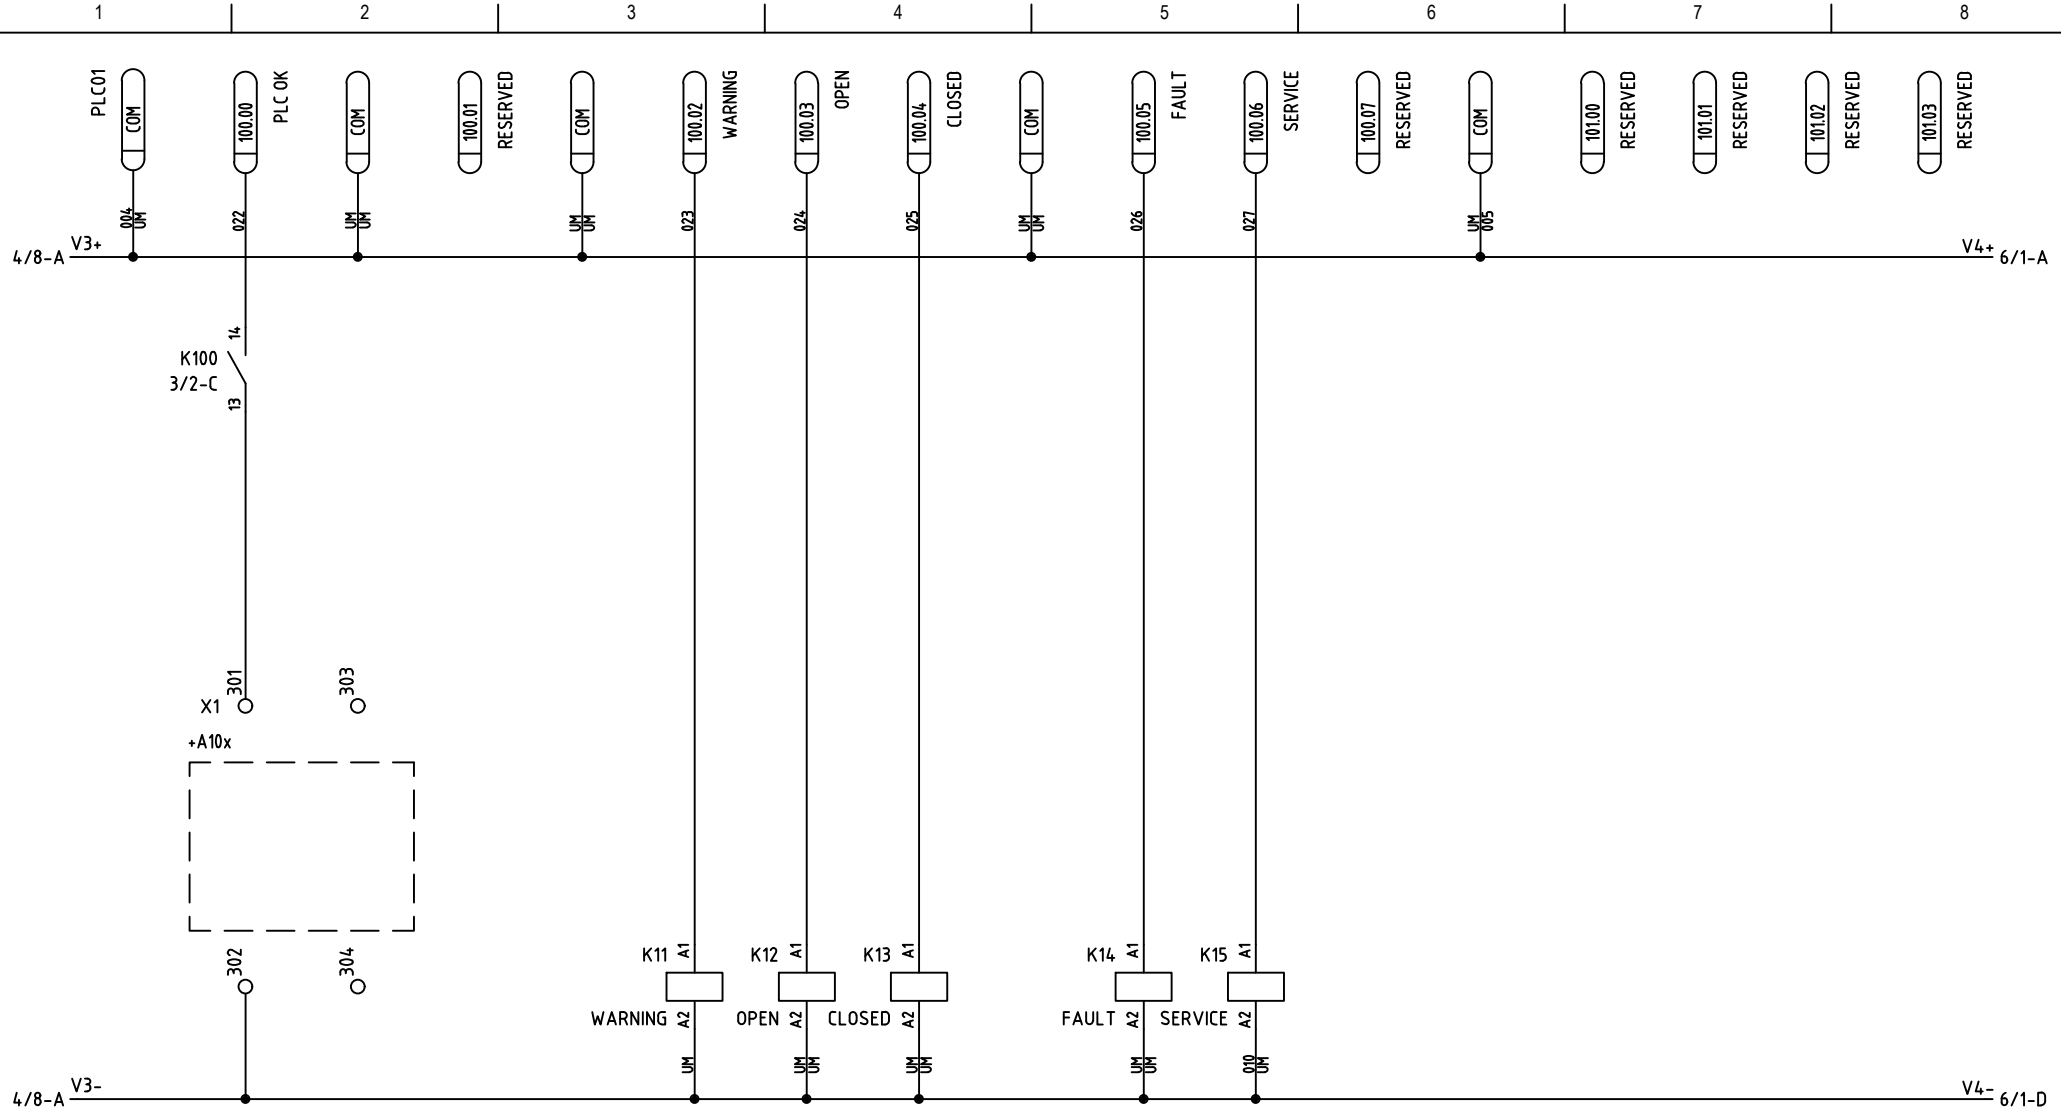

ASSA ABLOY

Property of ASSA ABLOY Entrance Systems AB and shall not without our written permission be copied, imparted to a third party or used for any other unauthorized purpose.

GMR Aero Technic Hyderabad

Direct drive | Single motor

Wiring diagram

Designed	Approved	Location	Code
MED	GO	+A1	84800001

Page	Date	Drawing No	Revision
5/45	221117	60109	--

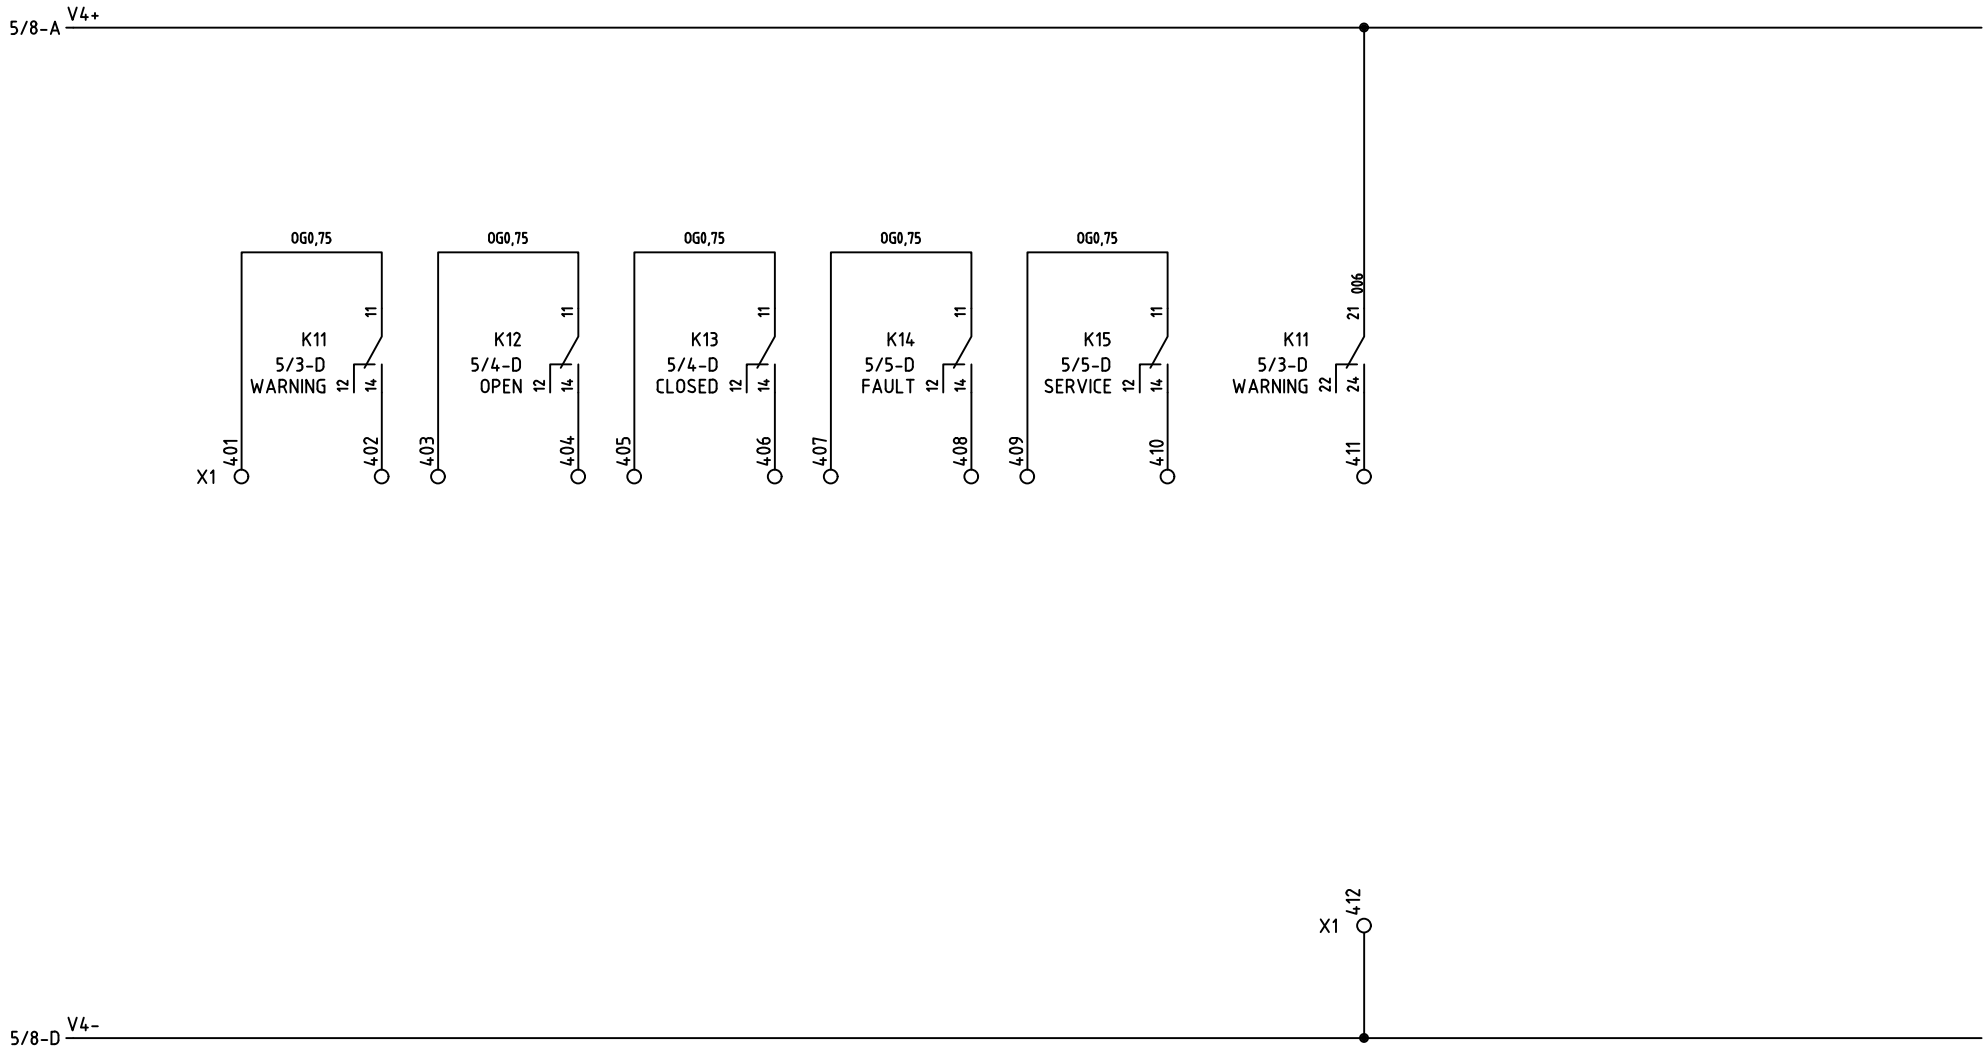

NO WIRE LABEL -> DBU0,75

ASSA ABLOY

Property of ASSA ABLOY Entrance Systems AB and shall not without our written permission be copied, imparted to a third party or used for any other unauthorized purpose.

GMR Aero Technic Hyderabad

Direct drive | Single motor

Wiring diagram

Designed	Approved	Location	Code
MED	GO	+A1	84800001

Page	Date	Drawing No	Revision
6/45	221117	60109	--

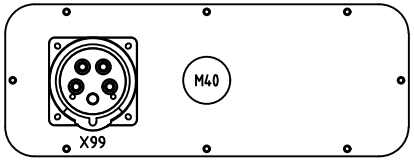

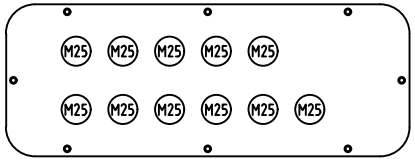

 

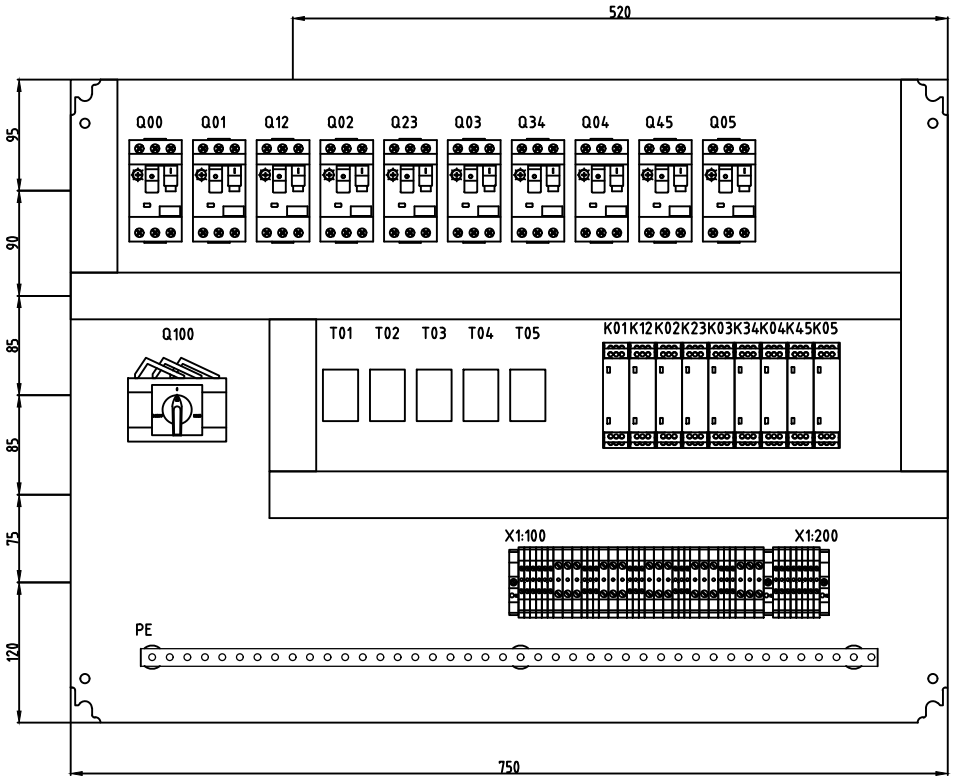

ASSA ABLOY

Property of ASSA ABLOY Entrance Systems AB and shall not without our written permission be copied, imparted to a third party or used for any other unauthorized purpose.

GMR Aero Technic Hyderabad

Direct drive | Single motor

Panel layout

Designed	Approved	Location	Code
MED	GO	+A10	84800001

Page	Date	Drawing No	Revision
7 / 45	221117	60109	--

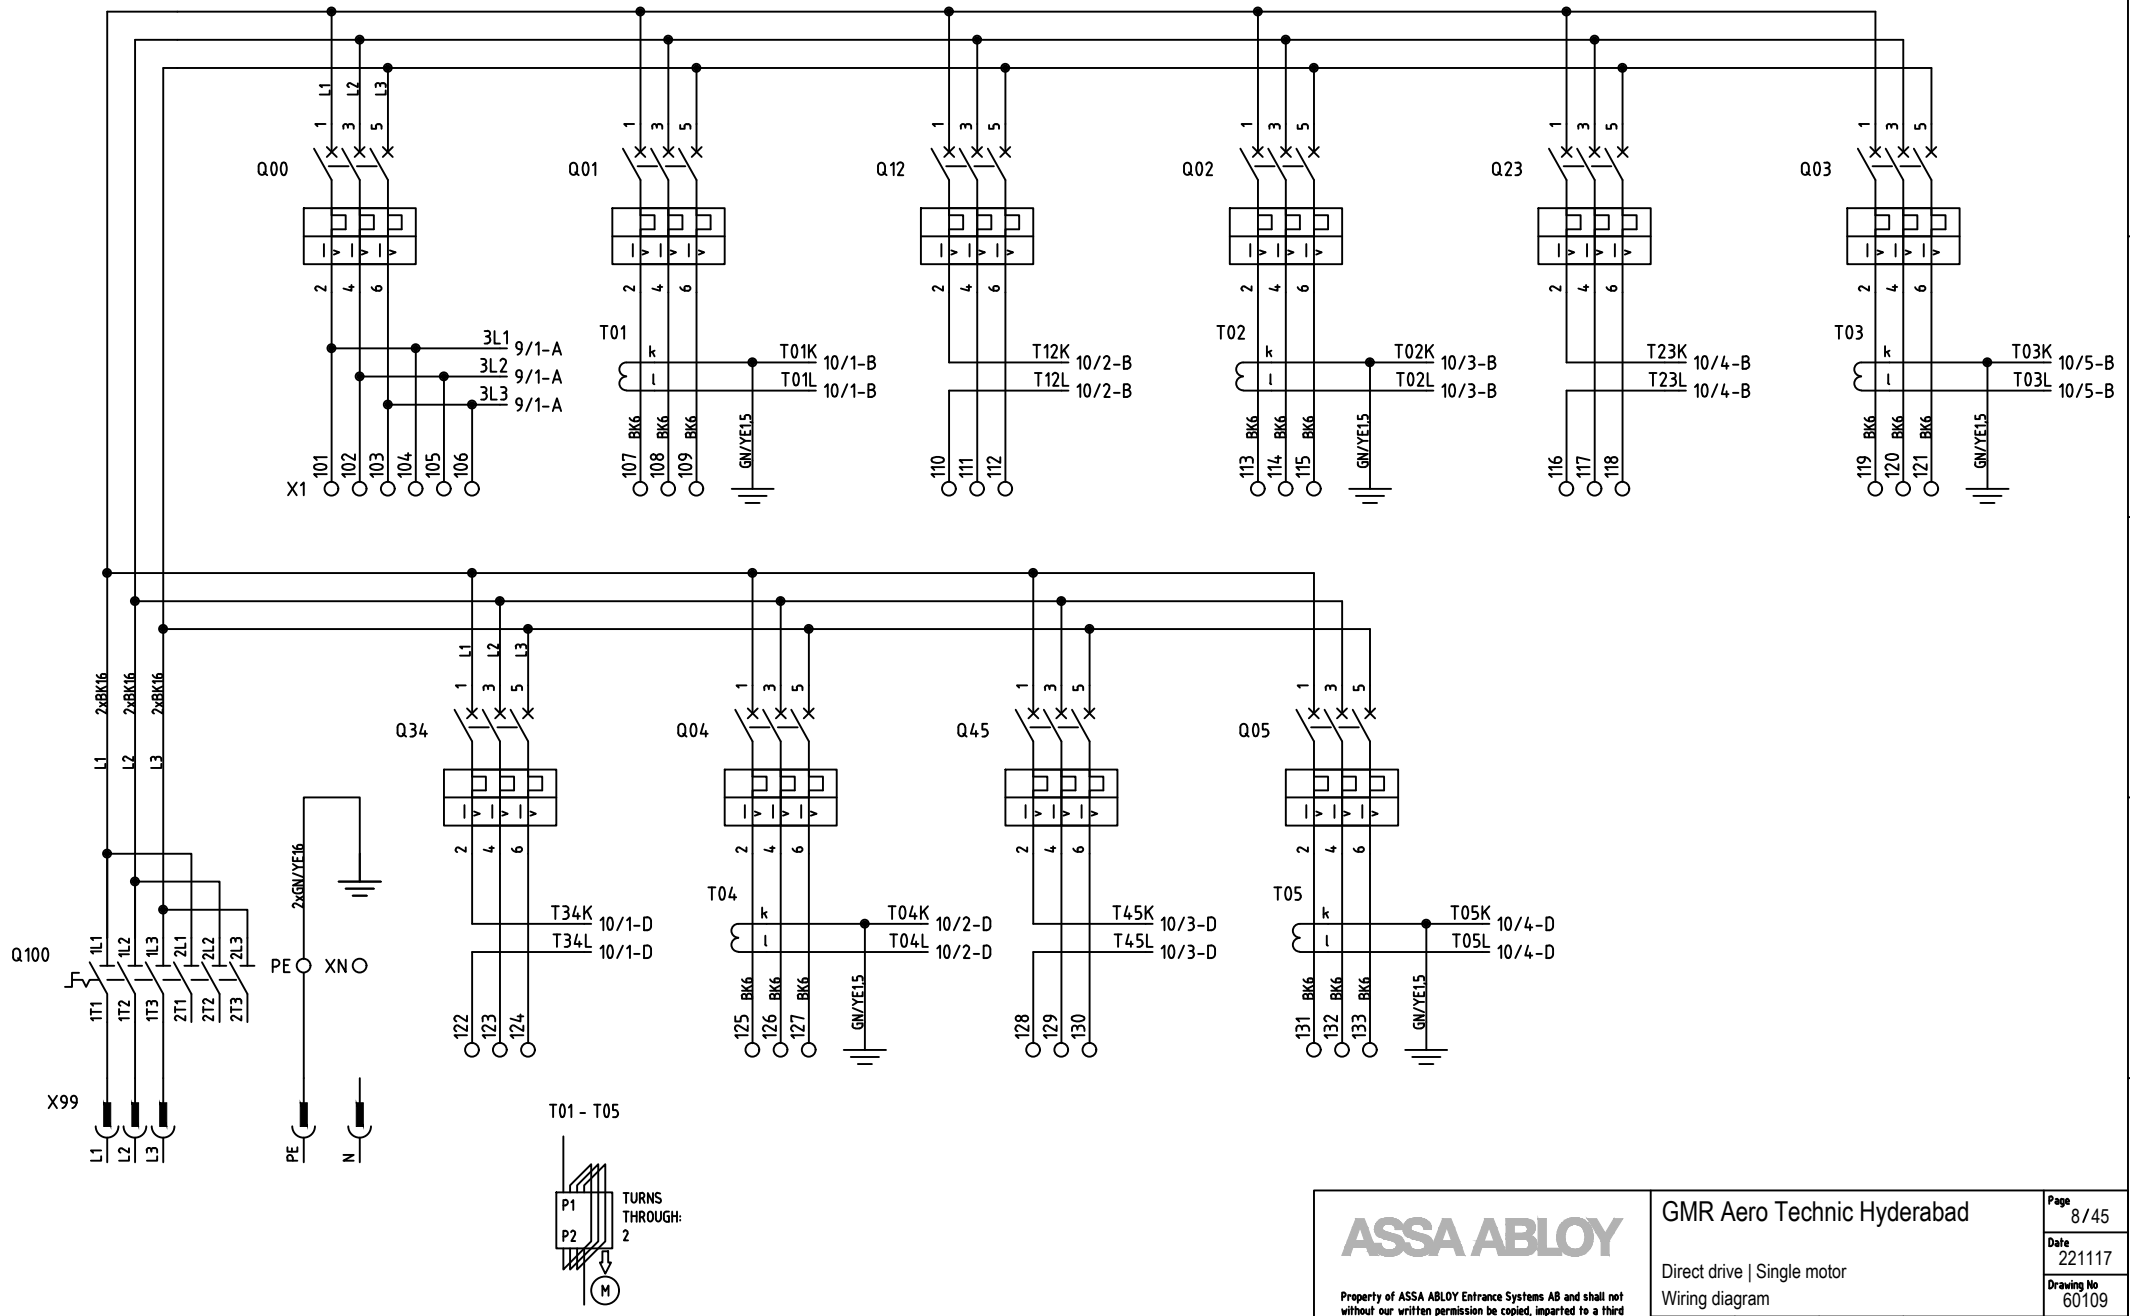

ASSA ABLOY

Property of ASSA ABLOY Entrance Systems AB and shall not without our written permission be copied, imparted to a third party or used for any other unauthorized purpose.

GMR Aero Technic Hyderabad

Direct drive | Single motor

Wiring diagram

Designed	Approved	Location	Code	Page	Date	Drawing No	Revision
MED	GO	+A10	84800001	8/45	221117	60109	--

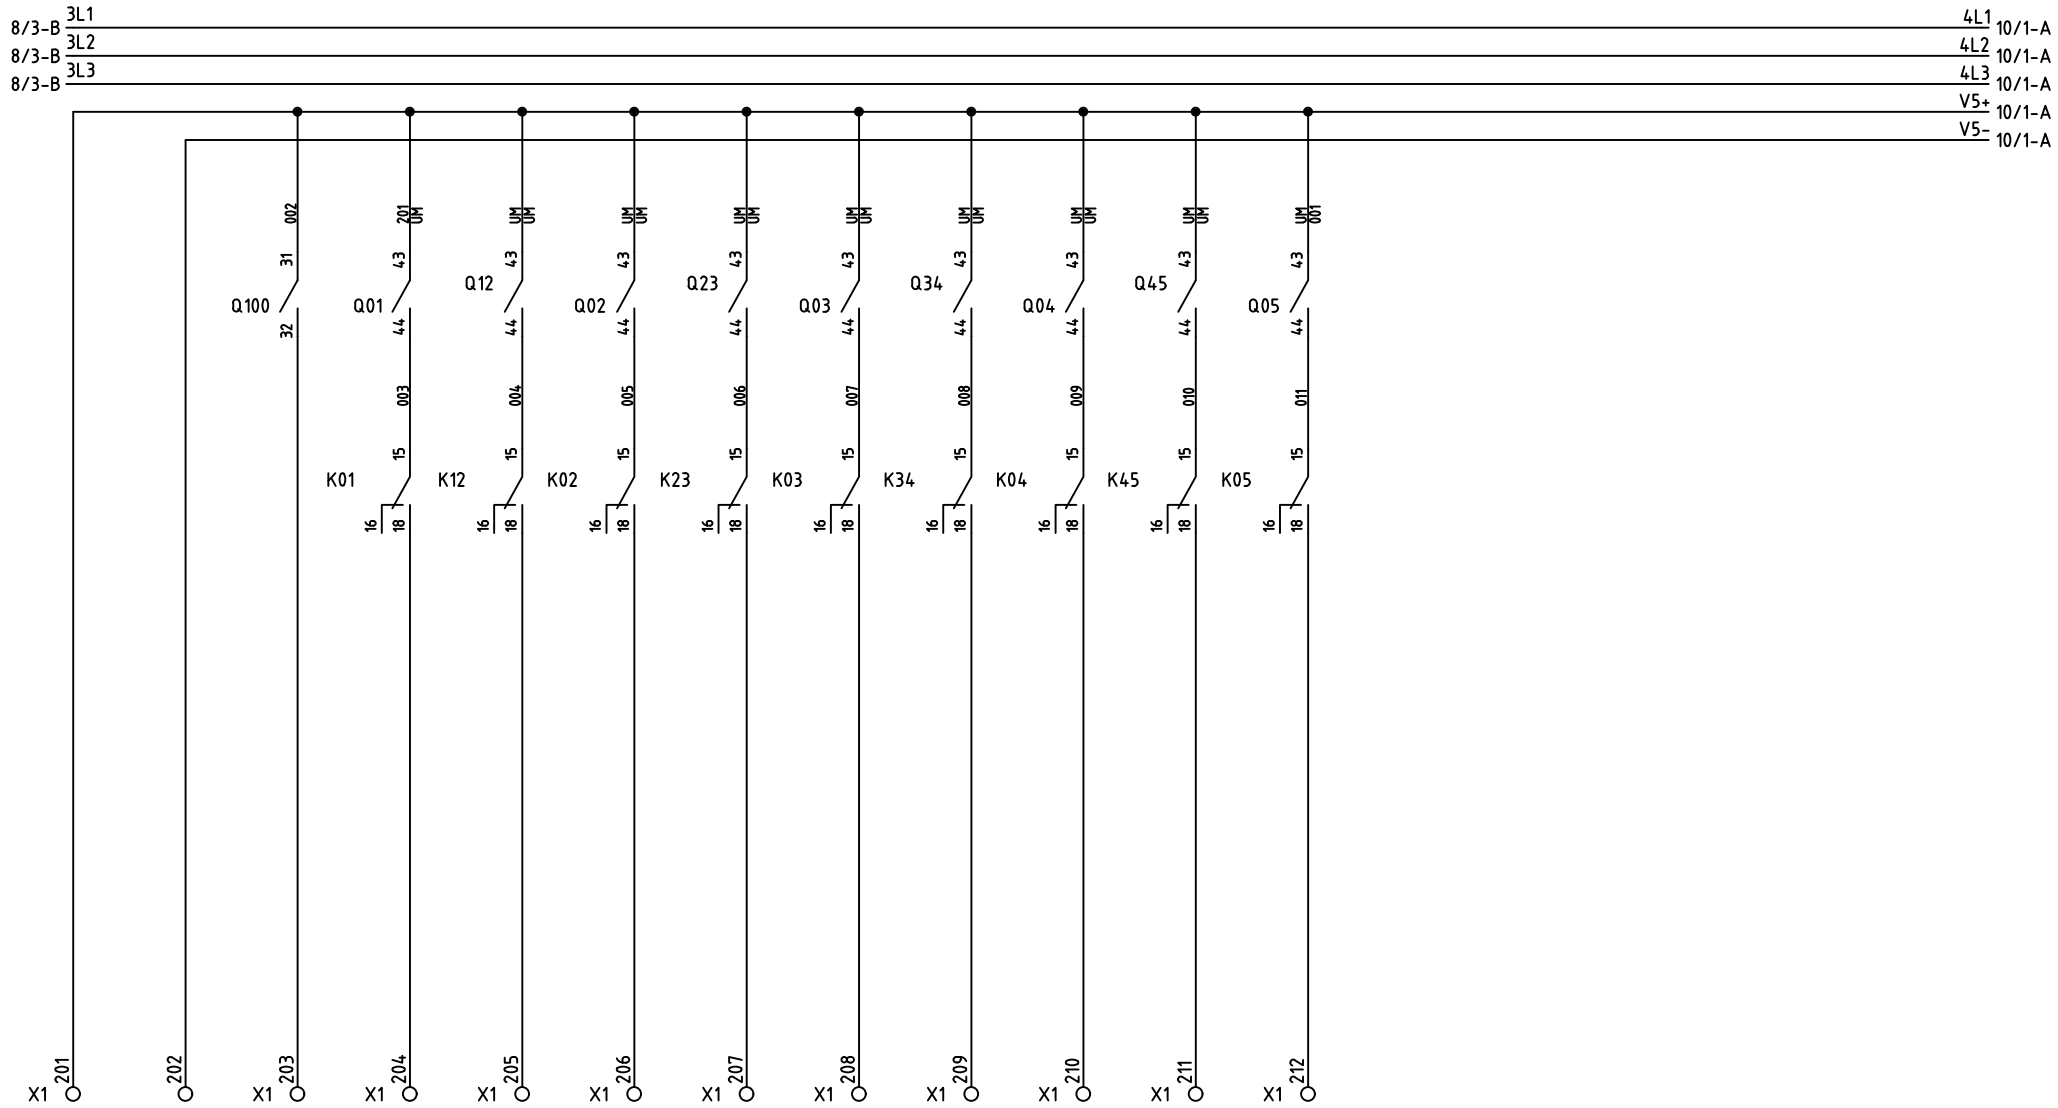

NO WIRE LABEL -> DBU0,75

ASSA ABLOY

Property of ASSA ABLOY Entrance Systems AB and shall not without our written permission be copied, imparted to a third party or used for any other unauthorized purpose.

GMR Aero Technic Hyderabad

Direct drive | Single motor

Wiring diagram

Designed	Approved	Location	Code
MED	GO	+A10	84800001

Page 9/45

Date 221117

Drawing No 60109

Revision --

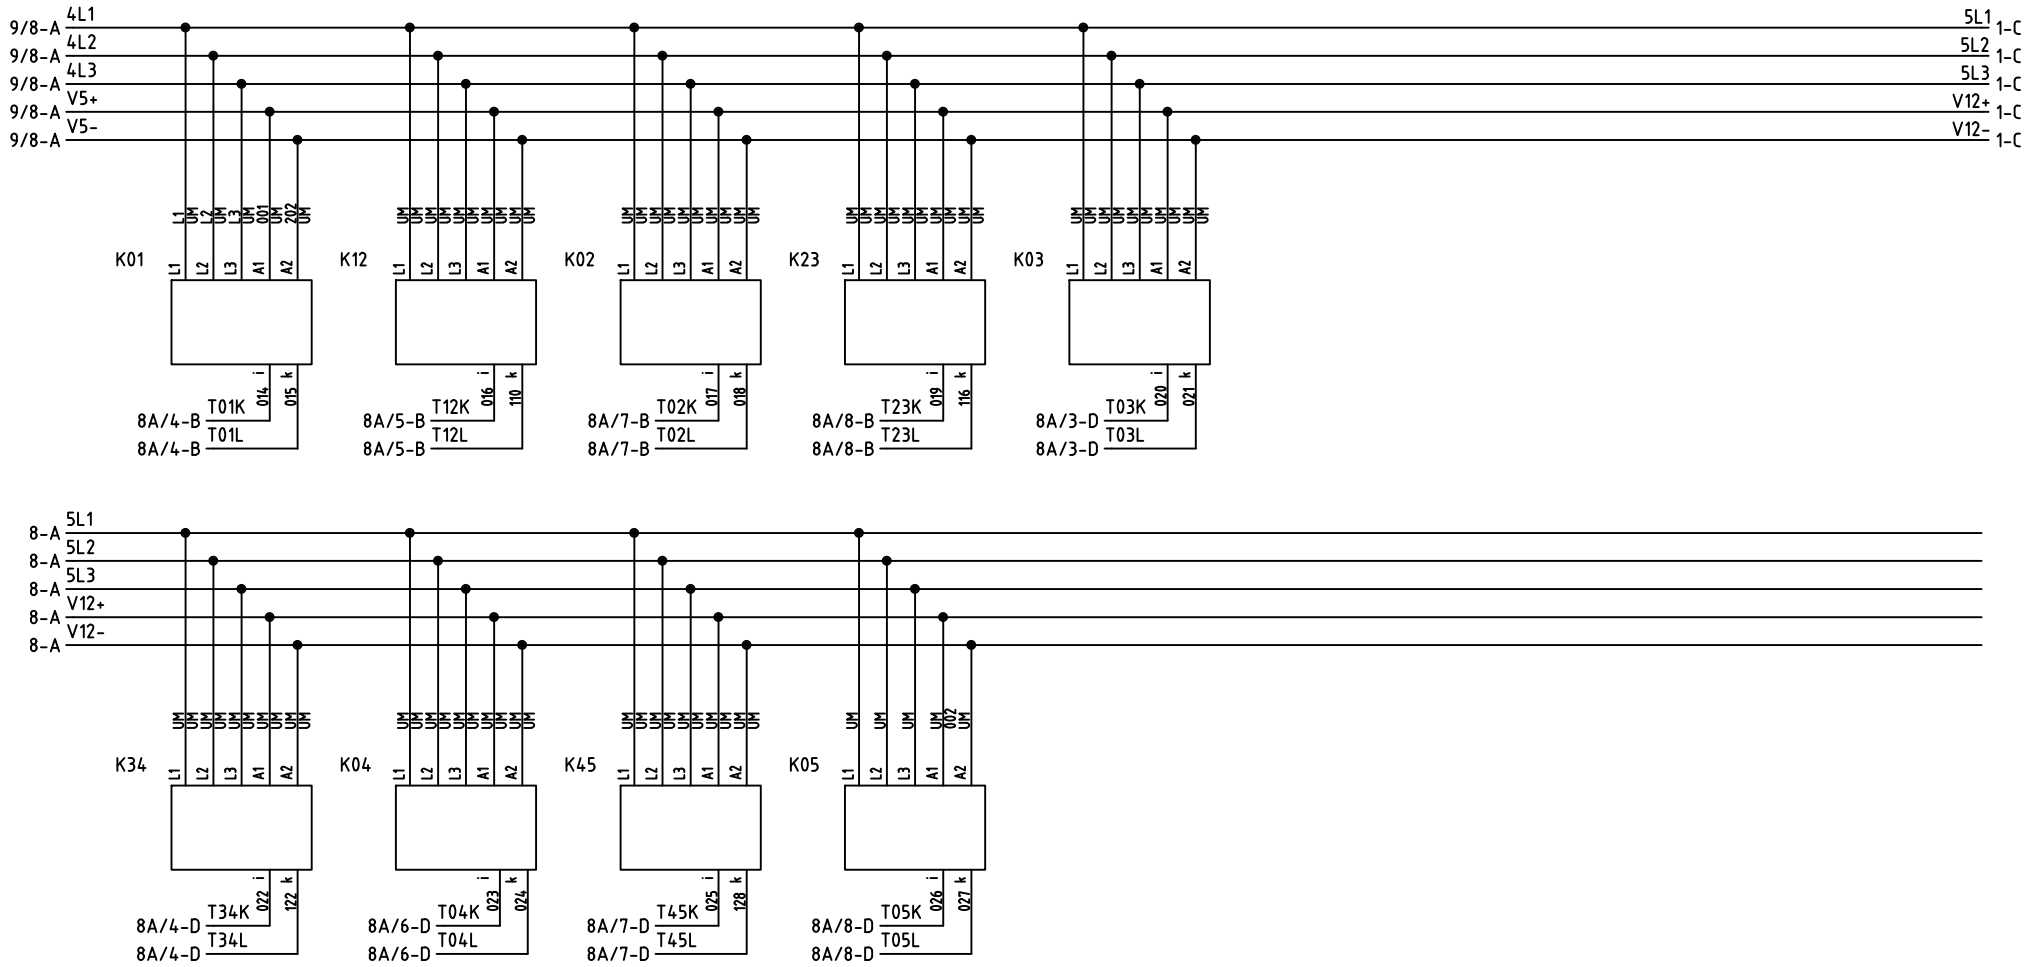

K01 - K05

TELE
START: .2-.5 s
POWER: 30 %
DELAY: 0.1 s
RANGE: 1 kW
FUNCTION: O+/I<

K12 - K45

TELE
START: .2-.5 s
POWER: 70 %
DELAY: 0.1 s
RANGE: 4 kW
FUNCTION: O+/I<

Power monitor RANGE & POWER settings must be individually adjusted to suit real conditions. Please refer to installation manual.

NO WIRE LABEL -> DBU0,75

Property of ASSA ABLOY Entrance Systems AB and shall not without our written permission be copied, imparted to a third party or used for any other unauthorized purpose.

ASSA ABLOY

GMR Aero Technic Hyderabad

Direct drive | Single motor

Wiring diagram

Page	Date	Drawing No
10/45	221117	60109

Designed	Approved	Location	Code	Revision
MED	GO	+A10	84800001	--

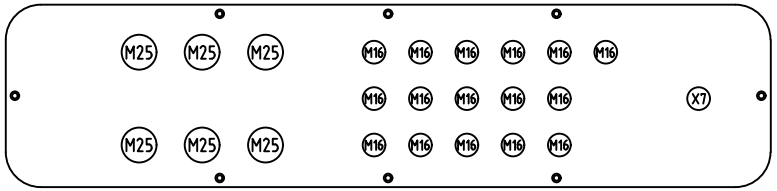

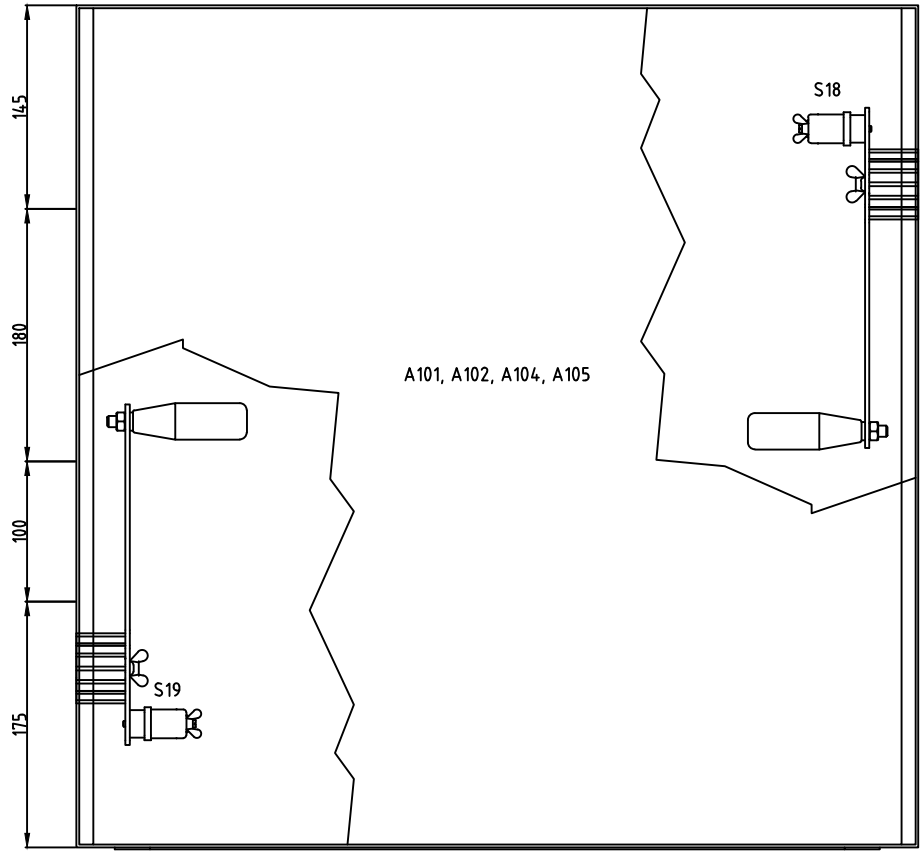

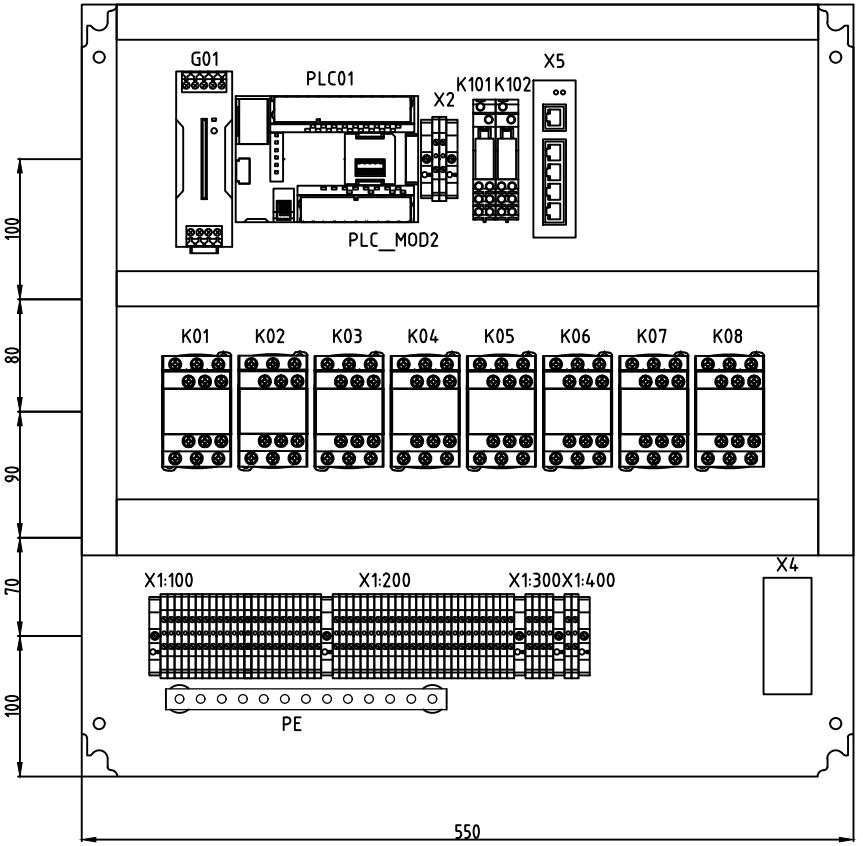

ASSA ABLOY

Property of ASSA ABLOY Entrance Systems AB and shall not without our written permission be copied, imparted to a third party or used for any other unauthorized purpose.

GMR Aero Technic Hyderabad

Applicable to A101, A102, A104, A105

Direct drive | Single motor

Panel layout

Designed	Approved	Location	Code	Revision
MED	GO		84800001	--

Page 11/45

Date 221117

Drawing No 60109

ASSA ABLOY

Property of ASSA ABLOY Entrance Systems AB and shall not without our written permission be copied, imparted to a third party or used for any other unauthorized purpose.

GMR Aero Technic Hyderabad

Applicable to A101, A102, A104, A105

Direct drive | Single motor

Wiring diagram

Designed	Approved	Location	Code	Page	Date	Drawing No	Revision
MED	GO		84800001	12/45	221117	60109	--

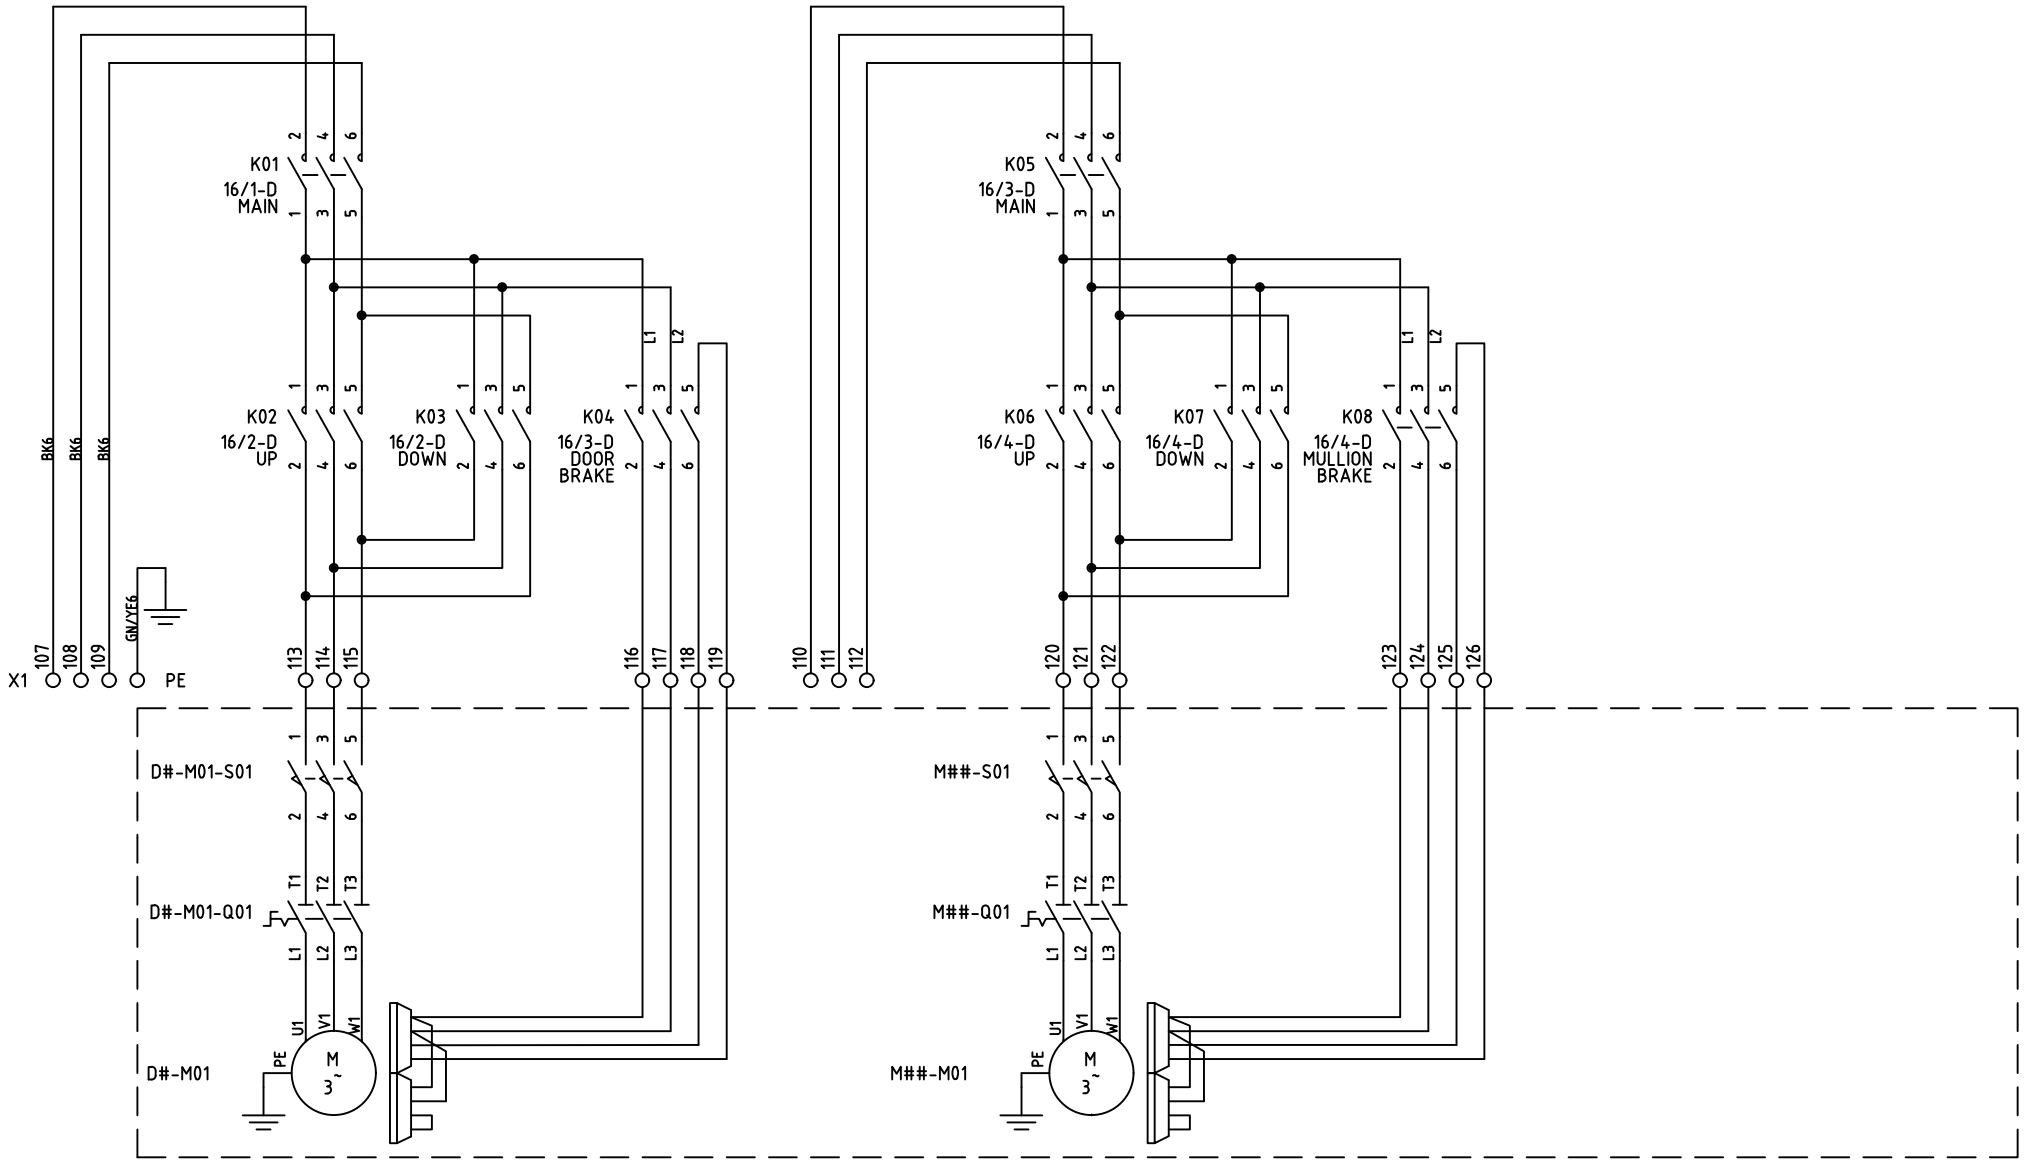

NO WIRE LABEL -> BK1,5

Property of ASSA ABLOY Entrance Systems AB and shall not without our written permission be copied, imparted to a third party or used for any other unauthorized purpose.

ASSA ABLOY

GMR Aero Technic Hyderabad

Applicable to A101, A102, A104, A105

Direct drive | Single motor

Wiring diagram

Designed	Approved	Location	Code	Page	Date	Drawing No	Revision
MED	GO		84800001	13/45	221117	60109	--

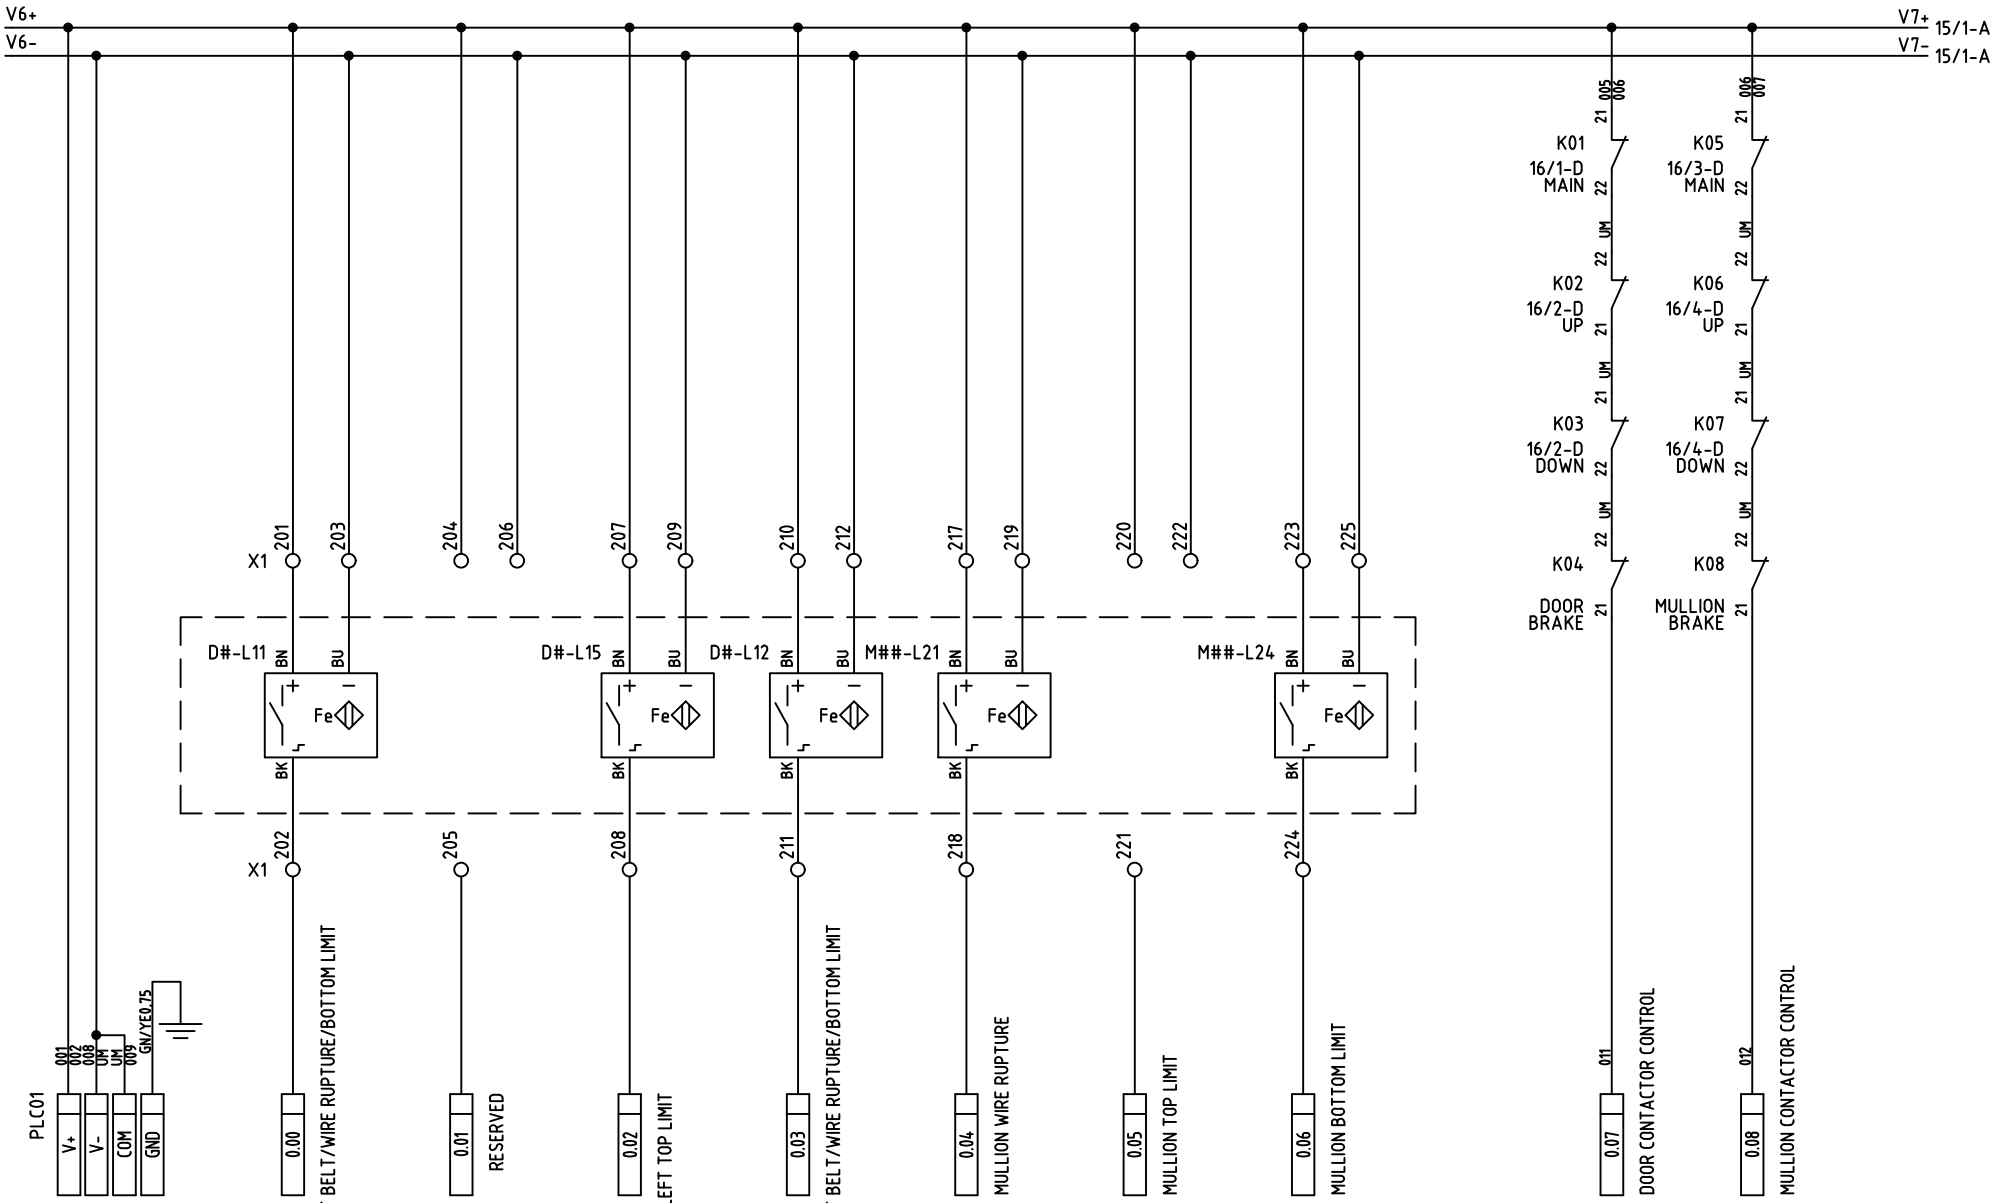

ASSA ABLOY

Property of ASSA ABLOY Entrance Systems AB and shall not without our written permission be copied, imparted to a third party or used for any other unauthorized purpose.

GMR Aero Technic Hyderabad

Applicable to A101, A102, A104, A105

Direct drive | Single motor

Wiring diagram

Designed	Approved	Location	Code	Revision
MED	GO		84800001	--

Page 14/45

Date 221117

Drawing No 60109

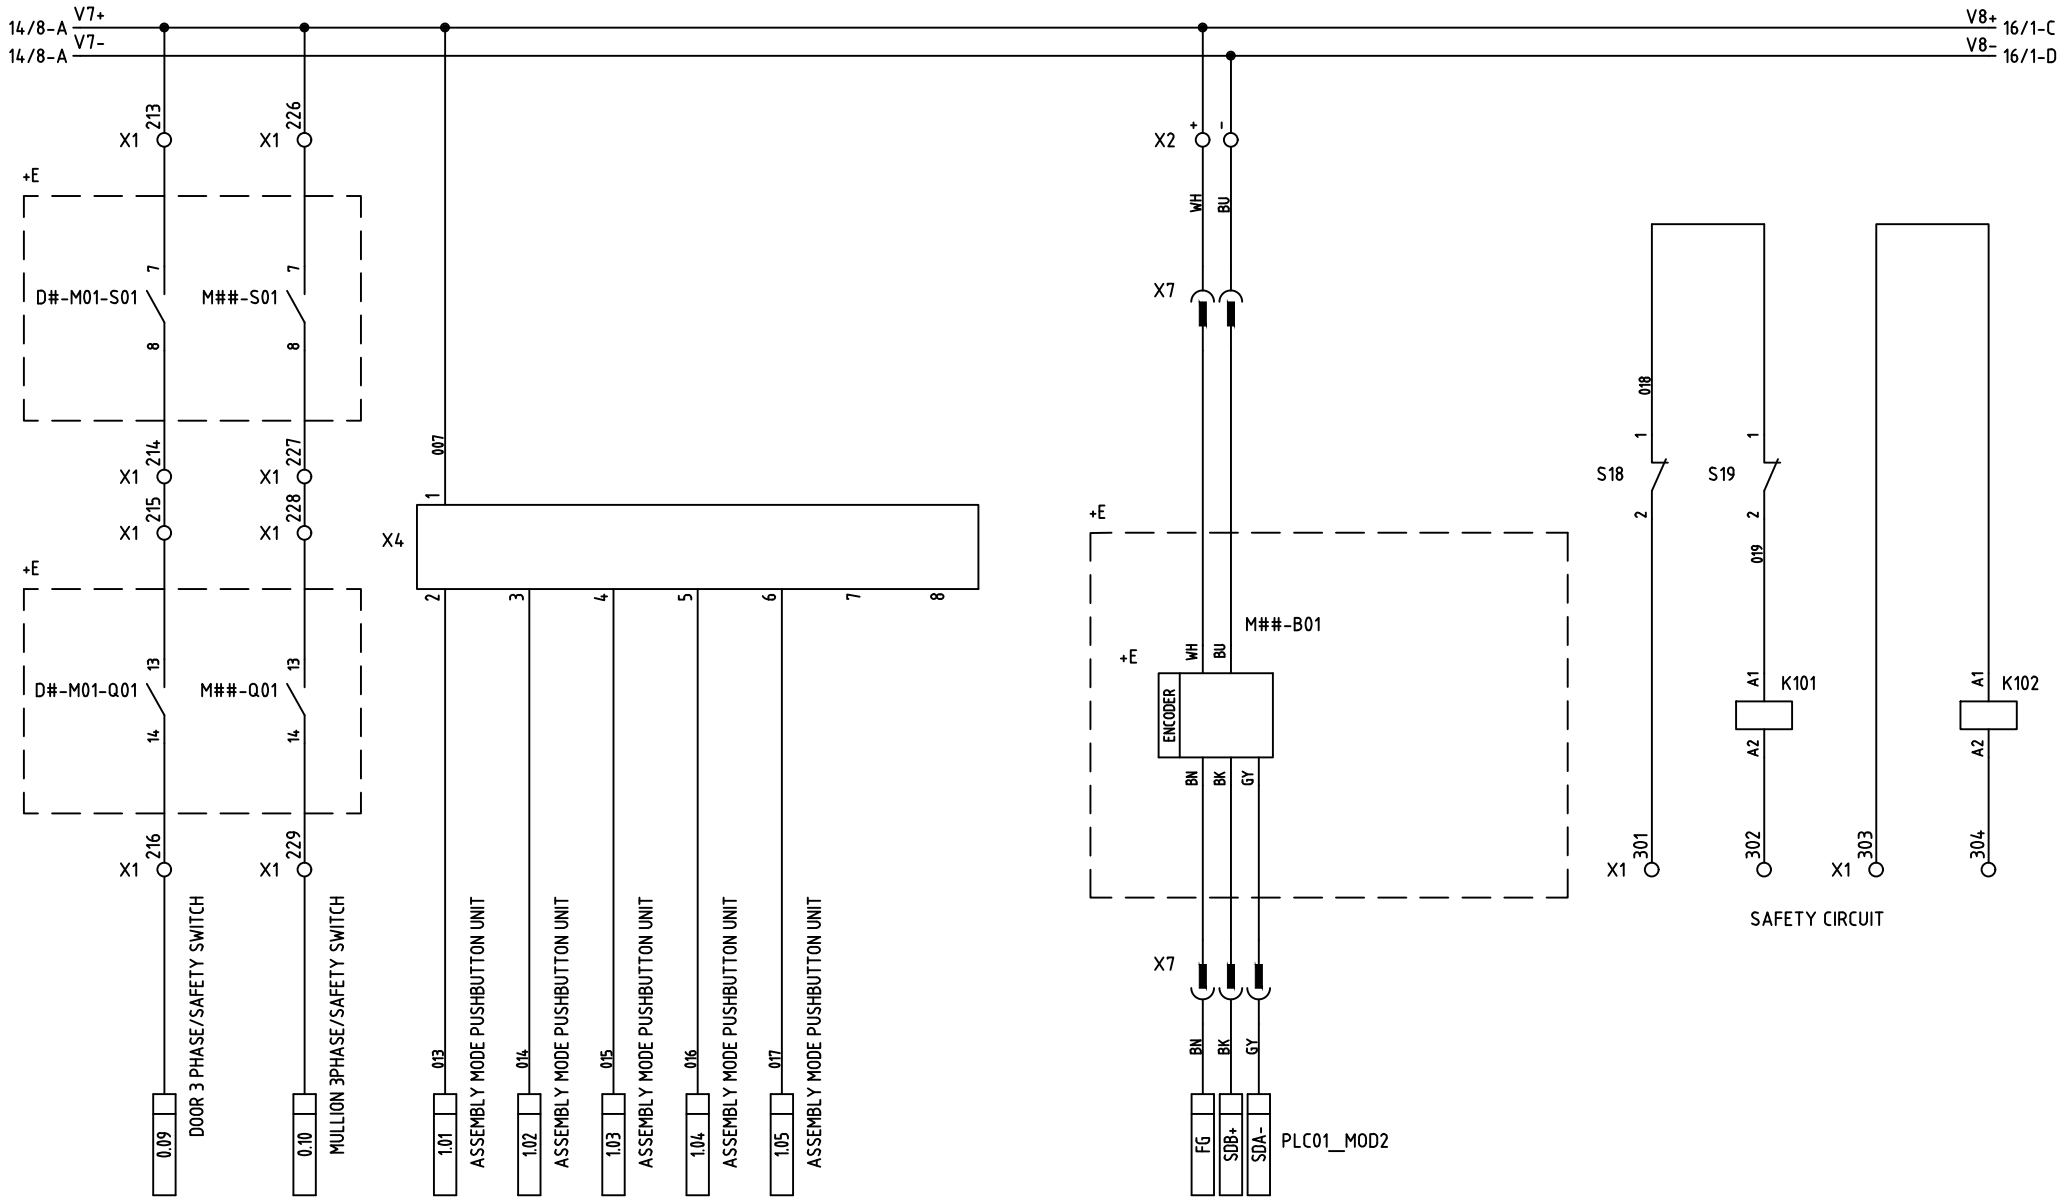

ASSA ABLOY

Property of ASSA ABLOY Entrance Systems AB and shall not without our written permission be copied, imparted to a third party or used for any other unauthorized purpose.

GMR Aero Technic Hyderabad

Applicable to A101, A102, A104, A105

Direct drive | Single motor

Wiring diagram

Designed	Approved	Location	Code	Revision
MED	GO		84800001	--

Page 15/45

Date 221117

Drawing No 60109

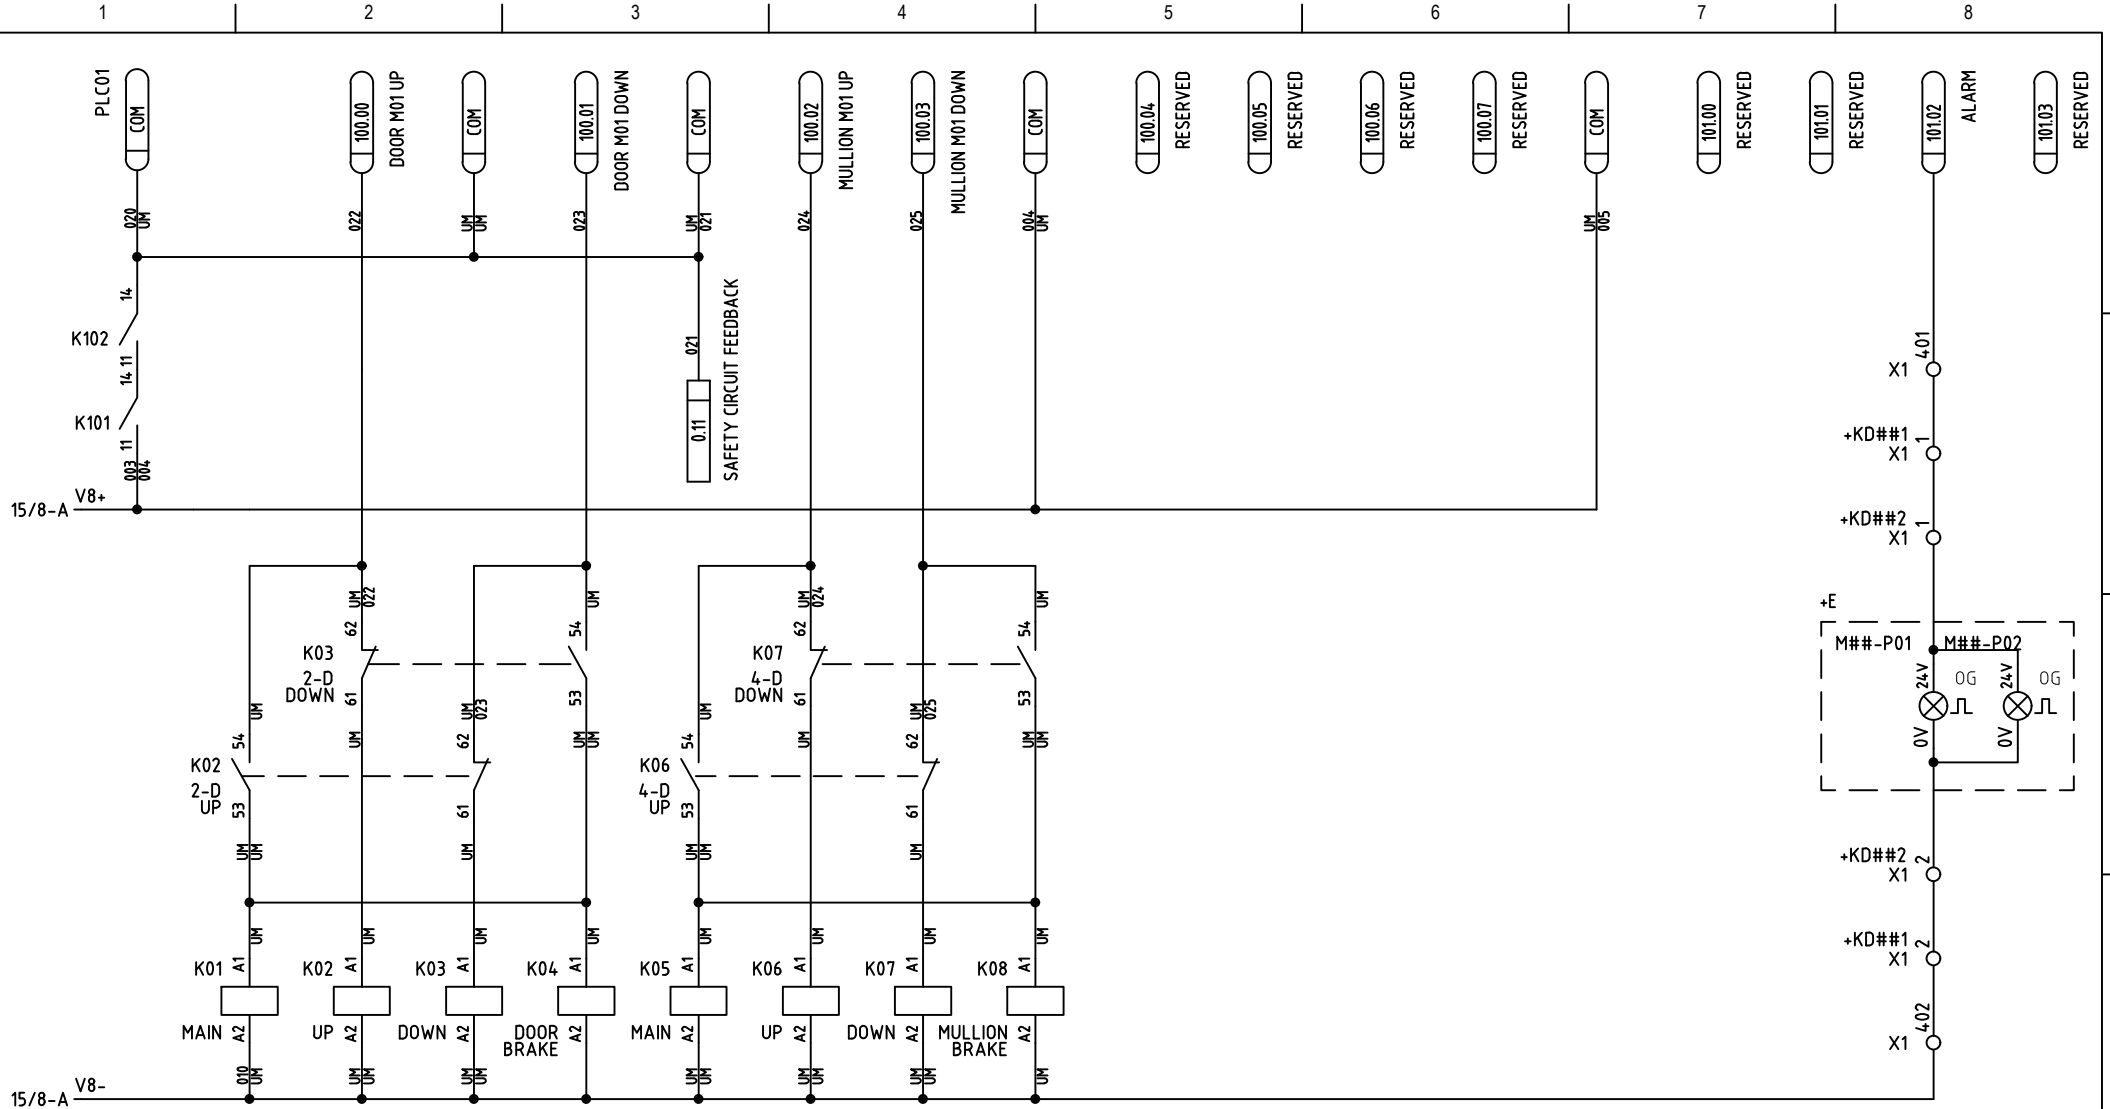

NO WIRE LABEL -> DBU0,75

Property of ASSA ABLOY Entrance Systems AB and shall not without our written permission be copied, imparted to a third party or used for any other unauthorized purpose.

ASSA ABLOY

GMR Aero Technic Hyderabad

Applicable to A101, A102, A104, A105

Direct drive | Single motor

Wiring diagram

Designed	Approved	Location	Code	Page	Date	Drawing No	Revision
MED	GO		84800001	16/45	221117	60109	--

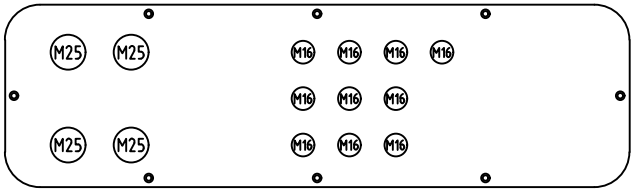

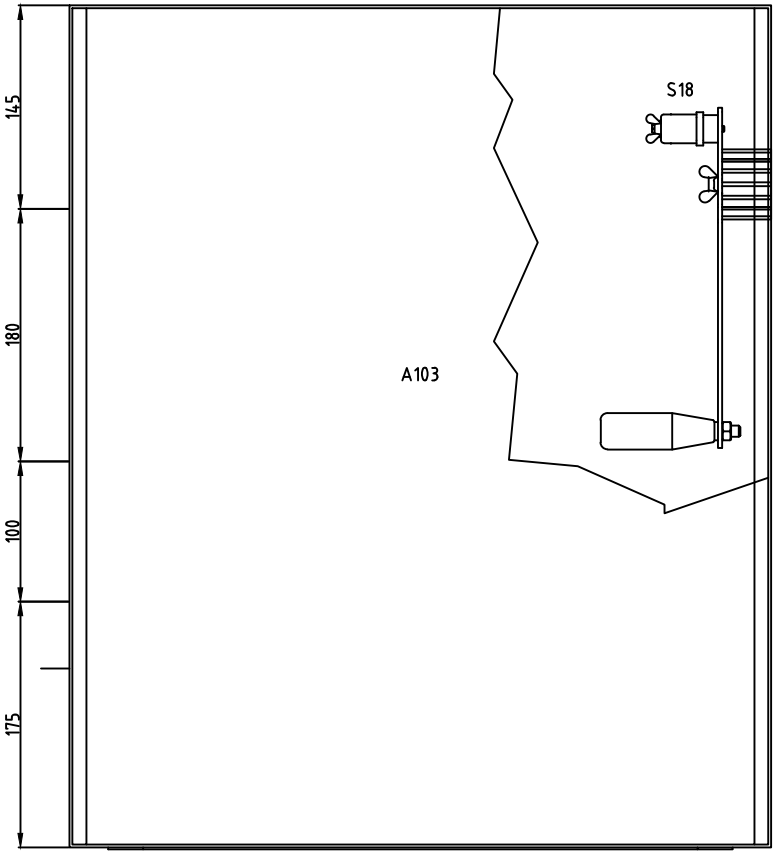

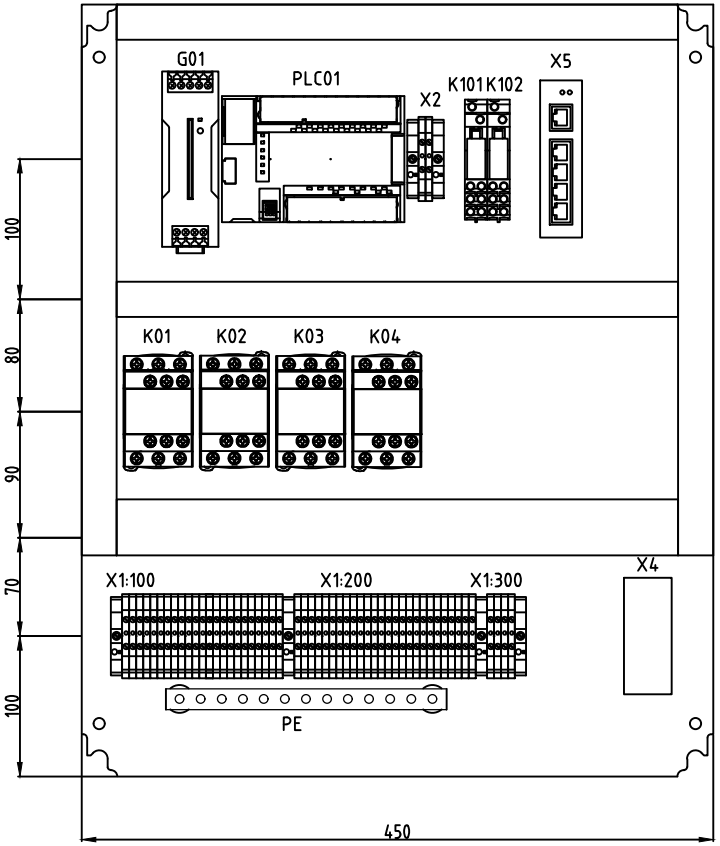

ASSA ABLOY

Property of ASSA ABLOY Entrance Systems AB and shall not without our written permission be copied, imparted to a third party or used for any other unauthorized purpose.

GMR Aero Technic Hyderabad

Direct drive | Single motor

Panel layout

Designed	Approved	Location	Code	Revision
MED	GO		84800001	--

Page 17/45

Date 221117

Drawing No 60109

ASSA ABLOY

Property of ASSA ABLOY Entrance Systems AB and shall not without our written permission be copied, imparted to a third party or used for any other unauthorized purpose.

GMR Aero Technic Hyderabad

Direct drive | Single motor

Wiring diagram

Designed	Approved	Location	Code	Page	Date	Drawing No	Revision
MED	GO		84800001	18/45	221117	60109	--

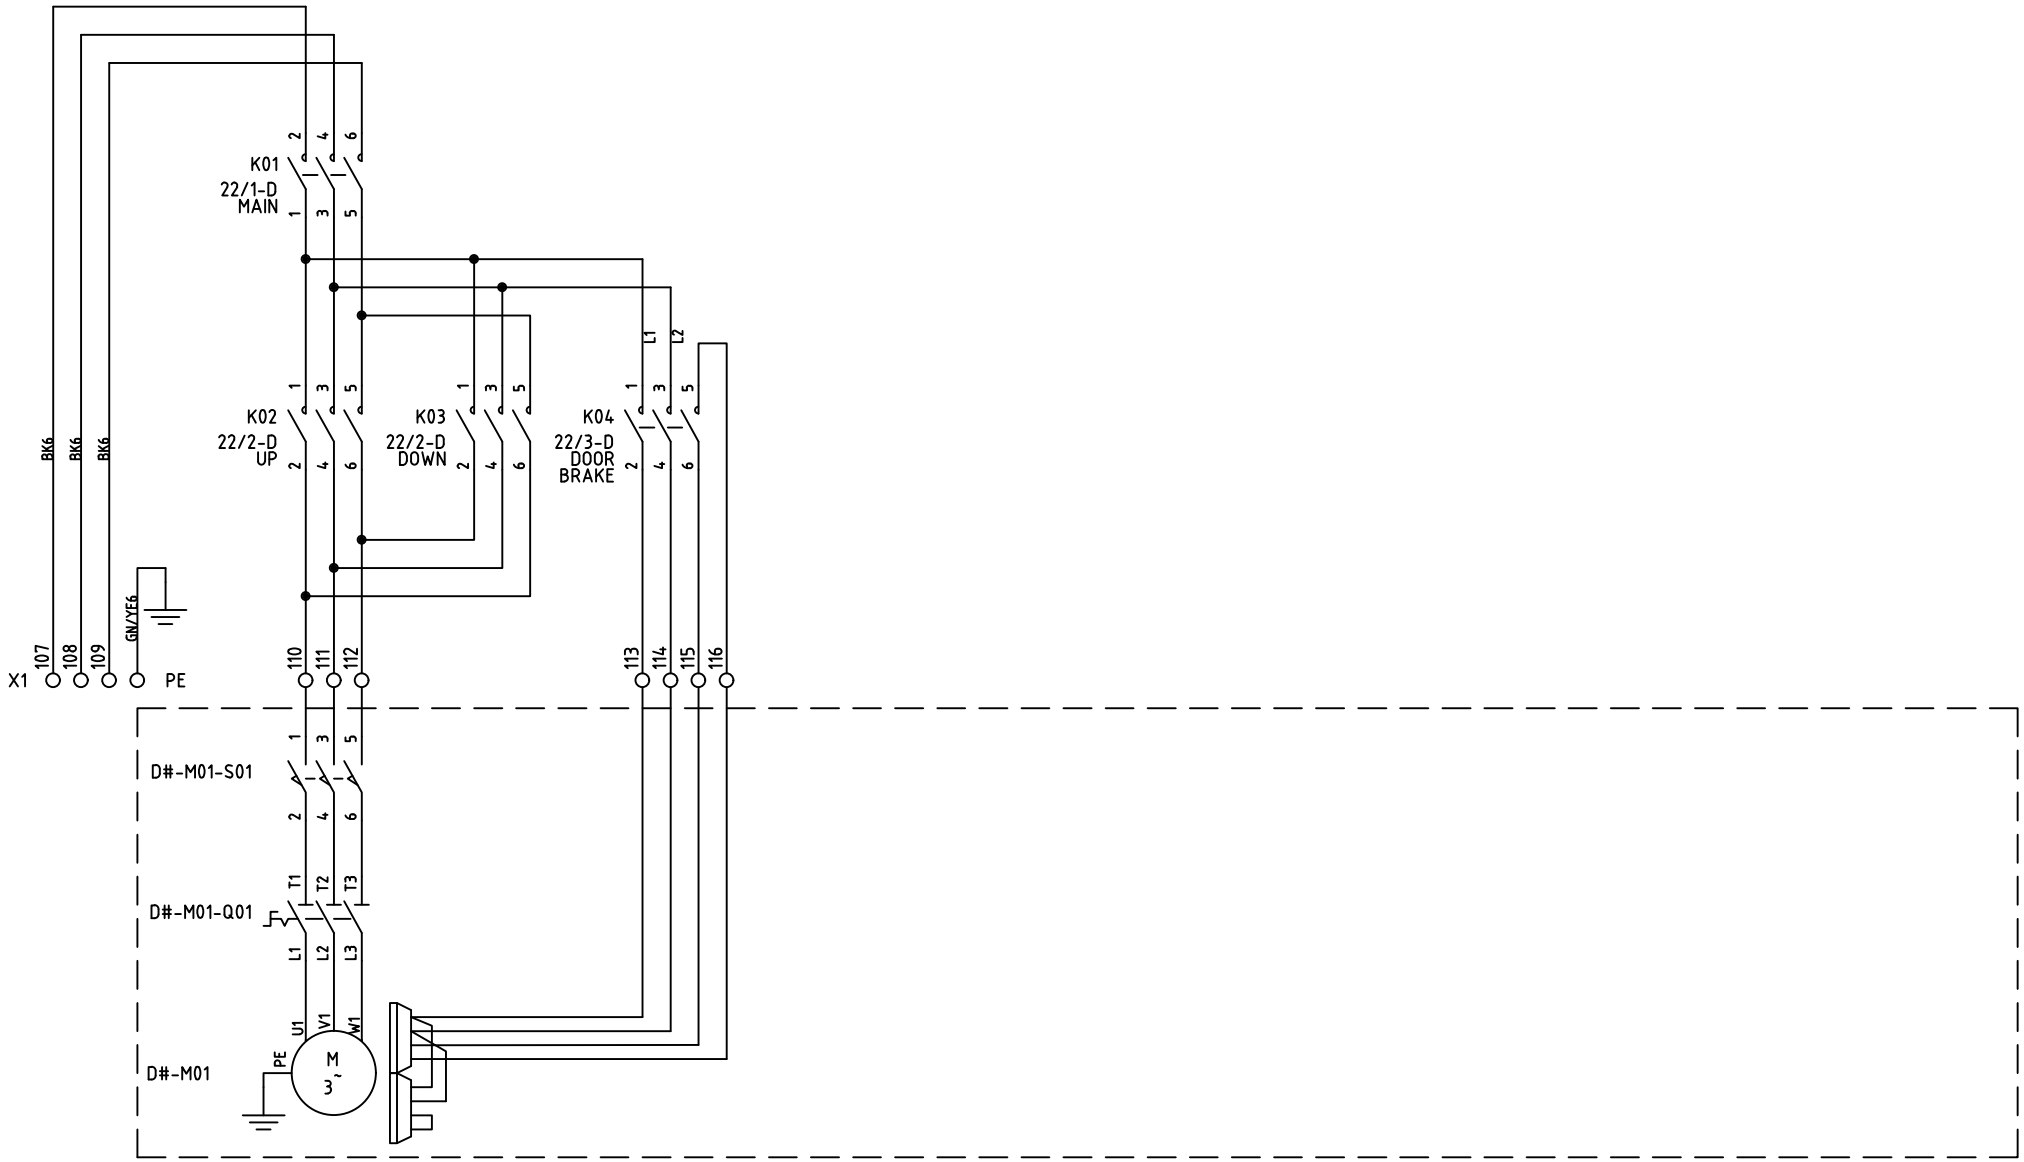

NO WIRE LABEL -> BK1,5

Property of ASSA ABLOY Entrance Systems AB and shall not without our written permission be copied, imparted to a third party or used for any other unauthorized purpose.

ASSA ABLOY

GMR Aero Technic Hyderabad

Direct drive | Single motor

Wiring diagram

Designed	Approved	Location	Code	Page	Date	Drawing No	Revision
MED	GO		84800001	19/45	221117	60109	--

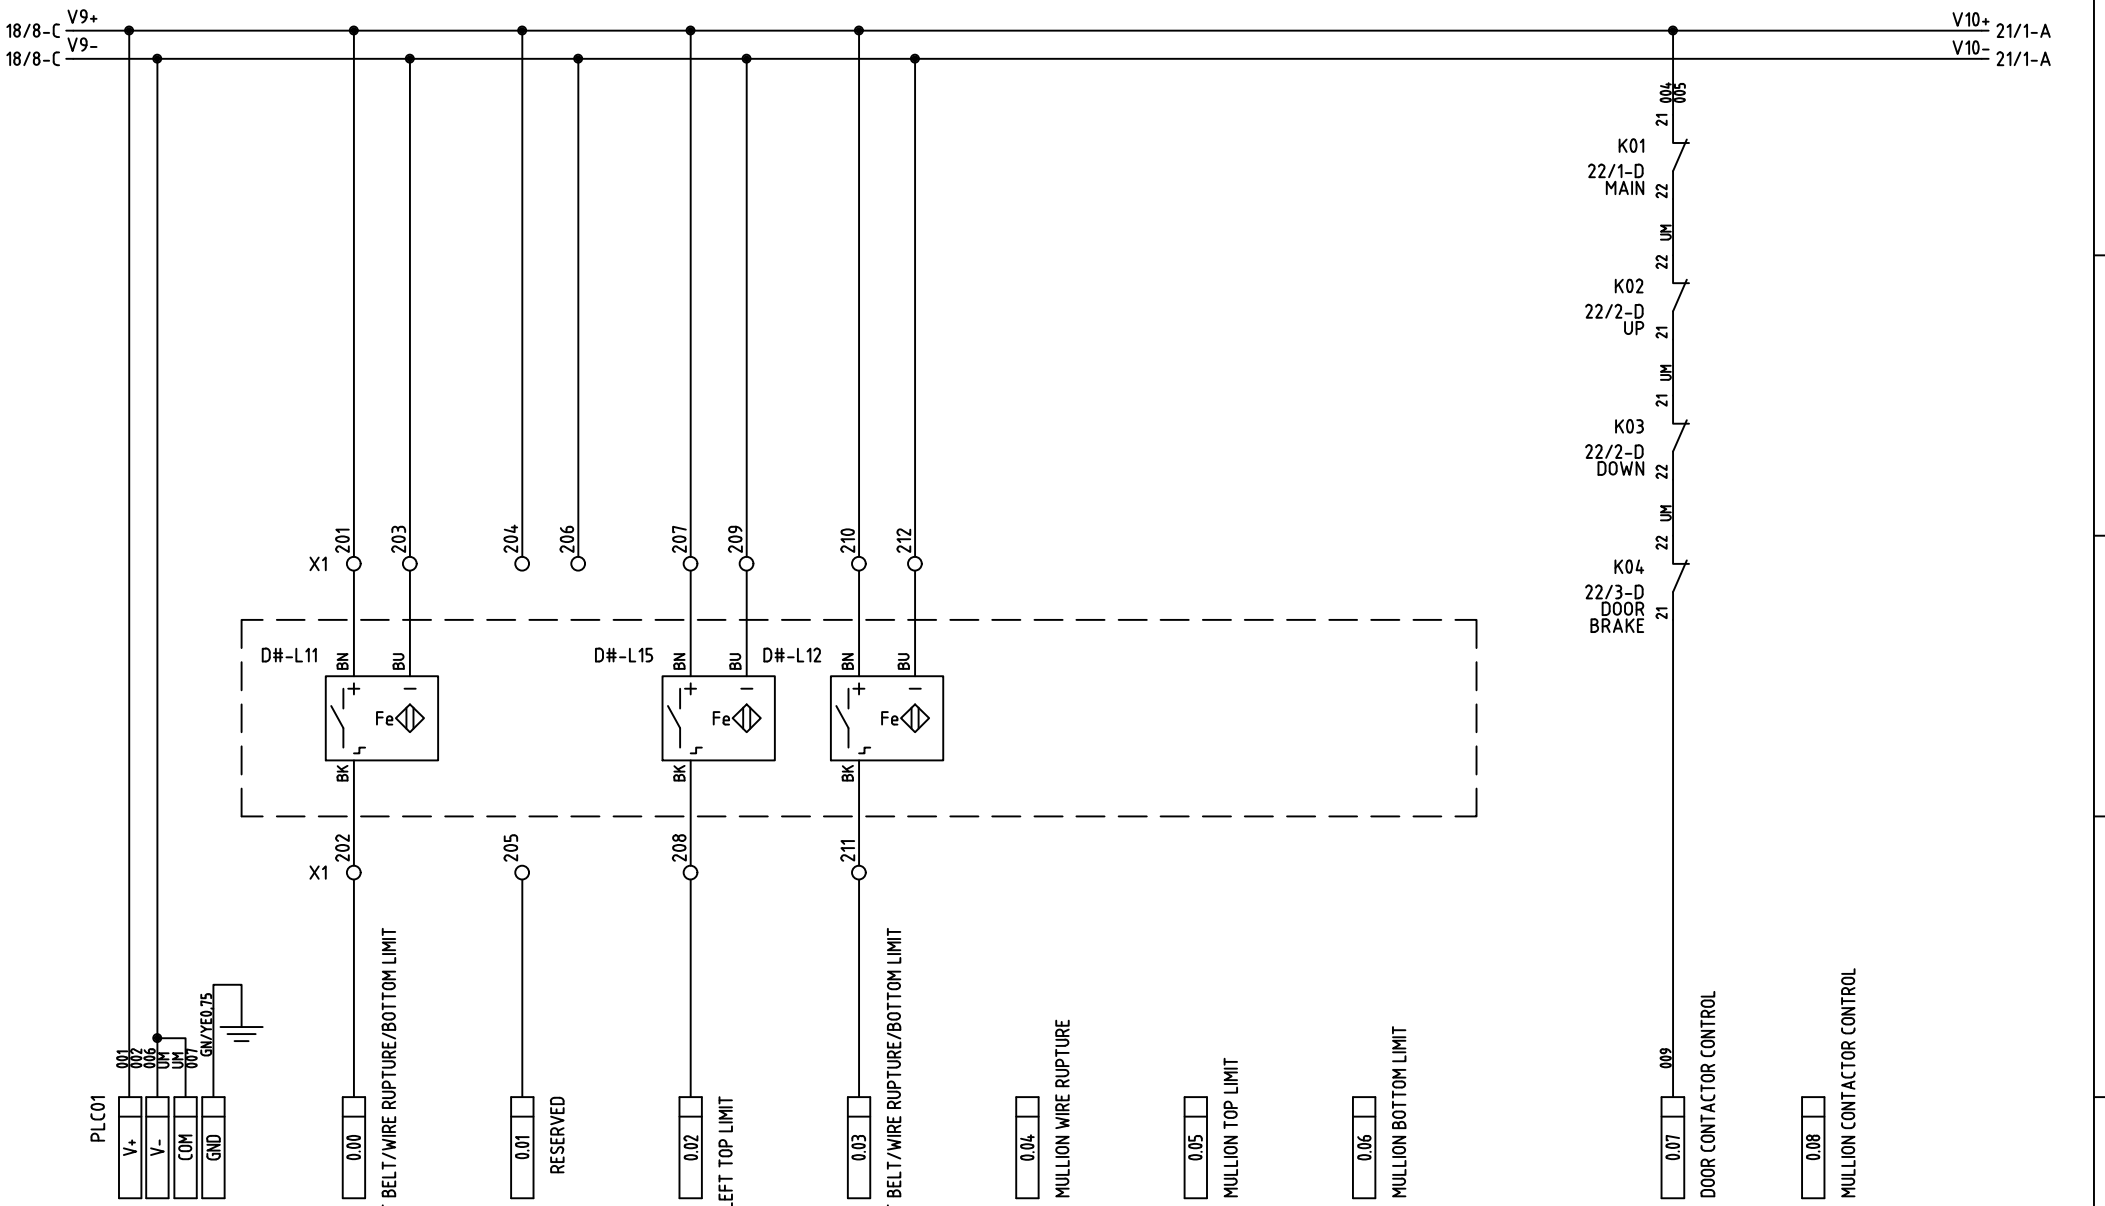

ASSA ABLOY

Property of ASSA ABLOY Entrance Systems AB and shall not without our written permission be copied, imparted to a third party or used for any other unauthorized purpose.

GMR Aero Technic Hyderabad

Direct drive | Single motor

Wiring diagram

Designed	Approved	Location	Code	Page	Date	Drawing No	Revision
MED	GO		84800001	20/45	221117	60109	--

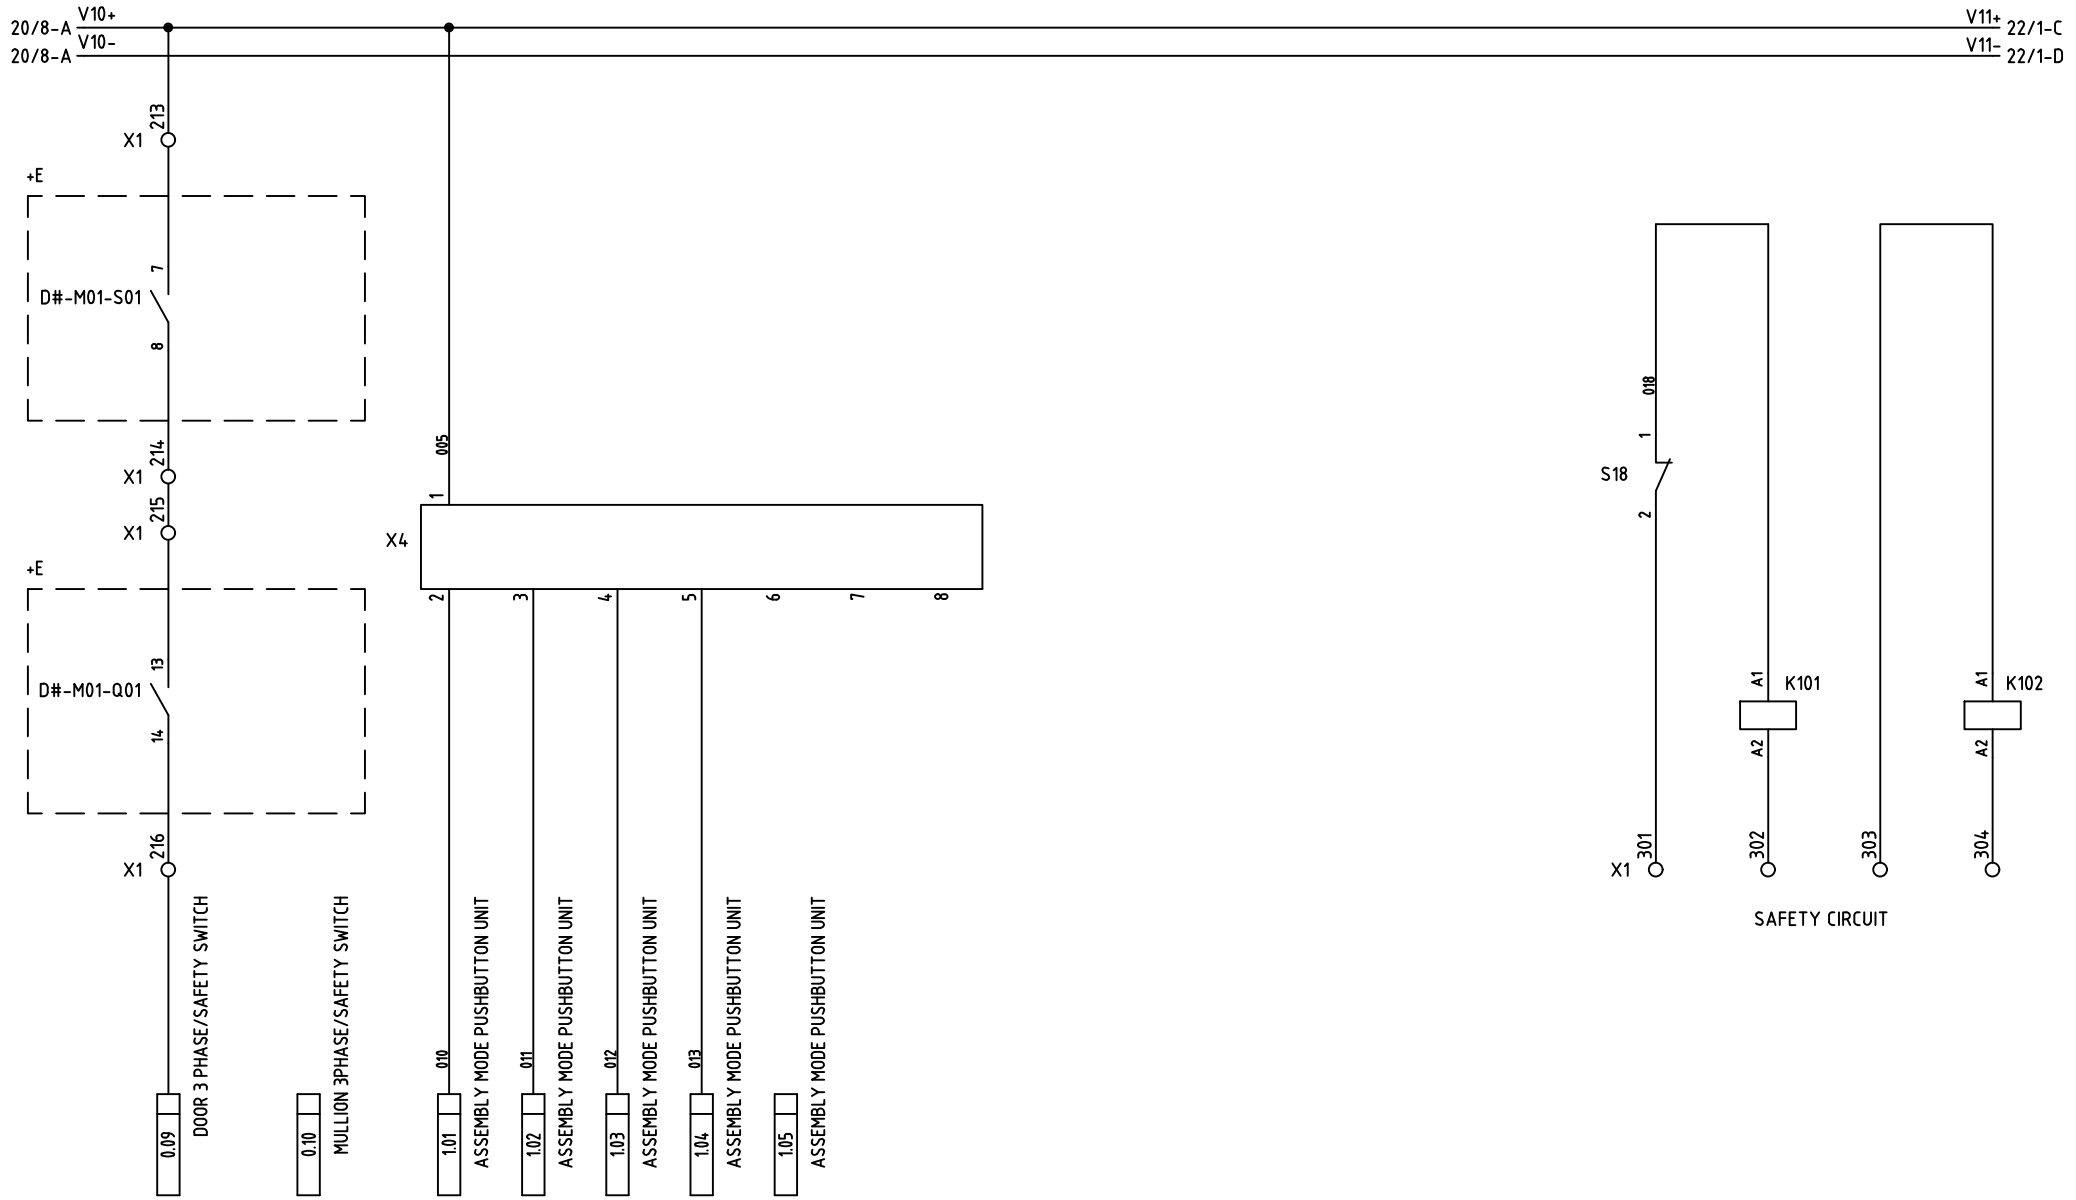

ASSA ABLOY

Property of ASSA ABLOY Entrance Systems AB and shall not without our written permission be copied, imparted to a third party or used for any other unauthorized purpose.

GMR Aero Technic Hyderabad

Direct drive | Single motor

Wiring diagram

Designed	Approved	Location	Code	Page	Date	Drawing No	Revision
MED	GO		84800001	21/45	221117	60109	--

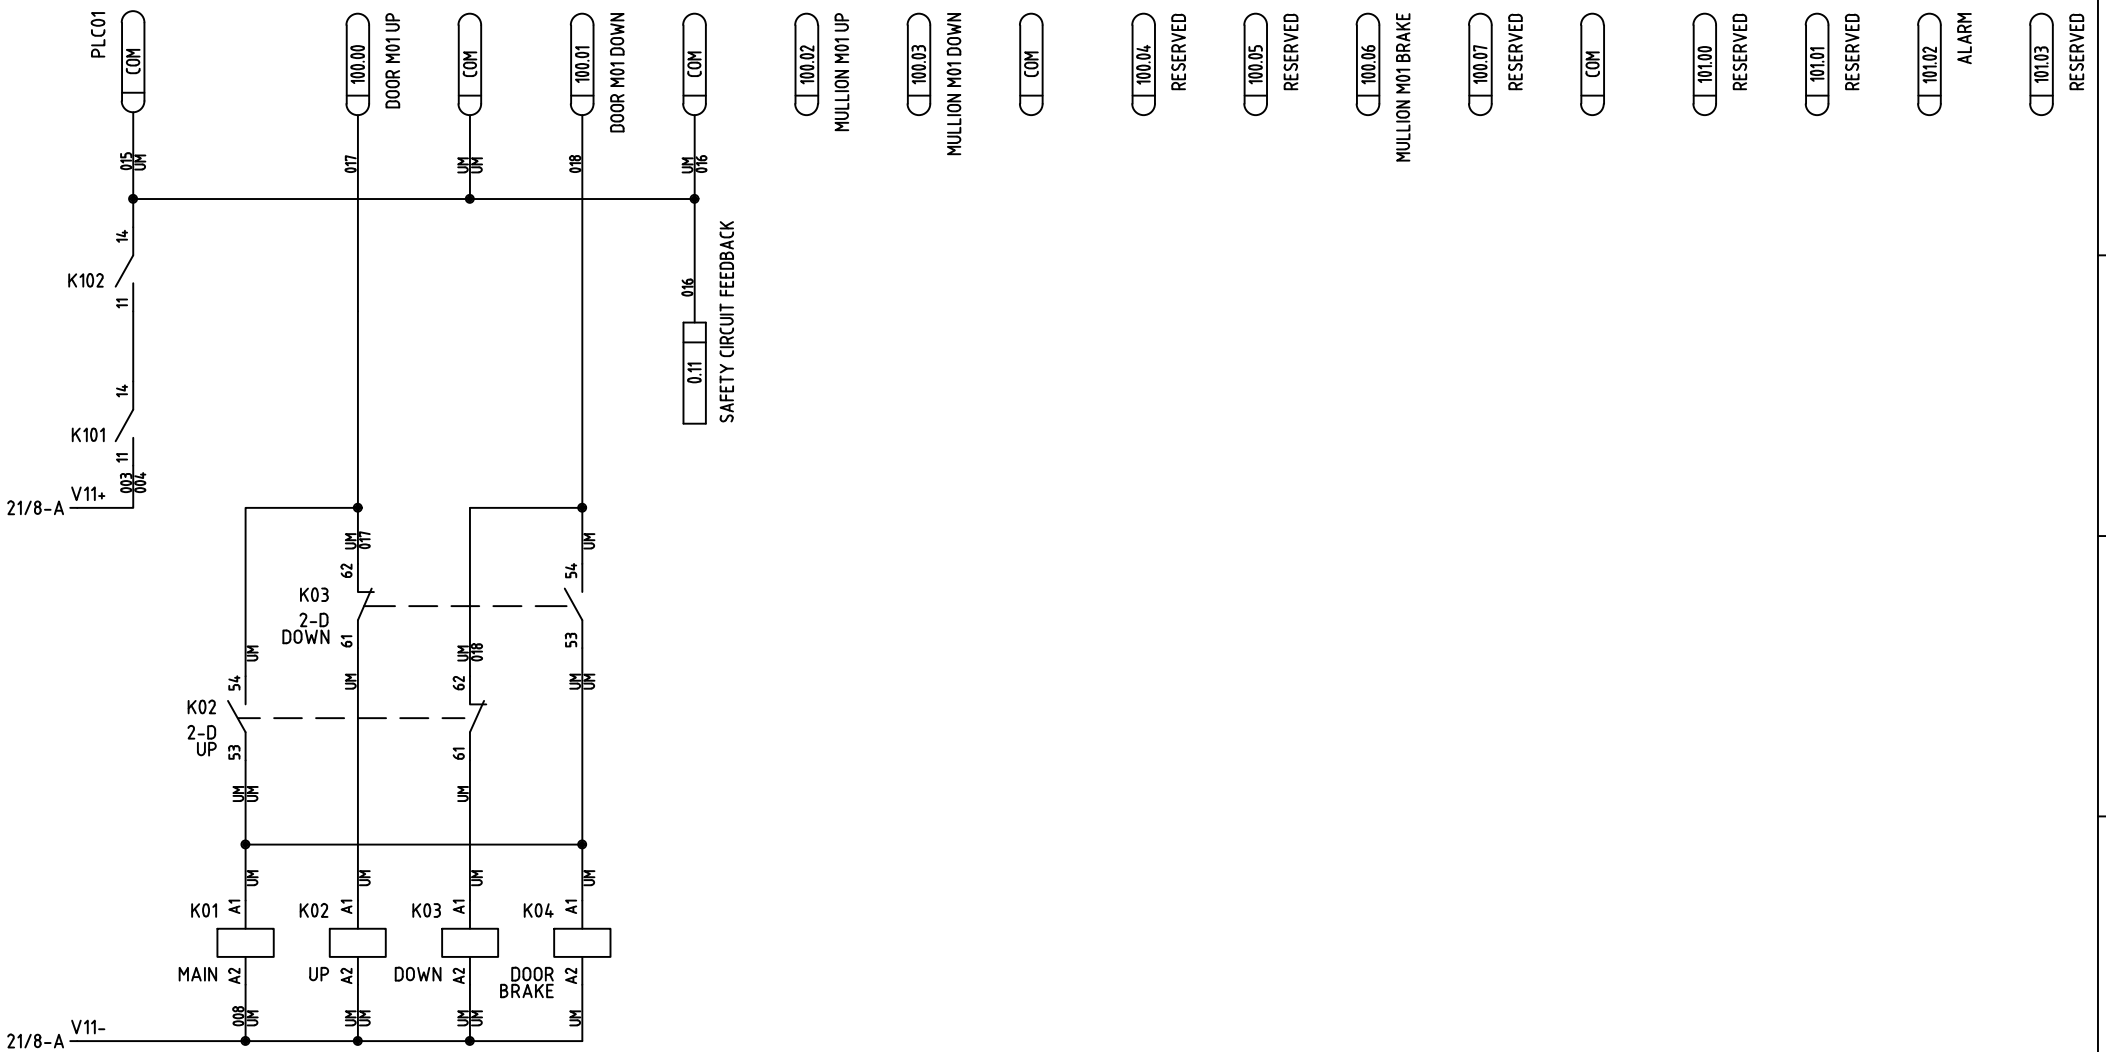

NO WIRE LABEL -> DBU0,75

ASSA ABLOY

Property of ASSA ABLOY Entrance Systems AB and shall not without our written permission be copied, imparted to a third party or used for any other unauthorized purpose.

GMR Aero Technic Hyderabad

Direct drive | Single motor

Wiring diagram

Designed	Approved	Location	Code	Page	Date	Drawing No	Revision
MED	GO		84800001	22/45	221117	60109	--

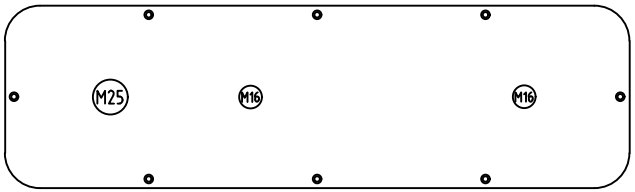

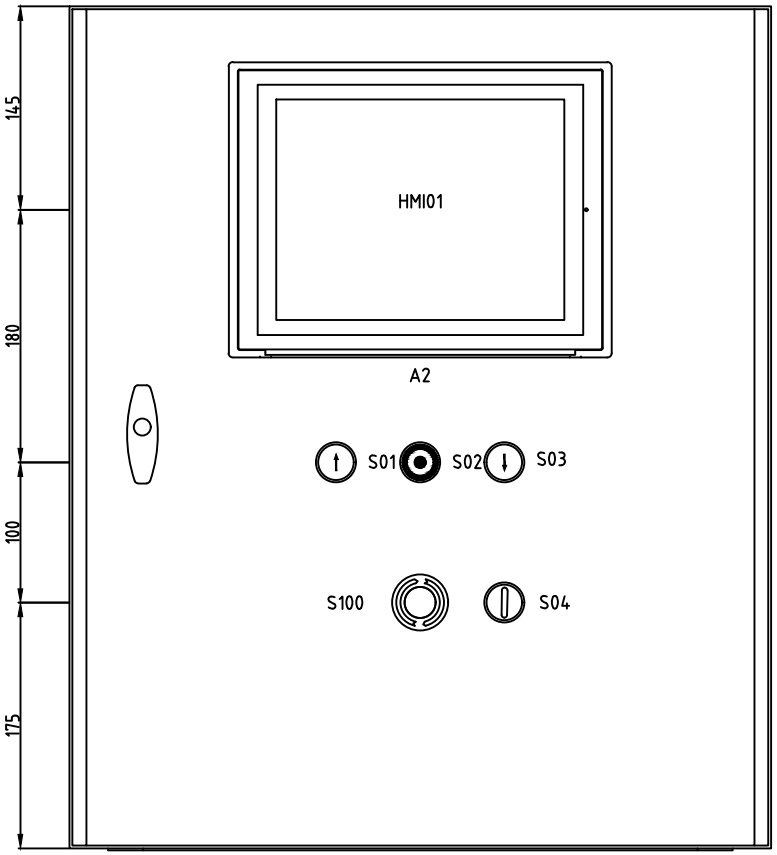

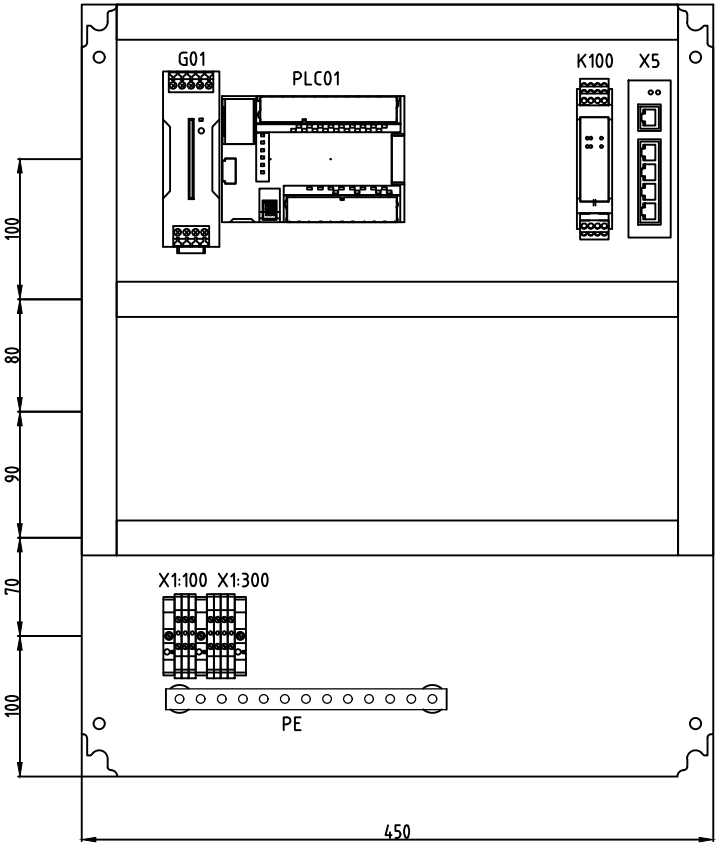

ASSA ABLOY

Property of ASSA ABLOY Entrance Systems AB and shall not without our written permission be copied, imparted to a third party or used for any other unauthorized purpose.

GMR Aero Technic Hyderabad

Direct drive | Single motor

Panel layout

Designed	Approved	Location	Code
MED	GO	+A2	84800001

Page	23 / 45
Date	221117
Drawing No	60109
Revision	C

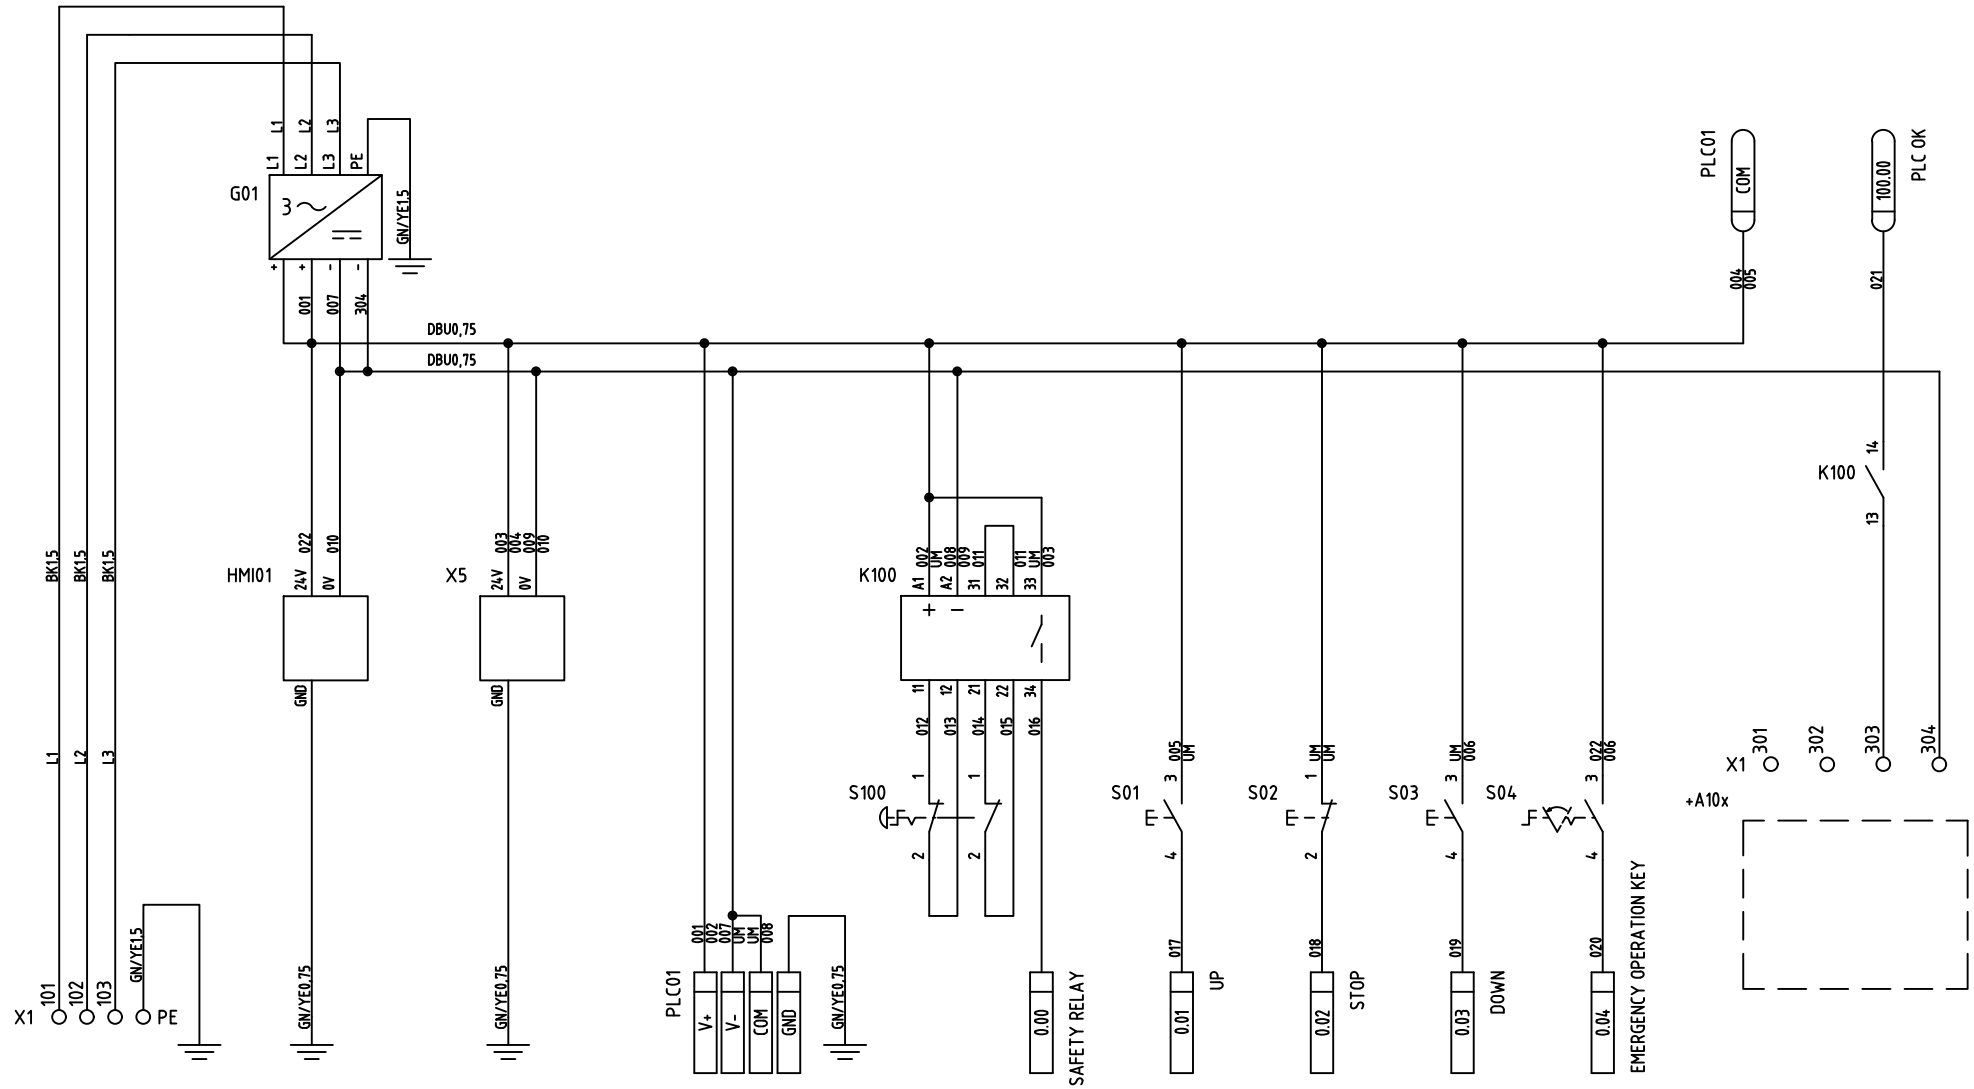

ASSA ABLOY

Property of ASSA ABLOY Entrance Systems AB and shall not without our written permission be copied, imparted to a third party or used for any other unauthorized purpose.

GMR Aero Technic Hyderabad

Direct drive | Single motor

Wiring diagram

Designed	Approved	Location	Code	Page	Date	Drawing No	Revision
MED	GO	+A2	84800001	24/45	221117	60109	C

UNIT	QTY	DESC	TYPE	MFG	TAG	CAT
PCS	1	ENCLOSURE	NSYS3D6525P	SCHNEIDER ELECTRIC	A1	19204653
PCS	1	WALL FIXING LUGS	SYAEFPFSC	SCHNEIDER ELECTRIC		19204015
PCS	1	BOTTOM PLATE	KNOCK OUT	N/A		19148751
PCS	3	TERMINAL	WDU 2,5	WEIDMÜLLER	X1:100	19203310
PCS	8	TERMINAL MARKER	DEK 5 GW X	WEIDMÜLLER		19204030
PCS	8	TERMINAL MARKER	DEK 5 GW 1	WEIDMÜLLER		19204031
PCS	3	TERMINAL MARKER	DEK 5 FWZ 101-103	WEIDMÜLLER		19204033
PCS	20	TERMINAL	WDU 2,5	WEIDMÜLLER	X1:200	19203310
PCS	20	TERMINAL MARKER	DEK 5 FW 201-220	WEIDMÜLLER		19204140
PCS	4	TERMINAL	WDU 2,5	WEIDMÜLLER	X1:300	19203310
PCS	4	TERMINAL MARKER	DEK 5 FW 301-304	WEIDMÜLLER		19204941
PCS	12	TERMINAL	WDU 2,5	WEIDMÜLLER	X1:400	19203310
PCS	12	TERMINAL MARKER	DEK 5 FW 401-412	WEIDMÜLLER		19204142
PCS	4	END BRACKET	WEW 35/2	WEIDMÜLLER		19204029
PCS	5	RELAY	G2R-2-SNI	OMRON	K11-K15	19203730
PCS	5	RELAY SOCKET	DIN 869	OMRON		19203328
PCS	1	VOLTAGE MONITOR	K8AK-PH1	OMRON	K05	19204062
PCS	1	POWER SUPPLY	S8VK T12024	OMRON	G01	19204903
PCS	1	PLC	CP1L-EM30DR-D	OMRON	PLC01	19204351
PCS	1	HMI	NB10W-TW01B	OMRON	HMI01	19204488
PCS	1	SAFETY RELAY	G9SB-3012-A	OMRON	K100	19204904
PCS	1	ETHERNET SWITCH	JET NET 2005	BEIJER	X5	19204271
PCS	1	PUSH BUTTON	ZB4BA334	SCHNEIDER ELECTRIC	S01	19203365
PCS	1	CONTACT BLOCK	ZB4BZ101	SCHNEIDER ELECTRIC		19203364
PCS	1	PUSH BUTTON	ZB4BA232	SCHNEIDER ELECTRIC	S02	19201807
PCS	1	CONTACT BLOCK	ZB4BZ102	SCHNEIDER ELECTRIC		19203005
PCS	1	PUSH BUTTON	ZB4BA334	SCHNEIDER ELECTRIC	S03	19203365
PCS	1	CONTACT BLOCK	ZB4BZ105	SCHNEIDER ELECTRIC		19204482
PCS	1	SWITCH HEAD KEY	ZB4BG6	SCHNEIDER ELECTRIC	S04	19203779
PCS	1	CONTACT BLOCK	ZB4BZ101	SCHNEIDER ELECTRIC		19203364
PCS	1	EMRG STOP	ZB4BS844	SCHNEIDER ELECTRIC	S100	19201805
PCS	1	CONTACT BLOCK	ZB4BZ104	SCHNEIDER ELECTRIC		19204481
PCS	1	USB MEMORY	16GB	NA	-	19205066

UNIT	QTY	DESC	TYPE	MFG	TAG	CAT
MM	200	PE BAR	JS 75	N/A	PE	19204158
PCS	2	SPACER	-	N/A		19204206
PCS	2	SCREW	MONTB420251	N/A		19204464
MM	1250	DIN RAIL	NS 35/7,5	N/A		19200897
PCS		SCREW	MONTB420131	N/A		19204169
PCS	3	BRACKET	TSTR 5/M5	N/A		19204159
PCS	3	SCREW	MRT-GF 5x12 ZIB	N/A		19201960
MM	1985	CABLE DUCT	25x80 PVC	N/A		19204407
PCS	12	SCREW	MONTB420131	N/A		19204169
MM	1000	SPIRAL HOSE	20 MM	N/A		19204265
PCS	4	CABLE TIE ATTACHMENT	ABM2S-A-D	N/A		19204037
PCS	4	CABLE TIE	2,5x142	N/A		19204011
		PLACEMENT OF ALL LABELS: REFER TO DRAWING 1835				
PCS	1	LABEL	ALARM	N/A		19204134
PCS	1	LABEL	YELLOW	N/A		19204087
PCS	1	LABEL	PE	N/A		19204068
PCS	1	LABEL	EARTH	N/A		19204086
PCS	1	LABEL	ASSEMBLY	N/A		19101834
PCS	1	LABEL	ASSEMBLY	N/A		19150549
PCS	1	LABEL	EMERGENCY	N/A		19101951
PCS	1	LABEL	DANGER	N/A		19101829
PCS	1	LABEL	EMERGENCY OPERATION	N/A		-
PCS	1	LABEL	CAUTION	N/A		19101952
PCS	1	LABEL	ID CEN	N/A		19146229
PCS	1	LABEL	ASSA ABLOY	N/A		19204680
PCS	1	LABEL	A1	N/A		19204259
PCS	2	CABLE GLAND	M25x1,5	N/A		19202961
PCS	2	LOCK NUT	M25x1,5	N/A		19203396
PCS	0	CABLE GLAND	M20x1,5	N/A		19202962
PCS	0	LOCK NUT	M20x1,5	N/A		19203059
PCS	2	CABLE GLAND	M16x1,5	N/A		19203314
PCS	2	LOCK NUT	M16x1,5	N/A		19203395

ASSA ABLOY

Property of ASSA ABLOY Entrance Systems AB and shall not without our written permission be copied, imparted to a third party or used for any other unauthorized purpose.

GMR Aero Technic Hyderabad

Direct drive | Single motor

Bill of material

Designed	Approved	Location	Code
MED	GO	+A1	84800001

Date 221117

Drawing No 60109

Revision --

UNIT	QTY	DESC	TYPE	MFG	TAG	CAT
PCS	1	ENCLOSURE	NSYS3D6830P	SCHNEIDER ELECTRIC	A10	19204636
PCS	1	WALL FIXING LUGS	SYAEFPFSC	SCHNEIDER ELECTRIC		19204015
PCS	1	BOTTOM PLATE	KNOCK OUT	N/A		19148753
PCS	1	BOTTOM PLATE	KNOCK OUT	N/A		19148754
PCS	1	ISOLATOR	KG105 T903/S-A308 xVE	KRAUS & NAIMER	Q100	-
PCS	1	TERMINAL	WDU 35 BL	WEIDMÜLLER	XN	19204301
PCS	6	TERMINAL	WDU 2,5	WEIDMÜLLER	X1:100-106	19203310
PCS	3	TERMINAL	WDU 6	WEIDMÜLLER	X1:107-109	19203770
PCS	3	TERMINAL	WDU 2,5	WEIDMÜLLER	X1:110-112	19203310
PCS	3	TERMINAL	WDU 6	WEIDMÜLLER	X1:113-115	19203770
PCS	3	TERMINAL	WDU 2,5	WEIDMÜLLER	X1:116-118	19203310
PCS	3	TERMINAL	WDU 6	WEIDMÜLLER	X1:119-121	19203770
PCS	3	TERMINAL	WDU 2,5	WEIDMÜLLER	X1:122-124	19203310
PCS	3	TERMINAL	WDU 6	WEIDMÜLLER	X1:125-127	19203770
PCS	3	TERMINAL	WDU 2,5	WEIDMÜLLER	X1:128-130	19203310
PCS	3	TERMINAL	WDU 6	WEIDMÜLLER	X1:131-133	19203770
PCS	33	TERMINAL MARKER	DEK 5 FWZ 101-133	WEIDMÜLLER		19205205
PCS	16	TERMINAL	WDU 2,5	WEIDMÜLLER	X1:200	19203310
PCS	16	TERMINAL MARKER	DEK 5 FW 201-216	WEIDMÜLLER		19204140
PCS	3	END BRACKET	WEW 35/2	WEIDMÜLLER		19204029
PCS	5	CURRENT TRANSFORMER	TAI-BB 50/1	TÄLJE MÄTINSTRUMENT	T01-T06	19200152
PCS	5	POWER MONITOR	G2BM400V12AFL10	TELE HAASE	K01 - K06	19204437
PCS	4	POWER MONITOR	G2BM400V12AFL10	TELE HAASE	K12 - K56	19204437
PCS	2	TERMINAL BLOCK	GV1G09	SCHNEIDER ELECTRIC		19204229
PCS	2	BUS BAR	GV2G254	SCHNEIDER ELECTRIC		19204230
PCS	1	BUS BAR	GV2G354	SCHNEIDER ELECTRIC		19204674
PCS	1	BUS BAR	GV2G554	SCHNEIDER ELECTRIC		19204494
PCS	1	CIRCUIT BREAKER	GV2ME10 4.0-6.3A	SCHNEIDER ELECTRIC	Q00	19203727
PCS	1	CIRCUIT BREAKER	GV2ME21 17-23A	SCHNEIDER ELECTRIC	Q01	19204451
PCS	1	CIRCUIT BREAKER	GV2ME14 6.0-10A	SCHNEIDER ELECTRIC	Q12	19203726
PCS	1	CIRCUIT BREAKER	GV2ME21 17-23A	SCHNEIDER ELECTRIC	Q02	19204451
PCS	1	CIRCUIT BREAKER	GV2ME14 6.0-10A	SCHNEIDER ELECTRIC	Q23	19203726
PCS	1	CIRCUIT BREAKER	GV2ME21 17-23A	SCHNEIDER ELECTRIC	Q03	19204451
PCS	1	CIRCUIT BREAKER	GV2ME14 6.0-10A	SCHNEIDER ELECTRIC	Q34	19203726
PCS	1	CIRCUIT BREAKER	GV2ME21 17-23A	SCHNEIDER ELECTRIC	Q04	19204451
PCS	1	CIRCUIT BREAKER	GV2ME14 6.0-10A	SCHNEIDER ELECTRIC	Q45	19203726
PCS	1	CIRCUIT BREAKER	GV2ME21 17-23A	SCHNEIDER ELECTRIC	Q05	19204451
PCS	9	CONTACT BLOCK	GVAN11	SCHNEIDER ELECTRIC		19204111

UNIT	QTY	DESC	TYPE	MFG	TAG	CAT
MM	600	PE BAR	JS 75	N/A	PE	19204158
PCS	3	SPACER	-	N/A		19204206
PCS	3	SCREW	MONTB420251	N/A		19204464
MM		DIN RAIL	NS 35/7,5	N/A		19200897
PCS		SCREW	MONTB420131	N/A		19204169
PCS	3	BRACKET	TSTR 5/M5	N/A		19204159
PCS	3	SCREW	MRT-GF 5x12 ZIB	N/A		19201960
MM		CABLE DUCT	40x80 PVC	N/A		19204356
PCS	12	SCREW	MONTB420131	N/A		19204169
PCS	1	3-PHASE INLET	432BU6	ABB	X99	19204138
PCS	4	SCREW	MRT-GF 5x16	N/A		19200263
		PLACEMENT OF ALL LABELS: REFER TO DRAWING 1835				
PCS	1	LABEL	PE	N/A		19204068
PCS	1	LABEL	EARTH	N/A		19204086
PCS	1	LABEL	ASSEMBLY	N/A		19101834
PCS	1	LABEL	ASSEMBLY	N/A		19150549
PCS	1	LABEL	DANGER	N/A		19101829
PCS	1	LABEL	CAUTION	N/A		19101952
PCS	1	LABEL	ASSA ABLOY	N/A		19204680
PCS	1	LABEL	A10	N/A		-
PCS	1	CABLE GLAND	M40x1,5	N/A		19204326
PCS	1	LOCK NUT	M40x1,5	N/A		19204327
PCS	11	CABLE GLAND	M25x1,5	N/A		19202961
PCS	11	LOCK NUT	M25x1,5	N/A		19203396
PCS	0	CABLE GLAND	M20x1,5	N/A		19202962
PCS	0	LOCK NUT	M20x1,5	N/A		19203059

ASSA ABLOY

Property of ASSA ABLOY Entrance Systems AB and shall not without our written permission be copied, imparted to a third party or used for any other unauthorized purpose.

GMR Aero Technic Hyderabad

Direct drive | Single motor

Bill of material

Designed	Approved	Location	Code
MED	GO	+A10	84800001

Page 26/45

Date 221117

Drawing No 60109

Revision --

UNIT	QTY	DESC	TYPE	MFG	TAG	CAT
PCS	1	ENCLOSURE	NSYS3D6625P	SCHNEIDER ELECTRIC	A101	19204303
PCS	1	WALL FIXING LUGS	SYAEFPFSC	SCHNEIDER ELECTRIC		19204015
PCS	1	BOTTOM PLATE	KNOCK OUT	N/A		19148752
PCS	20	TERMINAL	WDU 2,5	WEIDMÜLLER	X1:100	19203310
PCS	3	TERMINAL	WDU 6	WEIDMÜLLER	X1:107-109	19203770
PCS	3	TERMINAL	WDU 6	WEIDMÜLLER	X1:113-115	19203770
PCS	8	TERMINAL MARKER	DEK 5 GW X	WEIDMÜLLER		19204030
PCS	8	TERMINAL MARKER	DEK 5 GW 1	WEIDMÜLLER		19204031
PCS	26	TERMINAL MARKER	DEK 5 FWZ 101-126	WEIDMÜLLER		19205205
PCS	29	TERMINAL	WDU 2,5	WEIDMÜLLER	X1:200	19203310
PCS	29	TERMINAL MARKER	DEK 5 FW 201-229	WEIDMÜLLER		19204140
PCS	4	TERMINAL	WDU 2,5	WEIDMÜLLER	X1:300	19203310
PCS	4	TERMINAL MARKER	DEK 5 FW 301-304	WEIDMÜLLER		19204941
PCS	2	TERMINAL	WDU 2,5	WEIDMÜLLER	X1:400	19203310
PCS	2	TERMINAL MARKER	DEK 5 FW 401-402	WEIDMÜLLER		19204142
PCS	4	END BRACKET	WEW 35/2	WEIDMÜLLER		19204029
PCS	2	RELAY	G2R-2-SNI	OMRON	K101-K102	19203730
PCS	2	RELAY SOCKET	DIN 869	OMRON		19203328
PCS	1	POWER SUPPLY	S8VK T12024	OMRON	G01	19204903
PCS	1	PLC	CP1L-EM30DR-D	OMRON	PLC01	19204351
PCS	1	OPTION BOARD	CP1W-CIF11	OMRON	PLC_MOD2	19204352
PCS	1	RJ45 TERMINAL	CIM/RJ45	CAMDENBOSS	X4	19204621
PCS	1	ETHERNET SWITCH	JET NET 2005	BEIJER	X5	19204271
PCS	2	BUS BAR	GV2G354	SCHNEIDER ELECTRIC		19204674
PCS	3	CONTACTOR	LC1D25 BL	SCHNEIDER ELECTRIC	K01-K03	19204489
PCS	3	CONTACTOR	LC1D09 BL	SCHNEIDER ELECTRIC	K05-K07	19204269
PCS	2	CONTACTOR	LC1D09 BL	SCHNEIDER ELECTRIC	K04,K08	19204269
PCS	4	CONTACT BLOCK	LADN11	SCHNEIDER ELECTRIC		19202995
PCS	2	TERMINAL	WDU 2,5	WEIDMÜLLER	X2	19203310
PCS	2	TERMINAL MARKER	DEK 5 GW X	WEIDMÜLLER		19204030
PCS	2	TERMINAL MARKER	DEK 5 GW 2	WEIDMÜLLER		19204478
PCS	2	TERMINAL MARKER	DEK 5 +	WEIDMÜLLER		19204675
PCS	2	TERMINAL MARKER	DEK 5 -	WEIDMÜLLER		19204676
PCS	2	END BRACKET	WEW 35/2	WEIDMÜLLER		19204029
PCS	1	HAND CRANK	Ø28	N/A	S18	19151069
PCS	1	HAND CRANK	Ø24	N/A	S19	19151068

UNIT	QTY	DESC	TYPE	MFG	TAG	CAT
MM	200	PE BAR	JS 75	N/A	PE	19204158
PCS	2	SPACER	-	N/A		19204206
PCS	2	SCREW	MONTB420251	N/A		19204464
MM	1250	DIN RAIL	NS 35/7,5	N/A		19200897
PCS		SCREW	MONTB420131	N/A		19204169
PCS	3	BRACKET	TSTR 5/M5	N/A		19204159
PCS	3	SCREW	MRT-GF 5x12 ZIB	N/A		19201960
MM	1800	CABLE DUCT	25x80 PVC	N/A		19204407
MM	500	CABLE DUCT	40x80 PVC	N/A		19204939
PCS	12	SCREW	MONTB420131	N/A		19204169
		PLACEMENT OF ALL LABELS: REFER TO DRAWING 1835				
PCS	1	LABEL	PE	N/A		19204068
PCS	1	LABEL	EARTH	N/A		19204086
PCS	1	LABEL	DANGER	N/A		19101829
PCS	1	LABEL	CAUTION	N/A		19101952
PCS	8	LABEL	ARROW	N/A		19200182
PCS	1	LABEL	A101	N/A		19204397
PCS	6	CABLE GLAND	M25x1,5	N/A		19202961
PCS	6	LOCK NUT	M25x1,5	N/A		19203396
PCS	16	CABLE GLAND	M16x1,5	N/A		19203314
PCS	16	LOCK NUT	M16x1,5	N/A		19203395
PCS	3	PROXIMITY SWITCH	IGS 277	IFM	D1-L11 - D1-L12, D1-L15	19203948
PCS	1	PROXIMITY SWITCH	IGS 277	IFM	M12-L21	19203948
PCS	1	PROXIMITY SWITCH	IGS 277	IFM	M12-L24	19203948
PCS	2	SIGNAL LIGHT/SIREN	SONL24/O-H	TOLEKA	M12-P02	19203722
PCS	2	JUNCTION BOX	UE2	GARO	KD121, KD122	19203000
PCS	1	3-PHASE SWITCH	CA25B WAA207GK1	KRAUS & NAIMER	D1-M01-S01	19204457
PCS	1	SAFETY SWITCH	KF325/11	KRAUS & NAIMER	D1-M01-Q01	19204102
PCS	2	CABLE GLAND	M25x1,5	N/A		19202961
PCS	1	CABLE GLAND	M20x1,5	N/A		19202962
PCS	1	3-PHASE SWITCH	CA25B WAA207GK1	KRAUS & NAIMER	M12-S01	19150905
PCS	1	SAFETY SWITCH	KF325/11	KRAUS & NAIMER	M12-Q01	19204102
PCS	2	CABLE GLAND	M25x1,5	N/A		19202961
PCS	1	CABLE GLAND	M20x1,5	N/A		19202962
PCS	1	M12 CONNECTOR	P/N 1200700237	MOLEX	X7	19205193
PCS	1	ABSOLUTE ENCODER	F5868.287579	KÜBLER	M12-B01	19204569

ASSA ABLOY

Property of ASSA ABLOY Entrance Systems AB and shall not without our written permission be copied, imparted to a third party or used for any other unauthorized purpose.

GMR Aero Technic Hyderabad

Direct drive | Single motor

Bill of material

Designed	Approved	Location	Code
MED	GO	+A10?	84800001

Date 221117

Drawing No 60109

Revision --

UNIT	QTY	DESC	TYPE	MFG	TAG	CAT
PCS	1	ENCLOSURE	NSYS3D6625P	SCHNEIDER ELECTRIC	A102	19204303
PCS	1	WALL FIXING LUGS	SYAEFPFSC	SCHNEIDER ELECTRIC		19204015
PCS	1	BOTTOM PLATE	KNOCK OUT	N/A		19148752
PCS	20	TERMINAL	WDU 2,5	WEIDMÜLLER	X1:100	19203310
PCS	3	TERMINAL	WDU 6	WEIDMÜLLER	X1:107-109	19203770
PCS	3	TERMINAL	WDU 6	WEIDMÜLLER	X1:113-115	19203770
PCS	8	TERMINAL MARKER	DEK 5 GW X	WEIDMÜLLER		19204030
PCS	8	TERMINAL MARKER	DEK 5 GW 1	WEIDMÜLLER		19204031
PCS	26	TERMINAL MARKER	DEK 5 FWZ 101-126	WEIDMÜLLER		19205205
PCS	29	TERMINAL	WDU 2,5	WEIDMÜLLER	X1:200	19203310
PCS	29	TERMINAL MARKER	DEK 5 FW 201-229	WEIDMÜLLER		19204140
PCS	4	TERMINAL	WDU 2,5	WEIDMÜLLER	X1:300	19203310
PCS	4	TERMINAL MARKER	DEK 5 FW 301-304	WEIDMÜLLER		19204941
PCS	2	TERMINAL	WDU 2,5	WEIDMÜLLER	X1:400	19203310
PCS	2	TERMINAL MARKER	DEK 5 FW 401-402	WEIDMÜLLER		19204142
PCS	4	END BRACKET	WEW 35/2	WEIDMÜLLER		19204029
PCS	2	RELAY	G2R-2-SNI	OMRON	K101-K102	19203730
PCS	2	RELAY SOCKET	DIN 869	OMRON		19203328
PCS	1	POWER SUPPLY	S8VK T12024	OMRON	G01	19204903
PCS	1	PLC	CP1L-EM30DR-D	OMRON	PLC01	19204351
PCS	1	OPTION BOARD	CP1W-CIF11	OMRON	PLC_MOD2	19204352
PCS	1	RJ45 TERMINAL	CIM/RJ45	CAMDENBOSS	X4	19204621
PCS	1	ETHERNET SWITCH	JET NET 2005	BEIJER	X5	19204271
PCS	2	BUS BAR	GV2G354	SCHNEIDER ELECTRIC		19204674
PCS	3	CONTACTOR	LC1D25 BL	SCHNEIDER ELECTRIC	K01-K03	19204489
PCS	3	CONTACTOR	LC1D09 BL	SCHNEIDER ELECTRIC	K05-K07	19204269
PCS	2	CONTACTOR	LC1D09 BL	SCHNEIDER ELECTRIC	K04,K08	19204269
PCS	4	CONTACT BLOCK	LADN11	SCHNEIDER ELECTRIC		19202995
PCS	2	TERMINAL	WDU 2,5	WEIDMÜLLER	X2	19203310
PCS	2	TERMINAL MARKER	DEK 5 GW X	WEIDMÜLLER		19204030
PCS	2	TERMINAL MARKER	DEK 5 GW 2	WEIDMÜLLER		19204478
PCS	2	TERMINAL MARKER	DEK 5 +	WEIDMÜLLER		19204675
PCS	2	TERMINAL MARKER	DEK 5 -	WEIDMÜLLER		19204676
PCS	2	END BRACKET	WEW 35/2	WEIDMÜLLER		19204029
PCS	1	HAND CRANK	Ø28	N/A	S18	19151069
PCS	1	HAND CRANK	Ø24	N/A	S19	19151068

UNIT	QTY	DESC	TYPE	MFG	TAG	CAT
MM	200	PE BAR	JS 75	N/A	PE	19204158
PCS	2	SPACER	-	N/A		19204206
PCS	2	SCREW	MONTB420251	N/A		19204464
MM	1250	DIN RAIL	NS 35/7,5	N/A		19200897
PCS		SCREW	MONTB420131	N/A		19204169
PCS	3	BRACKET	TSTR 5/M5	N/A		19204159
PCS	3	SCREW	MRT-GF 5x12 ZIB	N/A		19201960
MM	1800	CABLE DUCT	25x80 PVC	N/A		19204407
MM	500	CABLE DUCT	40x80 PVC	N/A		19204939
PCS	12	SCREW	MONTB420131	N/A		19204169
		PLACEMENT OF ALL LABELS: REFER TO DRAWING 1835				
PCS	1	LABEL	PE	N/A		19204068
PCS	1	LABEL	EARTH	N/A		19204086
PCS	1	LABEL	DANGER	N/A		19101829
PCS	1	LABEL	CAUTION	N/A		19101952
PCS	8	LABEL	ARROW	N/A		19200182
PCS	1	LABEL	A102	N/A		19204398
PCS	6	CABLE GLAND	M25x1,5	N/A		19202961
PCS	6	LOCK NUT	M25x1,5	N/A		19203396
PCS	16	CABLE GLAND	M16x1,5	N/A		19203314
PCS	16	LOCK NUT	M16x1,5	N/A		19203395
PCS	3	PROXIMITY SWITCH	IGS 277	IFM	D2-L11 - D2-L12, D2-L15	19203948
PCS	1	PROXIMITY SWITCH	IGS 277	IFM	M23-L21	19203948
PCS	1	PROXIMITY SWITCH	IGS 277	IFM	M23-L24	19203948
PCS	2	SIGNAL LIGHT/SIREN	SONL24/O-H	TOLEKA	M23-P01/2	19203722
PCS	2	JUNCTION BOX	UE2	GARO	KD231, KD232	19203000
PCS	1	3-PHASE SWITCH	CA25B WAA207GK1	KRAUS & NAIMER	D2-M01-S01	19204457
PCS	1	SAFETY SWITCH	KF325/11	KRAUS & NAIMER	D2-M01-Q01	19204102
PCS	2	CABLE GLAND	M25x1,5	N/A		19202961
PCS	1	CABLE GLAND	M20x1,5	N/A		19202962
PCS	1	3-PHASE SWITCH	CA25B WAA207GK1	KRAUS & NAIMER	M23-S01	19150905
PCS	1	SAFETY SWITCH	KF325/11	KRAUS & NAIMER	M23-Q01	19204102
PCS	2	CABLE GLAND	M25x1,5	N/A		19202961
PCS	1	CABLE GLAND	M20x1,5	N/A		19202962
PCS	1	M12 CONNECTOR	P/N 1200700237	MOLEX	X7	19205193
PCS	1	ABSOLUTE ENCODER	F5868.287579	KÜBLER	M23-B01	19204569

ASSA ABLOY

Property of ASSA ABLOY Entrance Systems AB and shall not without our written permission be copied, imparted to a third party or used for any other unauthorized purpose.

GMR Aero Technic Hyderabad

Direct drive | Single motor

Bill of material

Designed	Approved	Location	Code
MED	GO	+A102	84800001

Date 221117

Drawing No 60109

Revision --

UNIT	QTY	DESC	TYPE	MFG	TAG	CAT
PCS	1	ENCLOSURE	NSYS3D6525P	SCHNEIDER ELECTRIC	A103	19204653
PCS	1	WALL FIXING LUGS	SYAEFPFSC	SCHNEIDER ELECTRIC		19204015
PCS	1	BOTTOM PLATE	KNOCK OUT	N/A		19148751
PCS	10	TERMINAL	WDU 2,5	WEIDMÜLLER	X1:100	19203310
PCS	3	TERMINAL	WDU 6	WEIDMÜLLER	X1:107-109	19203770
PCS	3	TERMINAL	WDU 6	WEIDMÜLLER	X1:110-112	19203770
PCS	8	TERMINAL MARKER	DEK 5 GW X	WEIDMÜLLER		19204030
PCS	8	TERMINAL MARKER	DEK 5 GW 1	WEIDMÜLLER		19204031
PCS	16	TERMINAL MARKER	DEK 5 FWZ 101-116	WEIDMÜLLER		19205205
PCS	16	TERMINAL	WDU 2,5	WEIDMÜLLER	X1:200	19203310
PCS	16	TERMINAL MARKER	DEK 5 FW 201-216	WEIDMÜLLER		19204140
PCS	4	TERMINAL	WDU 2,5	WEIDMÜLLER	X1:300	19203310
PCS	4	TERMINAL MARKER	DEK 5 FW 301-304	WEIDMÜLLER		19204941
PCS	3	END BRACKET	WEW 35/2	WEIDMÜLLER		19204029
PCS	2	RELAY	G2R-2-SNI	OMRON	K101-K102	19203730
PCS	2	RELAY SOCKET	DIN 869	OMRON		19203328
PCS	1	POWER SUPPLY	S8VK T12024	OMRON	G01	19204903
PCS	1	PLC	CP1L-EM30DR-D	OMRON	PLC01	19204351
PCS	1	RJ45 TERMINAL	CIM/RJ45	CAMDENBOSS	X4	19204621
PCS	1	ETHERNET SWITCH	JET NET 2005	BEIJER	X5	19204271
PCS	1	BUS BAR	GV2G354	SCHNEIDER ELECTRIC		19204674
PCS	3	CONTACTOR	LC1D25 BL	SCHNEIDER ELECTRIC	K01-K03	19204489
PCS	1	CONTACTOR	LC1D09 BL	SCHNEIDER ELECTRIC	K04	19204269
PCS	2	CONTACT BLOCK	LADN11	SCHNEIDER ELECTRIC		19202995
PCS	2	TERMINAL	WDU 2,5	WEIDMÜLLER	X2	19203310
PCS	2	TERMINAL MARKER	DEK 5 GW X	WEIDMÜLLER		19204030
PCS	2	TERMINAL MARKER	DEK 5 GW 2	WEIDMÜLLER		19204478
PCS	2	TERMINAL MARKER	DEK 5 +	WEIDMÜLLER		19204675
PCS	2	TERMINAL MARKER	DEK 5 -	WEIDMÜLLER		19204676
PCS	2	END BRACKET	WEW 35/2	WEIDMÜLLER		19204029
PCS	1	HAND CRANK	Ø28	N/A	S18	19151069

UNIT	QTY	DESC	TYPE	MFG	TAG	CAT
MM	200	PE BAR	JS 75	N/A	PE	19204158
PCS	2	SPACER	-	N/A		19204206
PCS	2	SCREW	MONTB420251	N/A		19204464
MM	1250	DIN RAIL	NS 35/7,5	N/A		19200897
PCS		SCREW	MONTB420131	N/A		19204169
PCS	3	BRACKET	TSTR 5/M5	N/A		19204159
PCS	3	SCREW	MRT-GF 5x12 ZIB	N/A		19201960
MM	1600	CABLE DUCT	25x80 PVC	N/A		19204407
MM	400	CABLE DUCT	40x80 PVC	N/A		19204939
PCS	12	SCREW	MONTB420131	N/A		19204169
		PLACEMENT OF ALL LABELS: REFER TO DRAWING 1835				
PCS	1	LABEL	PE	N/A		19204068
PCS	1	LABEL	EARTH	N/A		19204086
PCS	1	LABEL	DANGER	N/A		19101829
PCS	1	LABEL	CAUTION	N/A		19101952
PCS	4	LABEL	ARROW	N/A		19200182
PCS	1	LABEL	A103	N/A		19204399
PCS	4	CABLE GLAND	M25x1,5	N/A		19202961
PCS	4	LOCK NUT	M25x1,5	N/A		19203396
PCS	10	CABLE GLAND	M16x1,5	N/A		19203314
PCS	10	LOCK NUT	M16x1,5	N/A		19203395
PCS	3	PROXIMITY SWITCH	IGS 277	IFM	D4-L11 - D4-L12, D4-L15	19203948
PCS	1	3-PHASE SWITCH	CA25B WAA207GK1	KRAUS & NAIMER	D3-M01-S01	19204457
PCS	1	SAFETY SWITCH	KF325/11	KRAUS & NAIMER	D3-M01-Q01	19204102
PCS	2	CABLE GLAND	M25x1,5	N/A		19202961
PCS	1	CABLE GLAND	M20x1,5	N/A		19202962

ASSA ABLOY

Property of ASSA ABLOY Entrance Systems AB and shall not without our written permission be copied, imparted to a third party or used for any other unauthorized purpose.

GMR Aero Technic Hyderabad

Direct drive | Single motor

Bill of material

Designed	Approved	Location	Code
MED	GO	+A103	84800001

Page 29/45

Date 221117

Drawing No 60109

Revision --

UNIT	QTY	DESC	TYPE	MFG	TAG	CAT
PCS	1	ENCLOSURE	NSYS3D6625P	SCHNEIDER ELECTRIC	A104	19204303
PCS	1	WALL FIXING LUGS	SYAEFPFSC	SCHNEIDER ELECTRIC		19204015
PCS	1	BOTTOM PLATE	KNOCK OUT	N/A		19148752
PCS	20	TERMINAL	WDU 2,5	WEIDMÜLLER	X1:100	19203310
PCS	3	TERMINAL	WDU 6	WEIDMÜLLER	X1:107-109	19203770
PCS	3	TERMINAL	WDU 6	WEIDMÜLLER	X1:113-115	19203770
PCS	8	TERMINAL MARKER	DEK 5 GW X	WEIDMÜLLER		19204030
PCS	8	TERMINAL MARKER	DEK 5 GW 1	WEIDMÜLLER		19204031
PCS	26	TERMINAL MARKER	DEK 5 FWZ 101-126	WEIDMÜLLER		19205205
PCS	29	TERMINAL	WDU 2,5	WEIDMÜLLER	X1:200	19203310
PCS	29	TERMINAL MARKER	DEK 5 FW 201-229	WEIDMÜLLER		19204140
PCS	4	TERMINAL	WDU 2,5	WEIDMÜLLER	X1:300	19203310
PCS	4	TERMINAL MARKER	DEK 5 FW 301-304	WEIDMÜLLER		19204941
PCS	2	TERMINAL	WDU 2,5	WEIDMÜLLER	X1:400	19203310
PCS	2	TERMINAL MARKER	DEK 5 FW 401-402	WEIDMÜLLER		19204142
PCS	4	END BRACKET	WEW 35/2	WEIDMÜLLER		19204029
PCS	2	RELAY	G2R-2-SNI	OMRON	K101-K102	19203730
PCS	2	RELAY SOCKET	DIN 869	OMRON		19203328
PCS	1	POWER SUPPLY	S8VK T12024	OMRON	G01	19204903
PCS	1	PLC	CP1L-EM30DR-D	OMRON	PLC01	19204351
PCS	1	OPTION BOARD	CP1W-CIF11	OMRON	PLC_MOD2	19204352
PCS	1	RJ45 TERMINAL	CIM/RJ45	CAMDENBOSS	X4	19204621
PCS	1	ETHERNET SWITCH	JET NET 2005	BEIJER	X5	19204271
PCS	2	BUS BAR	GV2G354	SCHNEIDER ELECTRIC		19204674
PCS	3	CONTACTOR	LC1D25 BL	SCHNEIDER ELECTRIC	K01-K03	19204489
PCS	3	CONTACTOR	LC1D09 BL	SCHNEIDER ELECTRIC	K05-K07	19204269
PCS	2	CONTACTOR	LC1D09 BL	SCHNEIDER ELECTRIC	K04,K08	19204269
PCS	4	CONTACT BLOCK	LADN11	SCHNEIDER ELECTRIC		19202995
PCS	2	TERMINAL	WDU 2,5	WEIDMÜLLER	X2	19203310
PCS	2	TERMINAL MARKER	DEK 5 GW X	WEIDMÜLLER		19204030
PCS	2	TERMINAL MARKER	DEK 5 GW 2	WEIDMÜLLER		19204478
PCS	2	TERMINAL MARKER	DEK 5 +	WEIDMÜLLER		19204675
PCS	2	TERMINAL MARKER	DEK 5 -	WEIDMÜLLER		19204676
PCS	2	END BRACKET	WEW 35/2	WEIDMÜLLER		19204029
PCS	1	HAND CRANK	Ø28	N/A	S18	19151069
PCS	1	HAND CRANK	Ø24	N/A	S19	19151068

UNIT	QTY	DESC	TYPE	MFG	TAG	CAT
MM	200	PE BAR	JS 75	N/A	PE	19204158
PCS	2	SPACER	-	N/A		19204206
PCS	2	SCREW	MONTB420251	N/A		19204464
MM	1250	DIN RAIL	NS 35/7,5	N/A		19200897
PCS		SCREW	MONTB420131	N/A		19204169
PCS	3	BRACKET	TSTR 5/M5	N/A		19204159
PCS	3	SCREW	MRT-GF 5x12 ZIB	N/A		19201960
MM	1800	CABLE DUCT	25x80 PVC	N/A		19204407
MM	500	CABLE DUCT	40x80 PVC	N/A		19204939
PCS	12	SCREW	MONTB420131	N/A		19204169
		PLACEMENT OF ALL LABELS: REFER TO DRAWING 1835				
PCS	1	LABEL	PE	N/A		19204068
PCS	1	LABEL	EARTH	N/A		19204086
PCS	1	LABEL	DANGER	N/A		19101829
PCS	1	LABEL	CAUTION	N/A		19101952
PCS	8	LABEL	ARROW	N/A		19200182
PCS	1	LABEL	A104	N/A		19205240
PCS	6	CABLE GLAND	M25x1,5	N/A		19202961
PCS	6	LOCK NUT	M25x1,5	N/A		19203396
PCS	16	CABLE GLAND	M16x1,5	N/A		19203314
PCS	16	LOCK NUT	M16x1,5	N/A		19203395
PCS	3	PROXIMITY SWITCH	IGS 277	IFM	D4-L11 - D4-L12, D4-L15	19203948
PCS	1	PROXIMITY SWITCH	IGS 277	IFM	M34-L21	19203948
PCS	1	PROXIMITY SWITCH	IGS 277	IFM	M34-L24	19203948
PCS	2	SIGNAL LIGHT/SIREN	SONL24/O-H	TOLEKA	M34-P01/2	19203722
PCS	2	JUNCTION BOX	UE2	GARO	KD231, KD232	19203000
PCS	1	3-PHASE SWITCH	CA25B WAA207GK1	KRAUS & NAIMER	D4-M01-S01	19204457
PCS	1	SAFETY SWITCH	KF325/11	KRAUS & NAIMER	D4-M01-Q01	19204102
PCS	2	CABLE GLAND	M25x1,5	N/A		19202961
PCS	1	CABLE GLAND	M20x1,5	N/A		19202962
PCS	1	3-PHASE SWITCH	CA25B WAA207GK1	KRAUS & NAIMER	M34-S01	19150905
PCS	1	SAFETY SWITCH	KF325/11	KRAUS & NAIMER	M34-Q01	19204102
PCS	2	CABLE GLAND	M25x1,5	N/A		19202961
PCS	1	CABLE GLAND	M20x1,5	N/A		19202962
PCS	1	M12 CONNECTOR	P/N 1200700237	MOLEX	X7	19205193
PCS	1	ABSOLUTE ENCODER	F5868.287579	KÜBLER	M34-B01	19204569

ASSA ABLOY

Property of ASSA ABLOY Entrance Systems AB and shall not without our written permission be copied, imparted to a third party or used for any other unauthorized purpose.

GMR Aero Technic Hyderabad

Direct drive | Single motor

Bill of material

Designed	Approved	Location	Code
MED	GO	+A104	84800001

UNIT	QTY	DESC	TYPE	MFG	TAG	CAT
PCS	1	ENCLOSURE	NSYS3D6625P	SCHNEIDER ELECTRIC	A105	19204303
PCS	1	WALL FIXING LUGS	SYAEFPFSC	SCHNEIDER ELECTRIC		19204015
PCS	1	BOTTOM PLATE	KNOCK OUT	N/A		19148752
PCS	20	TERMINAL	WDU 2,5	WEIDMÜLLER	X1:100	19203310
PCS	3	TERMINAL	WDU 6	WEIDMÜLLER	X1:107-109	19203770
PCS	3	TERMINAL	WDU 6	WEIDMÜLLER	X1:113-115	19203770
PCS	8	TERMINAL MARKER	DEK 5 GW X	WEIDMÜLLER		19204030
PCS	8	TERMINAL MARKER	DEK 5 GW 1	WEIDMÜLLER		19204031
PCS	26	TERMINAL MARKER	DEK 5 FWZ 101-126	WEIDMÜLLER		19205205
PCS	29	TERMINAL	WDU 2,5	WEIDMÜLLER	X1:200	19203310
PCS	29	TERMINAL MARKER	DEK 5 FW 201-229	WEIDMÜLLER		19204140
PCS	4	TERMINAL	WDU 2,5	WEIDMÜLLER	X1:300	19203310
PCS	4	TERMINAL MARKER	DEK 5 FW 301-304	WEIDMÜLLER		19204941
PCS	2	TERMINAL	WDU 2,5	WEIDMÜLLER	X1:400	19203310
PCS	2	TERMINAL MARKER	DEK 5 FW 401-402	WEIDMÜLLER		19204142
PCS	4	END BRACKET	WEW 35/2	WEIDMÜLLER		19204029
PCS	2	RELAY	G2R-2-SNI	OMRON	K101-K102	19203730
PCS	2	RELAY SOCKET	DIN 869	OMRON		19203328
PCS	1	POWER SUPPLY	S8VK T12024	OMRON	G01	19204903
PCS	1	PLC	CP1L-EM30DR-D	OMRON	PLC01	19204351
PCS	1	OPTION BOARD	CP1W-CIF11	OMRON	PLC_MOD2	19204352
PCS	1	RJ45 TERMINAL	CIM/RJ45	CAMDENBOSS	X4	19204621
PCS	1	ETHERNET SWITCH	JET NET 2005	BEIJER	X5	19204271
PCS	2	BUS BAR	GV2G354	SCHNEIDER ELECTRIC		19204674
PCS	3	CONTACTOR	LC1D25 BL	SCHNEIDER ELECTRIC	K01-K03	19204489
PCS	3	CONTACTOR	LC1D09 BL	SCHNEIDER ELECTRIC	K05-K07	19204269
PCS	2	CONTACTOR	LC1D09 BL	SCHNEIDER ELECTRIC	K04,K08	19204269
PCS	4	CONTACT BLOCK	LADN11	SCHNEIDER ELECTRIC		19202995
PCS	2	TERMINAL	WDU 2,5	WEIDMÜLLER	X2	19203310
PCS	2	TERMINAL MARKER	DEK 5 GW X	WEIDMÜLLER		19204030
PCS	2	TERMINAL MARKER	DEK 5 GW 2	WEIDMÜLLER		19204478
PCS	2	TERMINAL MARKER	DEK 5 +	WEIDMÜLLER		19204675
PCS	2	TERMINAL MARKER	DEK 5 -	WEIDMÜLLER		19204676
PCS	2	END BRACKET	WEW 35/2	WEIDMÜLLER		19204029
PCS	1	HAND CRANK	Ø28	N/A	S18	19151069
PCS	1	HAND CRANK	Ø24	N/A	S19	19151068

UNIT	QTY	DESC	TYPE	MFG	TAG	CAT
MM	200	PE BAR	JS 75	N/A	PE	19204158
PCS	2	SPACER	-	N/A		19204206
PCS	2	SCREW	MONTB420251	N/A		19204464
MM	1250	DIN RAIL	NS 35/7,5	N/A		19200897
PCS		SCREW	MONTB420131	N/A		19204169
PCS	3	BRACKET	TSTR 5/M5	N/A		19204159
PCS	3	SCREW	MRT-GF 5x12 ZIB	N/A		19201960
MM	1800	CABLE DUCT	25x80 PVC	N/A		19204407
MM	500	CABLE DUCT	40x80 PVC	N/A		19204939
PCS	12	SCREW	MONTB420131	N/A		19204169
		PLACEMENT OF ALL LABELS: REFER TO DRAWING 1835				
PCS	1	LABEL	PE	N/A		19204068
PCS	1	LABEL	EARTH	N/A		19204086
PCS	1	LABEL	DANGER	N/A		19101829
PCS	1	LABEL	CAUTION	N/A		19101952
PCS	8	LABEL	ARROW	N/A		19200182
PCS	1	LABEL	A105	N/A		19205242
PCS	6	CABLE GLAND	M25x1,5	N/A		19202961
PCS	6	LOCK NUT	M25x1,5	N/A		19203396
PCS	16	CABLE GLAND	M16x1,5	N/A		19203314
PCS	16	LOCK NUT	M16x1,5	N/A		19203395
PCS	3	PROXIMITY SWITCH	IGS 277	IFM	D5-L11 - D5-L12, D5-L15	19203948
PCS	1	PROXIMITY SWITCH	IGS 277	IFM	M45-L21	19203948
PCS	1	PROXIMITY SWITCH	IGS 277	IFM	M45-L24	19203948
PCS	2	SIGNAL LIGHT/SIREN	SONL24/O-H	TOLEKA	M45-P01/2	19203722
PCS	2	JUNCTION BOX	UE2	GARO	KD451, KD452	19203000
PCS	1	3-PHASE SWITCH	CA25B WAA207GK1	KRAUS & NAIMER	D5-M01-S01	19204457
PCS	1	SAFETY SWITCH	KF325/11	KRAUS & NAIMER	D5-M01-Q01	19204102
PCS	2	CABLE GLAND	M25x1,5	N/A		19202961
PCS	1	CABLE GLAND	M20x1,5	N/A		19202962
PCS	1	3-PHASE SWITCH	CA25B WAA207GK1	KRAUS & NAIMER	M45-S01	19150905
PCS	1	SAFETY SWITCH	KF325/11	KRAUS & NAIMER	M45-Q01	19204102
PCS	2	CABLE GLAND	M25x1,5	N/A		19202961
PCS	1	CABLE GLAND	M20x1,5	N/A		19202962
PCS	1	M12 CONNECTOR	P/N 1200700237	MOLEX	X7	19205193
PCS	1	ABSOLUTE ENCODER	F5868.287579	KÜBLER	M45-B01	19204569

ASSA ABLOY

Property of ASSA ABLOY Entrance Systems AB and shall not without our written permission be copied, imparted to a third party or used for any other unauthorized purpose.

GMR Aero Technic Hyderabad

Direct drive | Single motor

Bill of material

Designed	Approved	Location	Code
MED	GO	+A105	84800001

Date 221117

Drawing No 60109

Revision --

UNIT	QTY	DESC	TYPE	MFG	TAG	CAT
PCS	1	ENCLOSURE	NSYS3D6525P	SCHNEIDER ELECTRIC	A2	19204653
PCS	1	WALL FIXING LUGS	SYAEFPFSC	SCHNEIDER ELECTRIC		19204015
PCS	1	BOTTOM PLATE	KNOCK OUT	N/A		19148751
PCS	3	TERMINAL	WDU 2,5	WEIDMÜLLER	X1:100	19203310
PCS	6	TERMINAL MARKER	DEK 5 GW X	WEIDMÜLLER		19204030
PCS	6	TERMINAL MARKER	DEK 5 GW 1	WEIDMÜLLER		19204031
PCS	3	TERMINAL MARKER	DEK 5 FWZ 101-103	WEIDMÜLLER		19204033
PCS	4	TERMINAL	WDU 2,5	WEIDMÜLLER	X1:300	19203310
PCS	4	TERMINAL MARKER	DEK 5 FW 301-304	WEIDMÜLLER		19204941
PCS	3	END BRACKET	WEW 35/2	WEIDMÜLLER		19204029
PCS	1	POWER SUPPLY	S8VK T12024	OMRON	G01	19204903
PCS	1	PLC	CP1L-EM30DR-D	OMRON	PLC01	19204351
PCS	1	HMI	NB10W-TW01B	OMRON	HMI01	19204488
PCS	1	SAFETY RELAY	G9SB-3012-A	OMRON	K100	19204904
PCS	1	ETHERNET SWITCH	JET NET 2005	BEIJER	X5	19204271
PCS	1	PUSH BUTTON	ZB4BA334	SCHNEIDER ELECTRIC	S01	19203365
PCS	1	CONTACT BLOCK	ZB4BZ101	SCHNEIDER ELECTRIC		19203364
PCS	1	PUSH BUTTON	ZB4BA232	SCHNEIDER ELECTRIC	S02	19201807
PCS	1	CONTACT BLOCK	ZB4BZ102	SCHNEIDER ELECTRIC		19203005
PCS	1	PUSH BUTTON	ZB4BA334	SCHNEIDER ELECTRIC	S03	19203365
PCS	1	CONTACT BLOCK	ZB4BZ105	SCHNEIDER ELECTRIC		19204482
PCS	1	SWITCH HEAD KEY	ZB4BG6	SCHNEIDER ELECTRIC	S04	19203779
PCS	1	CONTACT BLOCK	ZB4BZ101	SCHNEIDER ELECTRIC		19203364
PCS	1	EMRG STOP	ZB4BS844	SCHNEIDER ELECTRIC	S100	19201805
PCS	1	CONTACT BLOCK	ZB4BZ104	SCHNEIDER ELECTRIC		19204481
PCS	1	USB MEMORY	16GB	NA	-	19205066

UNIT	QTY	DESC	TYPE	MFG	TAG	CAT
MM	200	PE BAR	JS 75	N/A	PE	19204158
PCS	2	SPACER	-	N/A		19204206
PCS	2	SCREW	MONTB420251	N/A		19204464
MM	1250	DIN RAIL	NS 35/7,5	N/A		19200897
PCS		SCREW	MONTB420131	N/A		19204169
PCS	3	BRACKET	TSTR 5/M5	N/A		19204159
PCS	3	SCREW	MRT-GF 5x12 ZIB	N/A		19201960
MM	1985	CABLE DUCT	25x80 PVC	N/A		19204407
PCS	12	SCREW	MONTB420131	N/A		19204169
MM	1000	SPIRAL HOSE	20 MM	N/A		19204265
PCS	4	CABLE TIE ATTACHMENT	ABM2S-A-D	N/A		19204037
PCS	4	CABLE TIE	2,5x142	N/A		19204011
		PLACEMENT OF ALL LABELS: REFER TO DRAWING 1835				
PCS	1	LABEL	ALARM	N/A		19204134
PCS	1	LABEL	YELLOW	N/A		19204087
PCS	1	LABEL	PE	N/A		19204068
PCS	1	LABEL	EARTH	N/A		19204086
PCS	1	LABEL	ASSEMBLY	N/A		19101834
PCS	1	LABEL	ASSEMBLY	N/A		19150549
PCS	1	LABEL	EMERGENCY	N/A		19101951
PCS	1	LABEL	DANGER	N/A		19101829
PCS	1	LABEL	EMERGENCY OPERATION	N/A		-
PCS	1	LABEL	CAUTION	N/A		19101952
PCS	1	LABEL	ID CEN	N/A		19146229
PCS	1	LABEL	ASSA ABLOY	N/A		19204680
PCS	1	LABEL	A2	N/A		19204400
PCS	1	CABLE GLAND	M25x1,5	N/A		19202961
PCS	1	LOCK NUT	M25x1,5	N/A		19203396
PCS	0	CABLE GLAND	M20x1,5	N/A		19202962
PCS	0	LOCK NUT	M20x1,5	N/A		19203059
PCS	2	CABLE GLAND	M16x1,5	N/A		19203314
PCS	2	LOCK NUT	M16x1,5	N/A		19203395

ASSA ABLOY

Property of ASSA ABLOY Entrance Systems AB and shall not without our written permission be copied, imparted to a third party or used for any other unauthorized purpose.

GMR Aero Technic Hyderabad

Direct drive | Single motor

Bill of material

Designed	Approved	Location	Code
MED	GO	+A2	84800001

Date 221117

Drawing No 60109

Revision C

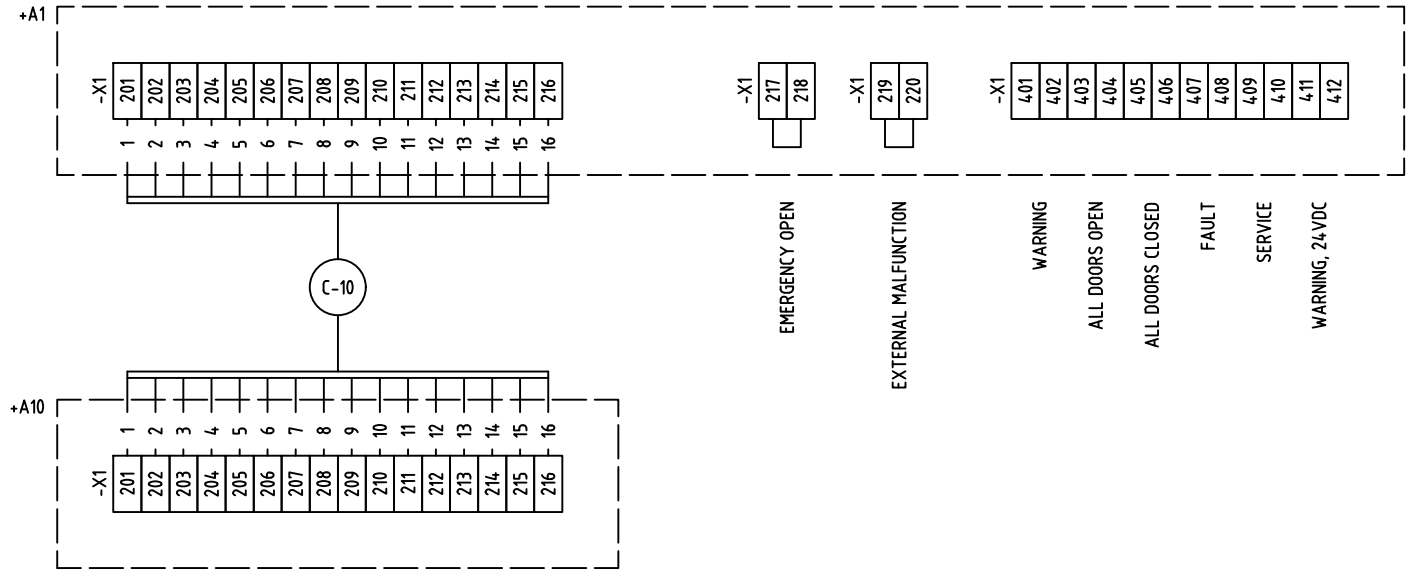

ASSA ABLOY

Property of ASSA ABLOY Entrance Systems AB and shall not without our written permission be copied, imparted to a third party or used for any other unauthorized purpose.

GMR Aero Technic Hyderabad

Direct drive | Single motor

External connections

Designed	Approved	Location	Code	Page	Date	Drawing No	Revision
MED	GO		84800001	33/45	221117	60109	--

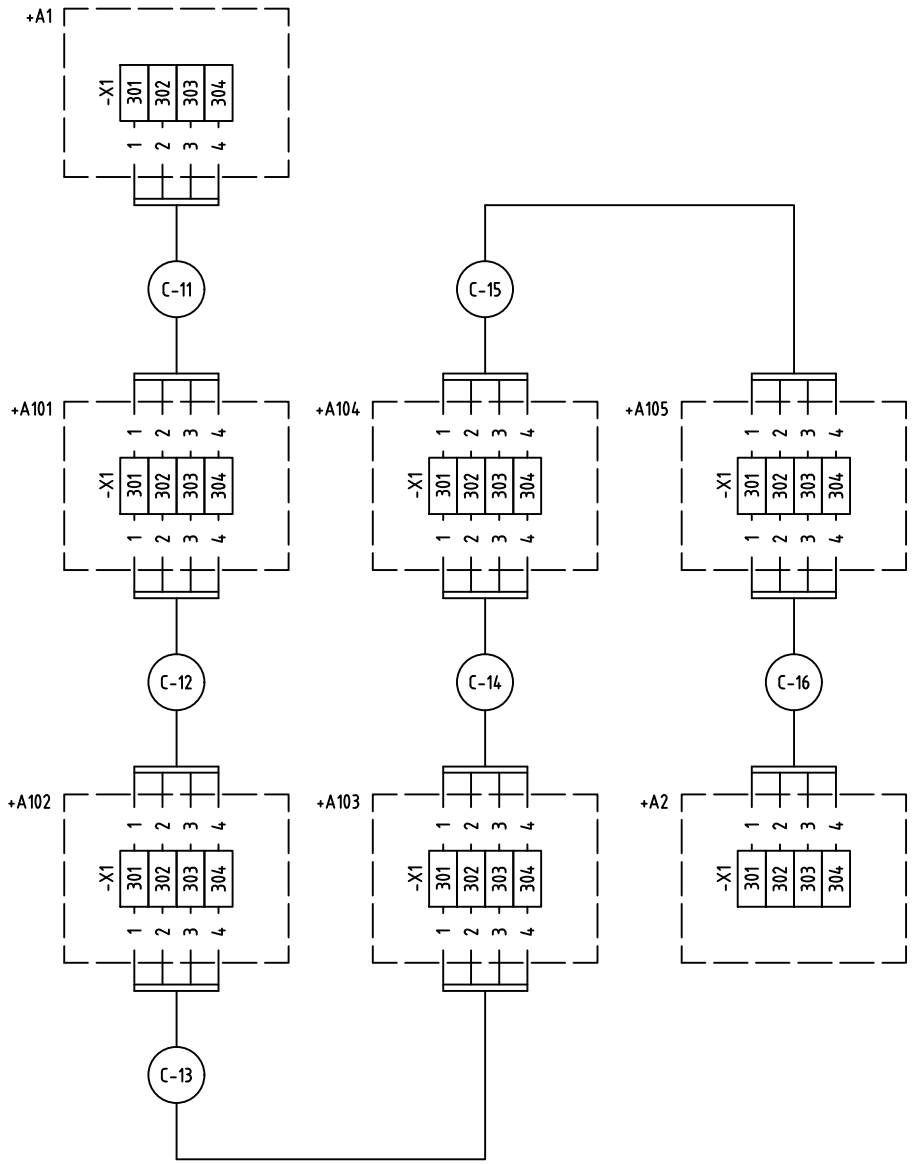

Property of ASSA ABLOY Entrance Systems AB and shall not without our written permission be copied, imparted to a third party or used for any other unauthorized purpose.

ASSA ABLOY

GMR Aero Technic Hyderabad

Direct drive | Single motor

External connections / Safety circuit

Designed	Approved	Location	Code	Page	Date	Drawing No	Revision
MED	GO		84800001	34/45	221117	60109	--

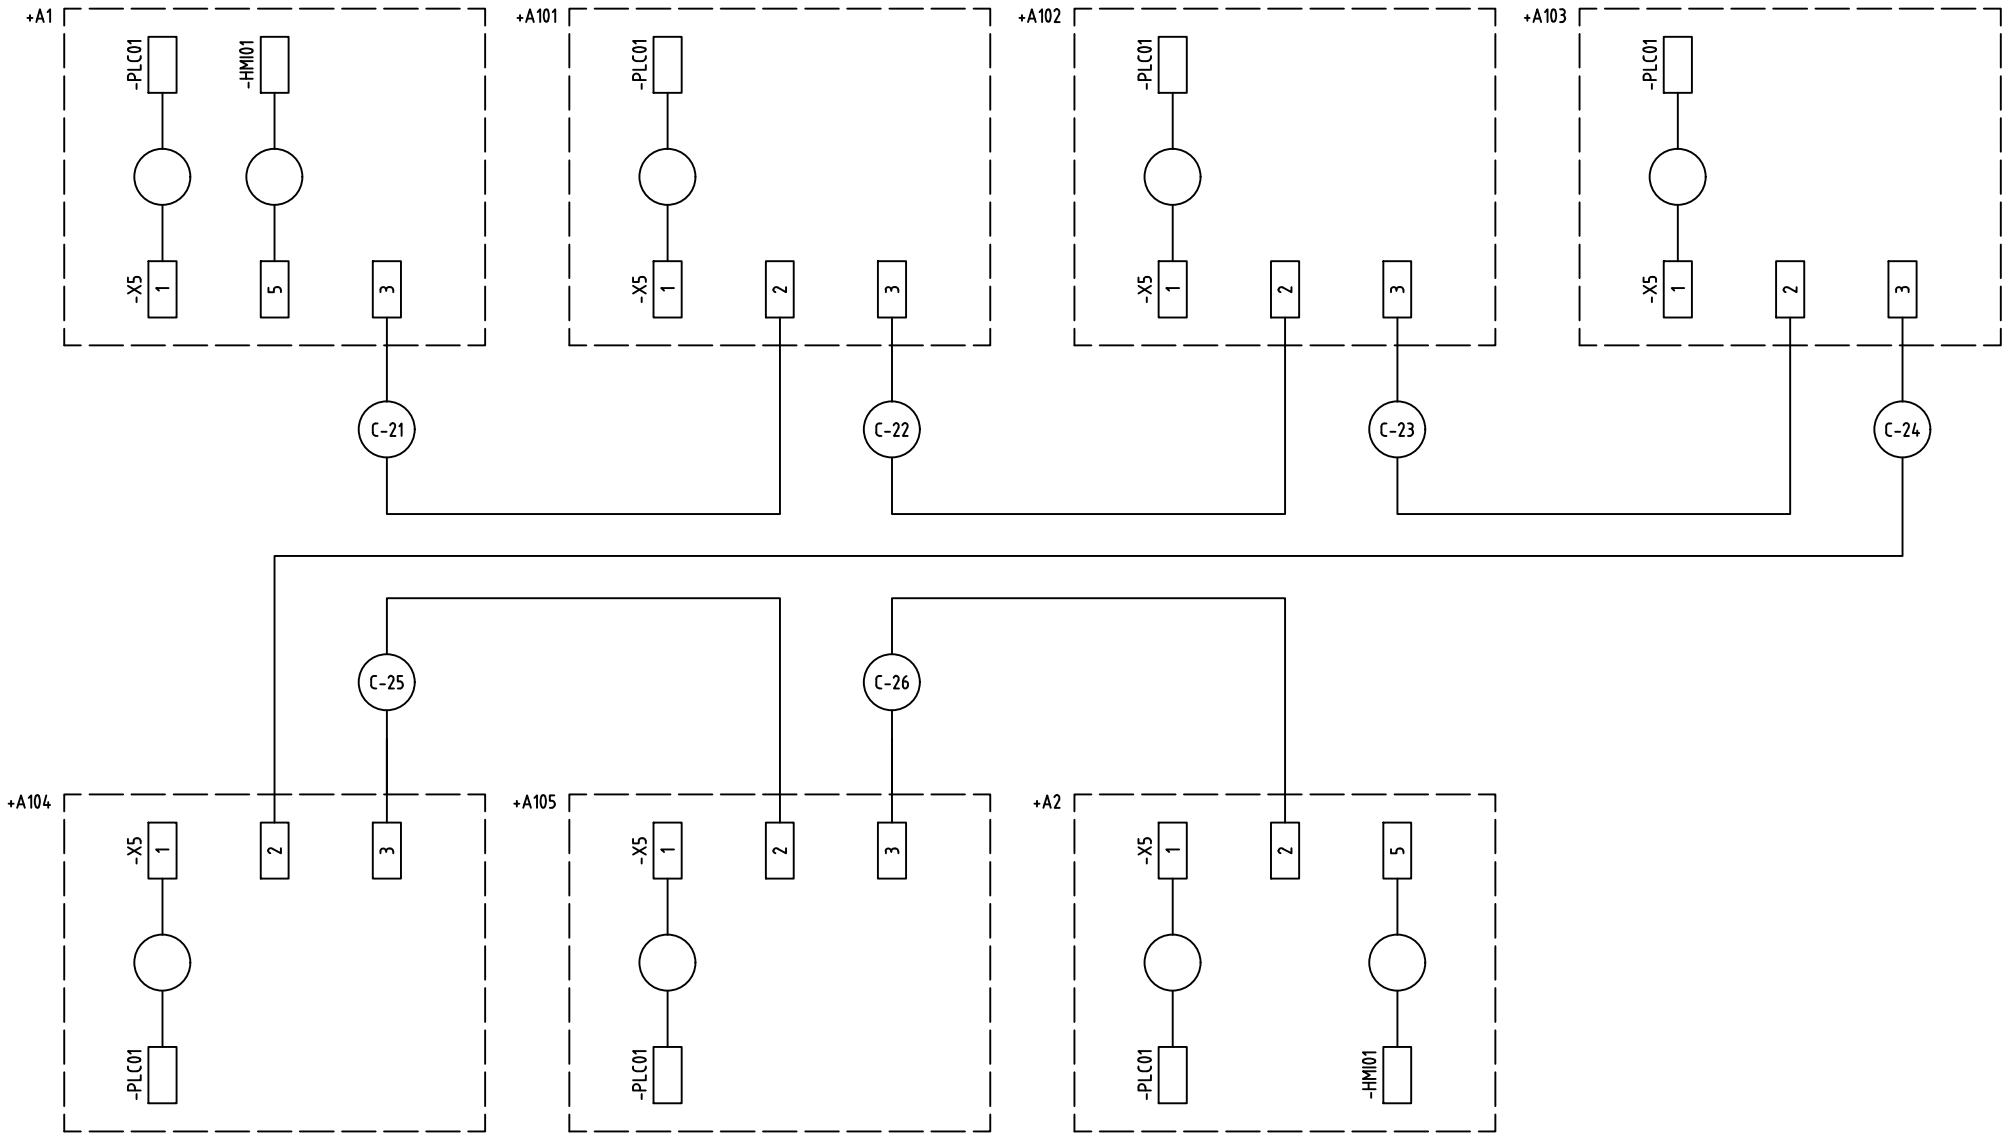

CAT 5 CONNECTORS							
1	2	3	4	5	6	7	8
OG/WH	OG	GN/WH	BU	BU/WH	GN	BN/WH	BN

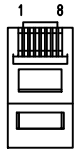

ASSA ABLOY

Property of ASSA ABLOY Entrance Systems AB and shall not without our written permission be copied, imparted to a third party or used for any other unauthorized purpose.

GMR Aero Technic Hyderabad

Direct drive | Single motor

External connections / Communication network

Designed	Approved	Location	Code
MED	GO		84800001

Page	Date	Drawing No	Revision
35/45	221117	60109	--

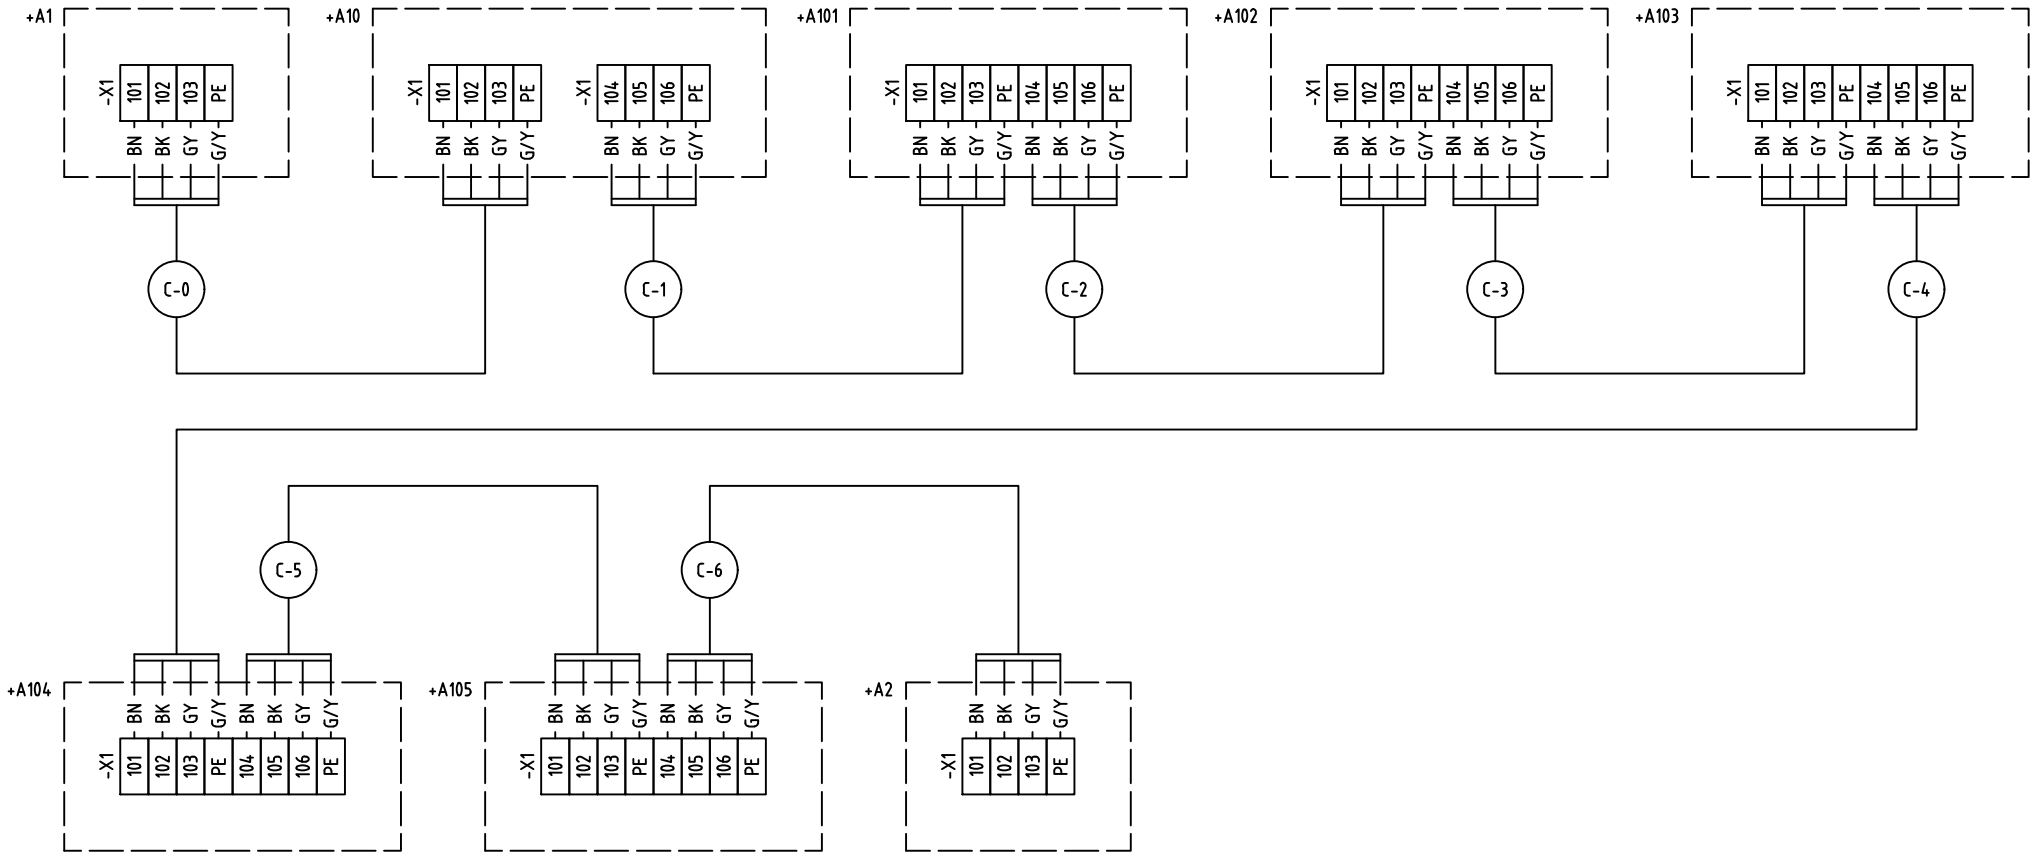

ASSA ABLOY

Property of ASSA ABLOY Entrance Systems AB and shall not without our written permission be copied, imparted to a third party or used for any other unauthorized purpose.

GMR Aero Technic Hyderabad

Direct drive | Single motor

External connections

Designed	Approved	Location	Code	Revision
MED	GO		84800001	--

Page 36/45

Date 221117

Drawing No 60109

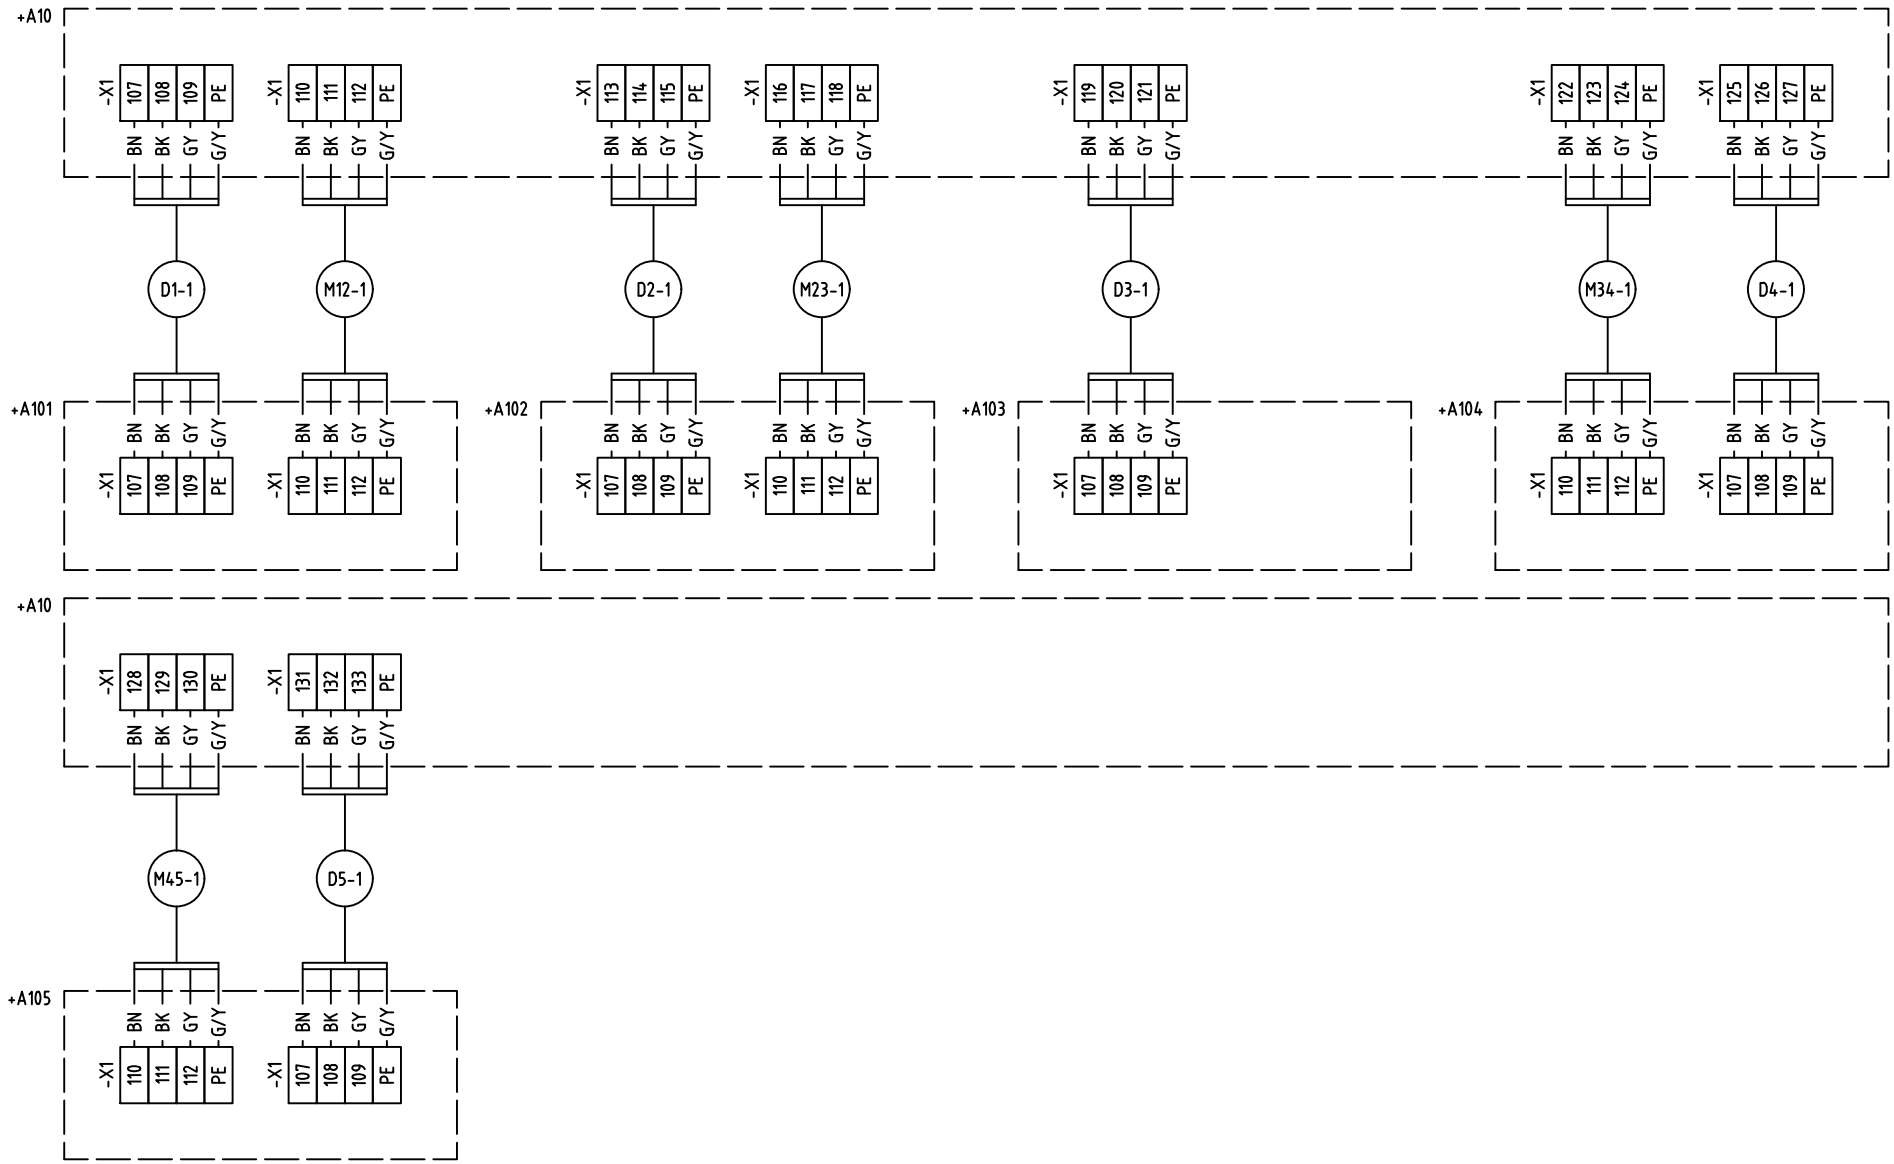

ASSA ABLOY

Property of ASSA ABLOY Entrance Systems AB and shall not without our written permission be copied, imparted to a third party or used for any other unauthorized purpose.

GMR Aero Technic Hyderabad

Direct drive | Single motor

External connections

Designed	Approved	Location	Code
MED	GO		84800001

Page 37/45

Date 221117

Drawing No 60109

Revision --

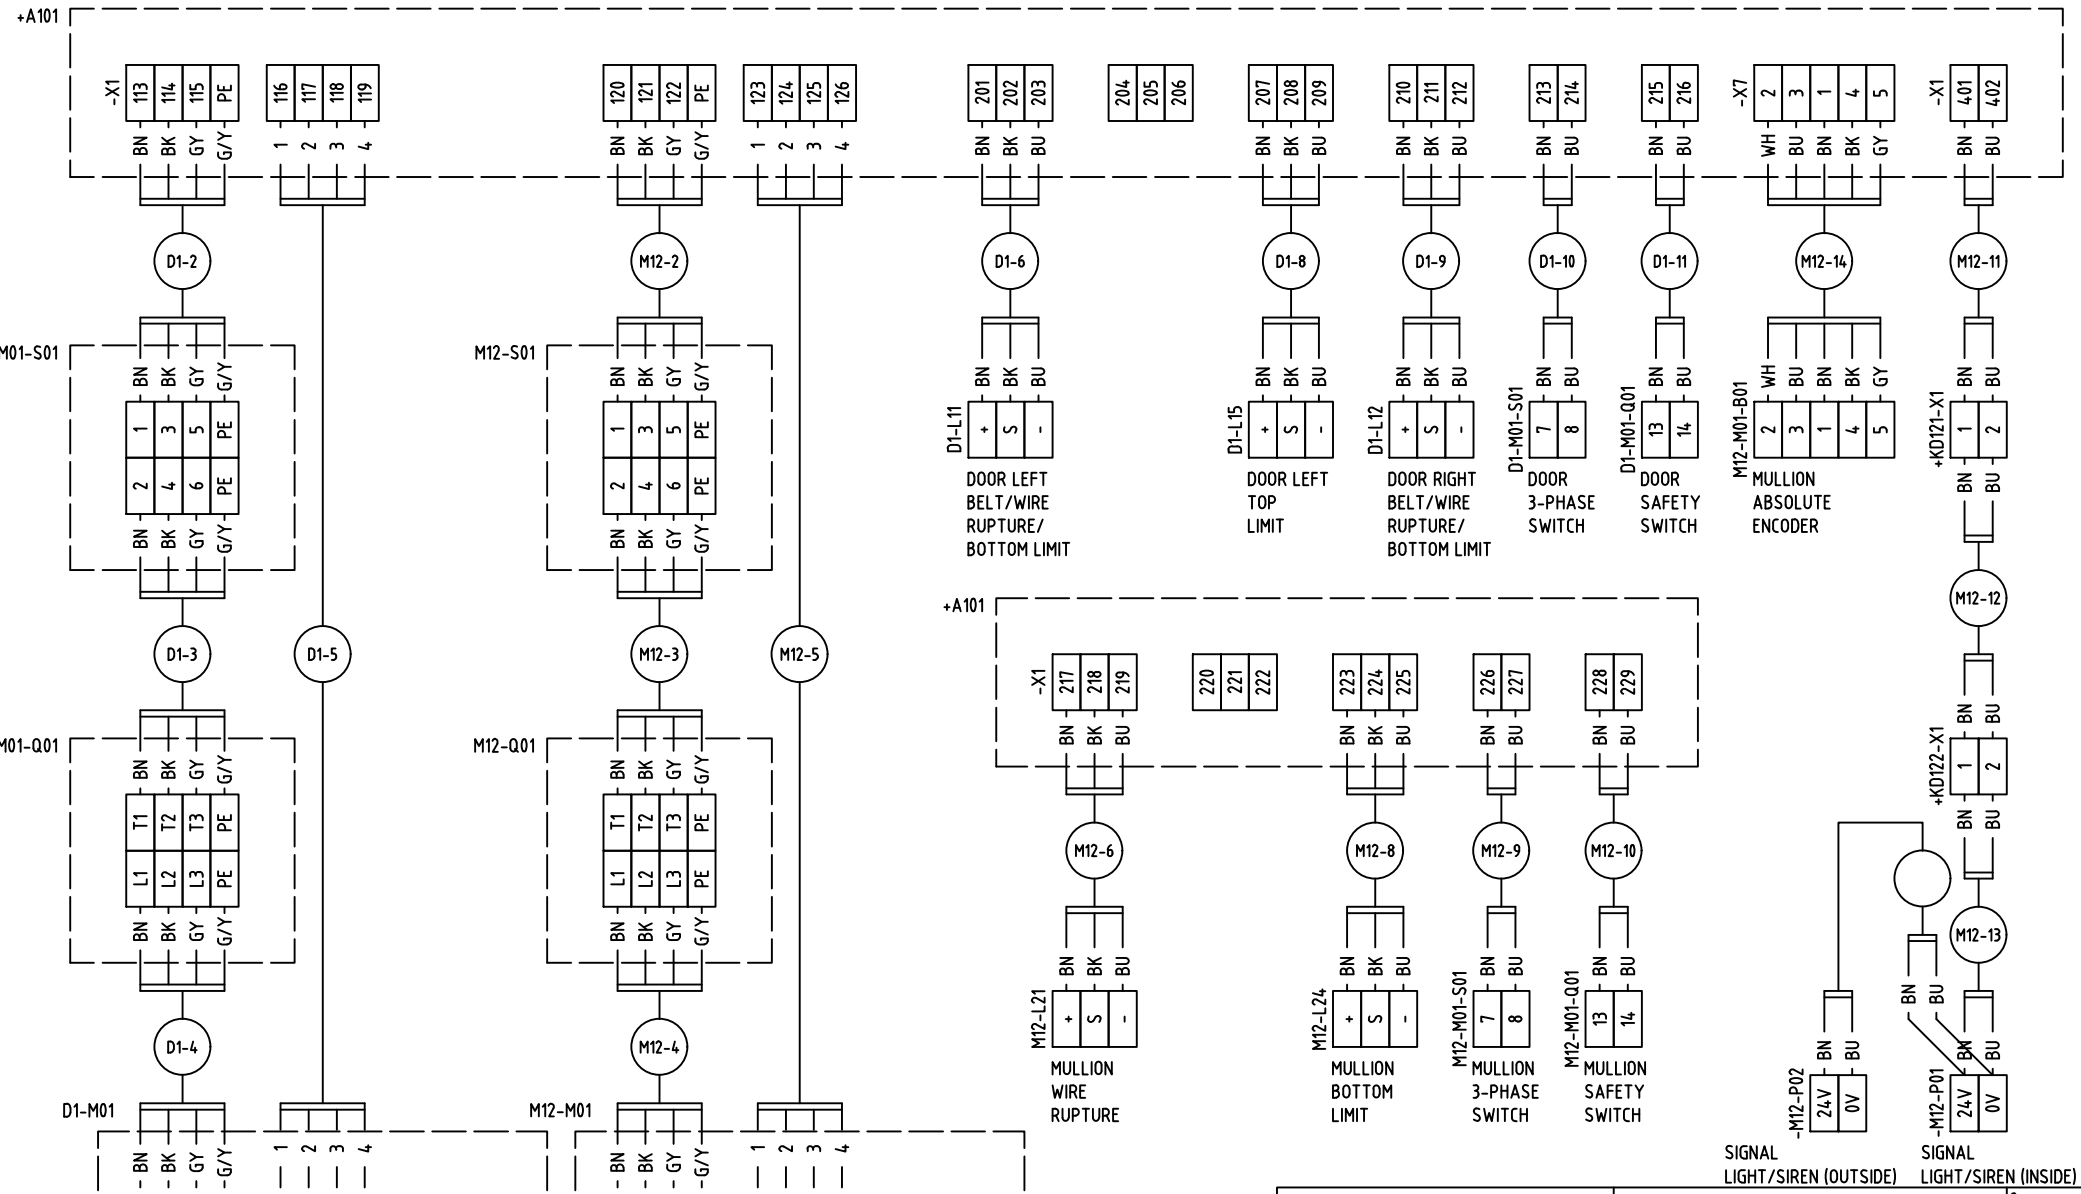

Property of ASSA ABLOY Entrance Systems AB and shall not without our written permission be copied, imparted to a third party or used for any other unauthorized purpose.

ASSA ABLOY

GMR Aero Technic Hyderabad

Direct drive | Single motor

External connections

Page	Date	Drawing No	Revision
38/45	221117	60109	--

Designed	Approved	Location	Code
MED	GO	+A101	84800001

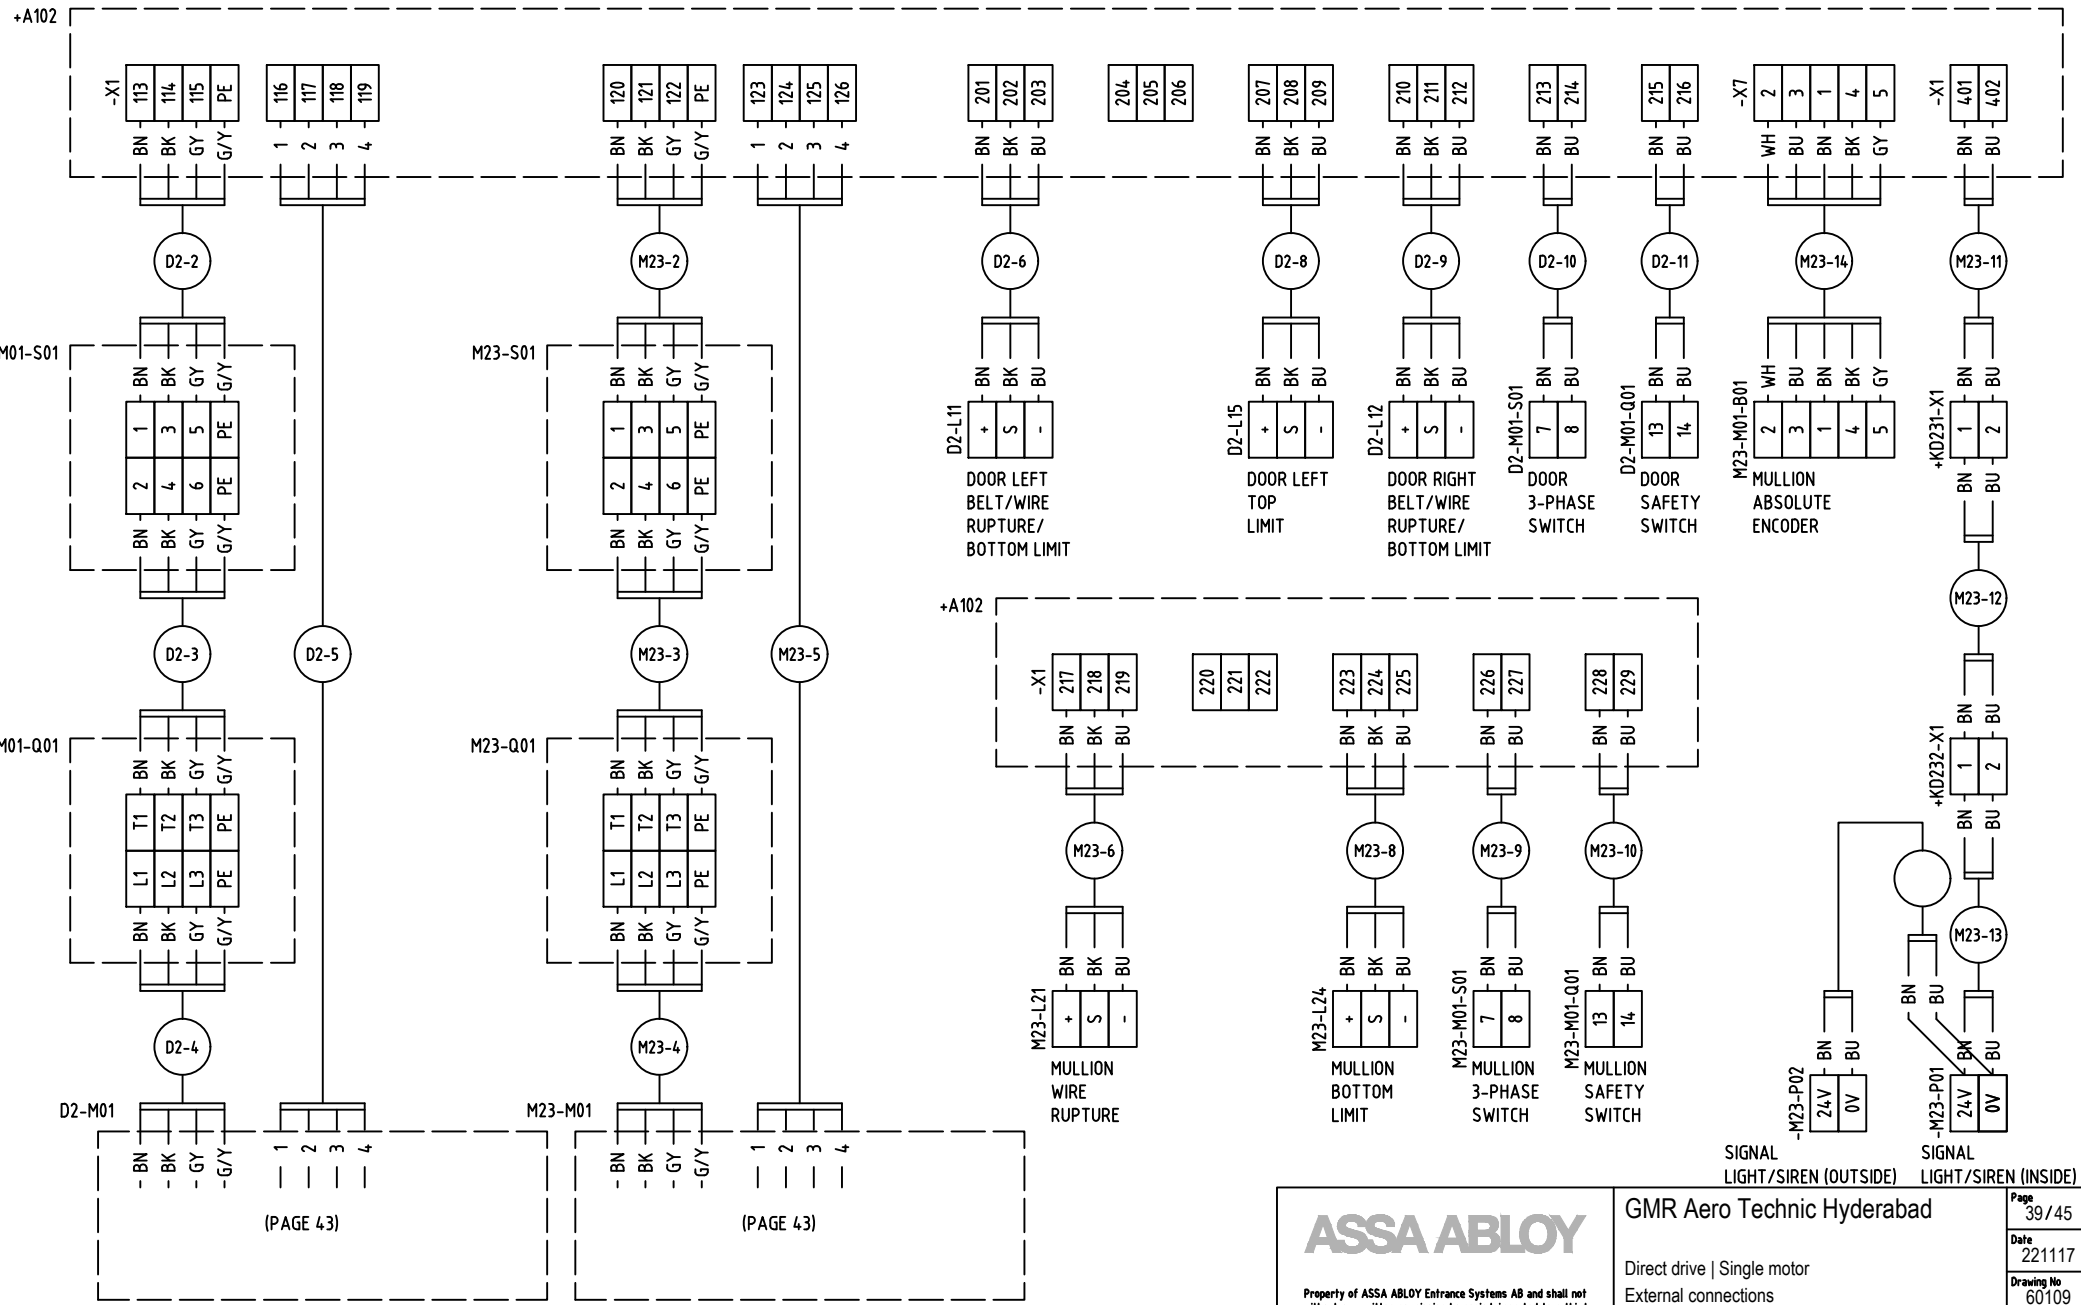

Property of ASSA ABLOY Entrance Systems AB and shall not without our written permission be copied, imparted to a third party or used for any other unauthorized purpose.

ASSA ABLOY

GMR Aero Technic Hyderabad

Direct drive | Single motor

External connections

Designed	Approved	Location	Code	Page	Date	Drawing No	Revision
MED	GO	+A102	84800001	39/45	221117	60109	--

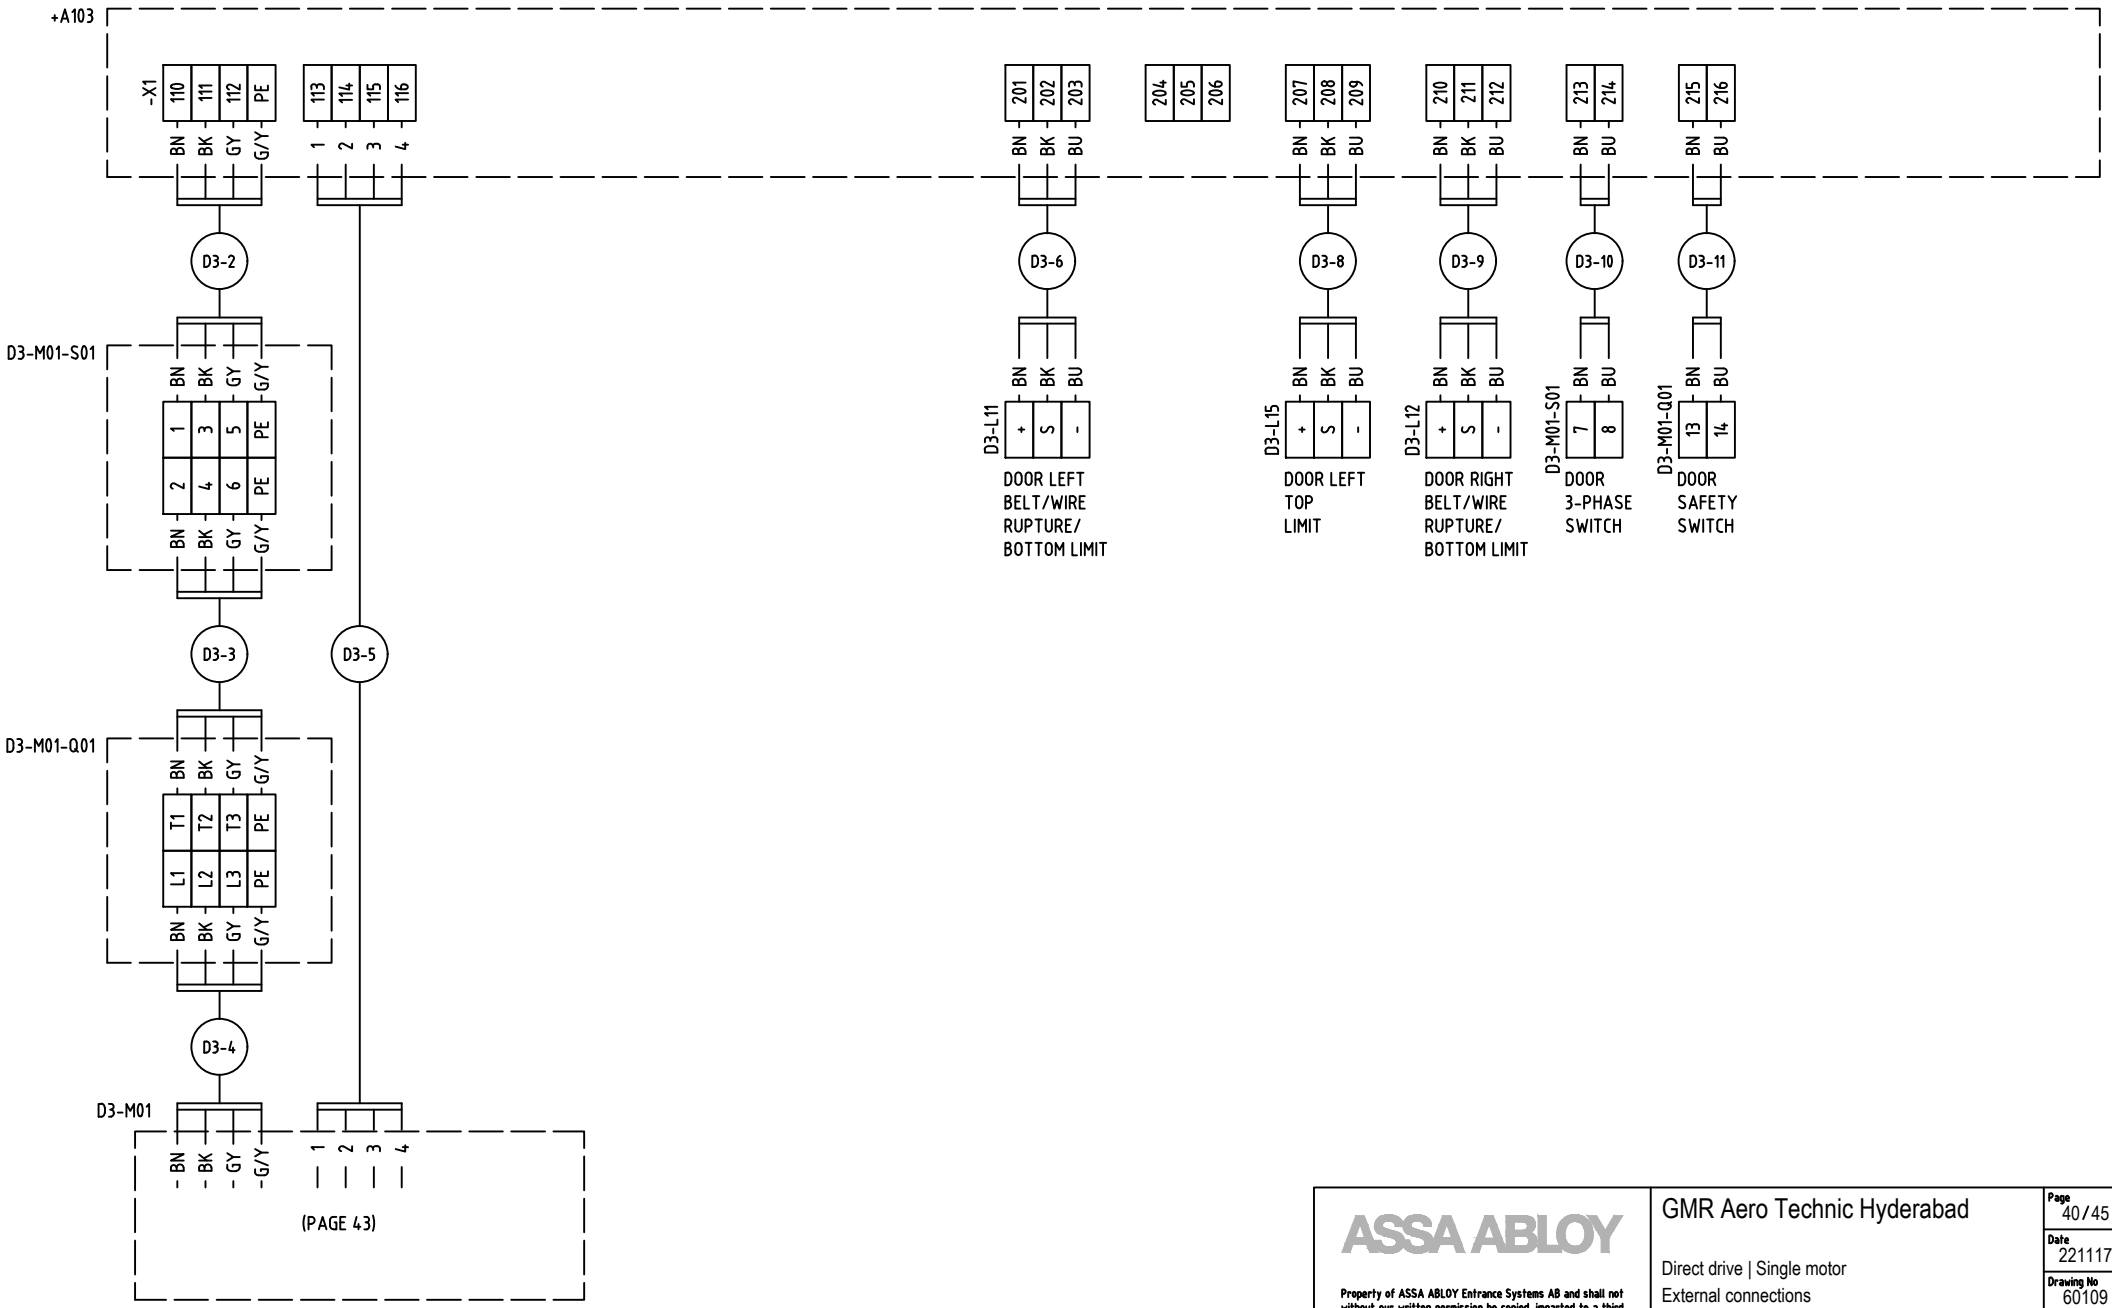

ASSA ABLOY

Property of ASSA ABLOY Entrance Systems AB and shall not without our written permission be copied, imparted to a third party or used for any other unauthorized purpose.

GMR Aero Technic Hyderabad

Direct drive | Single motor

External connections

Designed	Approved	Location	Code
MED	GO	+A103	84800001

Page 40/45

Date 221117

Drawing No 60109

Revision --

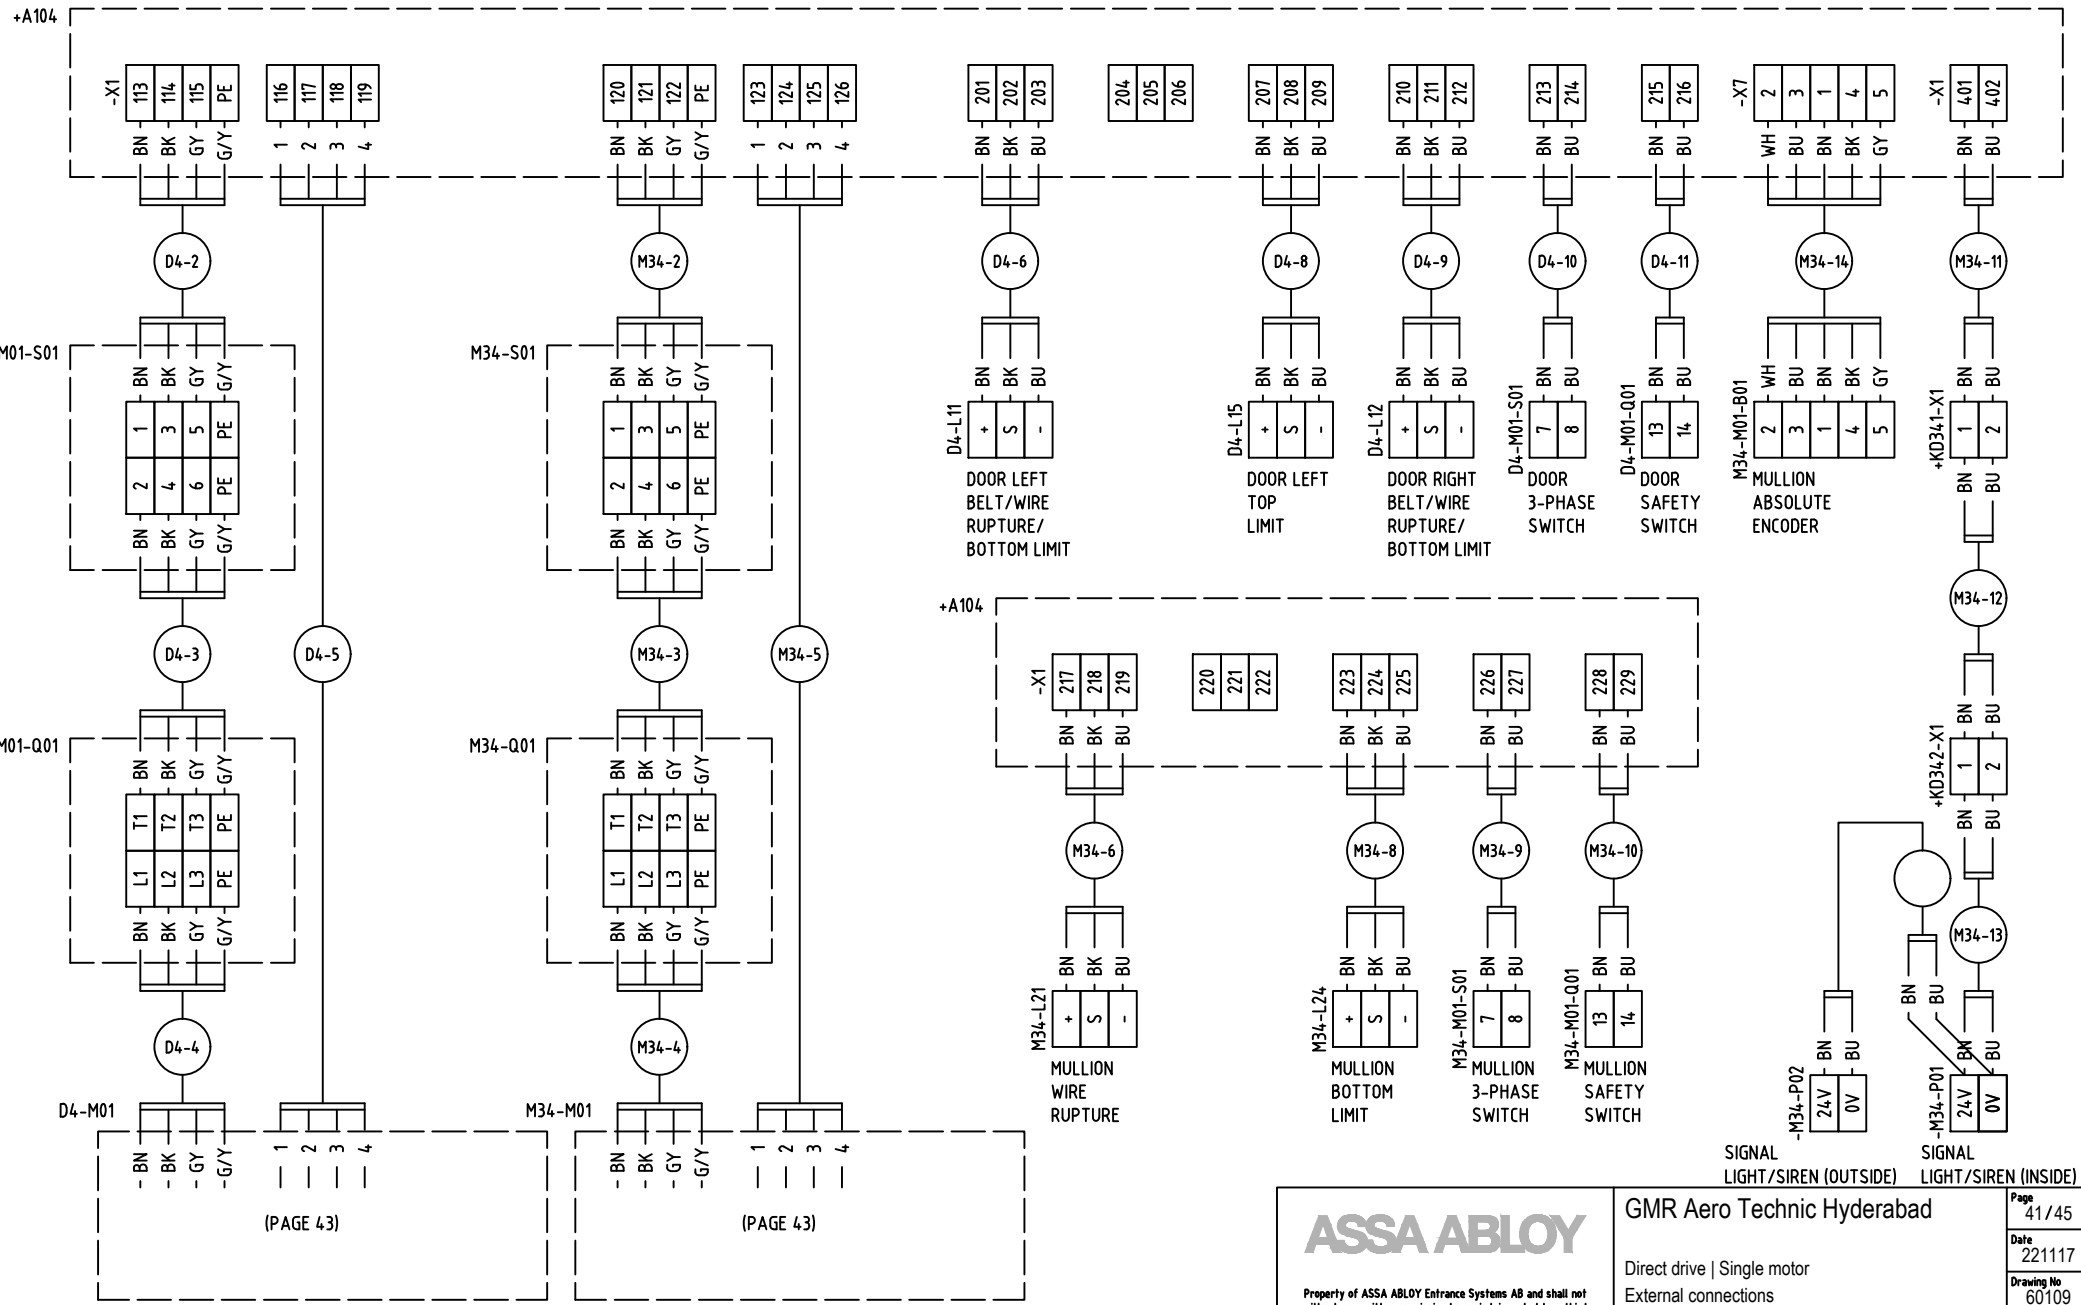

ASSA ABLOY

Property of ASSA ABLOY Entrance Systems AB and shall not without our written permission be copied, imparted to a third party or used for any other unauthorized purpose.

GMR Aero Technic Hyderabad

Direct drive | Single motor

External connections

Designed	Approved	Location	Code	Revision
MED	GO	+A104	84800001	--

Page 41/45

Date 221117

Drawing No 60109

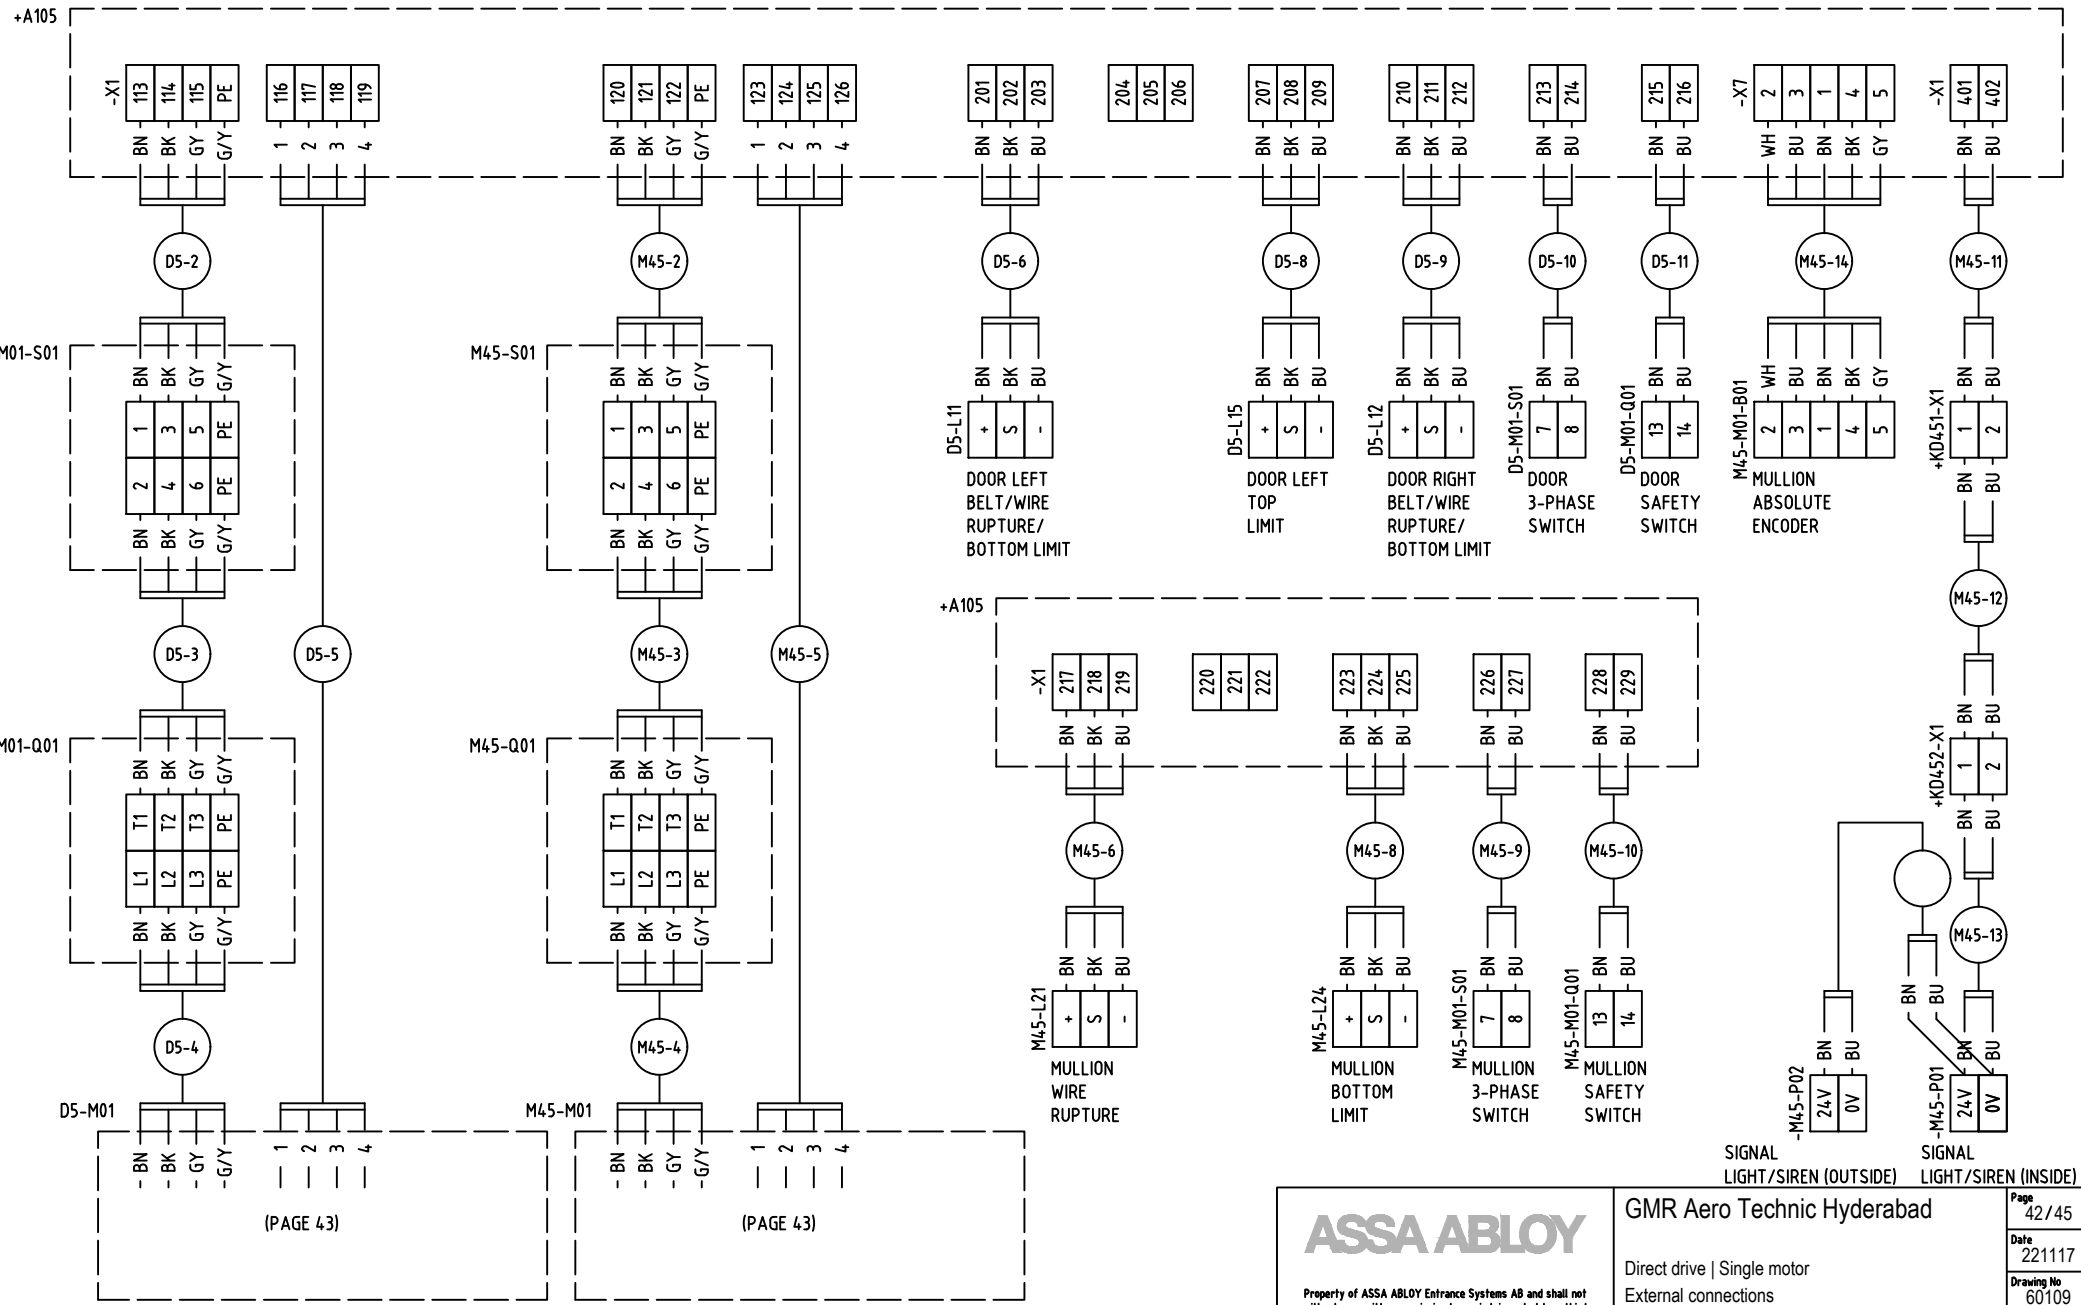

ASSA ABLOY

Property of ASSA ABLOY Entrance Systems AB and shall not without our written permission be copied, imparted to a third party or used for any other unauthorized purpose.

GMR Aero Technic Hyderabad

Direct drive | Single motor

External connections

Designed	Approved	Location	Code	Page	Date	Drawing No	Revision
MED	GO	+A105	84800001	42/45	221117	60109	--

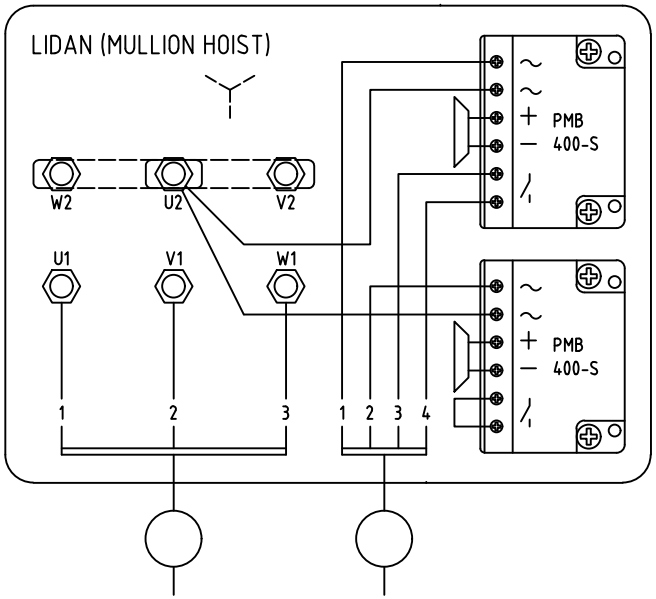

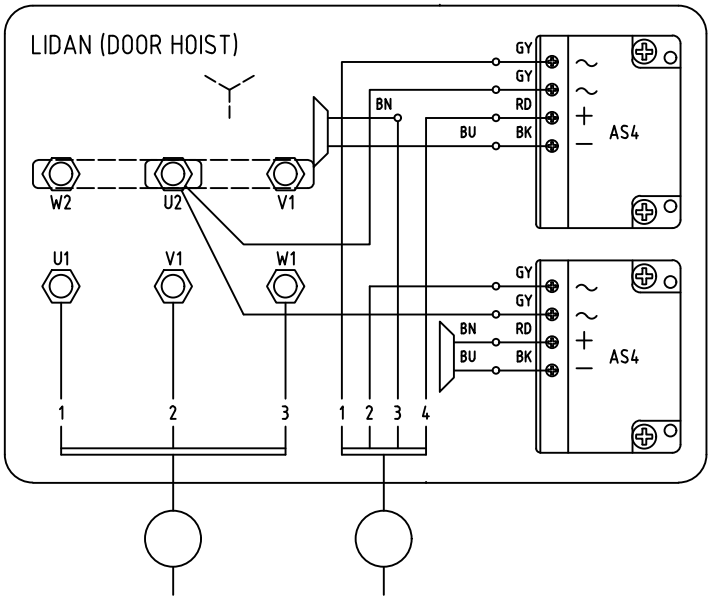

Property of ASSA ABLOY Entrance Systems AB and shall not without our written permission be copied, imparted to a third party or used for any other unauthorized purpose.

GMR Aero Technic Hyderabad

Direct drive | Single motor

Motor connection

Designed	Approved	Location	Code	Page	Date	Drawing No	Revision
MED	GO		84800001	43/45	221117	60109	--

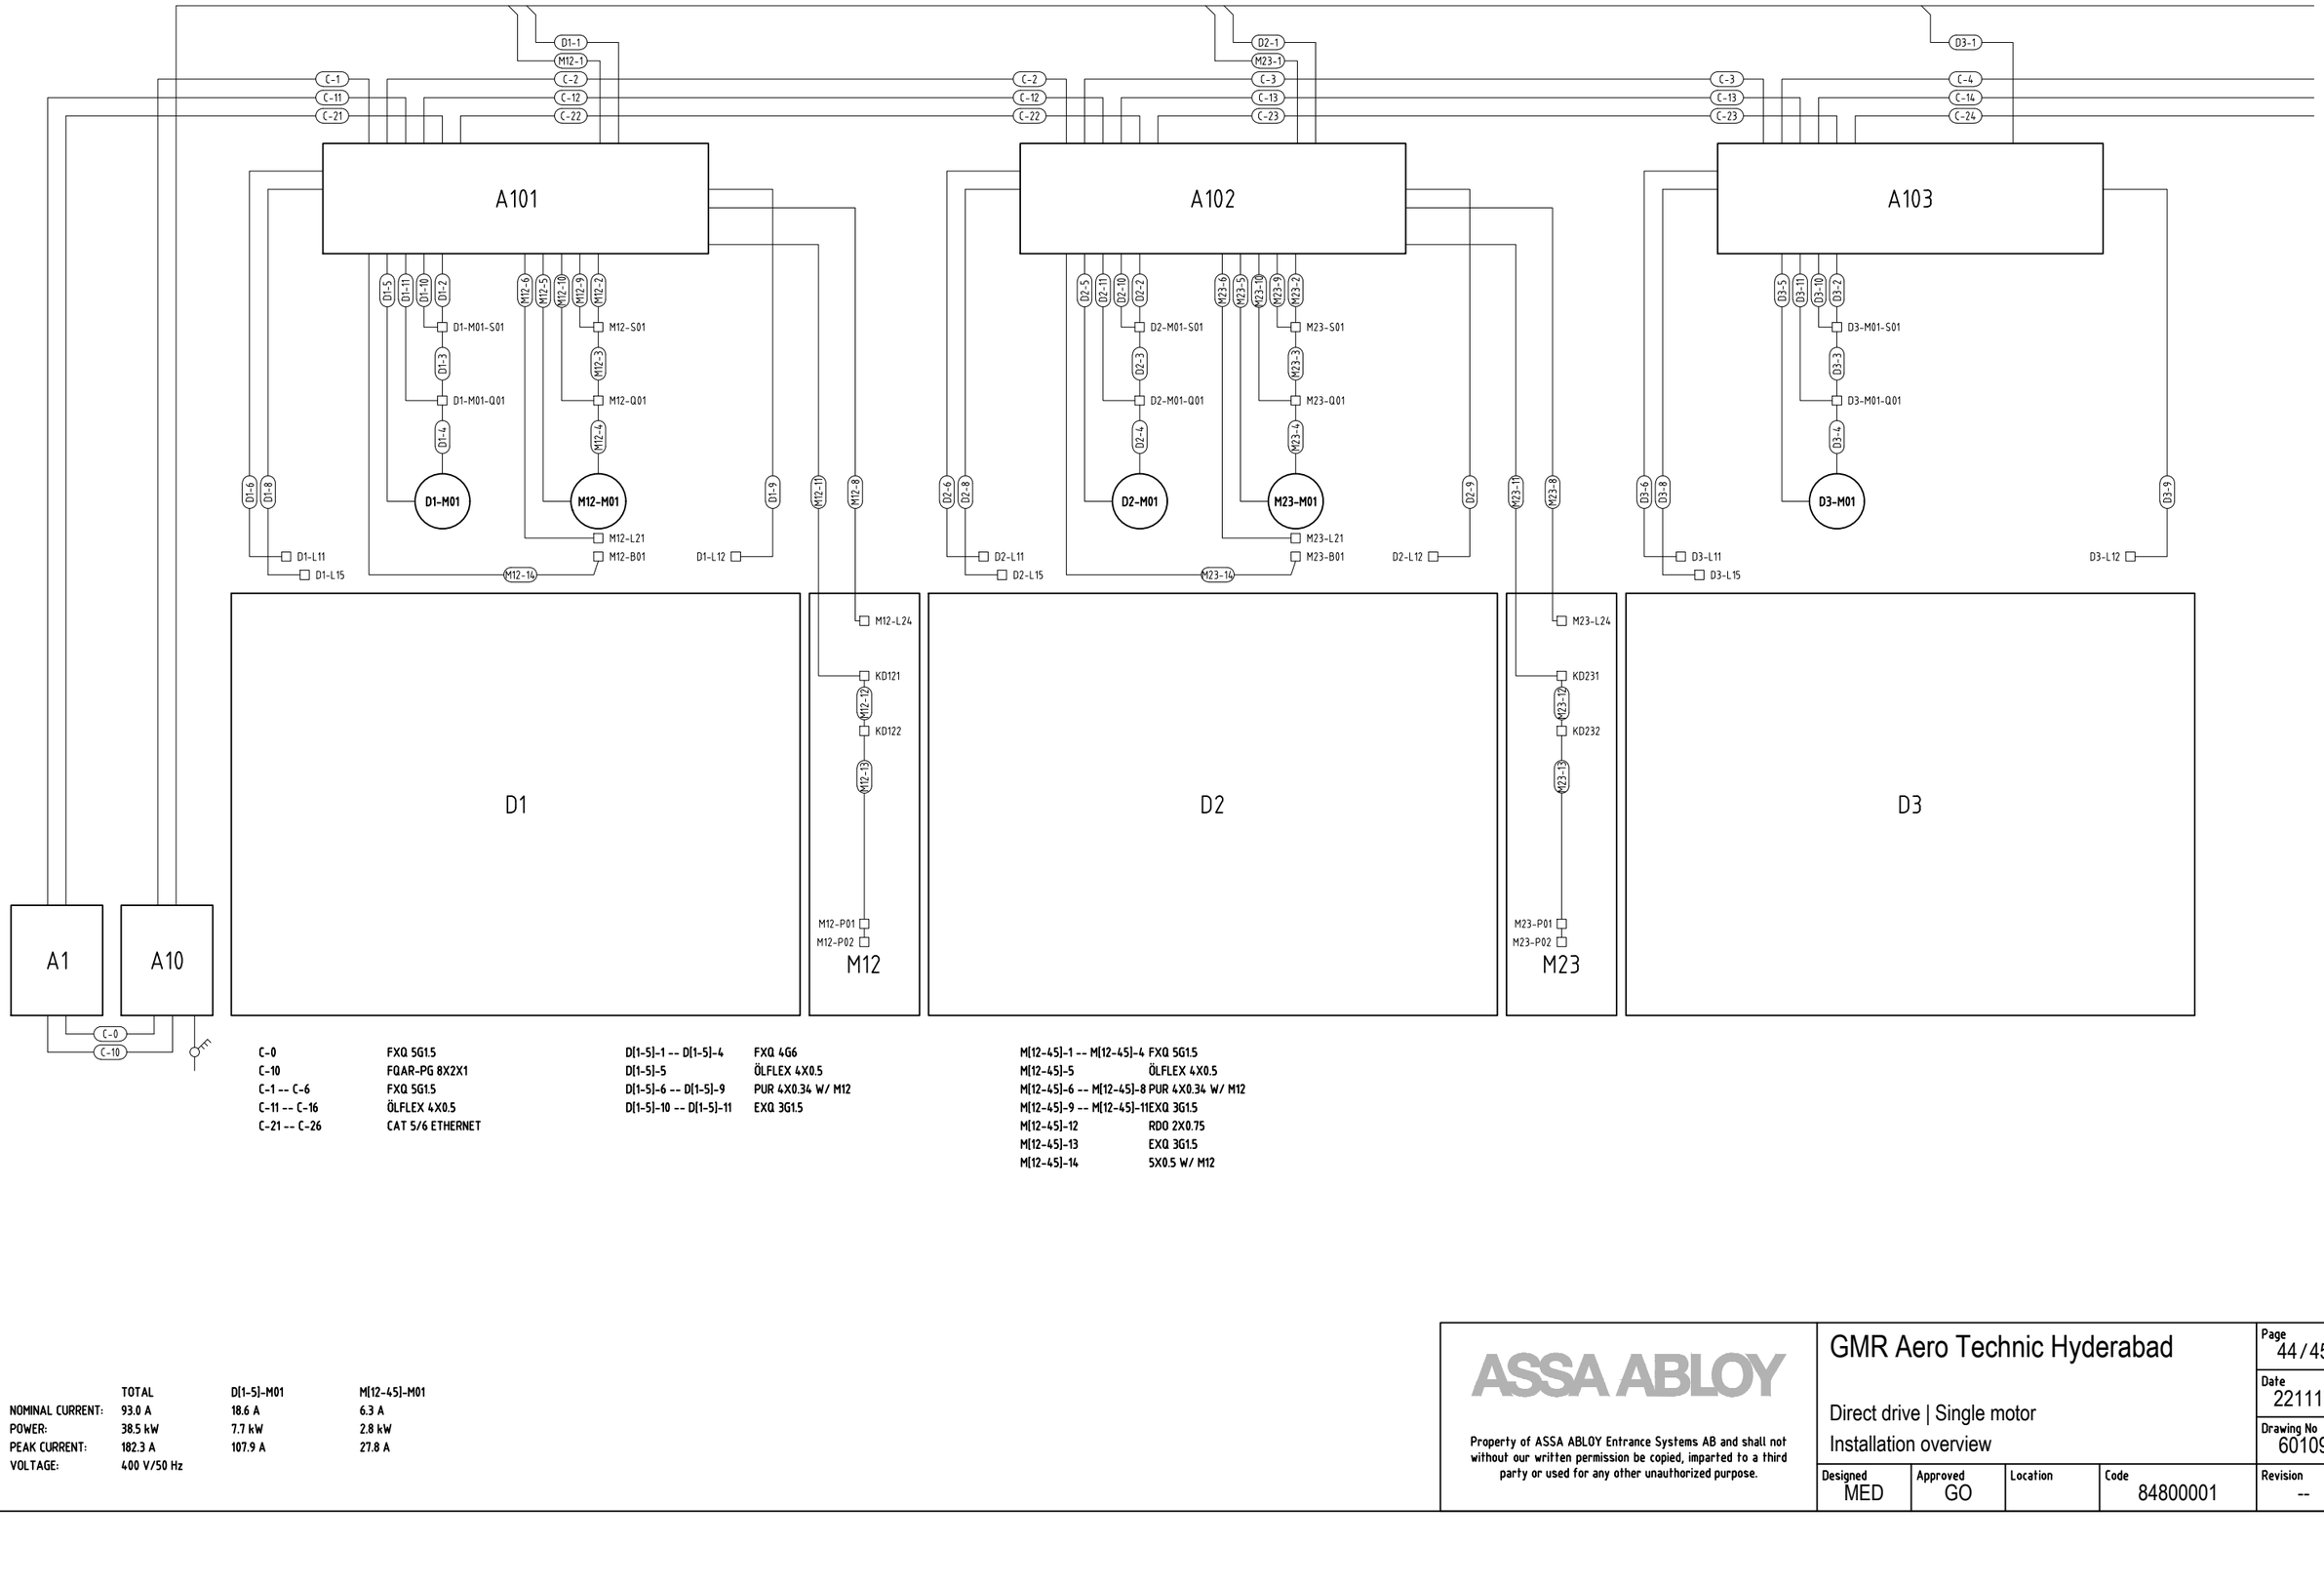

C-0	FXQ 5G1.5	D[1-5]-1 -- D[1-5]-4	FXQ 4G6
C-10	FQAR-PG 8X2X1	D[1-5]-5	ÖLFLEX 4X0.5
C-1 -- C-6	FXQ 5G1.5	D[1-5]-6 -- D[1-5]-9	PUR 4X0.34 W/ M12
C-11 -- C-16	ÖLFLEX 4X0.5	D[1-5]-10 -- D[1-5]-11	EXQ 3G1.5
C-21 -- C-26	CAT 5/6 ETHERNET		

M[12-45]-1 -- M[12-45]-4	FXQ 5G1.5
M[12-45]-5	ÖLFLEX 4X0.5
M[12-45]-6 -- M[12-45]-8	PUR 4X0.34 W/ M12
M[12-45]-9 -- M[12-45]-11	EXQ 3G1.5
M[12-45]-12	RDO 2X0.75
M[12-45]-13	EXQ 3G1.5
M[12-45]-14	5X0.5 W/ M12

	TOTAL	D[1-5]-M01	M[12-45]-M01
NOMINAL CURRENT:	93.0 A	18.6 A	6.3 A
POWER:	38.5 kW	7.7 kW	2.8 kW
PEAK CURRENT:	182.3 A	107.9 A	27.8 A
VOLTAGE:	400 V/50 Hz		

ASSA ABLOY

Property of ASSA ABLOY Entrance Systems AB and shall not without our written permission be copied, imparted to a third party or used for any other unauthorized purpose.

GMR Aero Technic Hyderabad

Direct drive | Single motor

Installation overview

Designed	Approved	Location	Code	Page	Date	Drawing No	Revision
MED	GO		84800001	44 / 45	221117	60109	--

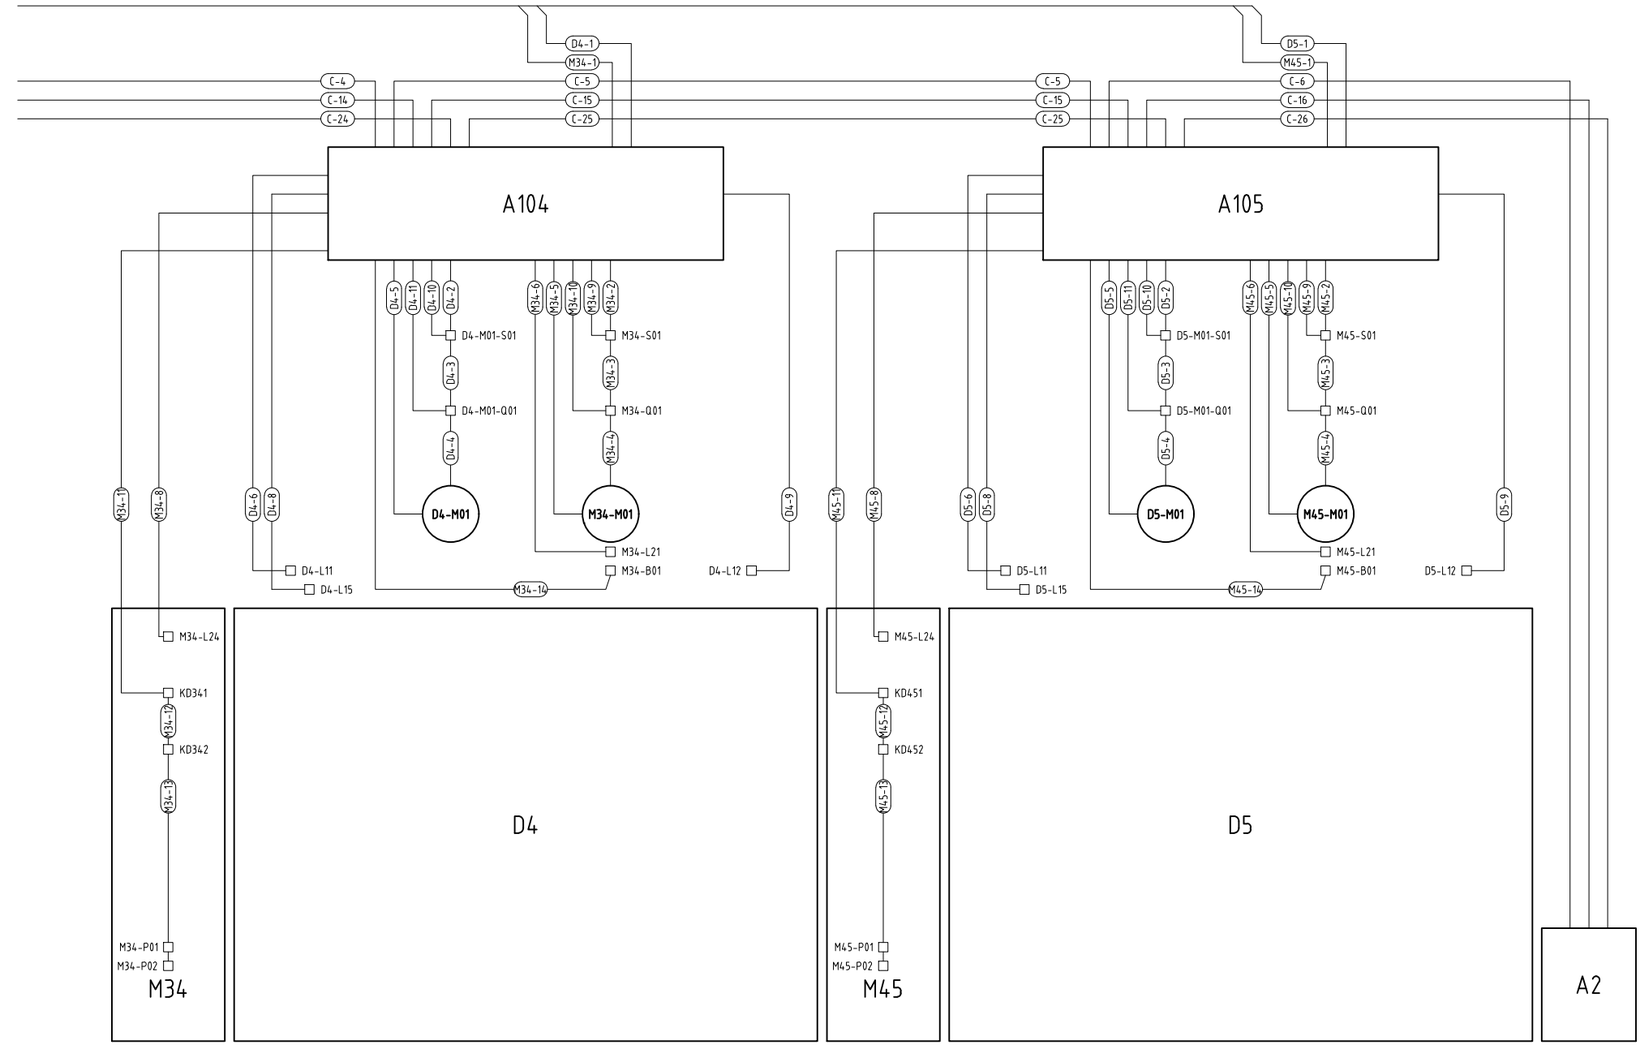

C-0	FXQ 5G1.5	D[1-5]-1 -- D[1-5]-4	FXQ 4G6
C-10	FQAR-PG 8X2X1	D[1-5]-5	ÖLFLEX 4X0.5
C-1 -- C-6	FXQ 5G1.5	D[1-5]-6 -- D[1-5]-9	PUR 4X0.34 W/ M12
C-11 -- C-16	ÖLFLEX 4X0.5	D[1-5]-10 -- D[1-5]-11	EXQ 3G1.5
C-21 -- C-26	CAT 5/6 ETHERNET		

M[12-45]-1 -- M[12-45]-4	FXQ 5G1.5
M[12-45]-5	ÖLFLEX 4X0.5
M[12-45]-6 -- M[12-45]-8	PUR 4X0.34 W/ M12
M[12-45]-9 -- M[12-45]-11	EXQ 3G1.5
M[12-45]-12	RDO 2X0.75
M[12-45]-13	EXQ 3G1.5
M[12-45]-14	5X0.5 W/ M12

	TOTAL	D[1-5]-M01	M[12-45]-M01
NOMINAL CURRENT:	93.0 A	18.6 A	6.3 A
POWER:	38.5 kW	7.7 kW	2.8 kW
PEAK CURRENT:	182.3 A	107.9 A	27.8 A
VOLTAGE:	400 V/50 Hz		

ASSA ABLOY

Property of ASSA ABLOY Entrance Systems AB and shall not without our written permission be copied, imparted to a third party or used for any other unauthorized purpose.

GMR Aero Technic Hyderabad

Direct drive | Single motor

Installation overview

Designed	Approved	Location	Code	Page	Date	Drawing No	Revision
MED	GO		84800001	45/45	221117	60109	--

Hall & Kapell

Protects assets & equipment all over the world

MEGADOOR

Megadoor
Folding instruction pre-lined door fabrics

1. 5 cm mark in the middle of the centre line (A)

2. Folds right side up, towards centre line. (like a warehouse)
   Fold approx. 700 mm - 1000 mm on both sides towards the centre line.

3. After the last fold the back side are supposed to point upwards.

   If possible fold one side over the other (B)

4. Roll towards the centre

   The core, on which the fabric are rolled up on to (for fabrics over 140 sqm) are supposed to point out approx 5 cm outside the fabric.

   A small PVC-sign on the folded fabric shows on which side the logo is placed.

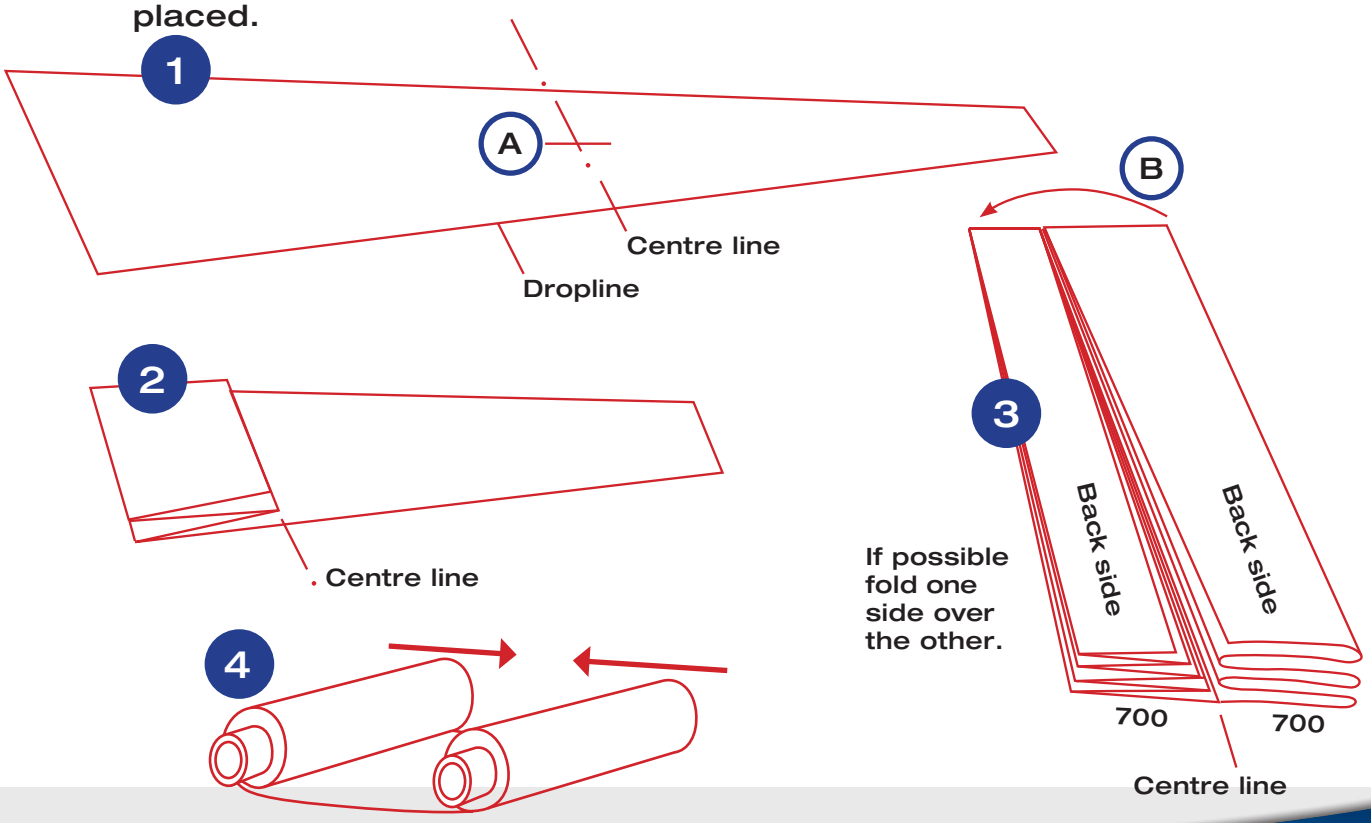

Norrlands Hall & Kapell AB
Kabelvägen 14 | 861 36 Timrå, Sweden | www.nhk.se | Phone: +46 60 - 606 20 00