

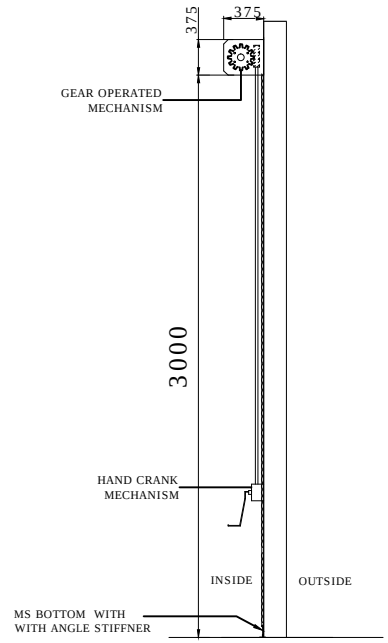


SIDE VIEW

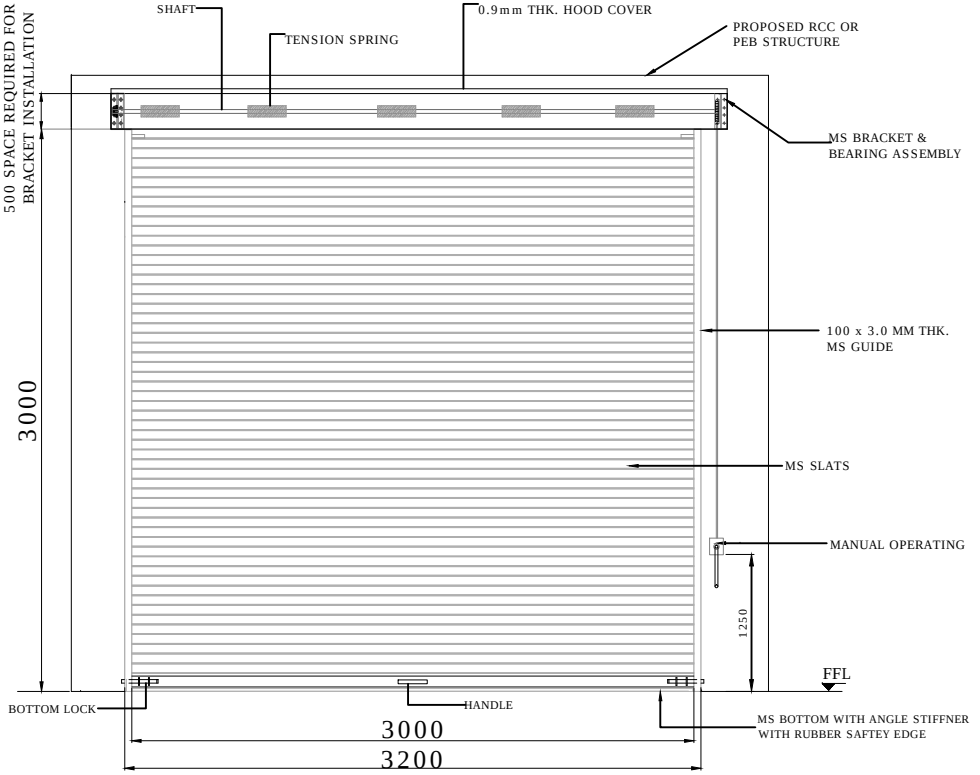


INSIDE ELEVATION

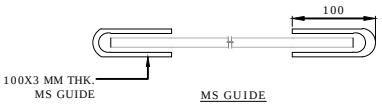

MS GUIDE



PLAN

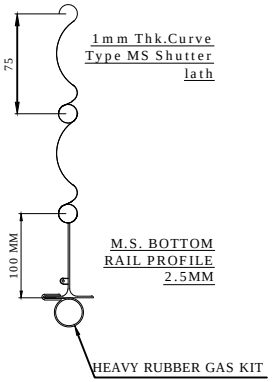

M.S. BOTTOM RAIL PROFILE 2.5MM

CLEAR WIDTH (CW)	CLEAR HEIGHT (CH)	GUIDE SIZE	BRACKET SIZE	SHAFT SIZE (O.D)	QUANTITY	LOCATION
3000	3000	100X3mm	375X375X5mm	50mm	3	PUMP ROOM

DIMENSION :

CLEAR WIDTH	CLEAR HEIGHT	QUANTITY
3000	3000	03 NOS

MATERIAL:

THICKNESS :

NOTE:
1.REQUIRED STRUCTURE FOR ROLLING SHUTTER WILL BE CLIENT'S SCOPE.
2. SHUTTER WILL BE POWDER COATED CLIENT SHOULD CONFIRM RAL COLOR SHADE.

REV NO	DATE	DESCRIPTION
REV 0	29-11-17	INITIAL DRAWING

NIHVA TECHNOLOGIES PVT. LTD.

NIHVA TECHNOLOGIES PVT. LTD. PUNE
Email:- info@nihva.com
Website:- www.nihva.com

TITLE:

GEAR OPERATED ROLLING SHUTTER 3X3m

CLIENT'S APPROVAL :

CLIENT - SCON PROJECTS

PROJECT - ENZENE BIOSCIENCES LTD.

SITE LOCATION - CHAKAN.

DWG. NO. : NIHVA/17-18/0297 | REV.:- 1

SCALE: NTS | WT: | SHEET:1 OF 1

		DATE	SIGN.
DRAWN	SURAJ	29-11-2017	
CHECK	OMKAR	29-11-2017	
APPRD	SHEKHAR	29-11-2017	

If any queries contact : projects@nihva.com

NOTE: ALL DIMENSIONS ARE IN mm

THIS DRAWING & DESIGN IS THE PROPERTY OF NIHVA TECHNOLOGIES. NOT TO BE SOLD OR COPIED TO ANY OTHER CONCERN.