

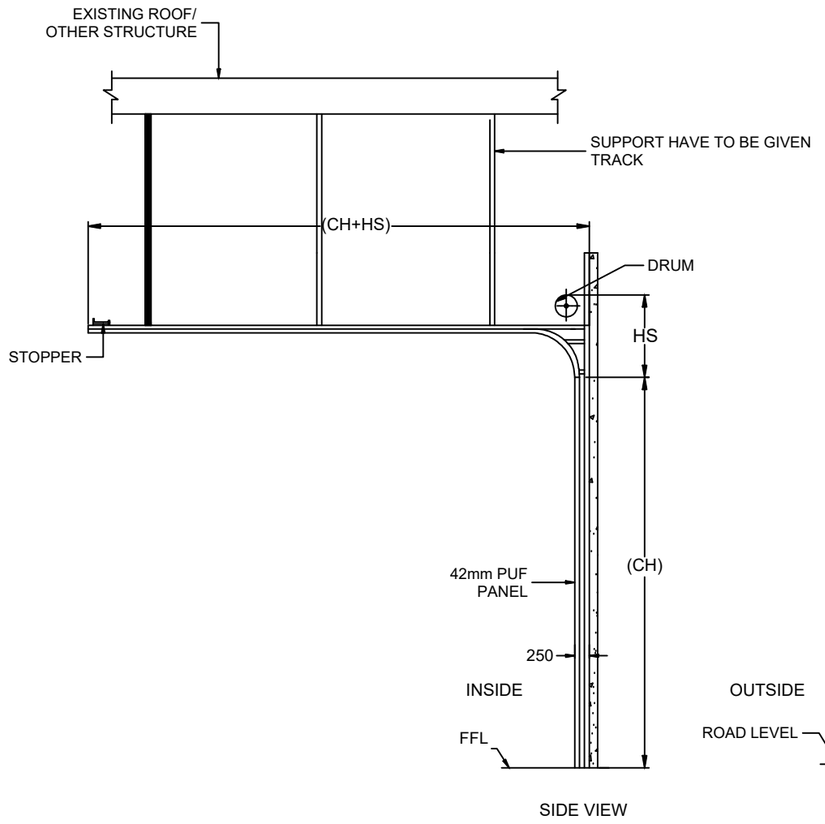



SIDE VIEW

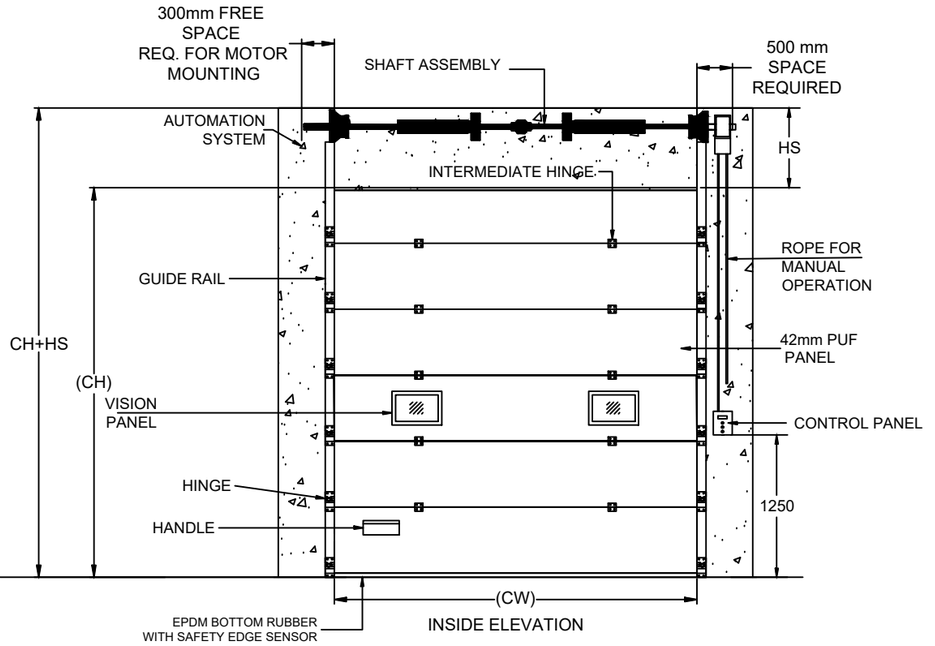

INSIDE ELEVATION

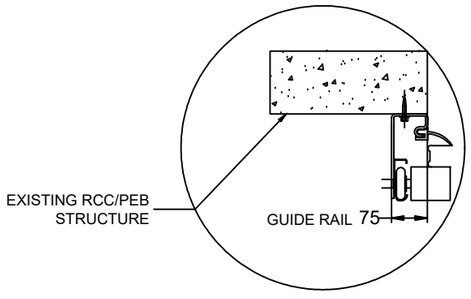

TRACK DETAILS

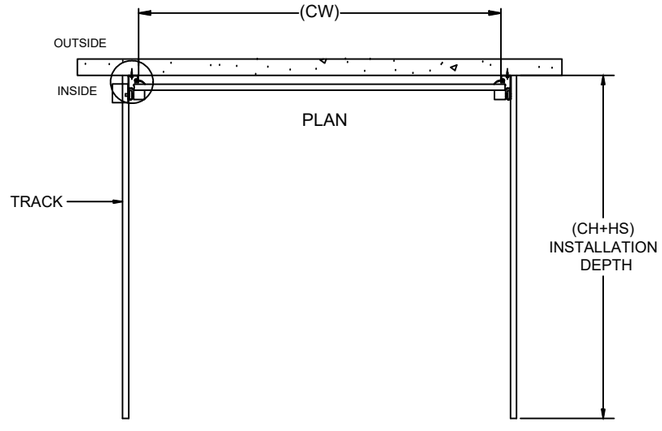

NOTE:-

1. ALL DIMENSION ARE IN MM.
2. THIS DRAWING IS ONLY FOR UNDERSTANDING PURPOSE.
3. ALL CIVIL WORK SHALL BE CLIENT'S SCOPE.

DIMENSION :

Sr.No	Clear Width (CW)	Clear Height (CH)	Header Space (HS)
1.	2200	3500	250

TECHNICAL DATA :

COMPONENTS	MATERIALS	SPECIFICATIONS
DOOR PANELS	GI & PUF	42mm CFC- FREE POLYURETHANE WITH 0.5mm THK, GI PRECOATED PANELS.
DOOR HINGE	———	HEAVY DUTY HINGES FOR INTERLOCKING OF PANELS
SHAFT ASSEMBLY	STD.	TORSIONAL SPRING WITH SHAFT & BEARING PLATES
FINISH		PANELS WILL BE COLORED IN STANDARD OUT SIDE RAL 9002 & INSIDE RAL-7016

ACCESSORIES-

1. SAFETY EDGE SENSOR.
2. MANUAL ROPE
3. PHOTOCELL
4. TWO VISION WINDOW
5. LED INDICATION

IMPORTANT NOTES:

1. ALL DIMENSION ARE IN MM.
2. THIS DRAWING IS ONLY FOR UNDERSTANDING PURPOSE.
3. ALL CIVIL WORK SHALL BE CLIENT'S SCOPE.

CLIENT APPROVAL :

NIHVA TECHNOLOGIES PVT. LTD.

NIHVA TECHNOLOGIES
PVT. LTD. PUNE
Email:- info@nihva.com
Website:- www.nihva.com

TITLE:

OVERHEAD SECTIONAL DOOR

CLIENT - MARS INTERNATIONAL INDIA PVT LTD

PROJECT - SECTIONAL DOOR

LOCATION - TELANGANA

DWG. NO. : NIHVA/24-25/00XX

SCALE: NTS	WT:	SHEET:1 OF 1	REV- 0

	NAME	DATE	SIGN
DRAWN	S.J	18/11/2024	
CHECK			
APPROVAL	V.T.	18/11/2024	

If any queries contact : design1@nihva.com

NOTE: ALL DIMENSIONS ARE IN mm

THIS DRAWING & DESIGNING IS THE PROPERTY OF NIHVA TECHNOLOGIES. NOT TO BE SOLD OR COPIED TO ANY OTHER CONCERN.