



DRAWING

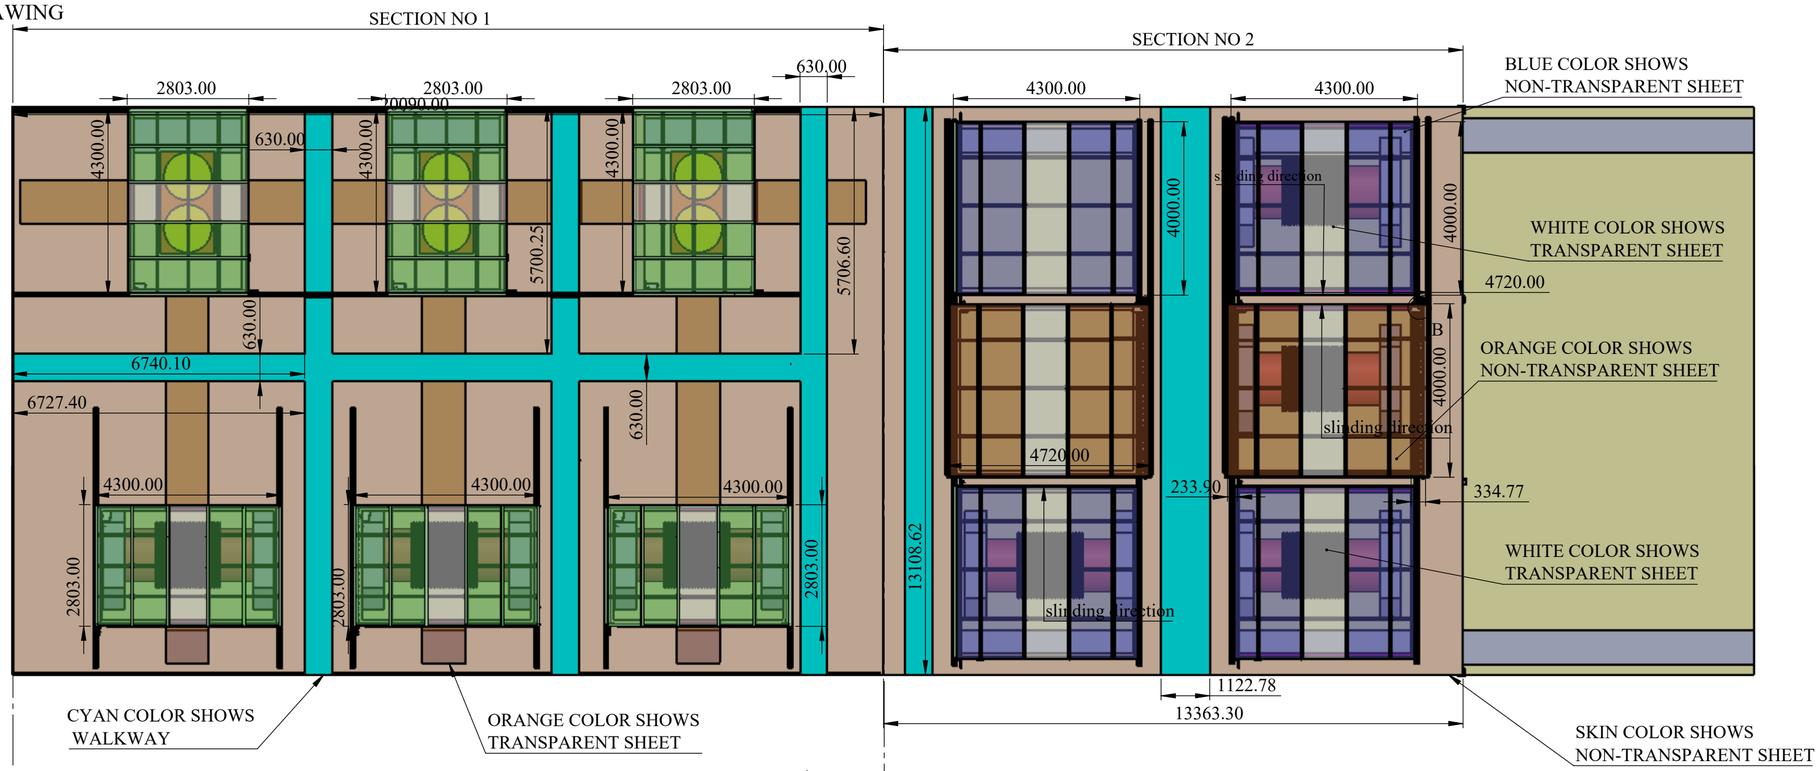

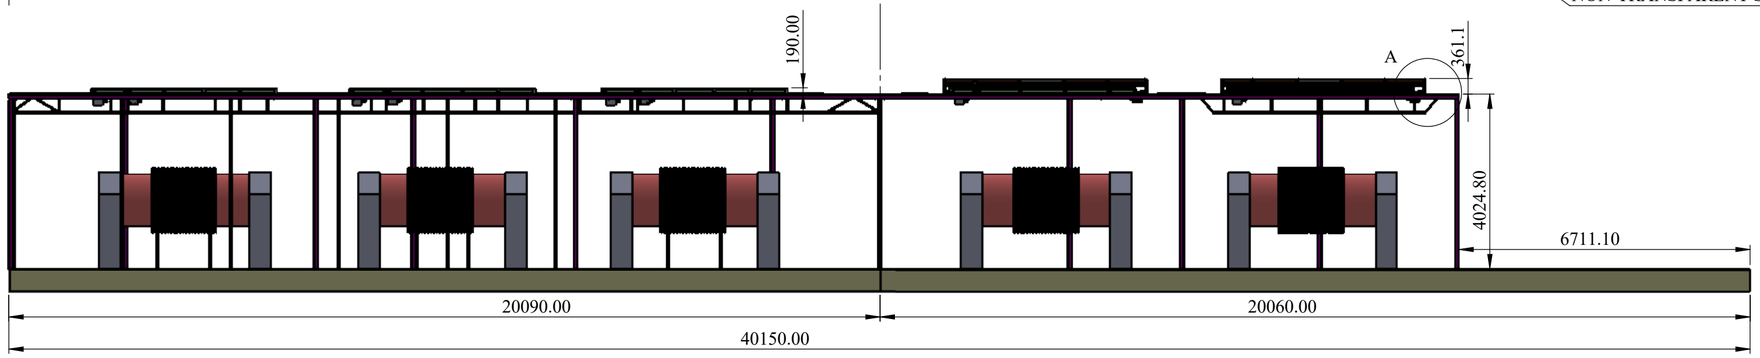

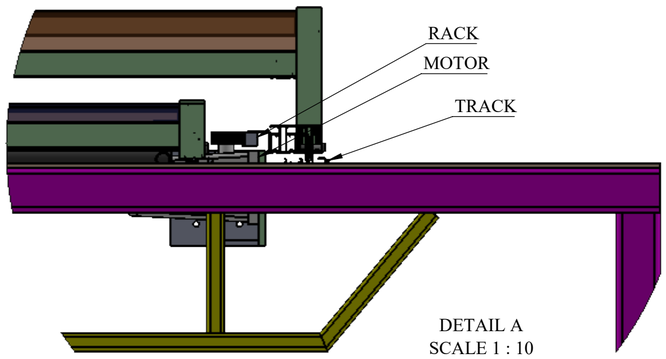

DETAIL A
SCALE 1 : 10
MOTOR ARRANGMENT

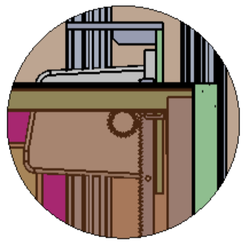

DETAIL B
SCALE 1 : 10

REV DESCRIPTION	DATE	REV NO
	08-08-2025	REV 00
1.		

NOTE :

GA DRAWING

SPECIAL INSTRUCTION'S :

TITLE - ROOF AUTOMATION				NIHVA Technologies Pvt. Ltd.	NIHVA TECHNOLOGIES PVT.LTD.PUNE Website - www.nihva.com
DWG NO - NTPL-244-PM-001-00-00-00					
	NAME	SIGNATURE	DATE	PRODUCT - RETRACTABLE ROOF	
DRAWN	V.W.		28-08-2025	PROJECT NO - NTPL-244-PM	REVISION - 00
CHK'D	S.P.		04-09-2025	SITE LOCATION - GUJARAT	WEIGHT -
APPV'D	V.T.		05-09-2025	MATRIAL -	QTY - 1
If any queries contact - Design@nihva.com				PROJECTION METHOD:	SCALE :
ALL DIMENSION ARE IN mm		A2			SHEET 1 OF 16