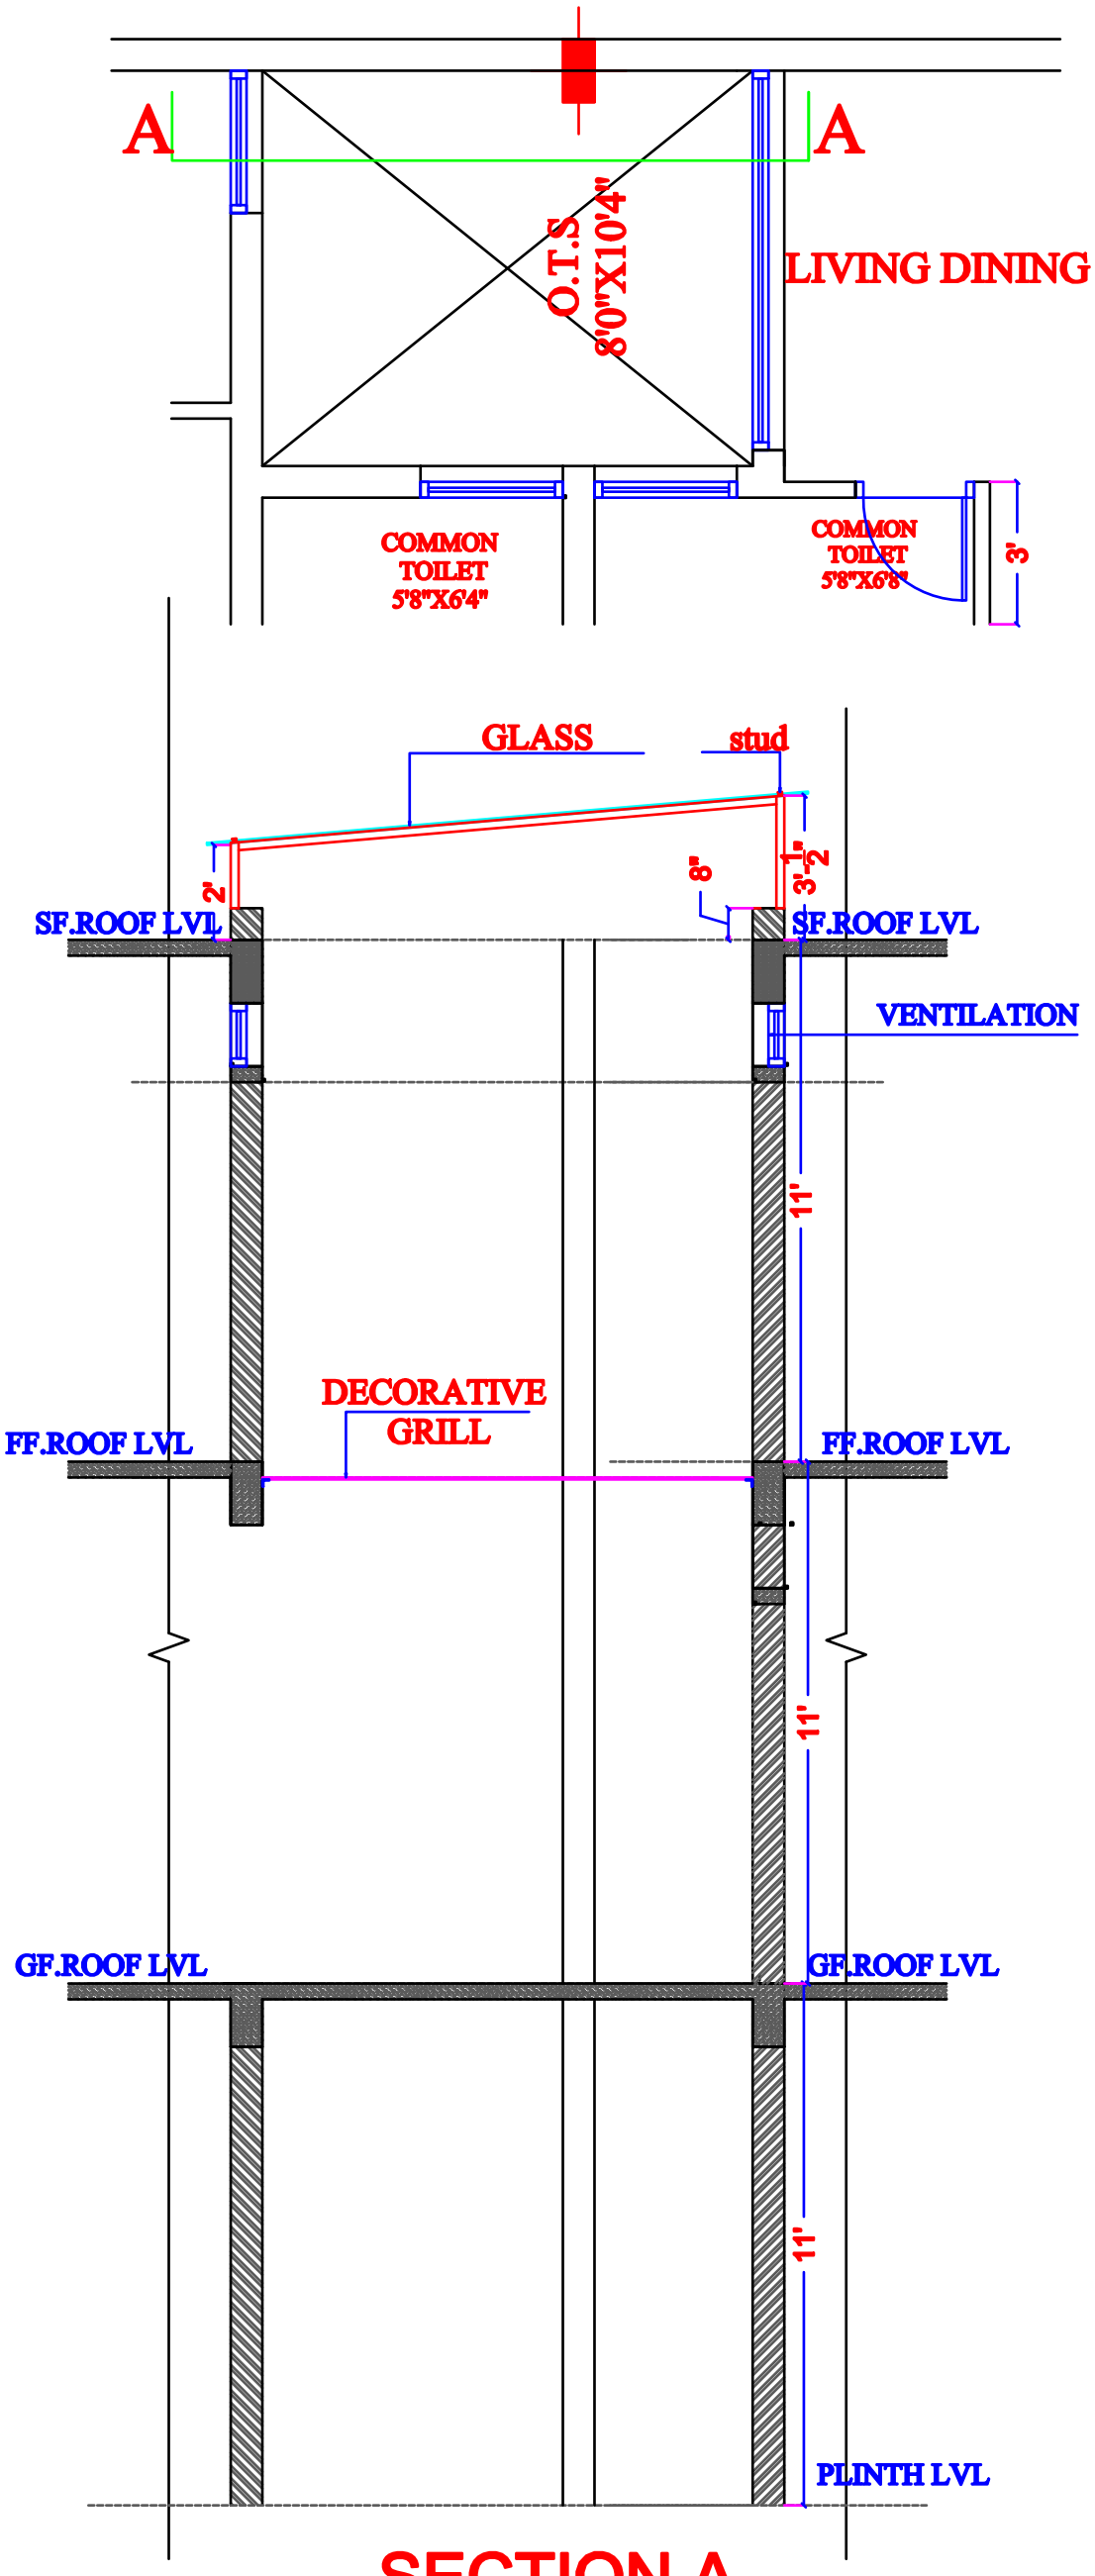


SECTION A

ABHISHEK & KULDEEP JULKA
ARCHITECTURE INTERIOR DESIGN ENVIRON PLANNING ENGINEERING
G-9 RITU APARTMENT 220 ANOOP NAGAR INDORE-18 PH.:+91731-4066008 FAX:+91731-2550067

TITLE : LIVING&DINING CUTOUT DETAIL

PROJECT :RESIDENCE OF MR. ABHISHEK GUPTA AT GORAKHPUR

EXECUTION RECORD TENDER APPROVAL

DRG.No. : AR-1527/WD-01F
DATE : 20/07/2022
SCALE : 1":48" (A3)