


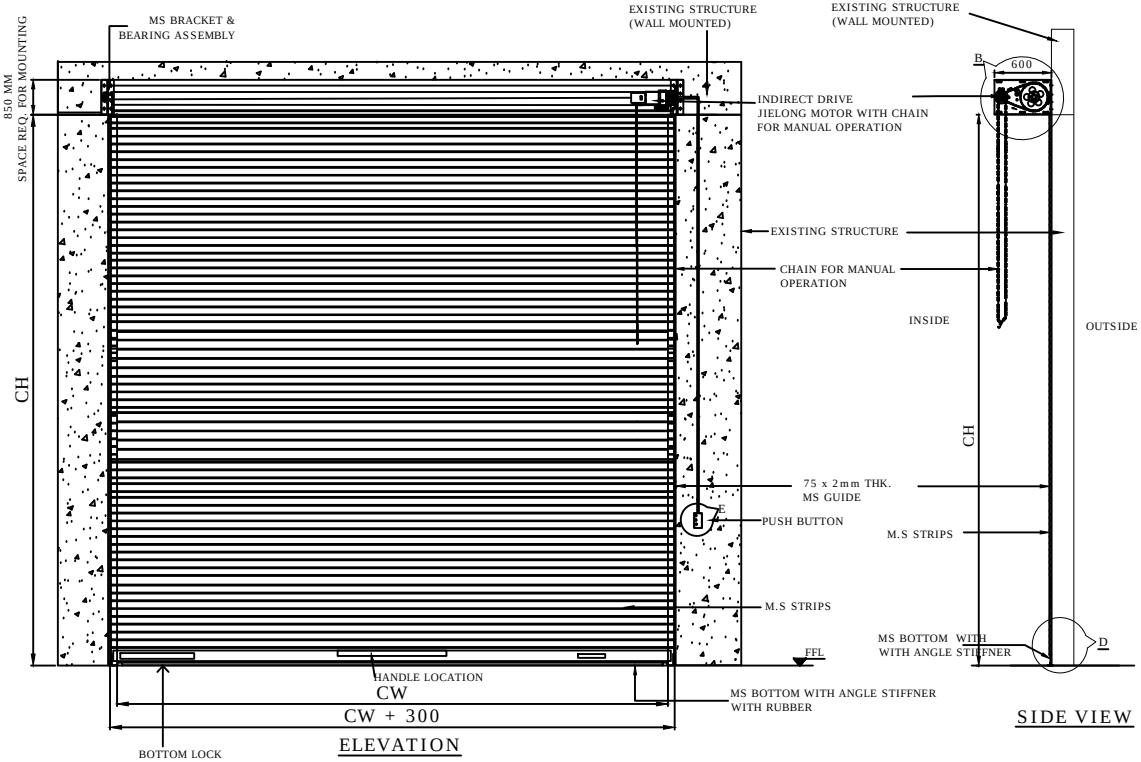


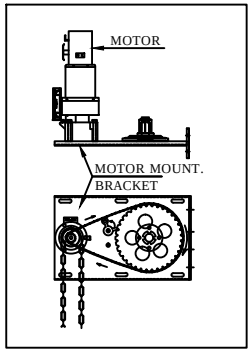


DETAILS : A & B

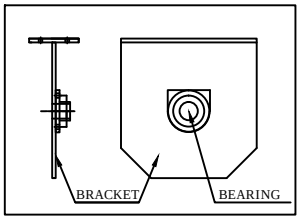


DETAILS : C

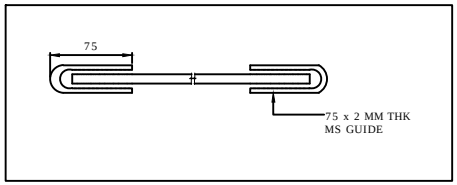

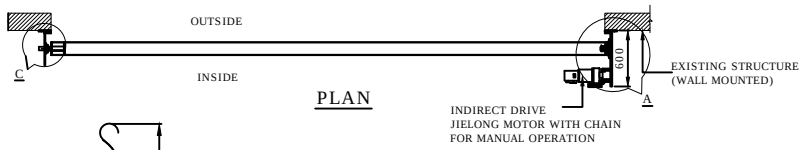

PLAN

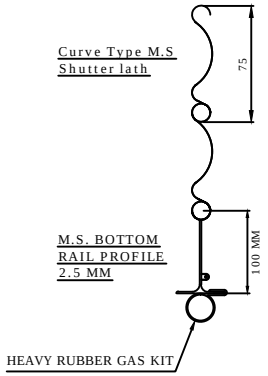

DETAILS : D

(NOTE: SHUTTER IS WALL MOUNTED.)

CLEAR WIDTH (CW)	CLEAR HEIGHT (CH)	QUANTITY	RAL COLOR
3555	5000	1	RAL - 9010
3575	5000	1	RAL - 9010

This drawing & design is the property of NIHVA TECHNOLOGIES. Not to be sold or copied to any other concern.

TITLE: WALL MOUNTED MOTORIZED ROLLING SHUTTER

NIHVA TECHNOLOGIES PVT. LTD.

NIHVA TECHNOLOGIES PVT. LTD. PUNE
Tel : 020 66304033
Email:- info@nihva.com
Website:- www.nihva.com

	NAME	SIGN	DATE
DRAWN	P.A		19.11.2019
CHECK	G.J		19.11.2019
APPRD.			

CLIENT -

PROJECT -

SITE LOCATION -

If any queries contact : design@nihva.com

DWG. NO. : NIHVA/19-20/VDR/229 REV- R00

ALL DIMENSION ARE IN mm

SCALE: NTS WT: SHEET: