




OUTSIDE ELEVATION

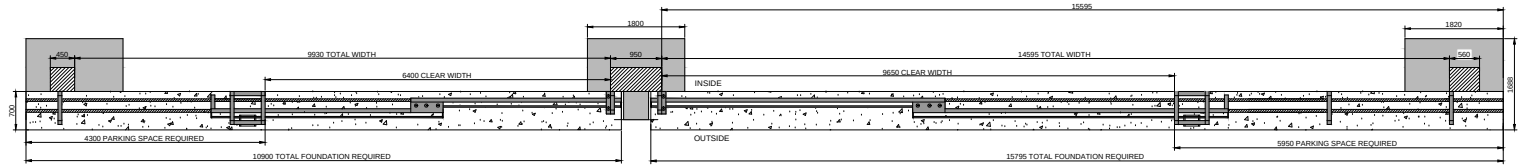


PLAN

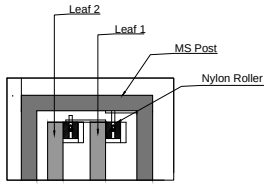


Detailed View of A

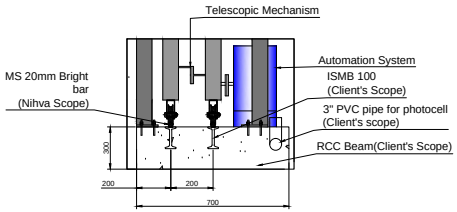

Detailed View of B

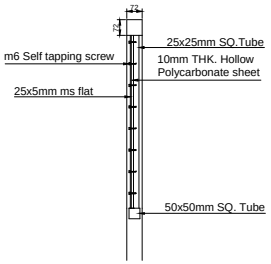

Gate leaf section details

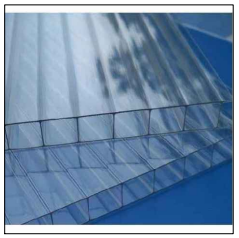

10mm THK. Hollow polycarbonate sheet

DIMENSION :

CLEAR WIDTH	CLEAR HEIGHT	QUANTITY
9650 mm	3000 mm	1 NOS.
6400 mm	3000 mm	1 NOS.

MATERIAL : MS

THICKNESS :

MATERIAL SPECIFICATION

SR NO	TUBE SIZE	
1	MS TUBE 72X72X3.2mm	OUTER TUBE
2	MS TUBE 50X50X2.6mm	INTERMEDIATE TUBE
3	MS TUBE 25X25X2mm	INNER TUBE
4	3mm MS SHEET	AT LOWER SIDE
5	10mm THK. HOLLOW POLYCARBONATE SHEET (TRANSPARENT)	AT UPPER SIDE
6	MS 25X5mm FLAT	FIXING OF POLYCARBONATE SHEET

NOTE: ALL REQUIRED CIVIL WORK WILL BE IN CLIENT'S SCOPE.
ONE COAT RED OXIDE PRIMER WILL BE GIVEN TO THE STRUCTURE OF GATE.
TWO COATS OF FINAL APPROVED RAL SHADE WILL BE GIVEN TO THE CLIENT.
ISMB 100 WILL BE CLIENTS SCOPE.

NIHVA TECHNOLOGIES PVT. LTD.
NIHVA TECHNOLOGY PVT. LTD. PUNE
Email:- info@nihva.com
Website:- www.nihva.com

TITLE:

TWO LEAF TELESCOPIC SLIDING GATE 9.65X3m & 6.4x3m

CLIENT'S APPROVAL :

CLIENT -

PROJECT -

SITE LOCATION -

DWG. NO. : NIHVA/17-18/VDR/0249 | REV- 0

SCALE: NTS | WT: | SHEET:1 OF 1

DRAWN BY: OMKAR | DATE: 26-02-2018

CHECK : SHEKHAR | DATE: 26-02-2018

APPROVED : SHEKHAR | DATE: 26-02-2018

If any queries contact : design@nihva.com

NOTE: ALL DIMENSION ARE IN mm

THIS DRAWING & DESIGNING IS THE PROPERTY OF NIHVA TECHNOLOGIES. NOT BE SOLD OR COPY TO ANY OTHER CONCERN.