


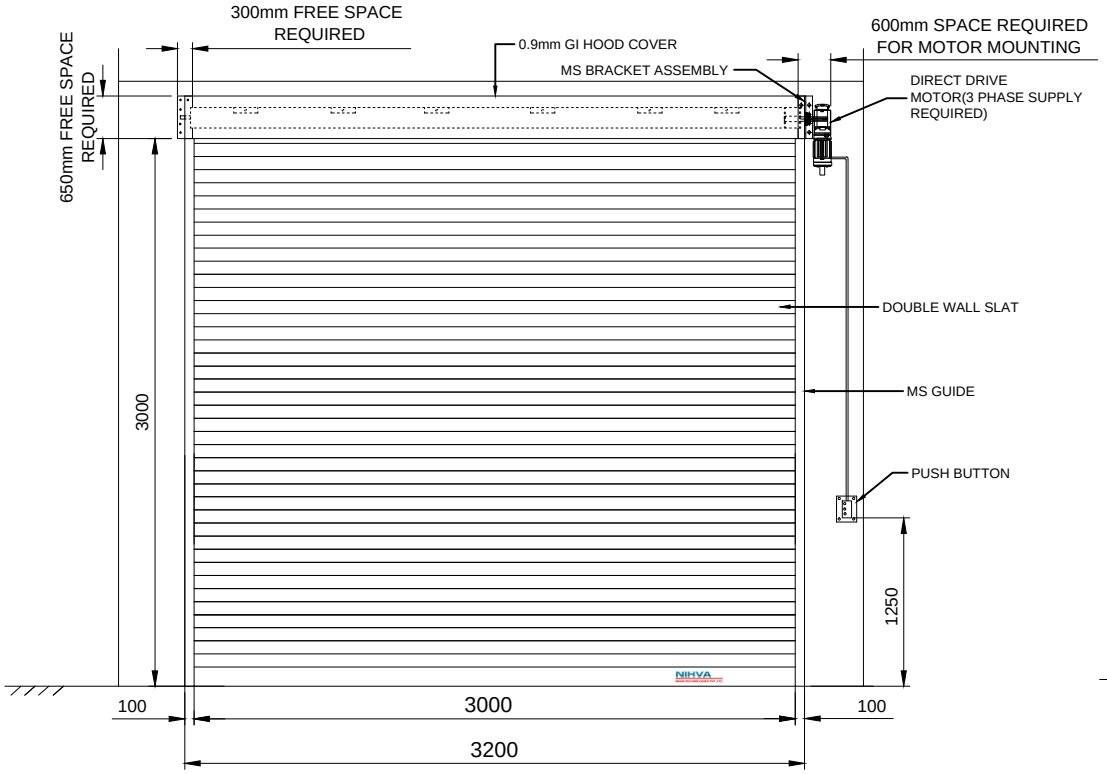


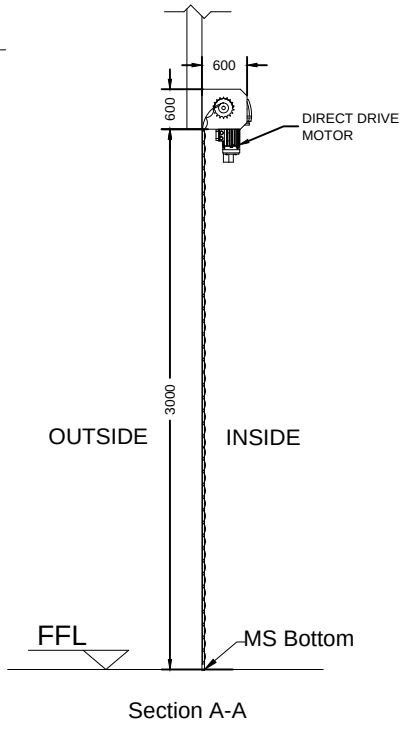


Section A-A

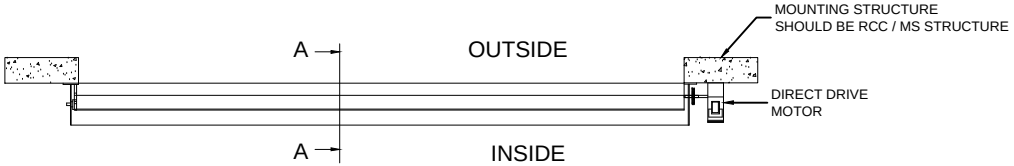

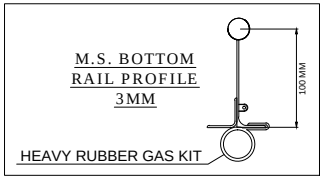

Main Slats
Double Wall Rolling Shutter

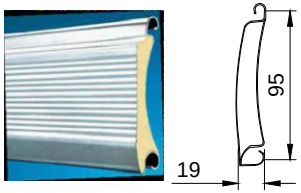

CLEAR WIDTH (CW)	CLEAR HEIGHT (CH)	QUANTITY
3000 mm	3000 mm	2 NOS

COLOR OF SLATS & SHUTTER -RAL9001

DIMENSION :

CLEAR WIDTH	CLEAR HEIGHT	QUANTITY
3000 mm	3000 mm	2 NOS

NOTE:-

1.STRUCTURE FOR SHUTTER FOR SHUTTER WILL BE IN CLIENT'S SCOPE.
2. 3 PHASE SUPPLY SHOULD BE PROVIDED.

CLIENT'S APPROVAL :

NIHVA TECHNOLOGIES PVT. LTD. PUNE
TEL:- 02066304033
Email:- info@nihva.com
Website:- www.nihva.com

NIHVA TECHNOLOGIES PVT. LTD.

TITLE :

DOUBLE WALL ROLLING SHUTTER

CLIENT - DHOOT BUILDERS

PROJECT -SKODA AUTO IND.PVT.LTD

SITE LOCATION - AURANGABD

DWG. NO. : NIHVA/17-18/0343 | REV: 0

SCALE: NTS | WT: | SHEET:1 OF 1

	NAME	SIGN	DATE
DRAWN	SURAJ		30-01-2018
CHECK	OMKAR		30-01-2018
APPV'D	SHEKHAR		30-01-2018

If any queries contact : design@nihva.com

NOTE: ALL DIMENSIONS ARE IN mm

THIS DRAWING & DESIGN IS THE PROPERTY OF NIHVA TECHNOLOGIES. NOT TO BE SOLD OR COPIED TO ANY OTHER CONCERN.