


1. 'L' SHAPED SLIDING ROOF STRUCTURE

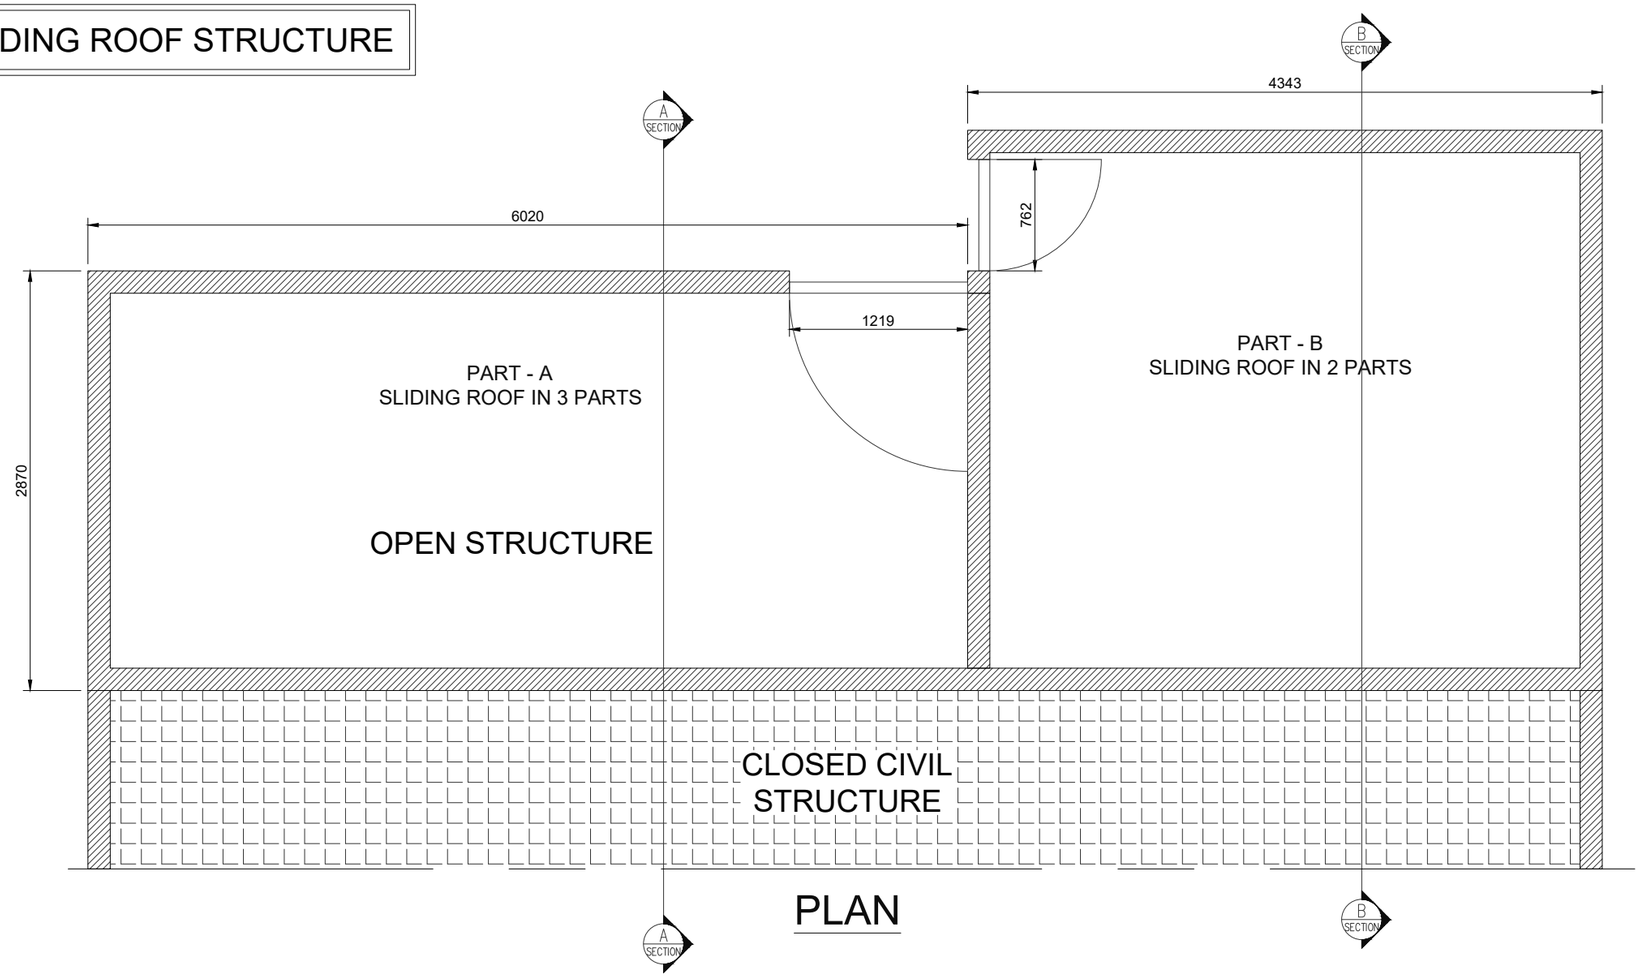

PLAN

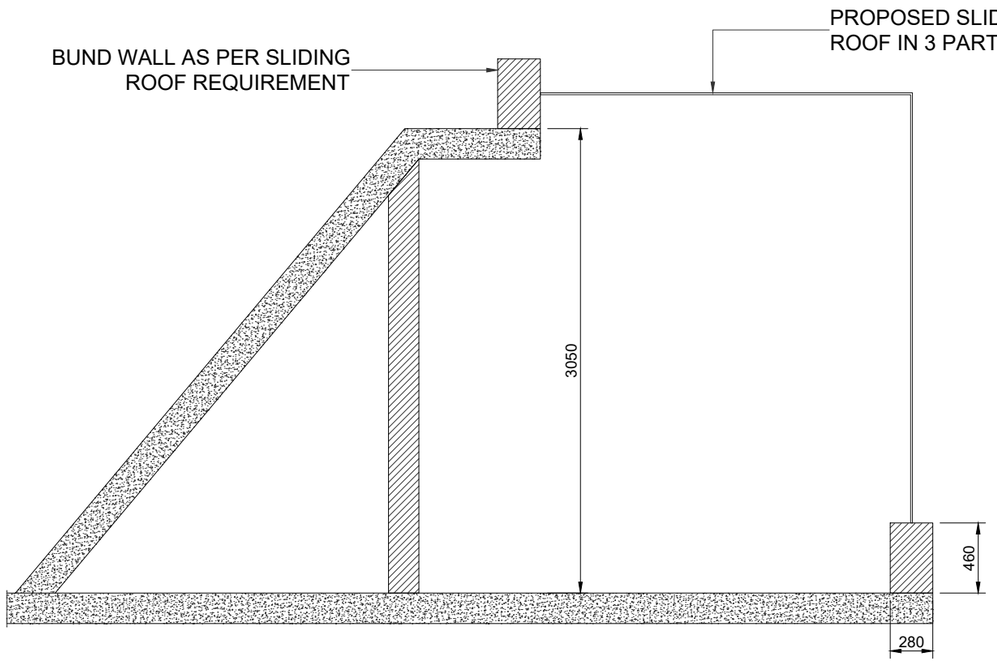

SECTION - A

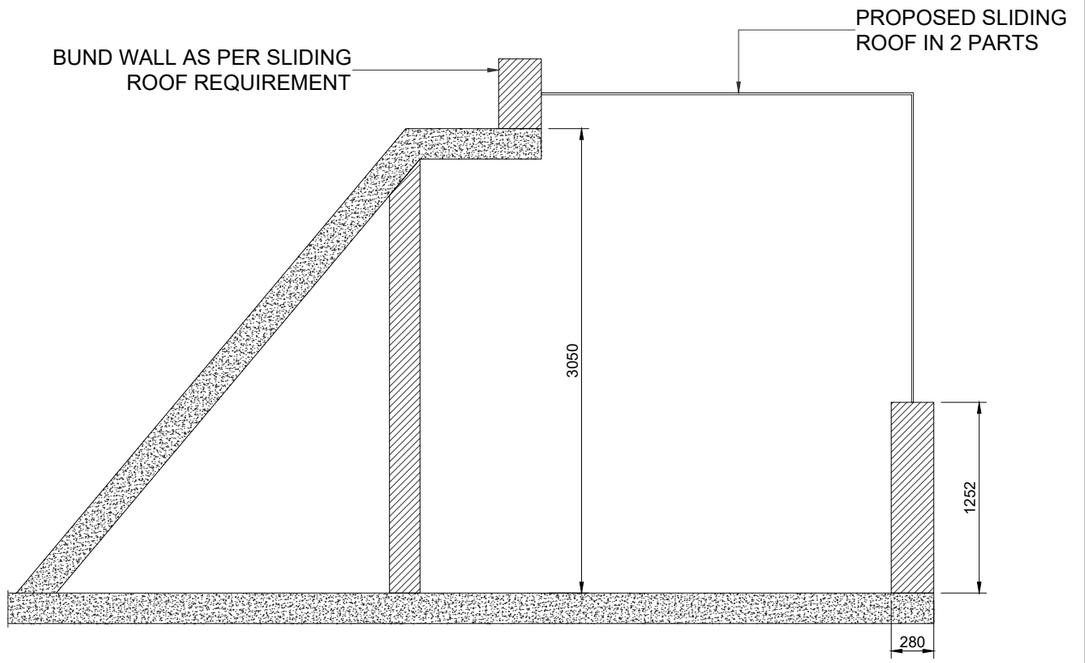

SECTION - B

GENERAL NOTES:

- ALL DIMENSIONS ARE IN MILLIMETERS.
- ALL ELEVATIONS VIEWED FROM OUTSIDE.
- DO NOT SCALE DRAWINGS, FOLLOW WRITTEN DIMENSIONS.
- THIS DRAWING IS PROPERTY OF GFS & IT IS NOT TO BE REPRODUCED, COPIED OR HANDED OVER IN ANY FORM EXCEPT FOR THE PURPOSE FOR WHICH IT IS INTENDED

REVISION	DESCRIPTION	DATE
R00	ISSUE FOR APPROVAL	25.02.2025

PROJECT:

KRC BUNGALOW
HYDERABAD

ARCHITECT:

-

CLIENT:

-

PMC :

FACADE CONSULTANT:

FACADE CONTRACTOR :

DESTEL
ENGINEERED TO DELIGHT
DESTEL INDIA PVT. LTD
Ellora Fiesta, 805, 8th Floor,
Plot No. 08, Sector - 11, Sanpada,
Navi Mumbai - 400 705.

DRAWING TITLE:


PLAN & SECTION

DRAWN	CHECKED	APPROVAL	DATE	SCALE
SW	JNA	JNA	25.02.2026	1:60


DRAWING NUMBER: DS-KRC-SD-01

REVISION: R00

1. SKYLIGHT STRUCTURE (STRAIGHT)

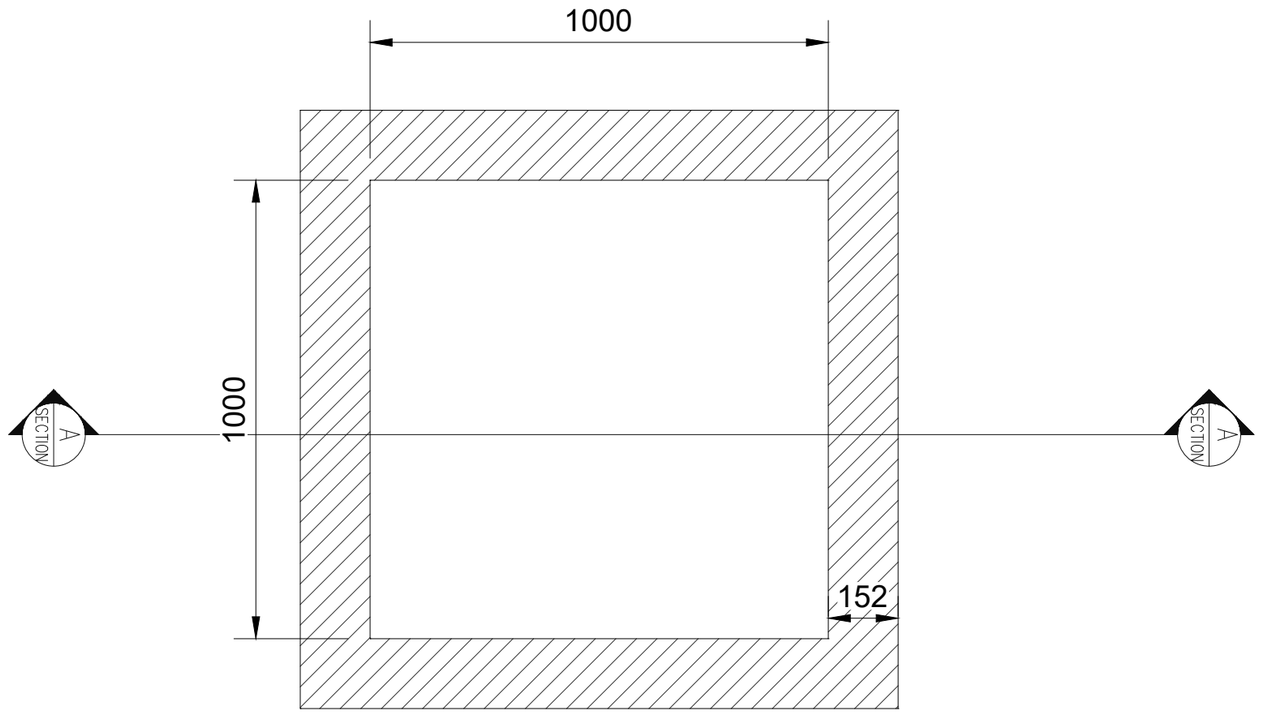

TOP VIEW

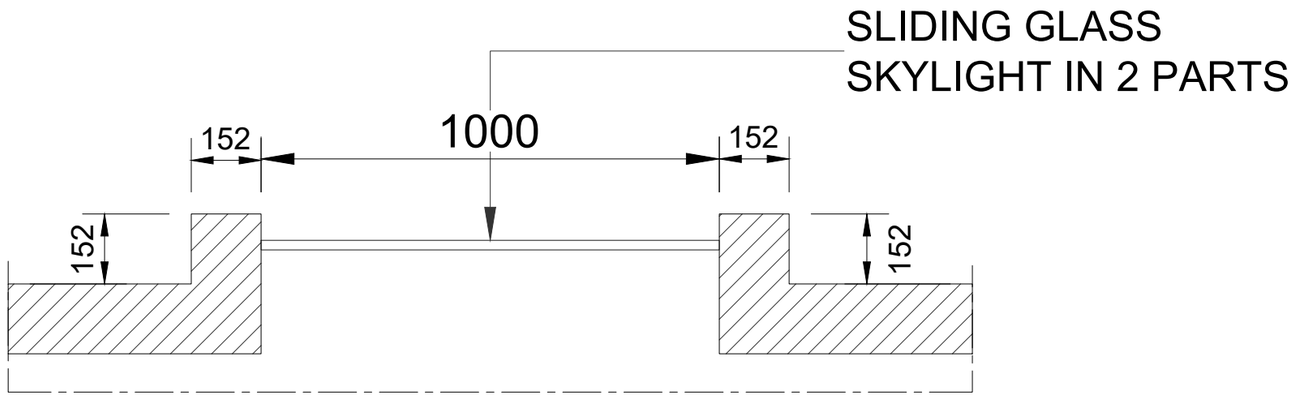

SECTION - A

GENERAL NOTES:

- ALL DIMENSIONS ARE IN MILLIMETERS.
- ALL ELEVATIONS VIEWED FROM OUTSIDE.
- DO NOT SCALE DRAWINGS, FOLLOW WRITTEN DIMENSIONS.
- THIS DRAWING IS PROPERTY OF GFS & IT IS NOT TO BE REPRODUCED, COPIED OR HANDED OVER IN ANY FORM EXCEPT FOR THE PURPOSE FOR WHICH IT IS INTENDED

REVISION	DESCRIPTION	DATE
R00	ISSUE FOR APPROVAL	25.02.2025

PROJECT:

KRC BUNGALOW
HYDERABAD

ARCHITECT:

-

CLIENT:

-

PMC :

FACADE CONSULTANT:

FACADE CONTRACTOR :

DESTEL
ENGINEERED TO DELIGHT
DESTEL INDIA PVT. LTD
Ellora Fiesta, 805, 8th Floor,
Plot No. 08, Sector - 11, Sanpada,
Navi Mumbai - 400 705.

DRAWING TITLE:

GROUND FLOOR PLAN

DRAWN	CHECKED	APPROVAL	DATE	SCALE
SW	JNA	JNA	25.02.2026	1:60

DRAWING NUMBER: DS-KRC-SD-02

REVISION: R00