

HOPPER CAPACITY : 5 KG

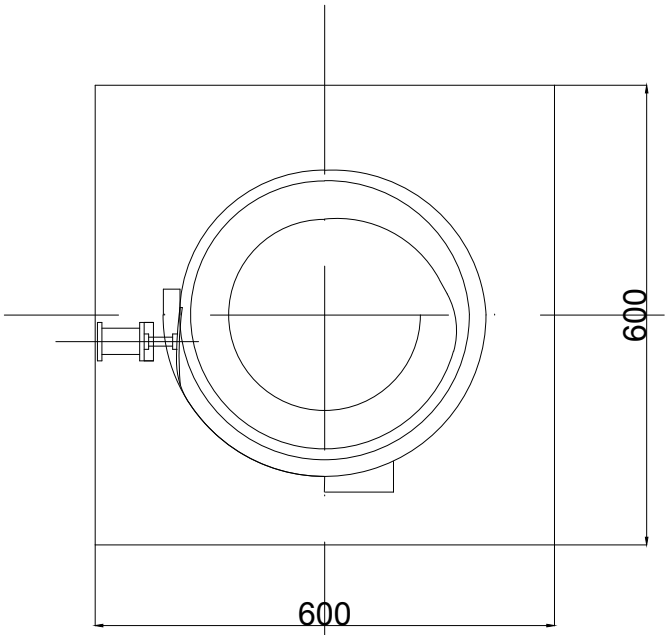

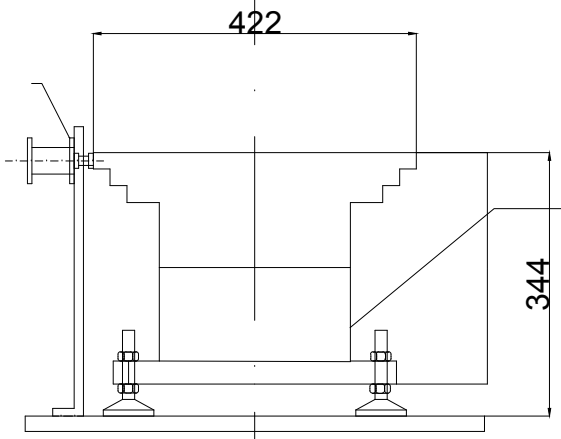

NOTE: 1) SUPPORT MOUNTING STRUCTURE
WILL BE CLIENT SCOPE
2) SPACE AVAILABLE AT INSTALLATION
SIZE TO BE ENSURE AS
PER TABLE SIZE

ALL DIMENSIONS ARE IN mm

UNLESS OTHERWISE SPECIFIED: DIMENSIONS ARE IN MILLIMETERS SURFACE FINISH: TOLERANCES: LINEAR: ANGULAR:	FINISH:				DEBURR AND BREAK SHARP EDGES	DO NOT SCALE DRAWING / REVISION
	NAME	SIGNATURE	DATE			NIHVA TECHNOLOGIES PVT LTD Email:-info@nihva.com Website:-www.nihva.com
DRAWN	SHAILENDRA		07/01/2020			TITLE: BOWL FEEDER G.A. DRAWING
CHK'D	SHAILENDRA		07/01/2020			
APPV'D	V.T.		08/01/2020			
MFG						
Q.A				MATERIAL: SS202		DWG NO. NIHVA19_20/BWLFD/001 A3
				WEIGHT: GMS		SCALE:1:20 SHEET 1 OF 1