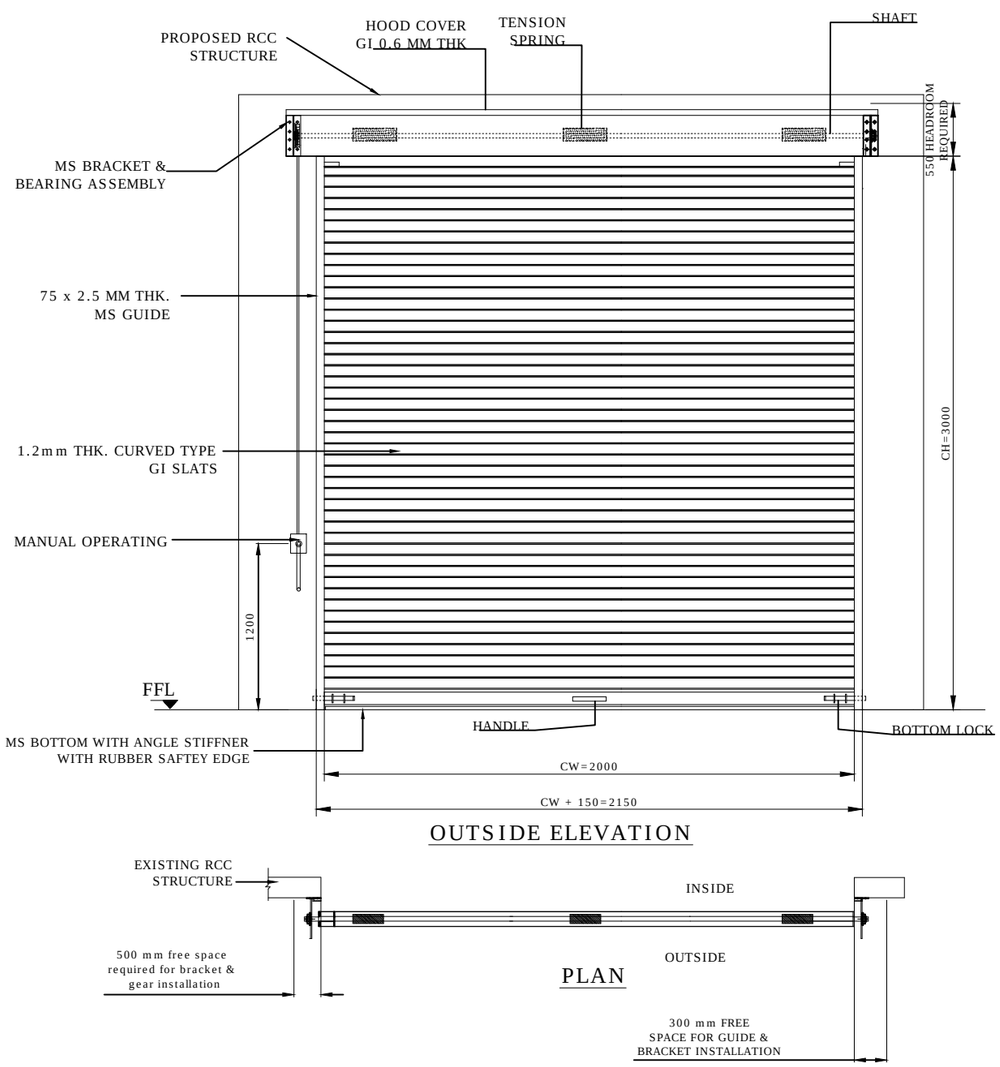
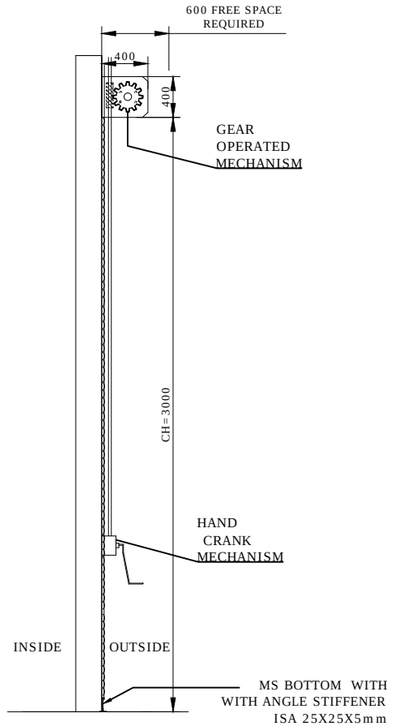


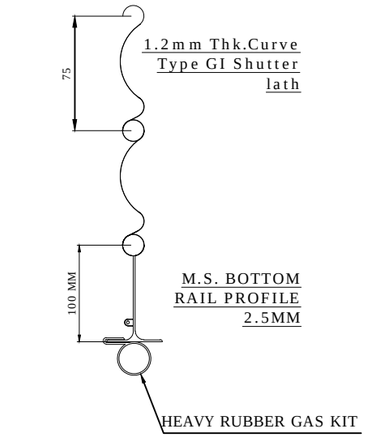

OUTSIDE ELEVATION



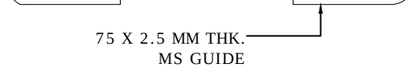

PLAN




SIDE VIEW




M.S. BOTTOM RAIL PROFILE 2.5MM




| RAL CODE | RAL COLOR | APPROVAL |
|---|---|---|
| RAL 7040 | WINDOW GREY | APPROVED |

| SR NO | ( CW ) CLEAR WIDTH | ( CH ) CLEAR HEIGHT | QUANTITY |
|---|---|---|---|
| 1 | 2000 | 3000 | 01 NO |

TOLERANCE - ±10mm

NOTE-
1. ALL DIMENSIONS ARE IN MM.
2. SURFACE FINISH: POWDER COATING OF APPROVED RAL CODE.
3. MOUNTING ON OUTSIDE CONCRETE STRUCTURE.
4. MOUNTING OF LEVER WILL BE ON LEFT SIDE.

This drawing & design is the property of NIHVA TECHNOLOGIES. Not to be sold or copied to any other concern.

TITLE
GEAR OPERATED ROLLING SHUTTER

| | NAME | SIGN | DATE |
|---|---|---|---|
| DRAWN | G.I.P | | 23.02.2022 |
| CHECK | A.K. | | 23.02.2022 |
| APPRD. | V.T. | | 23.02.2022 |

If any queries contact : design@nihva.com

ALL DIMENSION ARE IN mm

NIHVA
NIHVA TECHNOLOGIES PVT. LTD.
Website:- www.nihva.com
NIHVA TECHNOLOGIES PVT. LTD. PUNE
Tel : 020 66304033
Email:- info@nihva.com

CLIENT -

PROJECT -GEAR OPERATED ROLLING SHUTTER

SITE LOCATION -

DWG. NO. : NIHVA/21-22/VDR/031 | REV- R0

SCALE: NTS | WT: | SHEET: 01 OF 01