

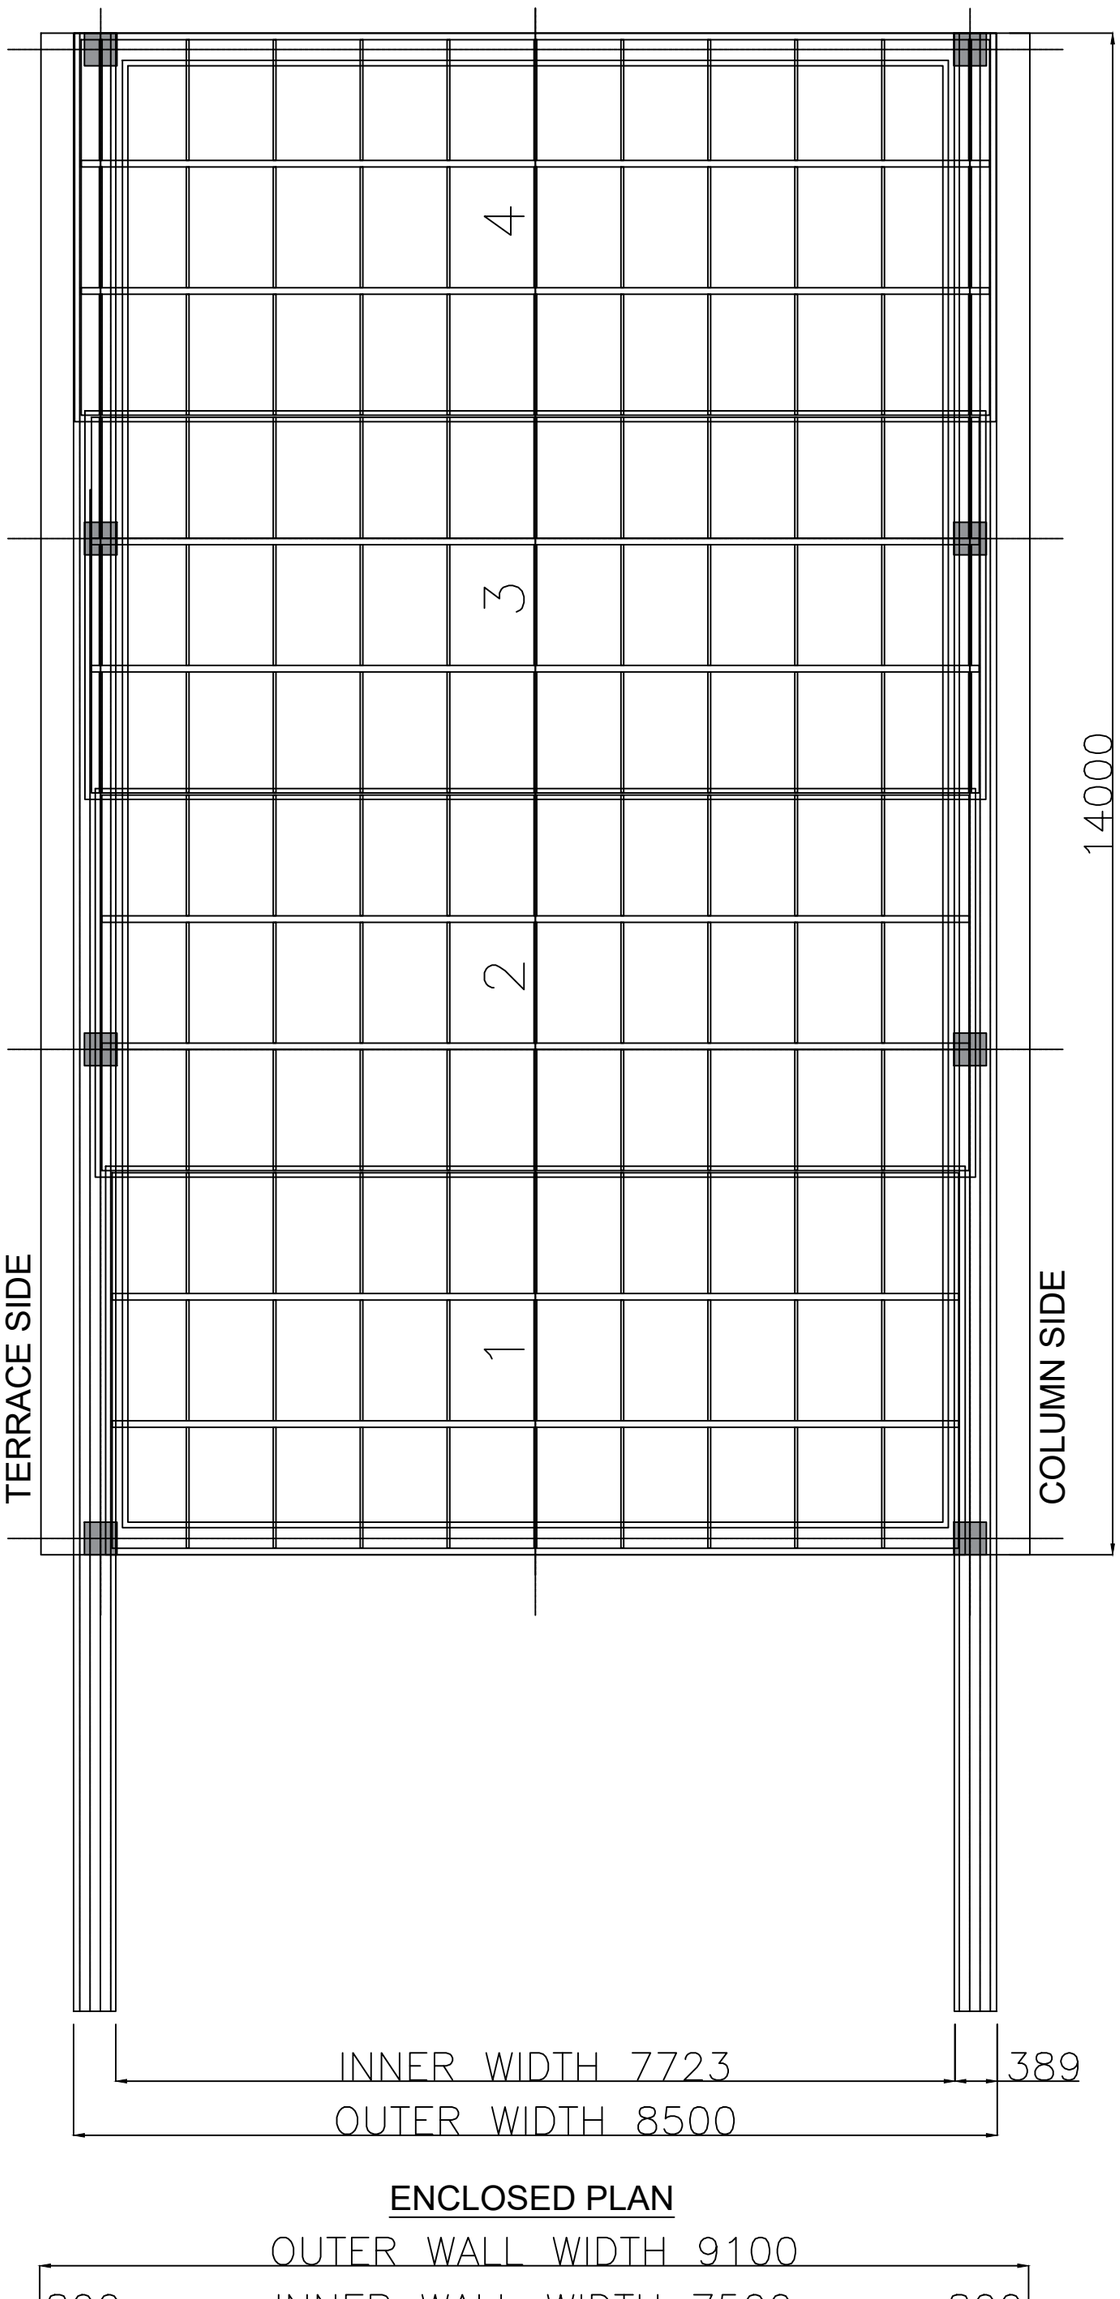


ENCLOSED PLAN

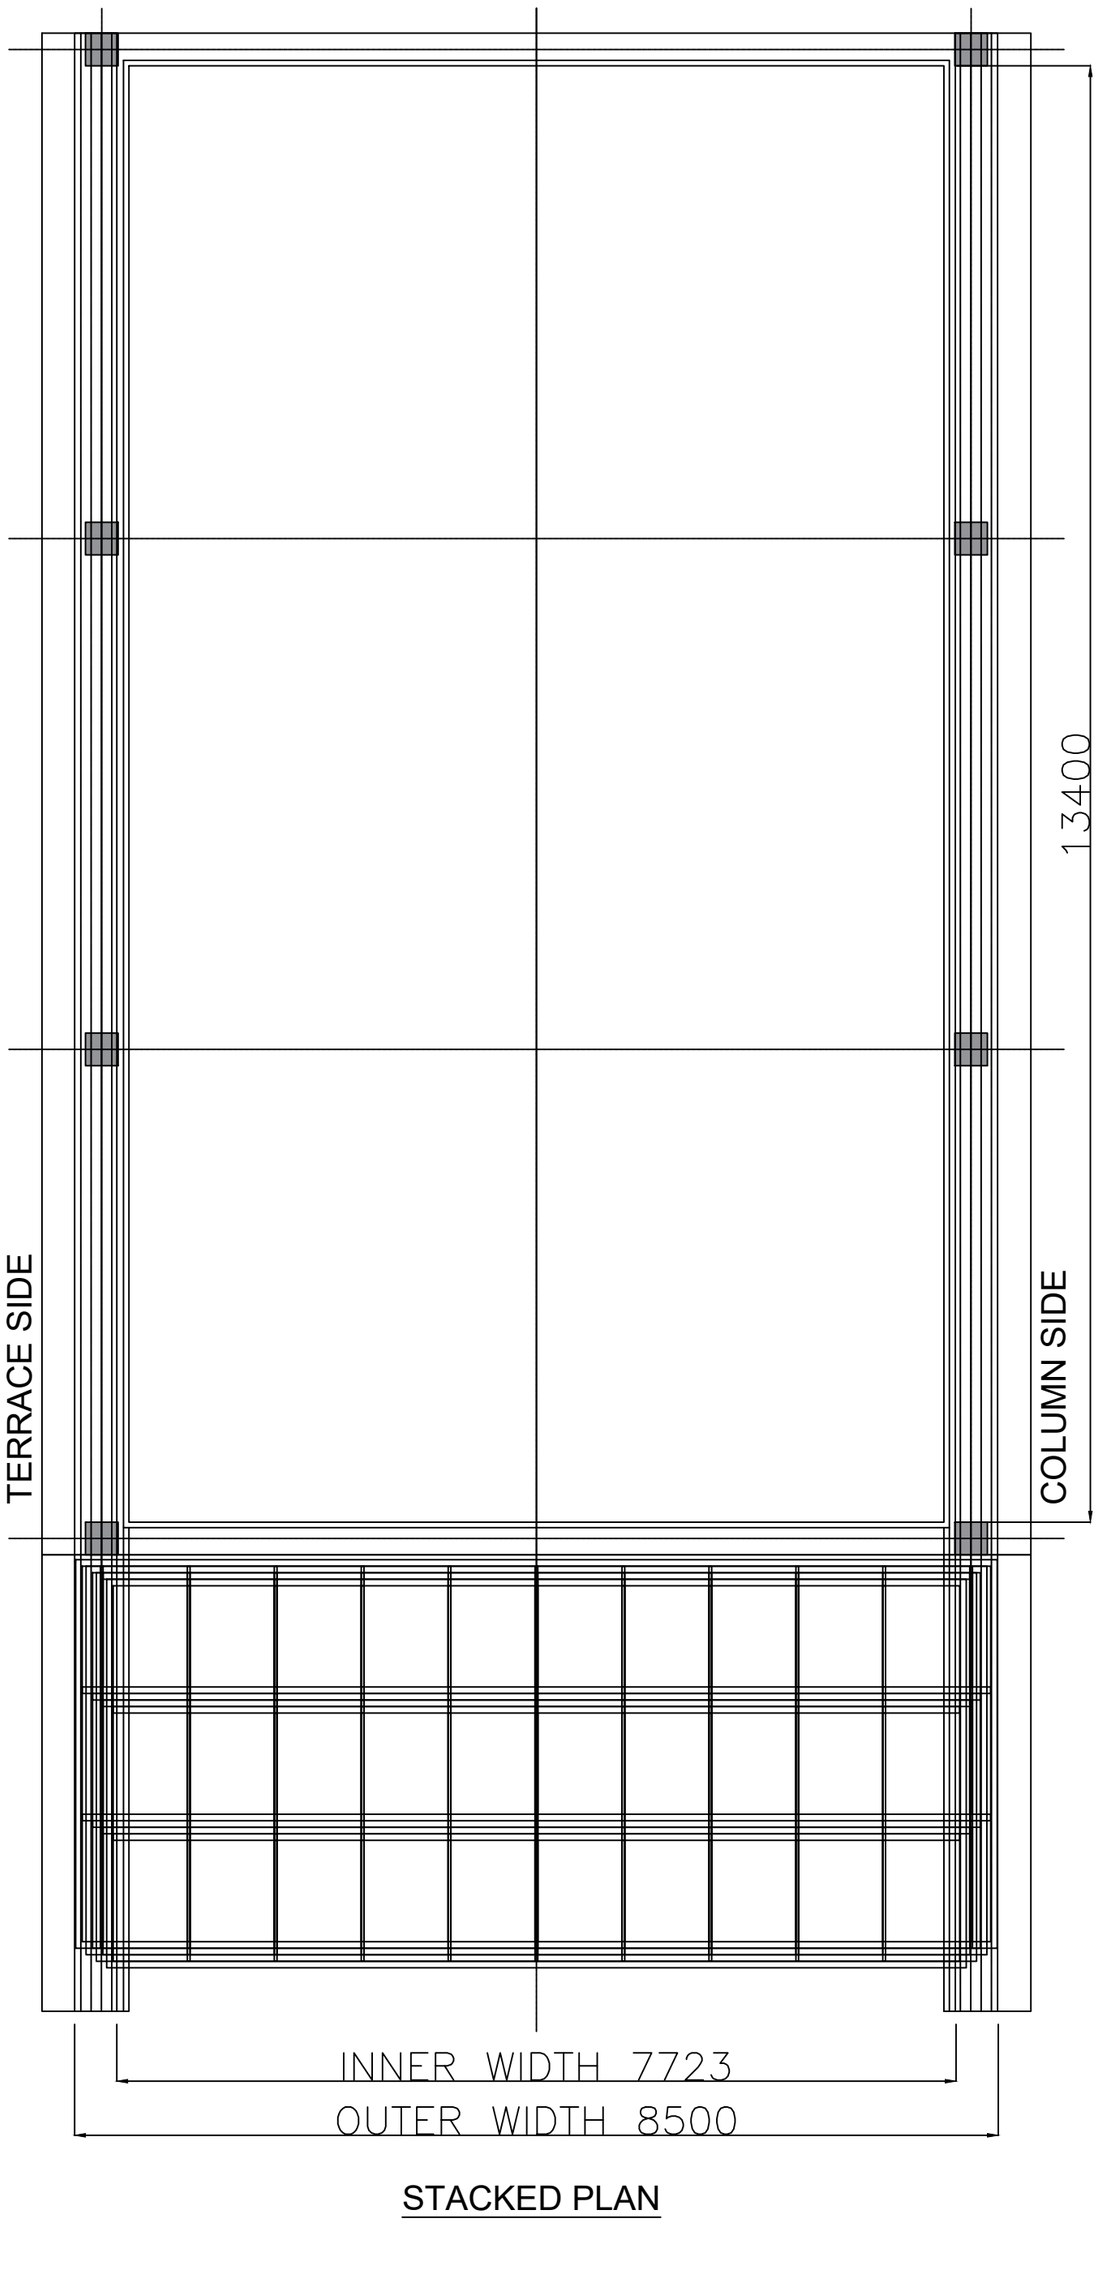

STACKED PLAN

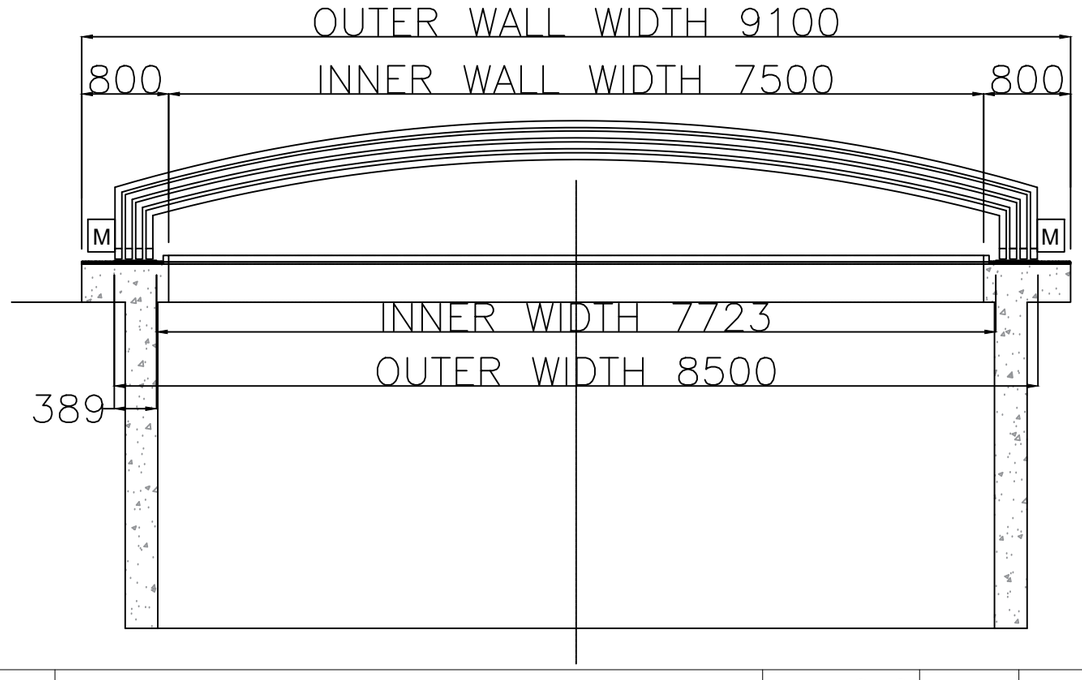

REV.	DESCRIPTION.	REVISED BY	SIGN	DATE
002	REVISED GA DRAWING PER SINGLE SIDE OUT OF CLEAR OPENING	MAHESH S.		08.10.22
001	REVISED GA DRAWING PER BI-PARTING WITHIN CLEAR OPENING	MAHESH S.		06.10.22
000	RELEASED GA DWG FOR APPROVAL	GAURAV J.		20.08.22

This drawing & design is the property of NIHVA TECHNOLOGIES. Not to be sold or copied to any other concern.

TITLE
ASSLY LAYOUT

NIHVA
NIHVA TECHNOLOGIES PVT. LTD.

	NAME	SIGN	DATE
DRAWN	G.J.		20.08.22
CHECK	A.K.		20.08.22
APPRD.	V.T.		20.08.22

CLIENT - MR. PRANAV
LOCATION - NOIDA_IN
PRODUCT - RETRACTABLE ROOF

If any queries contact : projectsautomation@nihva.com
NIHVA\22-23\02XX
REV- 0

ALL DIMENSION ARE IN mm
SCALE: NTS
SHEET: 01 OF 01