



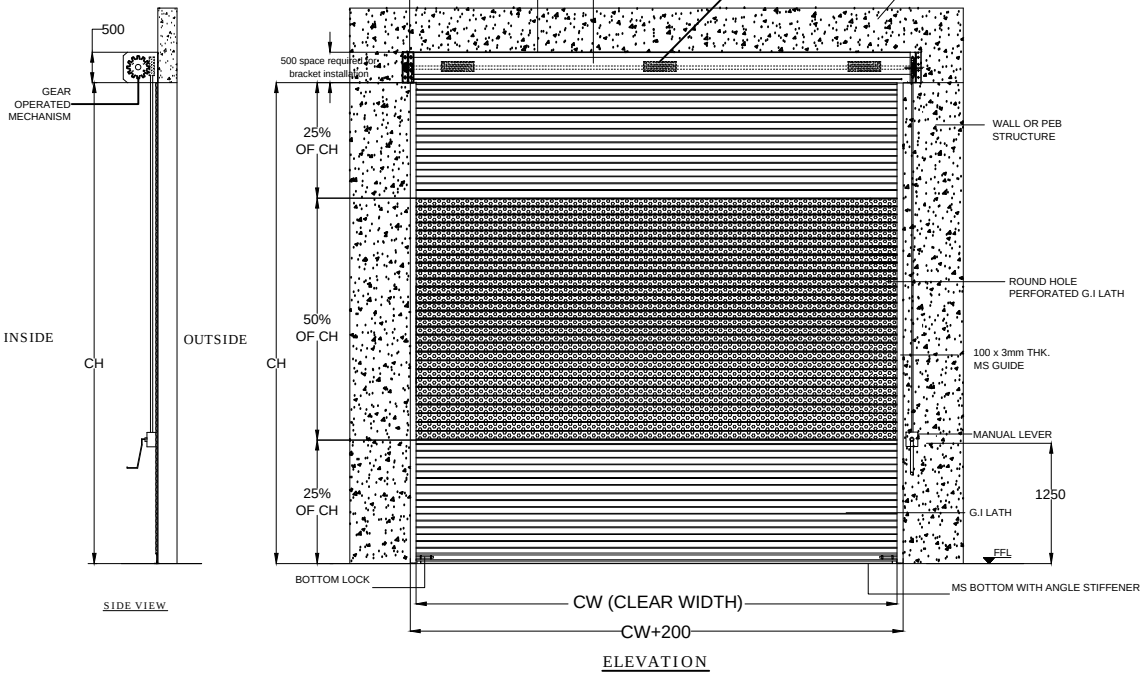


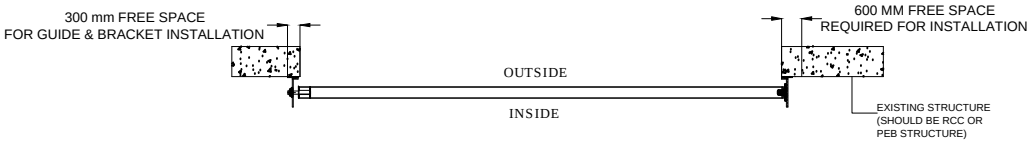

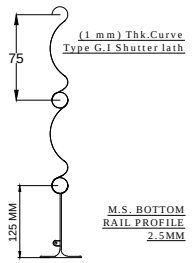

M.S. BOTTOM RAIL PROFILE 2.5MM

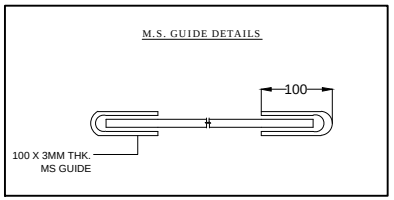

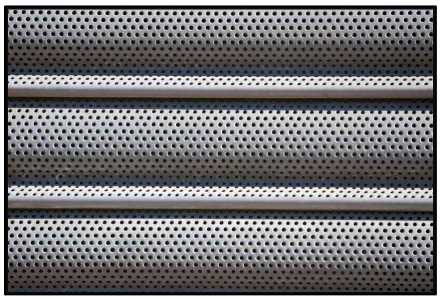

ROUND HOLE PERFORATED G.I LATH

NOTE:
1 REQUIRED STRUCTURE FOR SHUTTER SHALL BE IN CLIENT SCOPE.
2.PLEASE CONFIRM RAL COLOR FOR ROLLING SHUTTER.

CLEAR WIDTH	CLEAR HEIGHT	QTY.
3000 MM	2150 MM	5 NOS
3000 MM	3000 MM	8 NOS
4500 MM	3000 MM	9 NOS

TOLERANCE - ±10mm

This drawing & design is the property of NIHVA TECHNOLOGIES. Not to be sold or copied to any other concern.

TITLE
GEAR OPERATED ROLLING SHUTTER

	NAME	SIGN	DATE
DRAWN	P.A		04.11.2019
CHECK	G.J		04.11.2019
APPRD.			

If any queries contact : design@nihva.com

ALL DIMENSION ARE IN mm

NIHVA TECHNOLOGIES PVT. LTD.
NIHVA TECHNOLOGIES PVT. LTD. PUNE
Tel : 020 66304033
Email:- info@nihva.com
Website:- www.nihva.com

CLIENT - DSP DESIGN & ASSOCIATES

PROJECT -

SITE LOCATION - PUNE

DWG. NO. : NIHVA/19-20/0146 | REV- 01

SCALE: NTS | WT: | SHEET: 01 OF 01