

THIS PRINT IS THE PROPERTY OF NIHVA IT IS TO BE USED ONLY FOR THE PURPOSE FOR WHICH IT WAS LENT AND MUST NOT BE USED IN ANY WAY DERTIMENTAL TO THE INTEREST OF THIS COMPANY AND IS SUBJECT TO RETURN ON DEMAND.

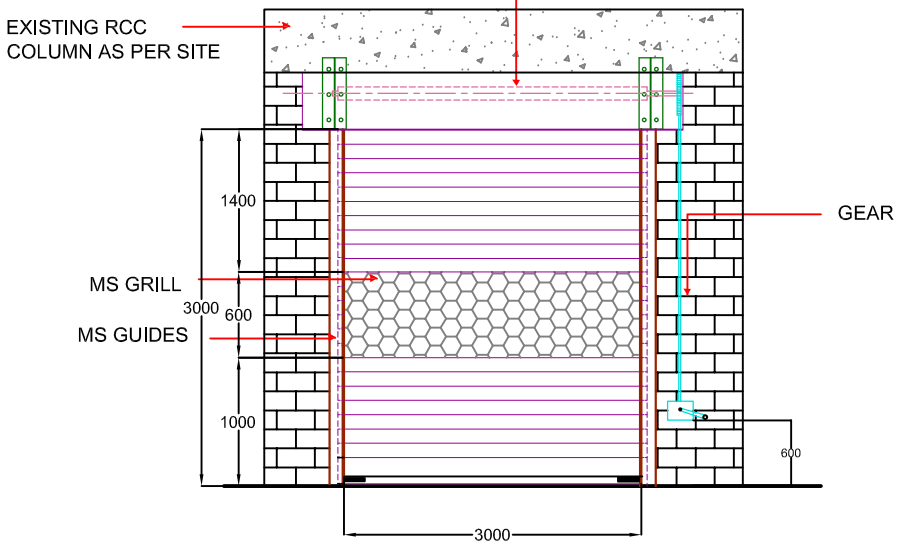


INSIDE ELEVATION


Clear Opening size:-
(W)3.0m x (H)3.0m

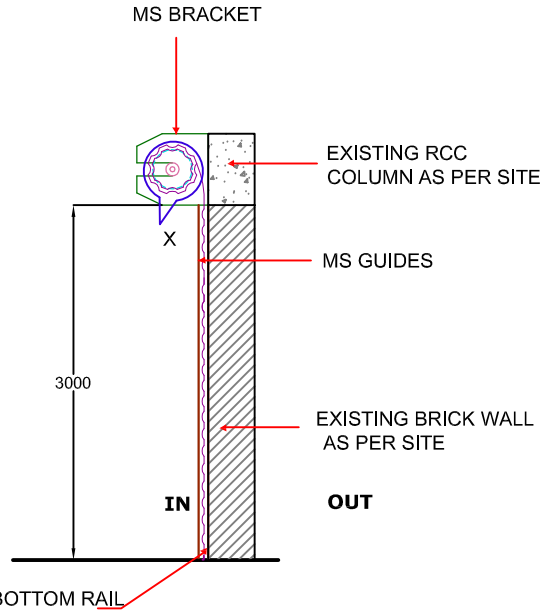


SIDE VIEW

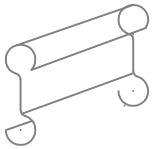


Box/Straight Type Slat Profile

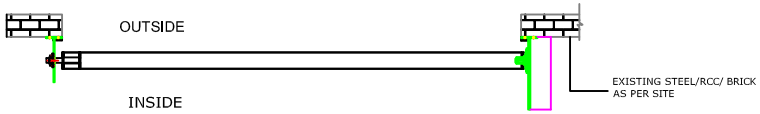

PLAN

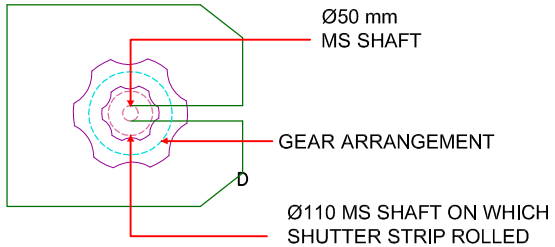

Bracket

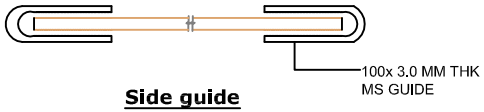

Side guide

NOTE :- Total no. of shutter Is 05 nos.

Location	:- 33 K.V Reciving station
Size	:- 3.0m(W) X 3.0M (H)
Qty	:- 03 nos
Type	:- RS7-Partly grilled

Location	:- Cafeteria
Size	:- 3.0m(W) X 3.0M (H)
Qty	:- 02 nos
Type	:- GRS4-Partly grilled

TITLE: Manual Gear Operated Rolling Shutter	DO NOT SCALE DRAWING		NIHVA TECHNOLOGIES PVT. LTD. Pune:-411044 Tel :- 020 66304033 Email :- info@nihva.com
		SIGN / DATE	
CLIENTS APPROVEL:–	DRAWN	Anil	CLIENT: Shapoorji Palonji Co. Ltd
	CHECK		PROJECT / SITE: GE,CHAKAN
	ENG		PRODUCT NAME:
UNLESS & OTHERWISE SPECIFIED DIMENSION ARE IN M.M.	APPRD.		DWG. NO.: NVA/SP/04R
	PROD		REV.: 0
	MFG		SCALE: NTS WT: SHEET: 1 OF 1
	Ref. No.		