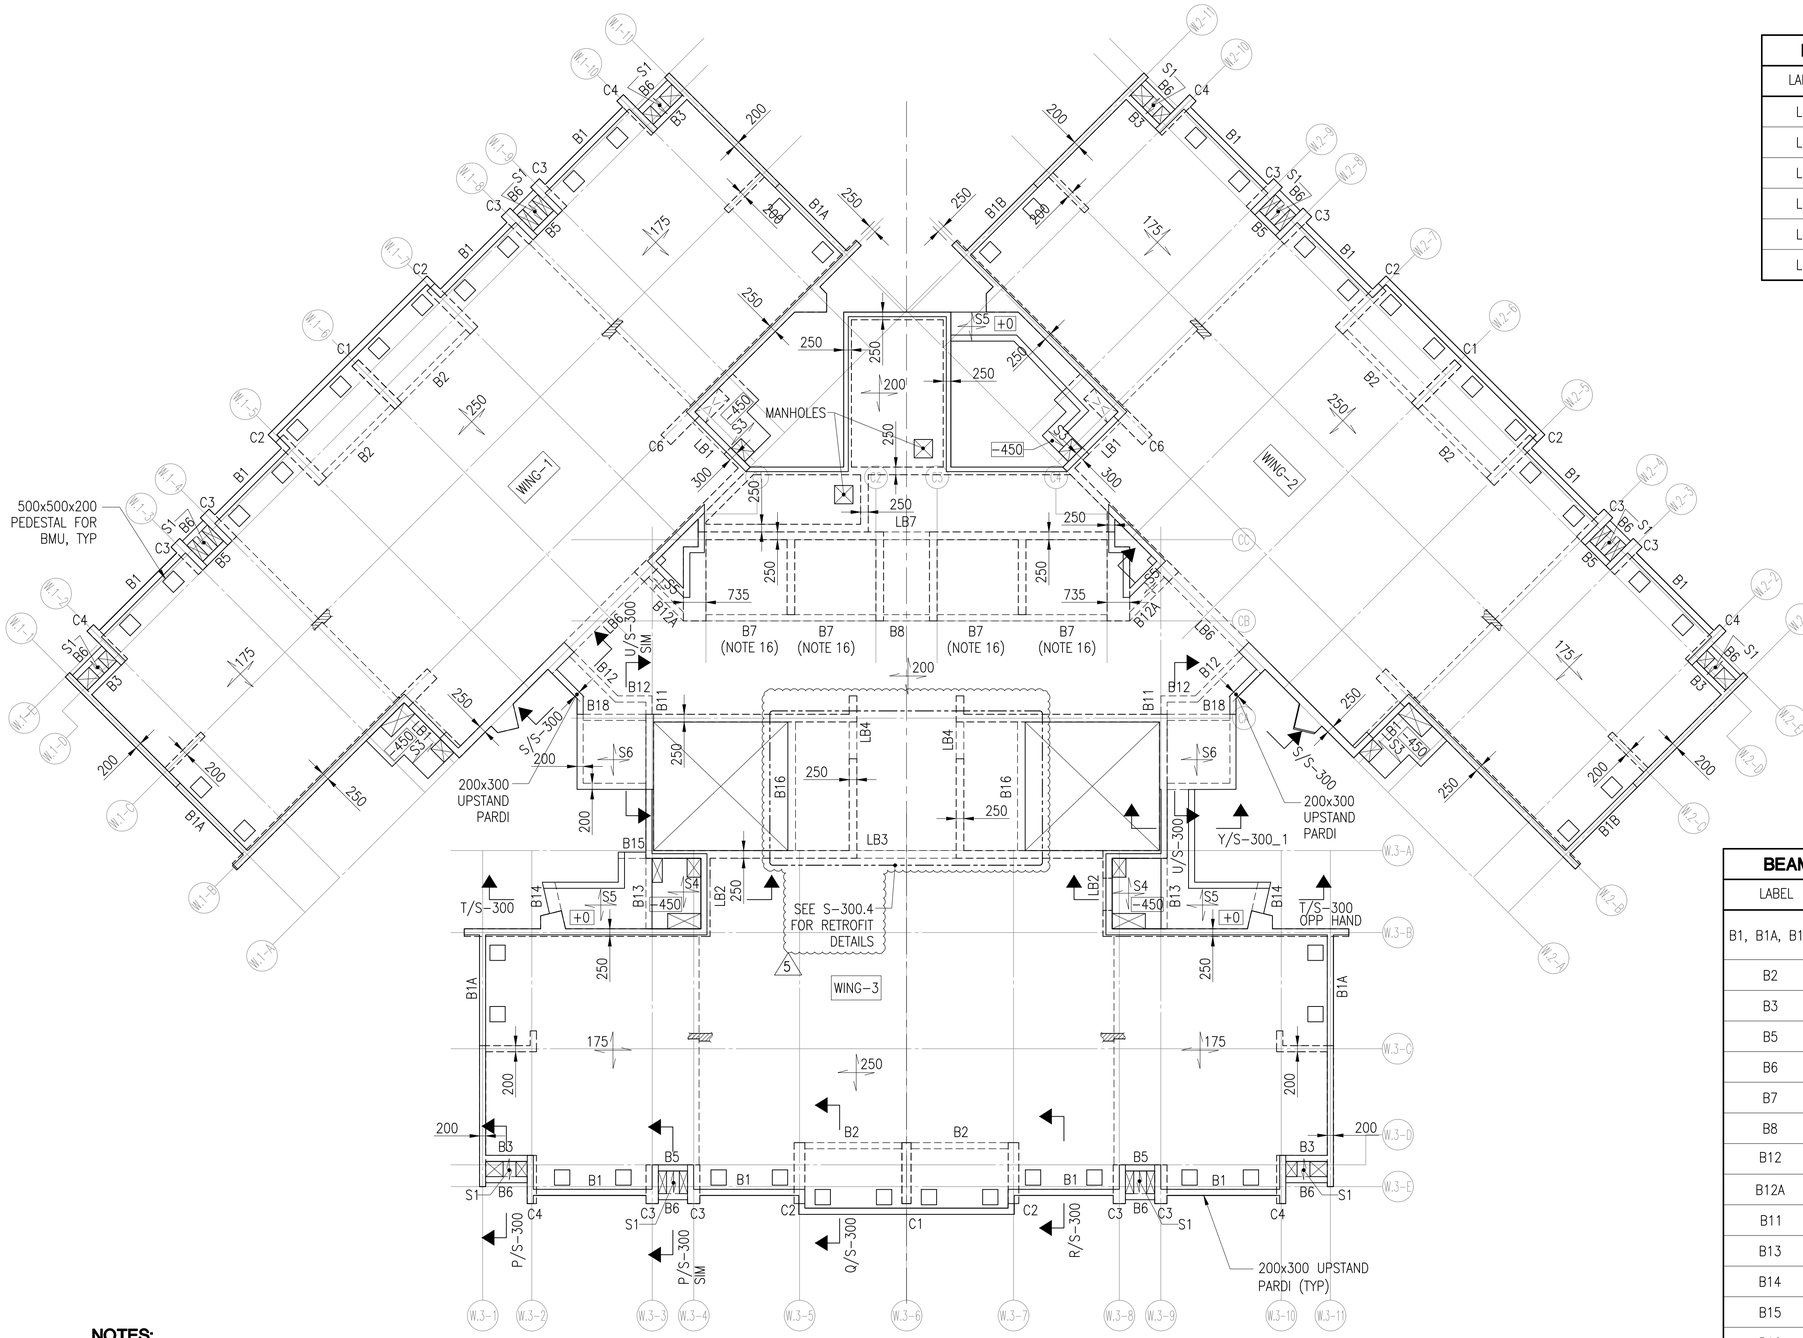


LINK BEAM SCHEDULE

LABEL	SIZE (MM)	REMARK
LB1	300 x 750	TOP OF BEAM AT +0
LB2	300 x 750	TOP OF BEAM AT +0
LB3	250 x 600	TOP OF BEAM AT +0
LB4	250 x 600	TOP OF BEAM AT +0
LB6	450 x 600	TOP OF BEAM AT +0
LB7	250 x 750	TOP OF BEAM AT +0

COLUMN SCHEDULE

LABEL	SIZE (MM)
C1	300 x 1990
C2	350 x 1990
C3	400 x 1265
C4	300 x 1575

SLAB SCHEDULE

LABEL	THICKNESS	SUNK FROM REF. ELEV.
S1	150	-450
S3	150	-450
S4	150	-450
S6	200	+0
S5	150	+0

BEAM SCHEDULE

LABEL	SIZE (MM)	REMARK
B1, B1A, B1B	200 x 450	200 x 300 UPSTAND PARDI
B2	200 x 450	
B3	200 x 600	200x300 UPSTAND PARDI
B5	200 x 600	200x300 UPSTAND PARDI
B6	200 x 350	
B7	200 x 375	
B8	200 x 600	
B12	200 x 600	
B12A	200 x 600	
B11	200 x 600	
B13	200 x 600	
B14	400 x 600	
B15	200 x 600	
B16	250 x 400	
B17	200 x 400	
B18	200 x 525	

NOTES:

1. TOP OF CONCRETE IS AT REFERENCE ELEVATION NOTED IN ARCH DWGS. UNLESS OTHERWISE NOTED [XXX] ; WHERE [XXX] IS MEASURED WITH RESPECT TO REFERENCE ELEVATION IN MM.
2. REFER S-300 FOR SECTIONS.
3. SOLID CONCRETE SLAB IS INDICATED. SL
4. REINFORCEMENT SHALL BE OF FE 500D (TESTED VARIETY), UON.
5. CONCRETE STRENGTH SHALL BE AS FOLLOWS, UON:
   SLABS & FLOOR BEAMS : M40
   LINK BEAMS, WALLS & COLUMNS : M40
6. READ THIS DRAWING IN CONJUNCTION WITH ARCHITECTURAL DRAWINGS.
7. READ THIS DRAWING IN CONJUNCTION WITH MECHANICAL, ELECTRICAL & PLUMBING DRAWINGS.
8. REFER ARCHITECTURAL DRAWINGS FOR THE LOCATION OF NON STRUCTURAL WALLS.
9. REFER MEP DRAWINGS FOR THE LOCATIONS & DETAILS OF SLEEVES.
10. ALL DIMENSIONS ARE IN MM.
11. [Ψ] INDICATES INFORMATION TO BE PROVIDED BY ARCHITECT.
12. INDICATES NON STRUCTURAL RCC WALL
13. ALLOWABLE FILL DEPTH ON ROOF LEVEL IS 100 MM
14. SEE ARCHITECTURAL DRAWING FOR THE PARDI ABOVE ROOF
15. SEE ARCHITECTURAL DRAWINGS FOR THE LOCATION OF SOLAR PANEL.
16. PROVIDE BEAM B17 (200x400) TO SUPPORT HOIST WAY BEAM. CONTRACTOR SHALL CO-ORDINATE LOCATION OF BEAM WITH ELEVATOR SHOP DRAWINGS.

LERA

Leslie E. Robertson Associates
Consulting Engineers (India), Pvt. Ltd.
The Ruby, North Wing, 23rd Floor,
29 Senapati Bapat Marg,
Dadar West, Mumbai – 400 028 India
Tel: 91 22 2437 6001 and 91 22 2437 6003

Client
Oberoi Realty Limited
Commerz, 3rd Floor, International Business Park,
Oberoi Garden City, Mumbai – 400 063 India
Tel: +91 22 6677 3333 Fax: +91 22 6677 3334

No.	Revision/Issue	Date
R5	REVISED AS MARKED	27 JAN 23
R4	REVISED AS MARKED	27 JUL 22
R3	REVISED AS MARKED	14 FEB 22
R2	REVISED AS MARKED	01 FEB 22
R1	REVISED AS MARKED	06 SEP 21
R0	ISSUED FOR CONSTRUCTION	21 JUL 21

Warning:
© Copyright LESLIE E. ROBERTSON ASSOCIATES, CONSULTING ENGINEERS (INDIA), PVT. LTD. IT IS A VIOLATION OF LAW FOR ANY PERSON, UNLESS ACTING UNDER THE DIRECTION OF A PROFESSIONAL, LICENSED IN THE STATE OF THIS PROJECT, TO ALTER IN ANY WAY THESE DRAWINGS. WHERE ANY ITEM IS ALTERED, THE SUPERVISING PROFESSIONAL SHALL AFFIX TO THE ITEM HIS SEAL AND THE INSCRIPTION "ALTERED BY" FOLLOWED BY HIS SIGNATURE, THE DATE, AND A SPECIFIC DESCRIPTION OF THE ALTERATION.

Professional Stamp:

Phase:
GOOD FOR CONSTRUCTION

Project Title:
MAXIMA

Drawing Title:
FLOOR PLAN
ROOF LEVEL

Drawn: LERA	Design: LERA
Check: LERA	Date: 21 JULY 2021
Scale: 1:100	Project Number: P 992

Sheet:
S-130