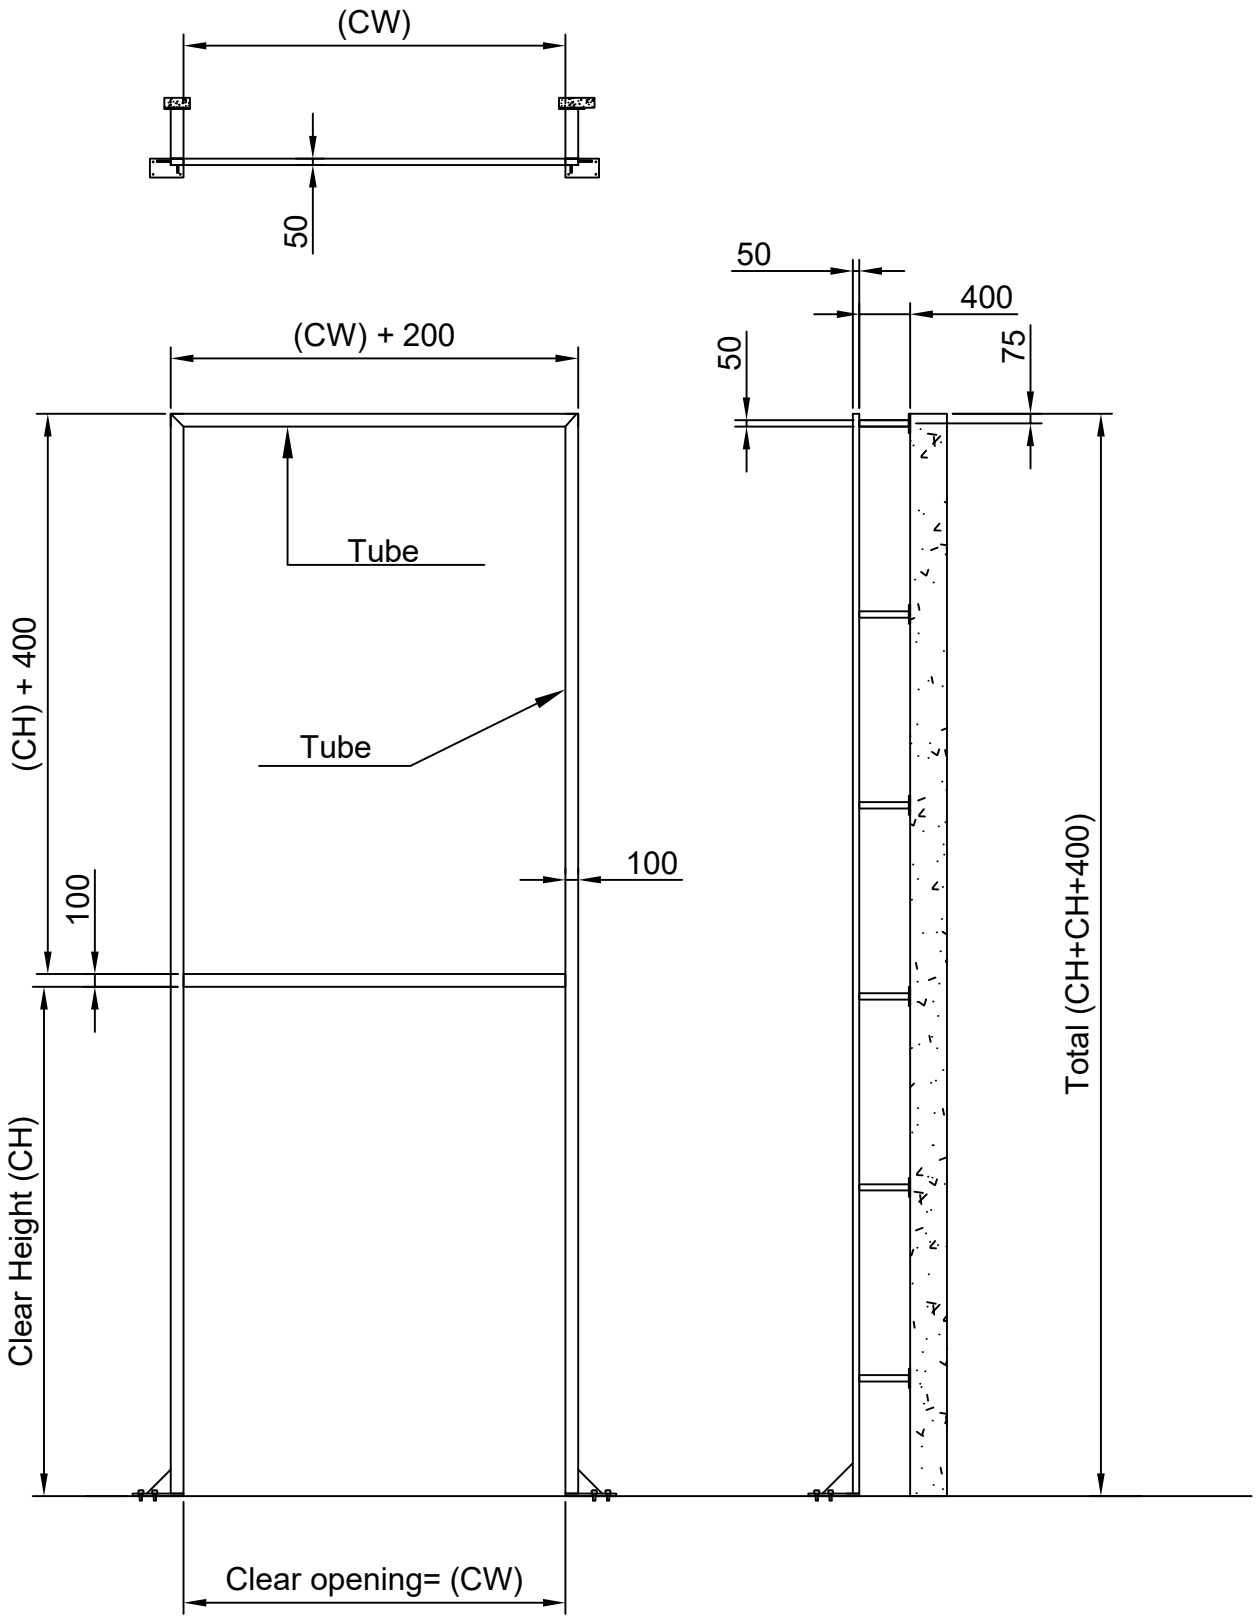


NOTE:-

1.All dimension are in MM

2.Required all civil work will be Client scope

This drawing & design is the property of NIHVA TECHNOLOGIES. Not to be sold or copied to any other concern.

TITLE:- MS Rect.tubular structure - VL

	NAME	DATE	SIGN
DRAWN	S.J	10-01-2023	
CHECK	A.K	10-01-2023	
APPRD.	V.T	10-01-2023	

If any queries contact : design@nihva.com

ALL DIMENSION ARE IN mm

NIHVA TECHNOLOGIES PVT. LTD.
NIHVA TECHNOLOGIES PVT. LTD. PUNE
Tel : 020 66304033
Email:- info@nihva.com
Website:- www.nihva.com

CLIENT - Systematic Conscom Ltd.

LOCATION -

PRODUCT - QTY :-

DWG NO:-NIHVA/23-24/57 REV- 0

SCALE: NTS SCALE:-- 1:1 SHEET: 01 OF 01