




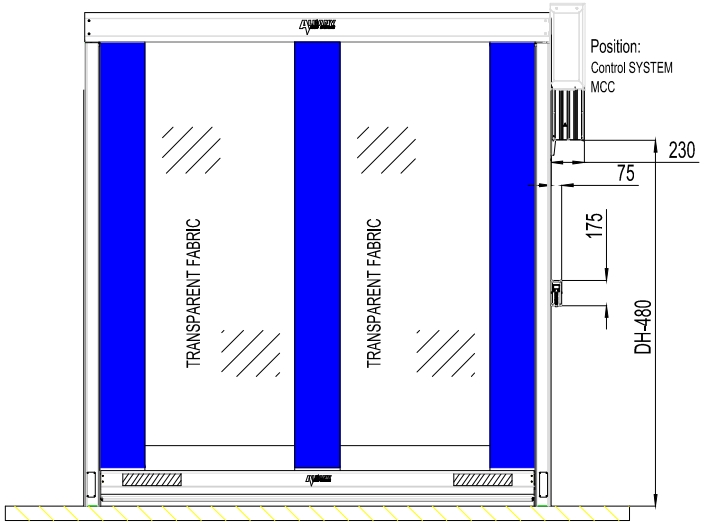


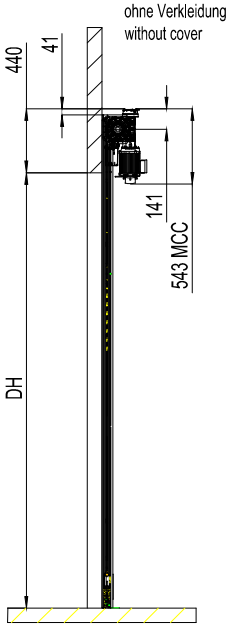

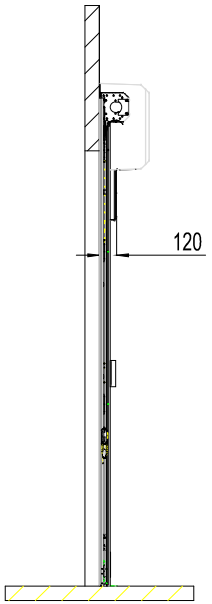

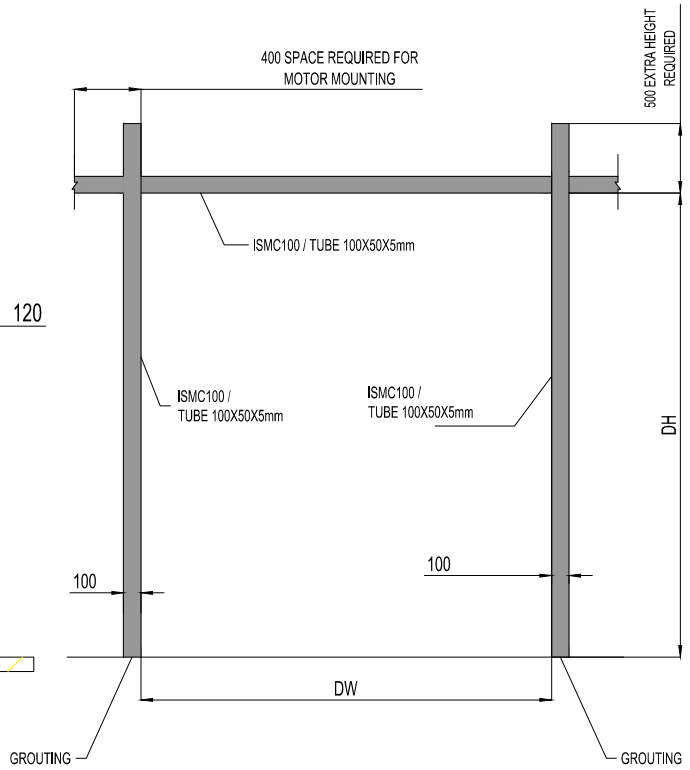

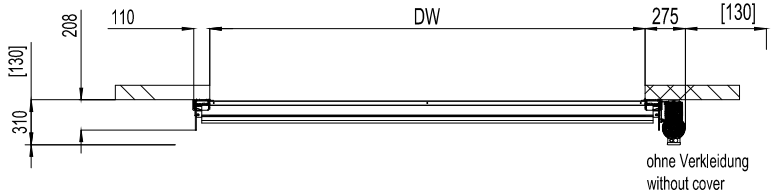

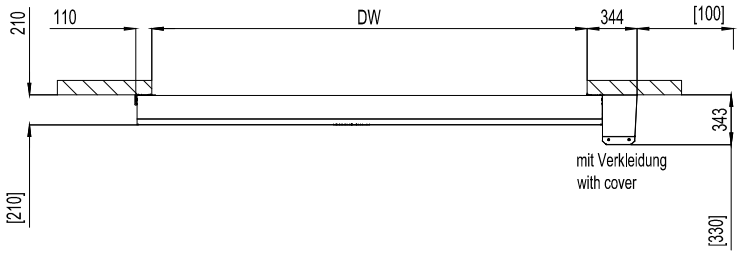

NOTE : ALL CIVIL & STRUCTURAL WORK WILL BE IN CLIENT SCOPE.

CURTAIN : PVC FABRIC
RAL : 5010 BLUE

CLEAR WIDTH(DW)	CLEAR HEIGHT(DH)	QTY
3200	2500mm	01 NO

Tolerance ±3 mm (for all dimensions)

Dimensions in [ ] ==> clearance for installation

This drawing & design is the property of NIHVA TECHNOLOGIES. Not to be sold or copied to any other concern.

TITLE: HIGH SPEED DOOR RP300 & STRUCTURE

NIHVA TECHNOLOGIES PVT. LTD. PUNE
Tel : 020 66304033
E-mail - info@nihva.com
Website - www.nihva.com

	NAME	SIGN	DATE
DRAWN	P.A		26.02.2020
CHECK	G.J		26.02.2020
APPVED			

CLIENT :- LEAN AUTOMATION PVT LTD
PROJECT :-
LOCATION :- CHAKAN
If any queries contact : design@nihva.com
DWG. NO. :- NIHVA/19-20/0219 REV.-00
ALL DIMENSION ARE IN mm
SCALE: NTS WT: SHEET: 01 OF 01