
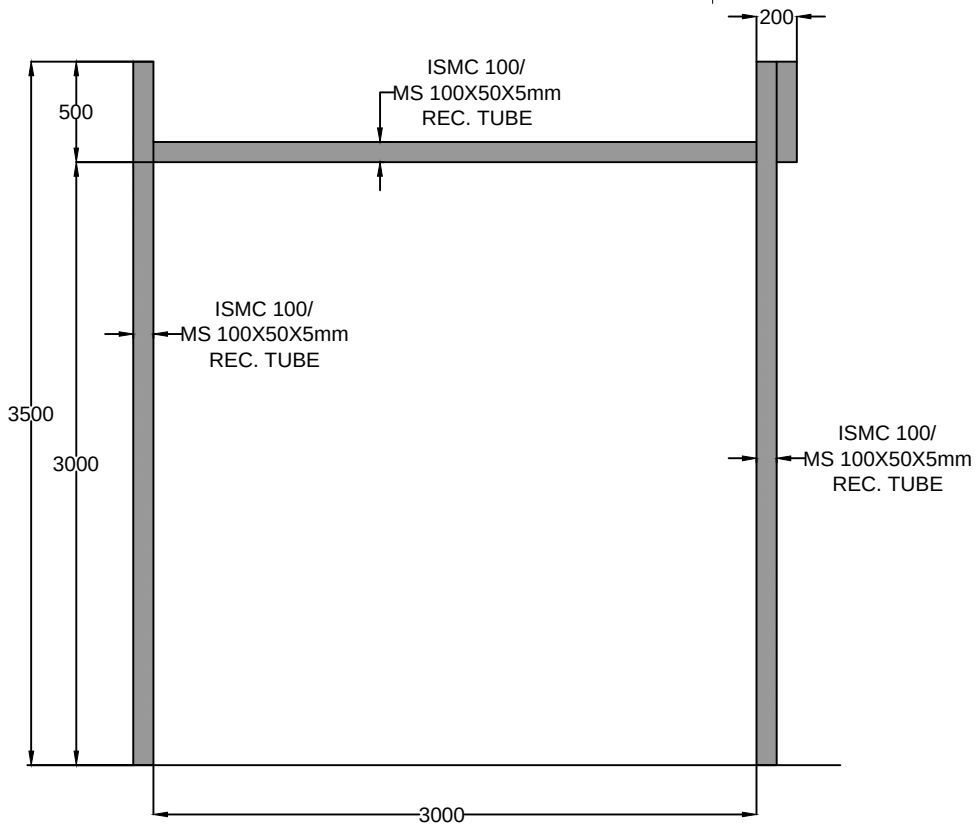


MS STRUCTURE

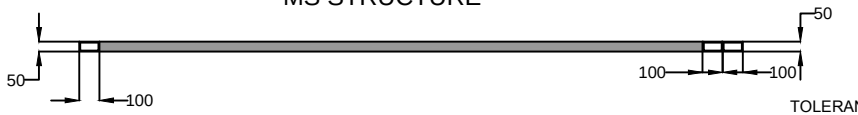

TOLERANCE - ±10mm

CLEAR WIDTH	CLEAR HEIGHT	QTY.
3000 mm	3000 mm	01NOS

This drawing & design is the property of NIHVA TECHNOLOGIES. Not to be sold or copied to any other concern.

TITLE	ROLLING SHUTTER STRUCTURE			NIHVA TECHNOLOGIES PVT. LTD. PUNE Tel : 020 66304033 Email:- info@nihva.com Website:- www.nihva.com	
	NAME	SIGN	DATE		
DRAWN	SURAJ		07-05-2018	CLIENT - FERRERO INDIA PVT. LTD	
CHECK	OMKAR		07-05-2018	PROJECT -	
APPRD.	PRADEEP		07-05-2018	SITE LOCATION - BARAMATI.	
If any queries contact : design@nihva.com				DWG. NO. : NIHVA/18-19/0030	REV- 0
ALL DIMENSION ARE IN mm				SCALE: NTS	WT: SHEET: 01 OF 01