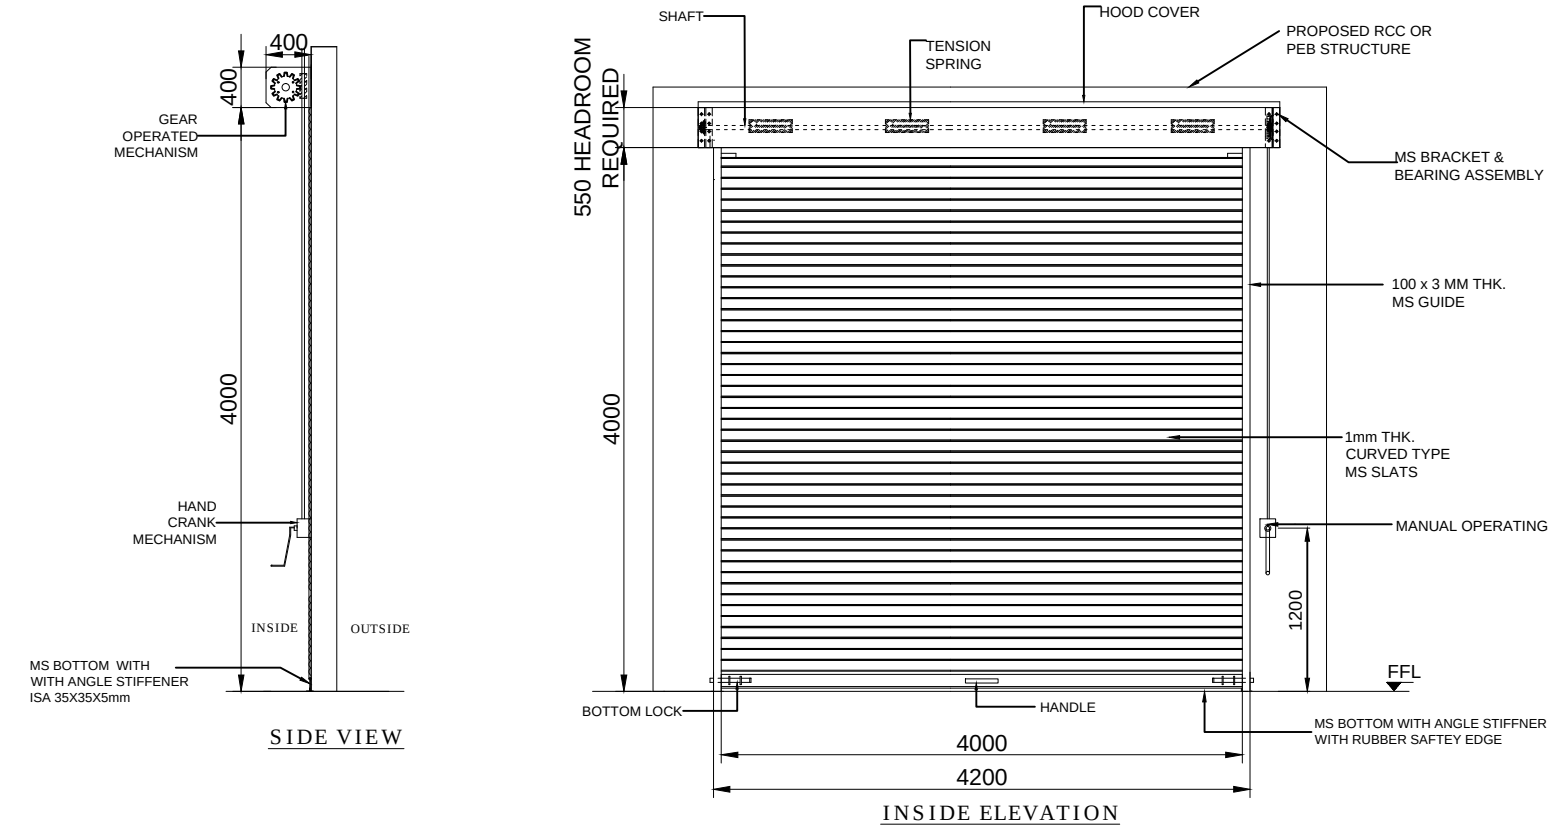


S.N.	LOCATION	SIZE	QUANTITY
1	-	4000(W)X4000(H)	01
TOTAL QTY. OF SHUTTER			01

TOLERANCE - ±10mm

NOTE:-
1. REQUIRED STRUCTURE FOR ROLLING SHUTTER SHALL BE IN CLIENT SCOPE.
2. ALL REQUIRED CIVIL WORK IN CLIENT SCOPE.
3. FOR FINAL FINISH CLIENT SHOULD CONFIRM RAL COLOR SHADE.
4. 3 PHASE POWER SUPPLY SHOULD BE PROVIDE.

SR.NO	REVISION NO	DESCRIPTION	DATE	DRAW
01	R01	CHANGED MOTORISED ROLLING SHUTTER TO GEAR OPERATED ROLLING SHUTTER	14-12-18	SURAJ

This drawing & design is the property of NIHVA TECHNOLOGIES. Not to be sold or copied to any other concern.

TITLE
GEAR OPERATED ROLLING SHUTTER 4mX4m

	NAME	SIGN	DATE
DRAWN	SURAJ		07.07.2018
CHECK	PRADEEP		07.07.2018
APPRD.	R.D		07.07.2018

If any queries contact : design@nihva.com

ALL DIMENSION ARE IN mm

NIHVA TECHNOLOGIES PVT. LTD.
NIHVA TECHNOLOGIES PVT. LTD. PUNE
Tel : 020 66304033
Email:- info@nihva.com
Website:- www.nihva.com

CLIENT - REWARD CONSTRUCTIONS PVT LTD.
PROJECT - REWARD CONSTRUCTIONS PVT LTD.
SITE LOCATION - RANJANGAON MIDC.
DWG. NO. : NIHVA/18-19/0193/R01 | REV- 01
SCALE: NTS | WT: | SHEET: 01 OF 01