


DWG.NO: SALT_1729_GA_01_R0

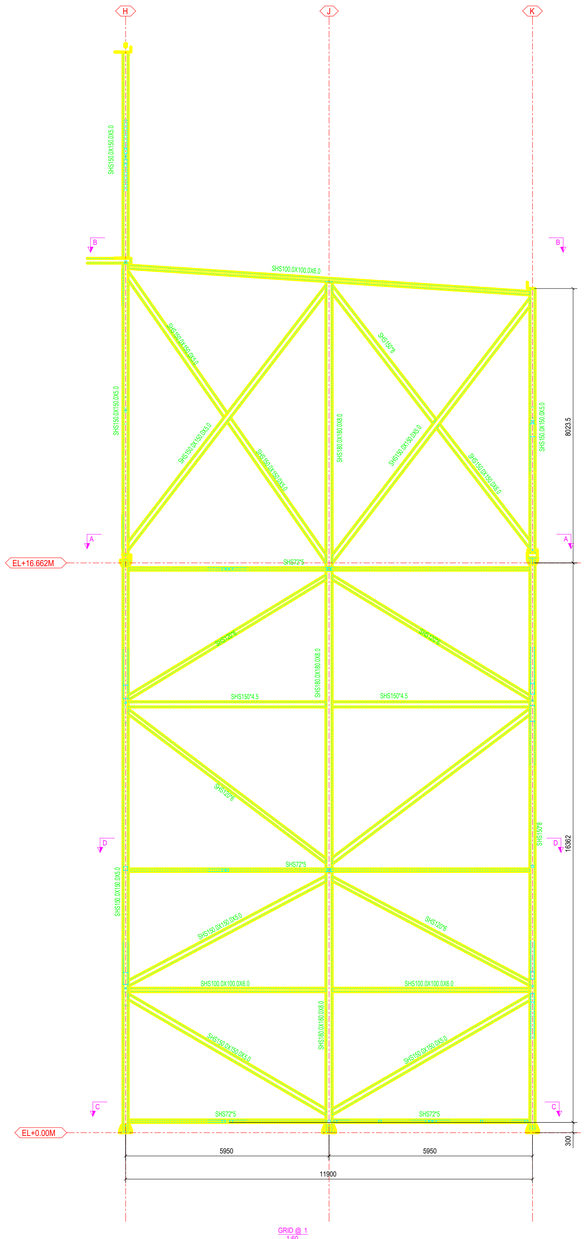


GRID @ 1
1:60

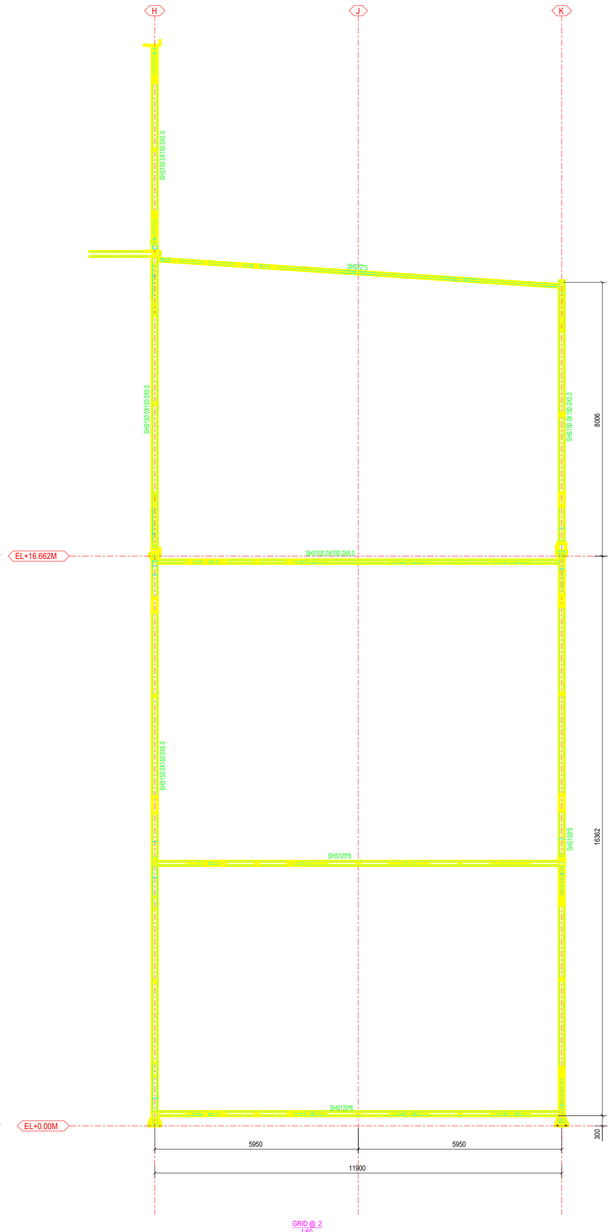


GRID @ 2
1:60

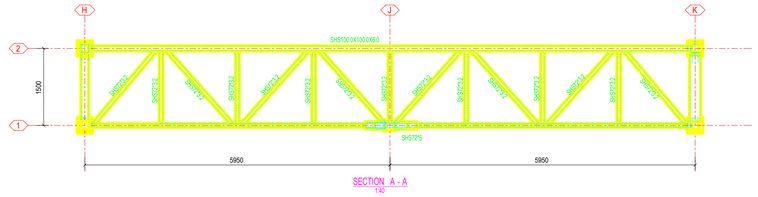


SECTION A - A
1:40

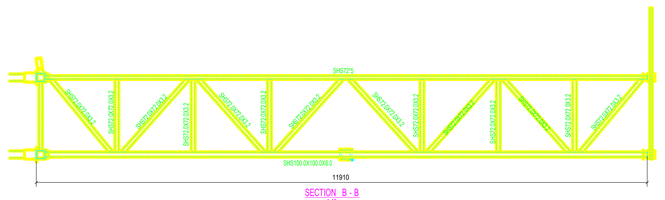

SECTION B - B
1:40

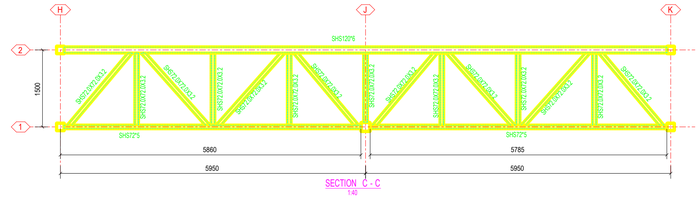

SECTION C - C
1:40

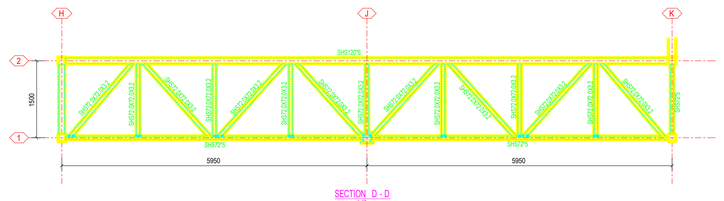

SECTION D - D
1:40

NOTES :-

1. ALL DIMENSIONS ARE IN MM & LEVEL ARE IN METER.
2. ALL STRUCTURAL STEEL AS PER IS:2062.
3. PROVIDE WELDING AS PER IS:816.
4. PROVIDE MIN. 6MM SHOP WELD AND 8MM SITE WELD
5. USE ELECTRODS AS PER IS:814 (PT.-I).
6. FILLET/ BUTT WELD SHALL BE OF 6MM SIZE AND SHALL BE CONTINUOUS.
7. FABRICATION AND ERECTION SHALL BE AS PER IS:800 AND IS:803.
8. WELD SHALL BE GROUND SMOOTH.
9. ALL GUSSET PLATES SHALL BE MIN. 8 THK.
10. ALL M.S. BLACK BOLTS AND NUTS SHALL CONFORM TO IS:1363(PT. 1 TO 3).
11. LIVE LOAD ON ROOF = 75KG/SQM.
12. STRUCTURE SHALL BE APPLIED WITH ONE COAT OF RED OXIDE ZINC CROMATE PRIMER AFTER FABRICATION FOLLOWED ONE MORE COAT BEFORE ERECTION. FINALLY APPLY 2 COATS OF SYNTHETIC ENAMAL OF APPROVED QUALITY.
13. STRUCTURAL MEMBER SHALL BE OF 355N/MM^2 MIN STRENGTH.

REV.NO.	DESCRIPTION.	REV.DATE	DRAWN.	CHKD.	APPD.
0	GA DRAWING FOR APPROVAL	05.11.22	MEGHA	HAB	HAB

DWG.TITLE :-	GA DRAWING FOR DOOR FRAME TRUSS BETWEEN 84M & 99M
PROJECT	MEGADOOR INSTALLATION AT HYDRABAD AIRPORT
CLIENT	GMR

SALT Design Services
NIHVA TECHNOLOGIES PVT. LTD.

SALT DESIGN SERVICES

NIHVA TECHNOLOGIES PVT. LTD. PUNE
Tel : 020 66304033
Email:- info@nihva.com
Website:- www.nihva.com

DRAWN :RRK	CHECKED : HAB	SCALE: 1:100
APPROVED : HAB	JOB CODE. : 1729	DATE: 05.11.2022
DWG.NO: SALT_1729_GA_01_R0	(SH-1OF1)	REV. - R0 SIZE. - A0

A1 [841 x 594]