

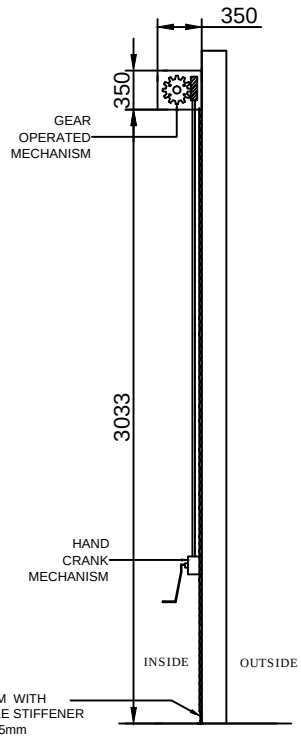



SIDE VIEW

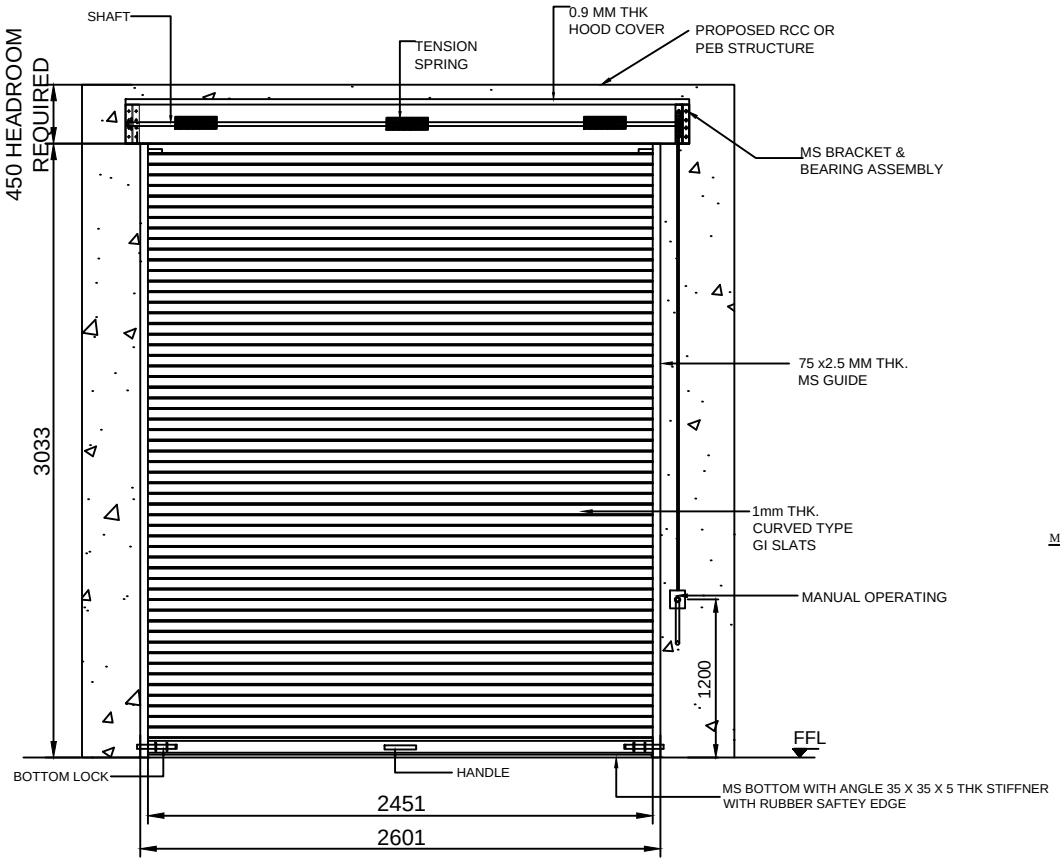


INSIDE ELEVATION

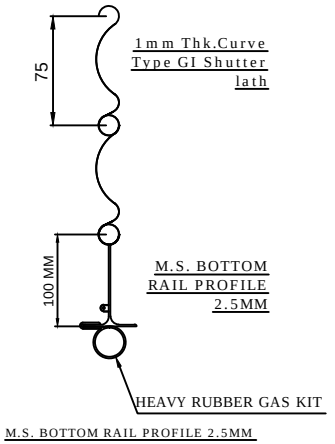

M.S. BOTTOM RAIL PROFILE 2.5MM

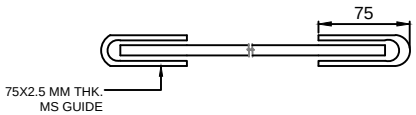

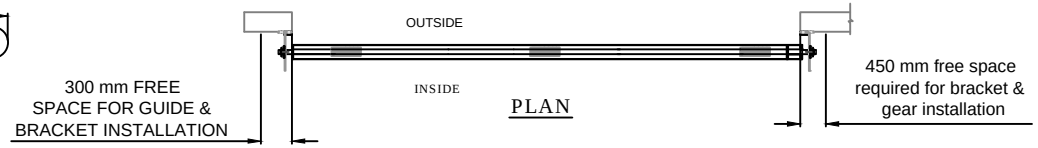

PLAN

S.N.	LOCATION	SIZE	QUANTITY
1	B50	2451(W)X3033(H)	11 Nos

NOTE-
1. ALL CIVIL WORK WILL BE CLIENT'S SCOPE.
2.STRUCTURE REQUIRED FOR SHUTTER IS IN CLIENT'S SCOPE.
3.FINAL FINISH OF SHUTTER WILL BE IN POWDER COATING OF APPROVED COLOR i.e.RAL 7001.
4.DESIGN OF SHUTTER IS AS PER I.S. 6248:1979 STANDARDS.

TOLERANCE - ±10mm

This drawing & design is the property of NIHVA TECHNOLOGIES. Not to be sold or copied to any other concern.

TITLE	GEAR OPERATED ROLLING SHUTTER 2.451mX3.033m Right side gear box.		
	NAME	SIGN	DATE
DRAWN	SURAJ		05.09.2018
CHECK	PRADEEP		05.09.2018
APPRD.	R.D		05.09.2018
If any queries contact : design@nihva.com			
ALL DIMENSION ARE IN mm			

NIHVA TECHNOLOGIES PVT. LTD.
Website:- www.nihva.com
NIHVA TECHNOLOGIES PVT. LTD. PUNE
Tel : 020 66304033
Email:- info@nihva.com

CLIENT -
PROJECT -
SITE LOCATION -
DWG. NO. : NIHVA/18-19/VDR/117 | REV- 0
SCALE: NTS | WT: | SHEET: 01 OF 01