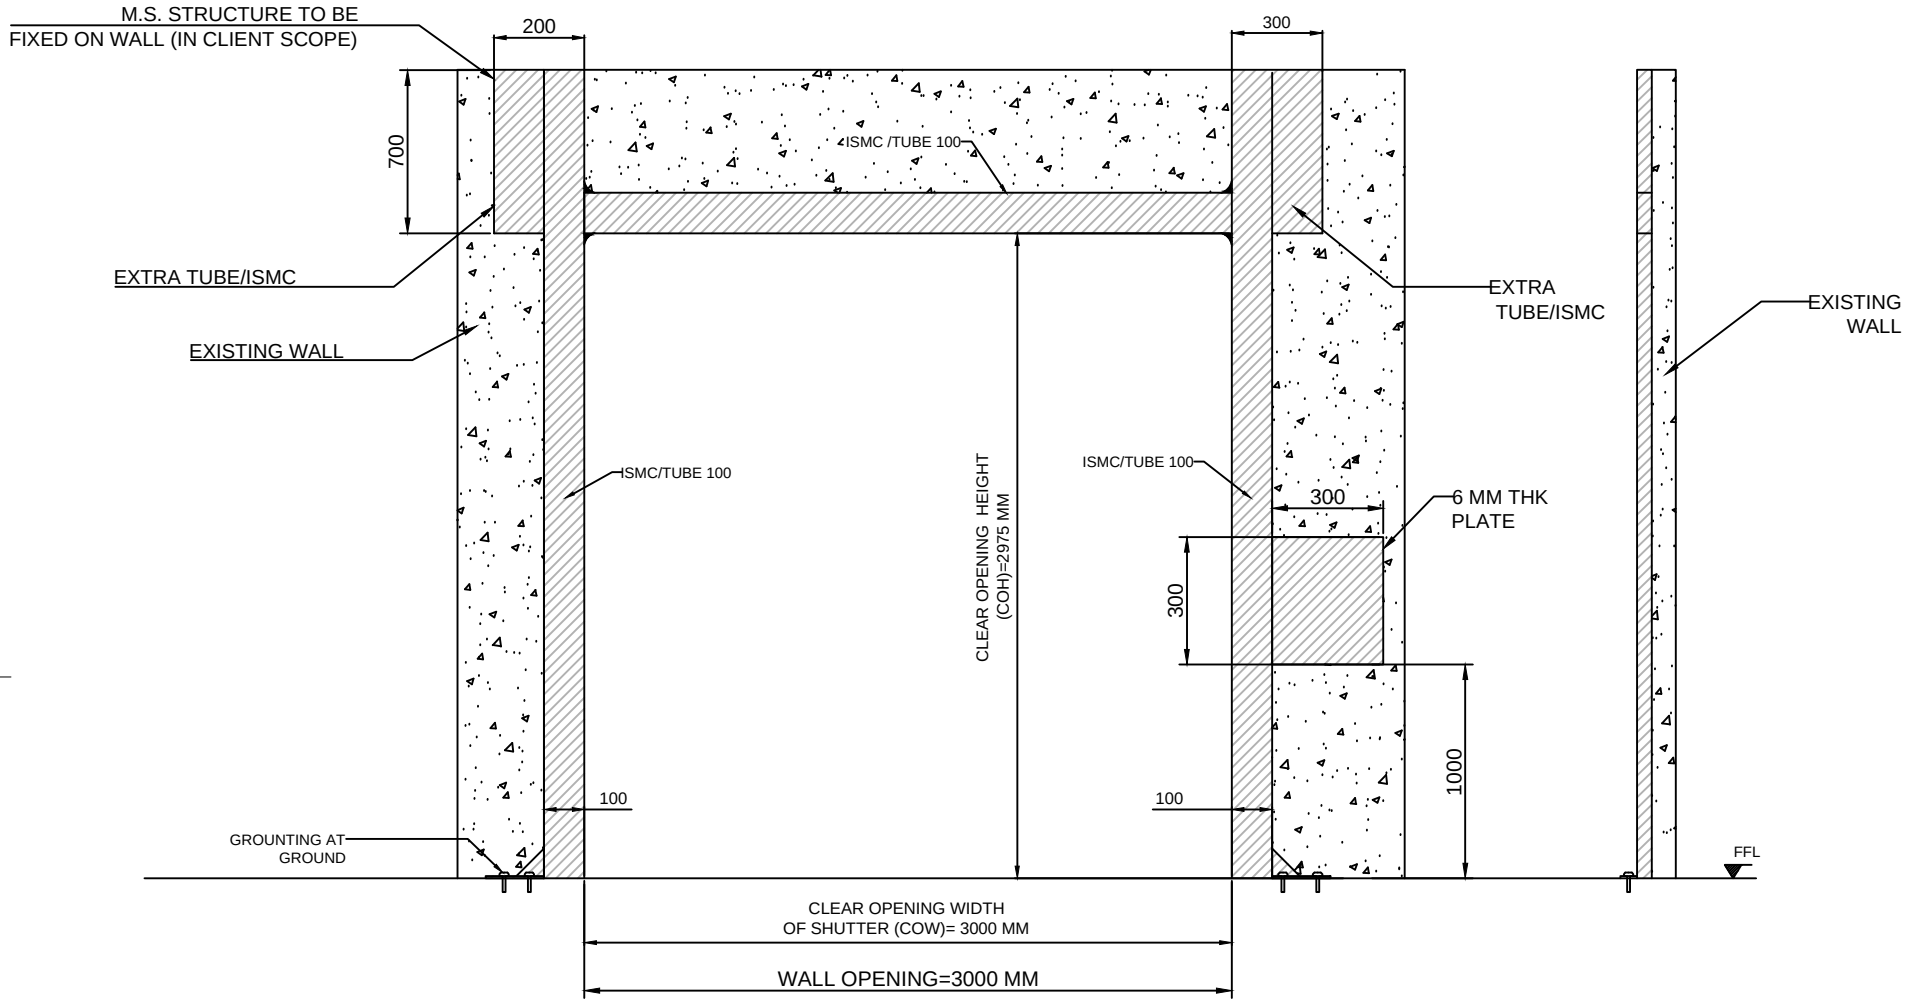



STRUCTURE

| SR NO | CLEAR OPENING WIDTH(CW) | CLEAR OPENING HEIGHT(CH) | QTY | LOCATION |
|---|---|---|---|---|
| 1 | 3000 | 2975 | 1 | 1 |

NOTES-
(1) MS STRUCTURE , FITTING & ALL CIVIL WORK IS IN CLIENT SCOPE.
(2) SHUTTER WILL BE ONLY INSTALLED AFTER READINESS OF STRUCTURE AS PER DRAWING PROVIDED.
(3) SPACE OF 700 mm ABOVE CLEAR HEIGHT IS REQUIRED FOR INSTALLATION OF GEAR OPERATED ROLLING SHUTTER.

TOLERANCE - ±10mm

This drawing & design is the property of NIHVA TECHNOLOGIES. Not to be sold or copied to any other concern.

TITLE M.S. STRUCTURE 1

NIHVA TECHNOLOGIES PVT. LTD.
NIHVA TECHNOLOGIES PVT. LTD. PUNE
Tel : 020 66304033
Website:- www.nihva.com
Email:- info@nihva.com

| | NAME | SIGN | DATE |
|---|---|---|---|
| DRAWN | S.M.S. | | 11.1.2021 |
| CHECK | V.T. | | 11.1.2021 |
| APPRD. | | | |

CLIENT - TRANS ENGG
PROJECT -
SITE LOCATION -
If any queries contact : design@nihva.com
DWG. NO. : NIHVA/20-21/0129
REV- R00
ALL DIMENSION ARE IN mm
SHEET: 01 OF 02