

PROPOSED PLAN LAYOUT

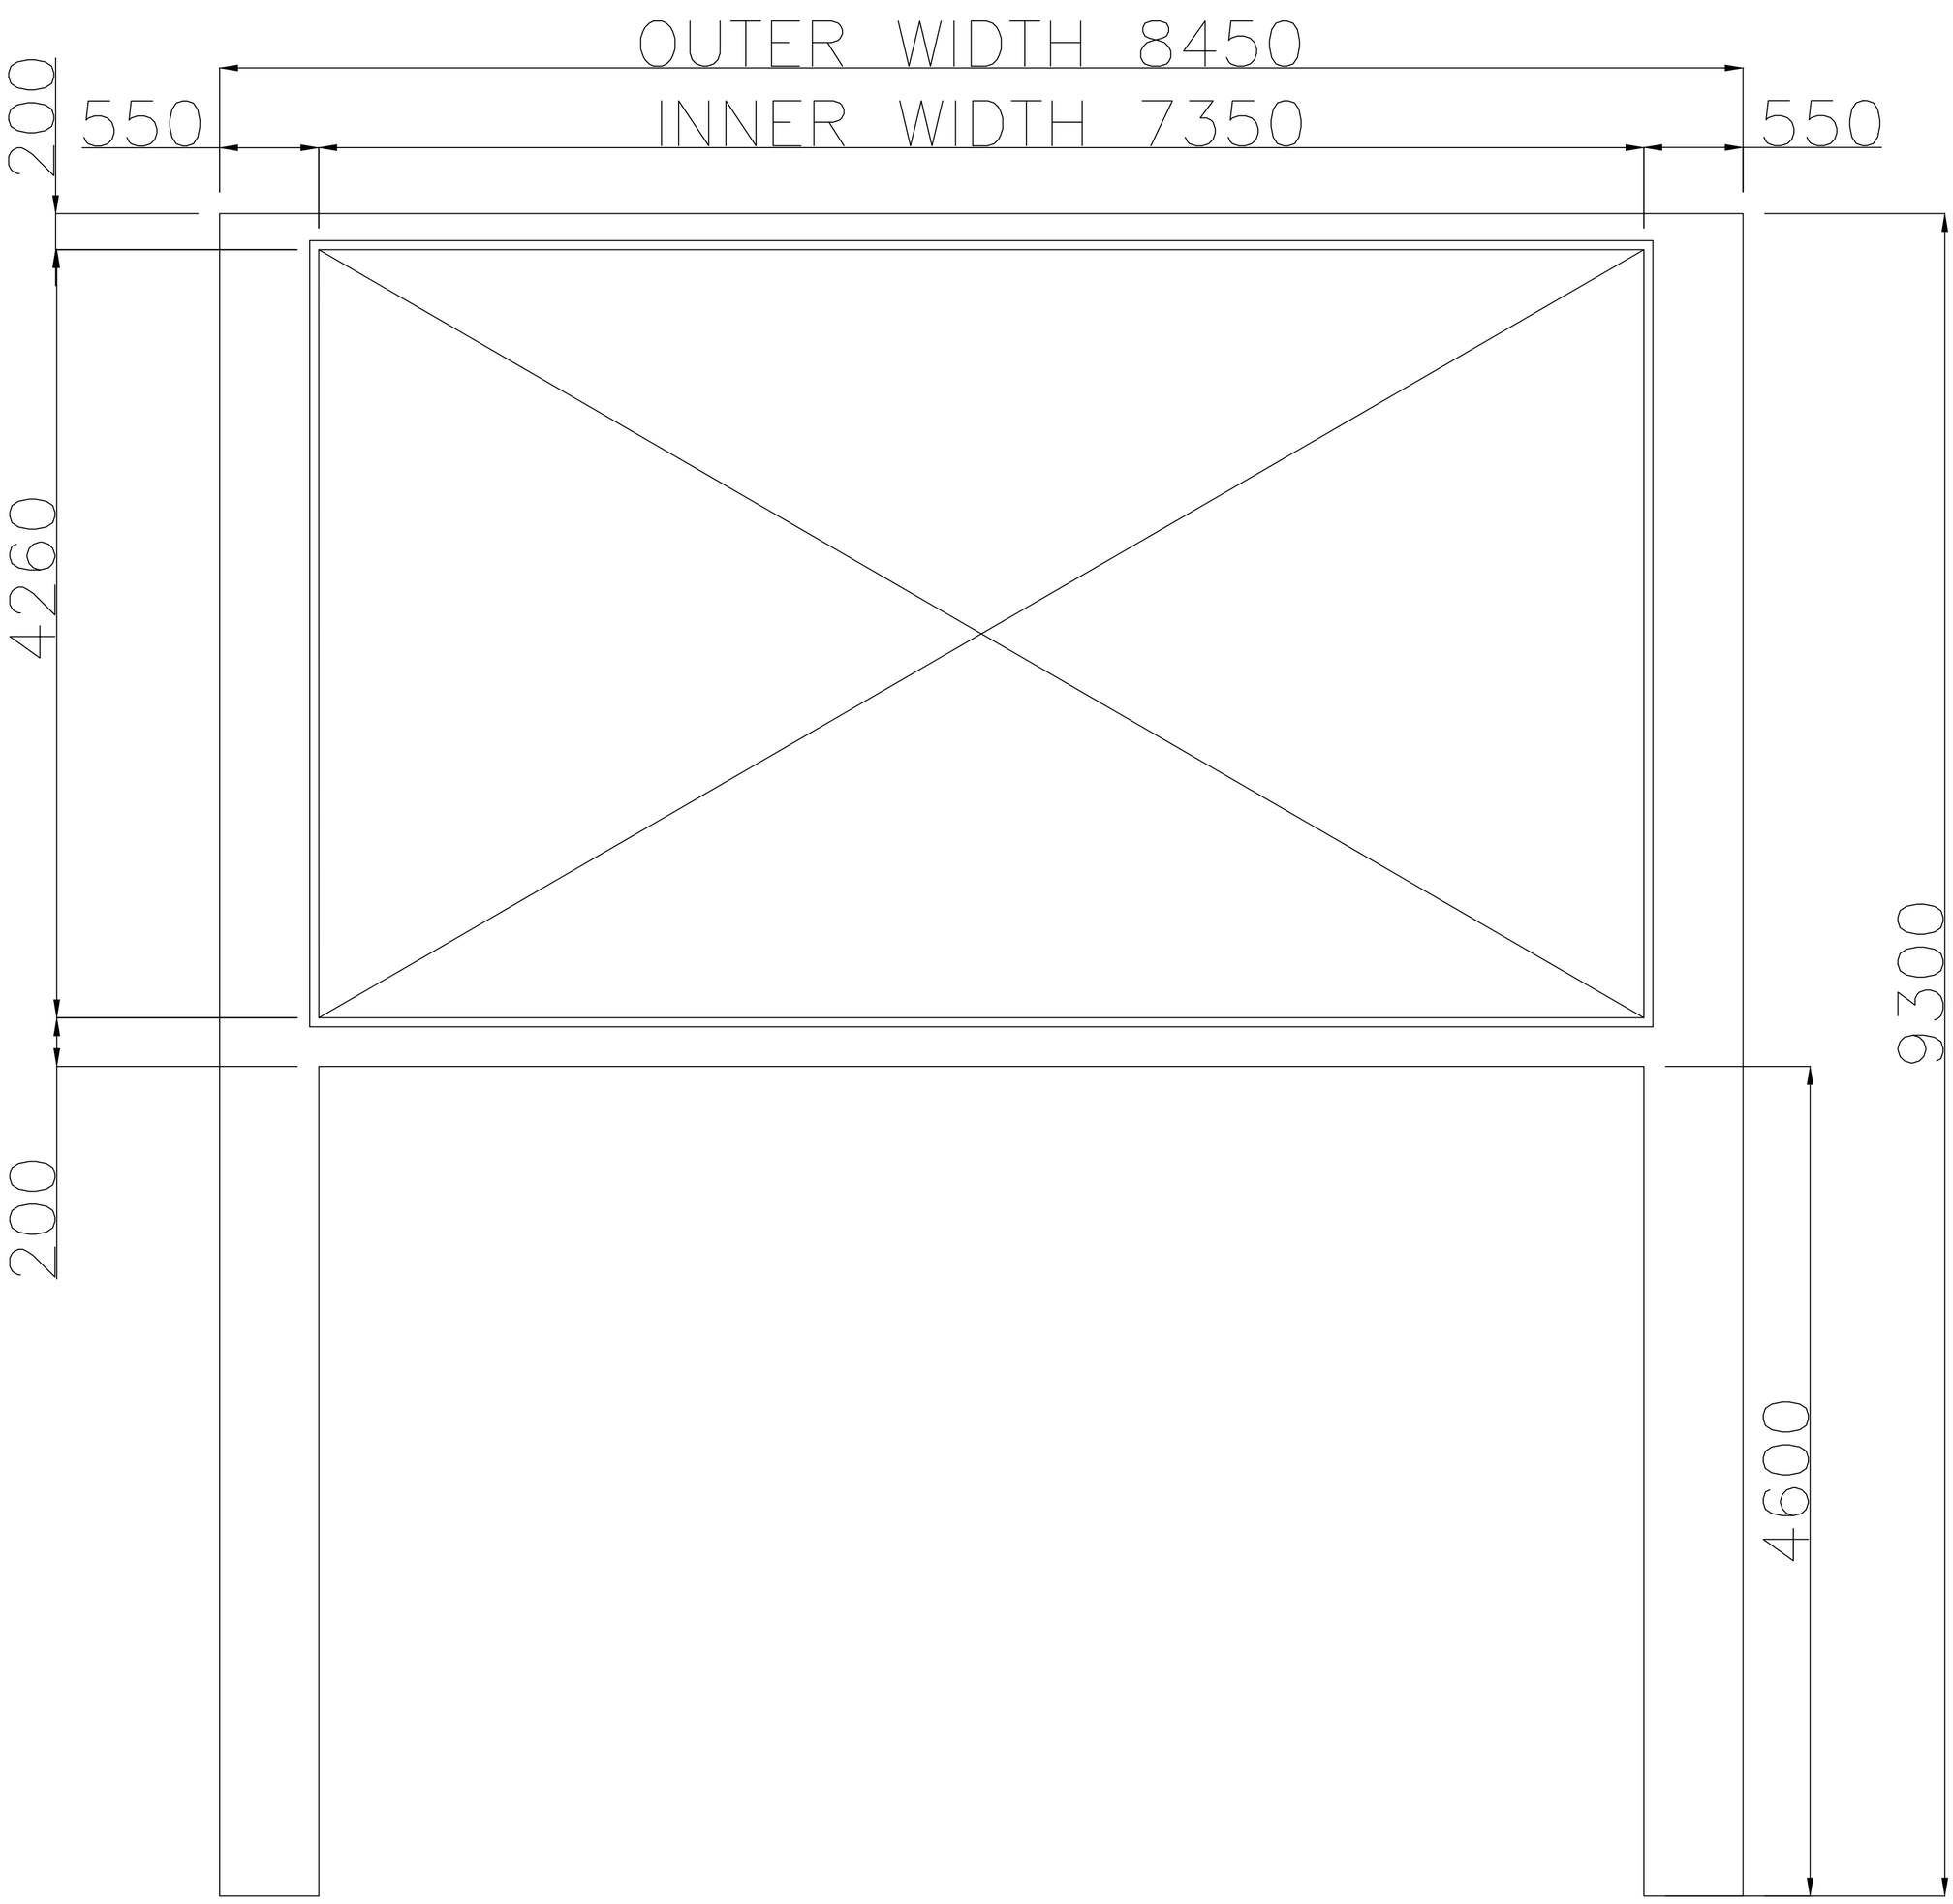

PROPOSED PLAN

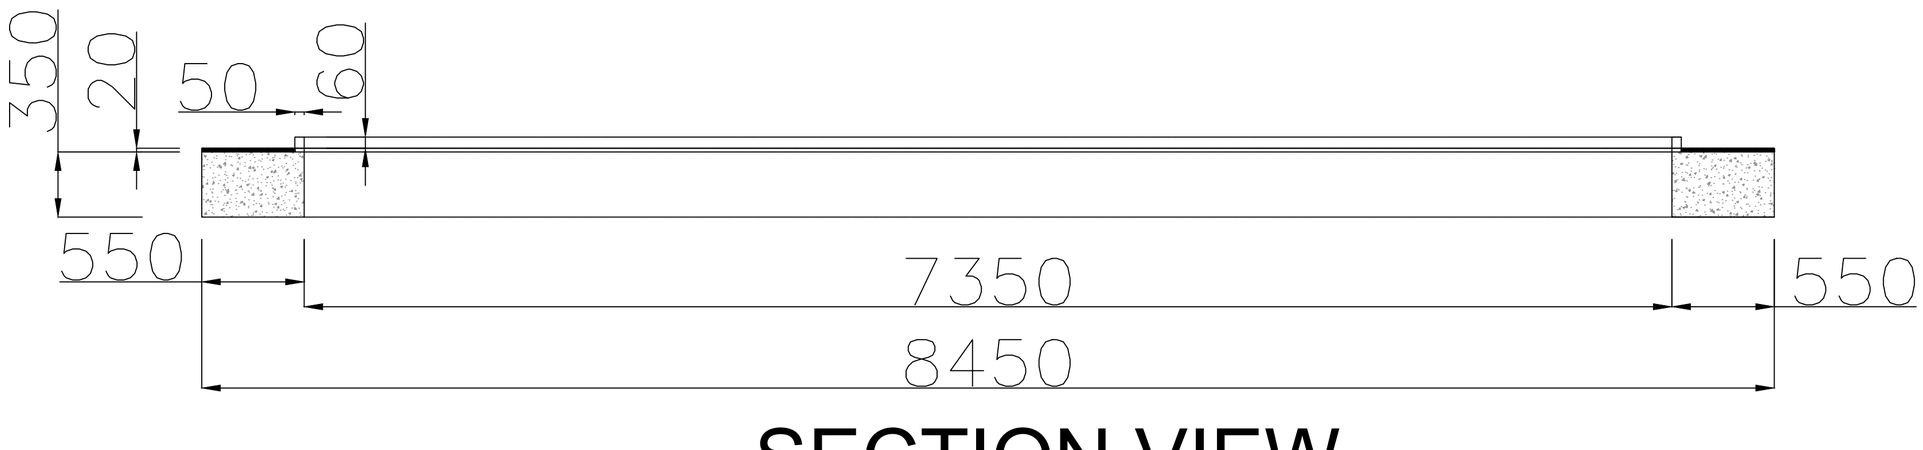

SECTION VIEW

1. THE STRUCTURE AROUND THE CUT OUT SHOULD BE OF CONCRETE FOR FOR PROPER FASTENING OF ROOF.
2. TOP SURFACE SHOULD BE OF GRANITE 20MM FOR SMOOTH FUNCTIONING OF ROOF.
3. ROOF EXTENSION IS SHOWN FOR ONLY REFERENCE. IT CAN BE MODIFIED AS PER THE WORK UNDERTAKEN.
4. GRADIENT OF 50MM NEED TO BE PROVIDED ALONG THE OUTER LENGTH TO AVOID WATER STAGNANCY IN GUIDE RAIL.
5. AL PROFILE - POWDER COATED 60X63 MM
6. GASKET - EPDM
7. MOTOR - ITALIAN/GERMAN MAKE
8. ALL DIMENSION IN MM.
9. ALL CIVIL WORK IS IN CLIENT SCOPE.

This drawing & design is the property of NIHVA TECHNOLOGIES. Not to be sold or copied to any other concern.

TITLE
PROPOSED PLAN LAYOUT
(IN CLIENT SCOPE)

NIHVA
NIHVA TECHNOLOGIES PVT. LTD.

	NAME	SIGN	DATE
DRAWN	AMIT KALE		13.12.22
CHECK	MAHESH S.		13.12.22
APPRD.	VIJAY T.		13.12.22

CLIENT - DR. BALAJI GOPALAN

LOCATION - PUNE_IN

PRODUCT - RETRACTABLE ROOF

If any queries contact : projectsautomation@nihva.com

NIHVA\22-23\02XX

REV- 0

ALL DIMENSION ARE IN mm

SCALE: NTS

SHEET: 01 OF 01