
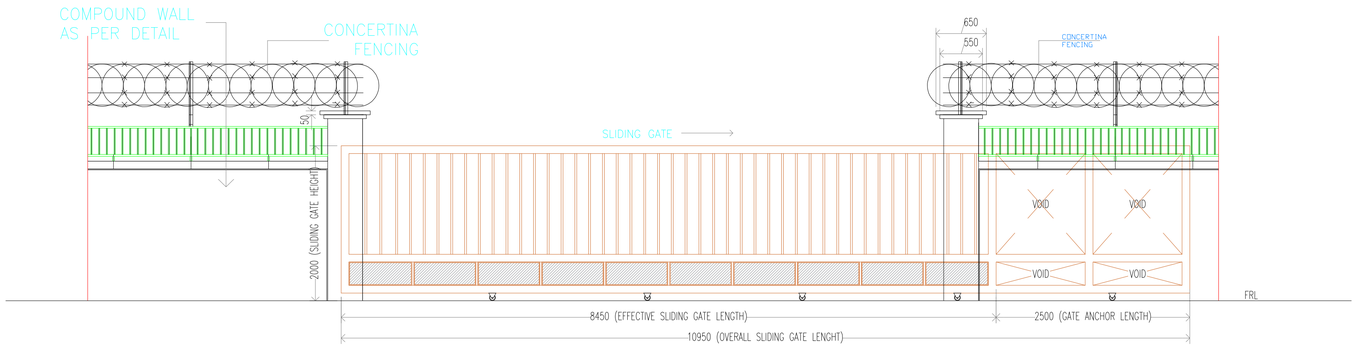


FRONT ELEVATION ENTRANCE GATE

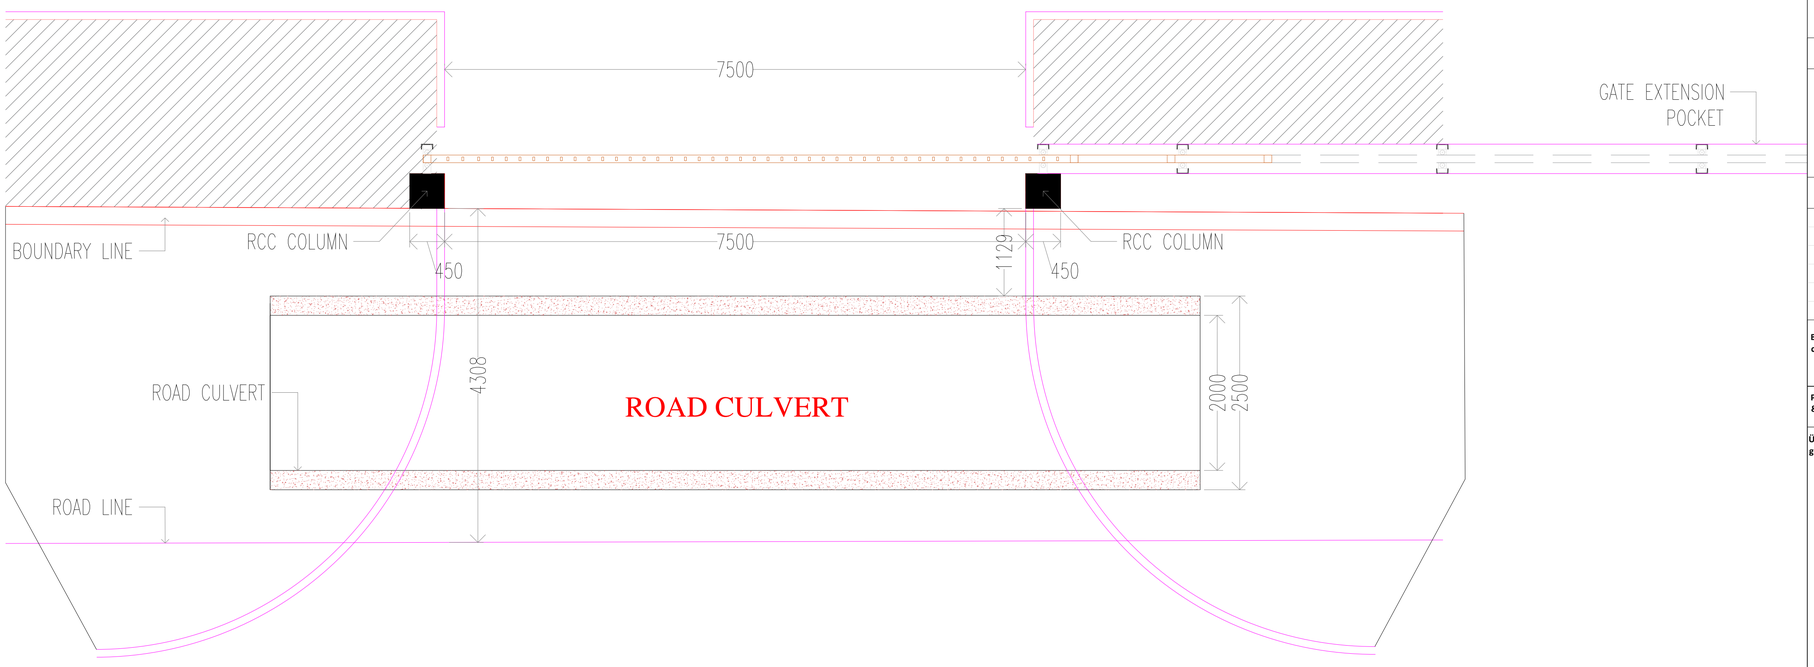


ENTRANCE GATE PLAN (SITE)

NOTES :

1) ONLY WRITTEN DIMENSIONS ARE TO BE FOLLOWED.
2) READ THIS DRAWING ALONG WITH THE RELEVANT DEPT. DRAWING.
3) ANY AMBIGUITY IN THIS DRAWING TO BE REFERED TO THE CONSULTANT BEFORE EXECUTION OF THE WORK
4) ALL DIMENSIONS ARE IN mm
5)
6)

REVISIONS :

NO.	DATE	REMARKS
R0	18.04.23	RELEASED FOR TENDER

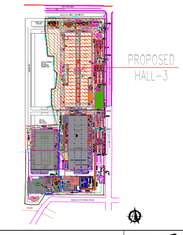Bauherr / client	**Schaeffler India Limited** (Formerly Known as FAG Bearings India Ltd.) GIDC, Savli, Vadodara 391 775. Gujarat, India — SCHAEFFLER
Projectname & -address	F4T EXPANSION SAVLI PHASE-2.2 AT-SAVLI, VADODARA, GUJARAT
Übersicht / general plan	
Projekt-management / project management	**Schaeffler Technologies AG & Co. KG** Industriestraße 1-3, 91074 Herzogenaurach, Germany — SCHAEFFLER Corporate Construction, Factory Maintenance & Administration
Entwurfs-verfasser / Designer	ARCHIVISTA ENGINEERING PROJECTS PVT.LTD. Office No.2018202,Sai Empire, Baner, PUNE-411045, MAHARASHTRA,INDIA. PH.91-20-66294444,460 www.archivistaindia.com — ARCHIVISTA AEPPL
Status/status Inhalt/content	**TENDER DRAWING DETAILS OF ENTRANCE GATE FOR MATERIAL ENTRY**

Discipline	Projektnummer / project number	Planformat / plan format
ARCHITECTURAL	SCH517	DIN

Datum / date	Gezeichnet	Geprüft	Maßstab / scale	Zeichnungsnummer / plan number	
18.04.2023	G.RAMESHKUMAR	RPJ	1:40	SCH517_TD_ARCH_SITE_ENT-GATE_006-04_R0	A1

THIS DRAWING IS THE PROPERTY OF ARCHIVISTA ENGINEERING PROJECTS PVT. LTD. IT IS ISSUED FOR PRELIMINARY ENGINEERING & APPROVAL. ANY MISUSE, DUPLICATION, ALTERATION OR REUSE FOR ANOTHER PURPOSE IS STRICTLY PROHIBITED & SHALL BE DEALT LEGALLY.ALL RIGHTS RESERVED WITH THE COMPANY.