



Abbrevation's:
WOW-Wall Opening Width
WOH-Wall Opening Height
UC-Under Cut
FFL-Finished Floor Level

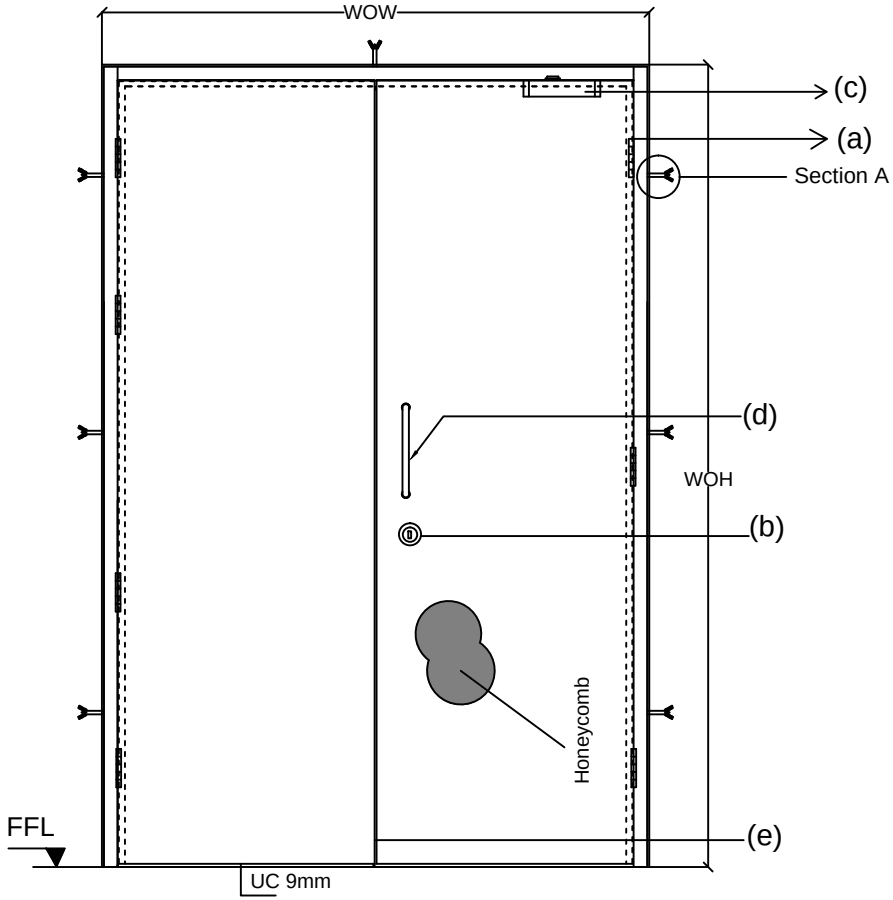

Elevation



Top View

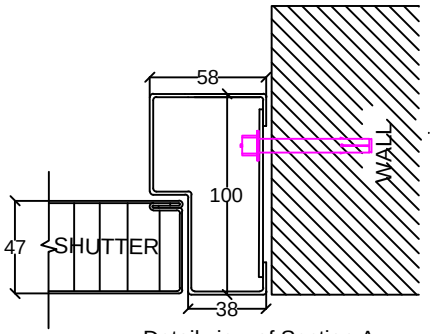

Detail view of Section A

ASSESORIES DETALES

(a) HINGES: SS Ball bearing butt hinges size 100x75x3mm

(b) LOCK : Mortise Dead lock,Cylinder(one side key & thumb turn on other side) with Escutcheon

(c) DOOR CLOSER

(d) HANDLE : D Handle(254 mm)

(e) CONCEALED FLUSH BOLT

Shutter thickness : 47 mm
Frame Sheet thick : 1.2mm
Shutter sheet thick :0.8mm
Fixing : On Soliid Brick plasterd wall with Anchors
Electrostatic powder coated

NOTE:- *All Dimensions are in mm.
*Tolerance:-All Linear Dimensions ±3mm,Others ±0.5mm.
*The Drawing Is For Location of Hardware only. Drawing Does Not Represent The Hardware For More Clarity, Please Go Through Hardware Broucher.

DOOR TYPE	WOW	WOH	TYPE 5	TYPE 6	TYPE 7	TYPE 8	TOTAL
STEEL DOOR	1500	2415					9

Client should mention door handling type from door handling sheet.

COLOR - RAL 7035 LIGHT GREY

This drawing & designing is the property of NIHVA TECHNOLOGIES. Not be sold or copy to any other concern.

DOUBLE LEAF STEEL DOOR

CLIENT APPROVAL

ALL DIMENSION ARE IN mm

	NAME	DATE	SIGN.
DRAWN	OMKAR	31/08/16	
CHECK	ANIL	31/08/16	
REV.	0		
APPRD.			
MFG			

NIHVA TECHNOLOGIES PVT. LTD.
NIHVA TECHNOLOGY PVT. LTD. PUNE
Tel : 020 66304033
Email:- info@nihva.com
Website:-www.nihva.com

CLIENT - INDOSPACE
PROJECT - RVK INDUSTRIAL PARK PVT. LTD.
SITE - RANJANGAON
DWG. NO. -NIHVA/16-17/0068
SCALE:NTS | WT: | SHEET: 01 OF 01
If any queries contact : projects@nihva.com