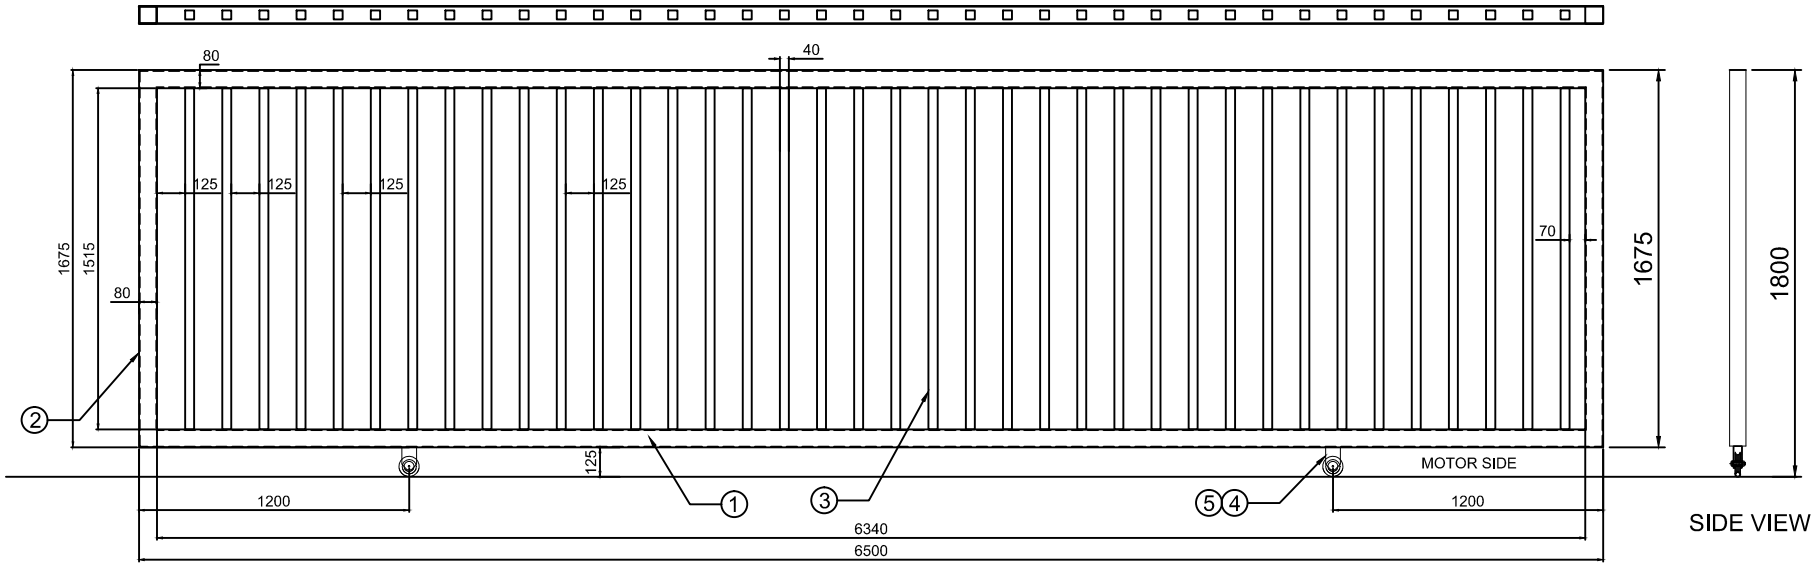



| SR.NO | DESCRIPTION | SPECIFICATION | QTY | WEIGHT |
|---|---|---|---|---|
| 5 | WHEEL | 4 " STEEL WHEEL | 2 NOS | |
| 4 | WHEEL BKT | STANDARD FOR 4 " WHEEL | 2 NOS | |
| 3 | SQ. TUBE | 40 X 40 X 2 THK X 1515L | 38 NOS | 135 KGS |
| 2 | SQ. TUBE | 80 X 80 X 3.2 THK X 1675L | 2 NOS | 27 KGS |
| 1 | SQ. TUBE | 80 X 80 X 3.2 THK X 6500L | 2 NOS | 104 KGS |

This drawing & designing is the property of NIHVA TECHNOLOGIES. Not to be sold or copied to any other concern.

TITLE: SLIDING GATE LEAF

NIHVA TECHNOLOGIES PVT. LTD.
NIHVA TECHNOLOGIES PVT. LTD. PUNE
Tel : 020 66304033
Website:- www.nihva.com
Email:- info@nihva.com

| | Name | SIGN | DATE |
|---|---|---|---|
| DRAWN | P.V.A | | 31.05.19 |
| CHECK | V.M.T | | 31.05.19 |
| APPROVAL | | | |

If any queries contact : design@nihva.com

CLIENT -

PROJECT -

SITE LOCATION -

DWG. NO. : NIHVA/19-20/VDR/051 REV.- 0

ALL DIMENSION ARE IN mm

SCALE: NTS WT: SHEET: 01 OF 01