
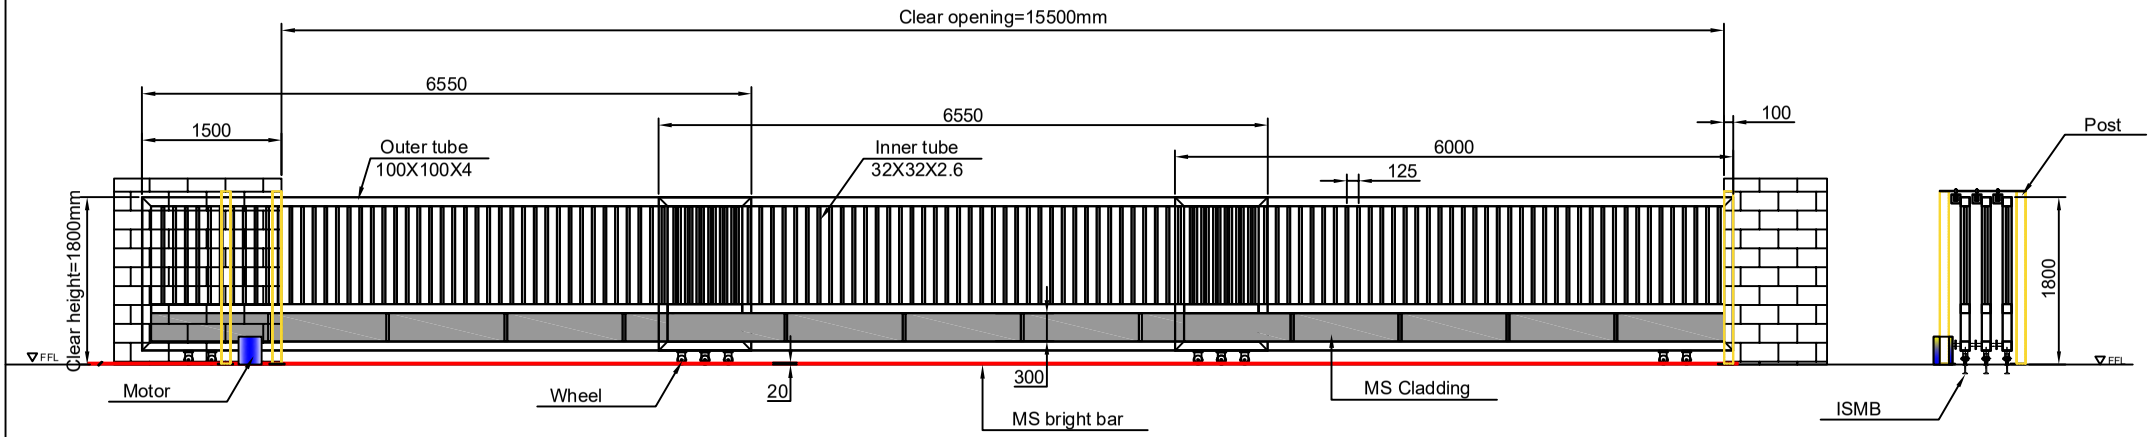


INSIDE

OPENING DIRECTION

ELEVATION VIEW

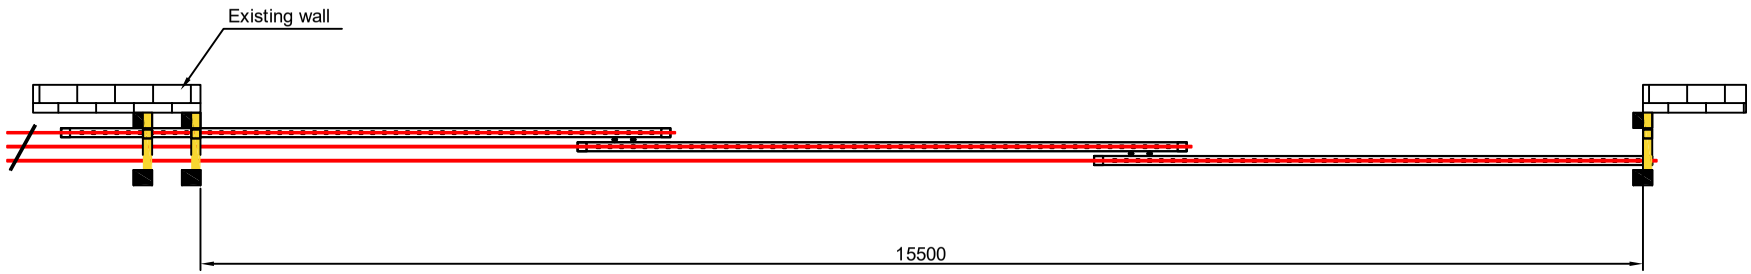

TECHNICAL SPECS FOR SWING GATE		
SL NO.	SPECIFICATION	
1	OPENING LENGTH	15500MM
2	OPENING HEIGHT	1800MM
3	TOTAL LEAF WEIGHT(APPROX)	1500KG
4	OUTER TUBE	100X100X4
5	INNER TUBE	32X32X2.6
6	OPERATION	MOTORIZED

Note:-
1. All dimension are in mm
2. All civil work is in client scope

Rev No.	Revision	Date	Revised By

This drawing & design is the property of NIHVA TECHNOLOGIES. Not to be sold or copied to any other concern.

TITLE:- TELESCOPIC SLIDING GATE

NIHVA TECHNOLOGIES PVT. LTD.

NIHVA TECHNOLOGIES PVT. PUNE
Tel : 020 66304033
Email:- info@nihva.com
Website:- www.nihva.com

	NAME	DATE	SIGN
DRAWN	SUJATA.B	03/01/2022	
CHECK	G.PATIL	03/01/2022	
APPRD.	A.K	03/01/2022	

CLIENT - Fanidhar Mega Food Park Private Limited

LOCATION -

PRODUCT - TEL.SLIDING GATE

If any queries contact : design@nihva.com

DWG NO:-NIHVA/21-22/CLT/0298 REV- 0

ALL DIMENSION ARE IN mm

SCALE: NTS SCALE:-- 1:1 SHEET: 01 OF 01