

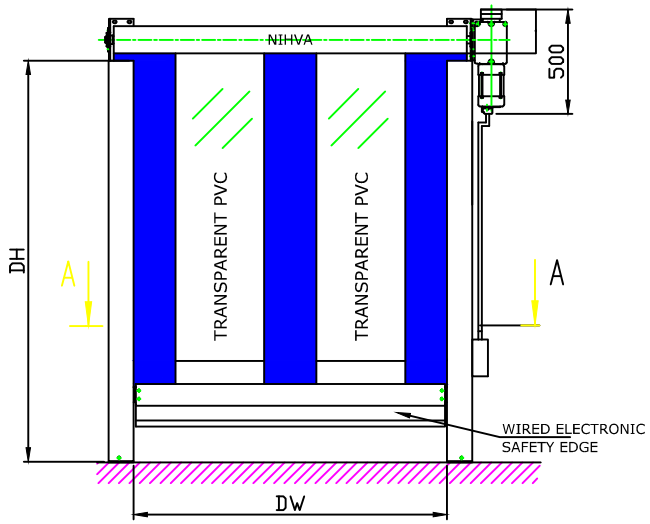


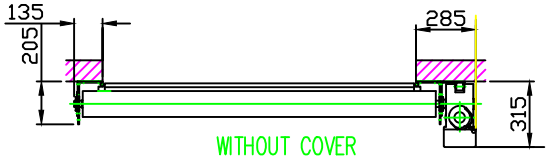



WITHOUT COVER

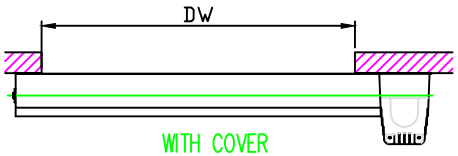


WITH COVER

A–A

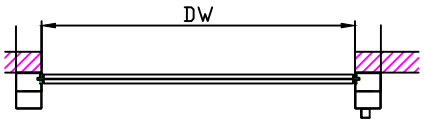

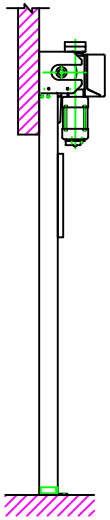

WITHOUT COVER

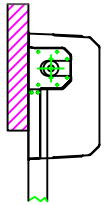

MOTOR COVER

NOTE :
1. TRANSPARENT PVC WITH BLUE REINFORCEMENT STRIPES.
2. VERTICAL TRANSPARENT VISION PANEL.
3. SAFETY EDGE.
4. VARIABLE FREQUENCY DRIVE (VFD) FOR SOFT START / CLOSE AND SPEED ADJUSTMENT.
5. REMOTE CONTROL WITH RECEIVER.
6. EXTRA PUSH BUTTON, EXTERNAL SWITCH SHOULD BE LOCKED IN BOX AND SHOULD BE OUT DOOR ONE.
7. EXTRA REMOTE.
8. EXTENDED ARM FOR MANUAL CRANK.
9. YELLOW FLASHING LIGHT WITH ALARM.
10. SAFETY PHOTOCELL.
11. KEY SWITCH FOR LOCKING MANUAL OPEARTION BUT SHOULD WORK IN REMOTE OPERATION.

SR NO	DW	DH	LOCATION	QUANTITY
2	3500	4000	Buffer Zone Shop Floor Side RS12	1 No
1	3200	3000	Pin Joint Loading Shop Floor Side Door(RS02 & RS03)	2 Nos
			DOOR DIMENSION	

This drawing & design is the property of NIHVA TECHNOLOGIES. Not to be sold or copied to any other concern.

TITLE - HIGH SPEED DOOR

NIHVA TECHNOLOGIES PVT. LTD.

NIHVA TECHNOLOGIES
PVT. LTD. PUNE
Tel : 020 66304033
Email:- info@nihva.com
Website:- www.nihva.com

	NAME	SIGN	DATE
DRAWN	P.V.A		18.07.19
CHECK	V.M.T		18.07.19
APPROVED			

CLIENT - LM WIND POWER BLADES

PROJECT -

SITE LOCATION - DABASPETH, BANGLORE.

If any queries contact:sales@nihva.com | DWG. NO. -NIHVA/19-20/0053 | REV- 0

ALL DIMENSION ARE IN mm | SCALE: NTS | WT: | SHEET:

Tolerance ±3 mm (for all dimensions)
Dimensions in [ ] ==> clearance for installation