
3RD FLOOR
OPTION 1

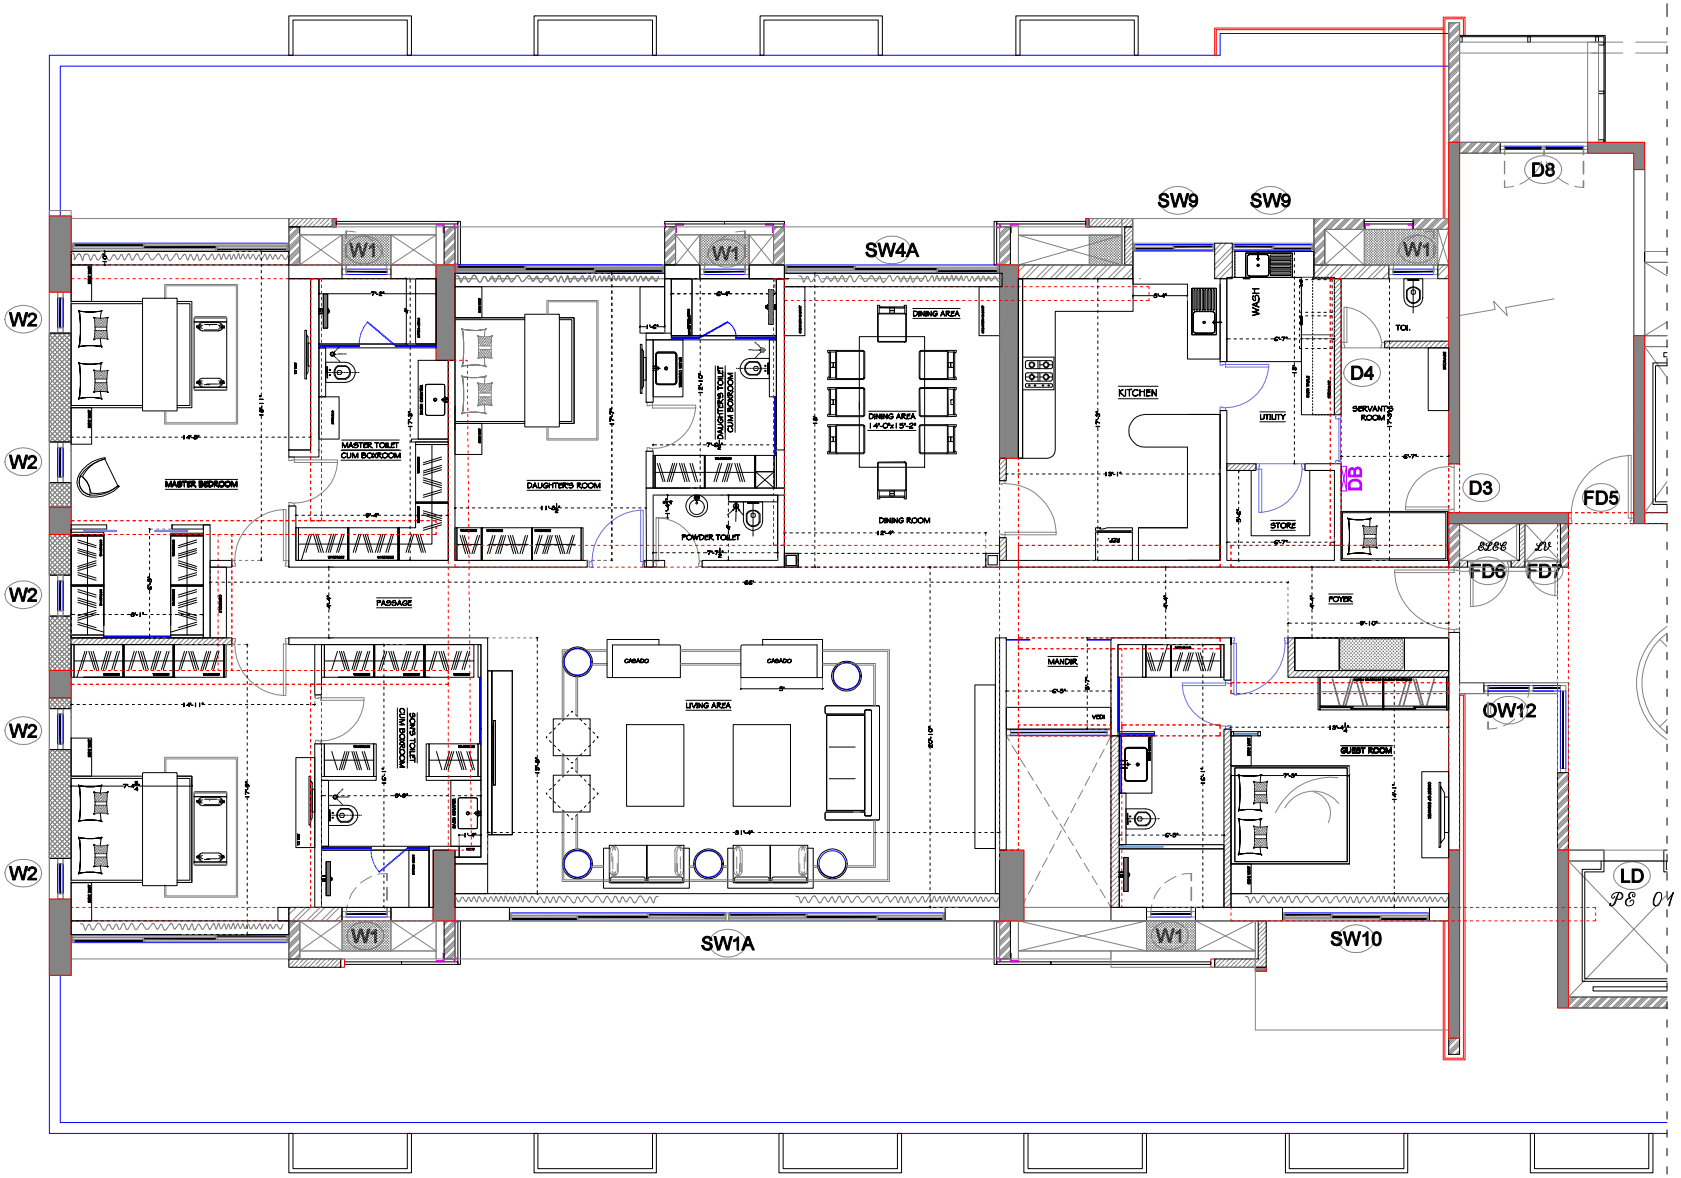

NOTE :-
1.RAW FLOOR TO RAW CEILING HT :- 10'-11".
2.DROP SLAB IN FLOOR OF BOX ROOM & TOILET :- 11" DROP.
3.DOOR LINTEL HT. :- 8'-0" FROM RAW FLOOR LVL.

GENERAL NOTES
1. Contractors to verify all site dimension.
2. Contractors is responsible for notifying Studio W.B if collusion arises on site or if dimensions and /or details from drawing set before proceeding at site
3. All wood grain on moveable and built-in furniture is to run in the direction as indicated by arrow on drawings.
4. No part of this work may be reproduced or used in any form or by any means without written permission from the publisher
5. All prints, specifications and their copyright are the property of Studio W.B and shall be returned at the completion of the work.
6. All dimensions shall checked on site before commencing any work or shop drawings. Any descrepancies occurring in the drawings must be reffered to this office before the commencement of any work or the cotractor shall bear the full responsibility for the same
7. Do not scale drawings.
8. Figured dimensions shall be taken in preference to scaled dimensions.

STUDIO W.B.
INTERIOR ARCHITECTS, DESIGNERS, PLANNERS
SILVER ARCADE
5,J.B.S. HALDEN AVENUE
1ST FLOOR, SUITE NO.-4
KOLKATA- 700105
TEL- 033 22510154
EMAIL- studiowb@gmail.com
info@studiowb.co.in

MR. MANOJ JAIN
ORBIT VICTORIA
3RD FLOOR , FLAT TYPE :- A
30 SHAKESPEARE SARANI
KOLKATA - 700017

DRAWING TITLE:
PROPOSED FURNITURE LAYOUT
(3RD FLOOR)

SCALE : SCALE TO FIT	AREA - 3420.0 SQ.FT(APPROX)
DATE: 26.06.2021	DRAWING NUMBER 78243 / FILE NO. J-10
DRAWN BY: JABA	CHECKED BY