

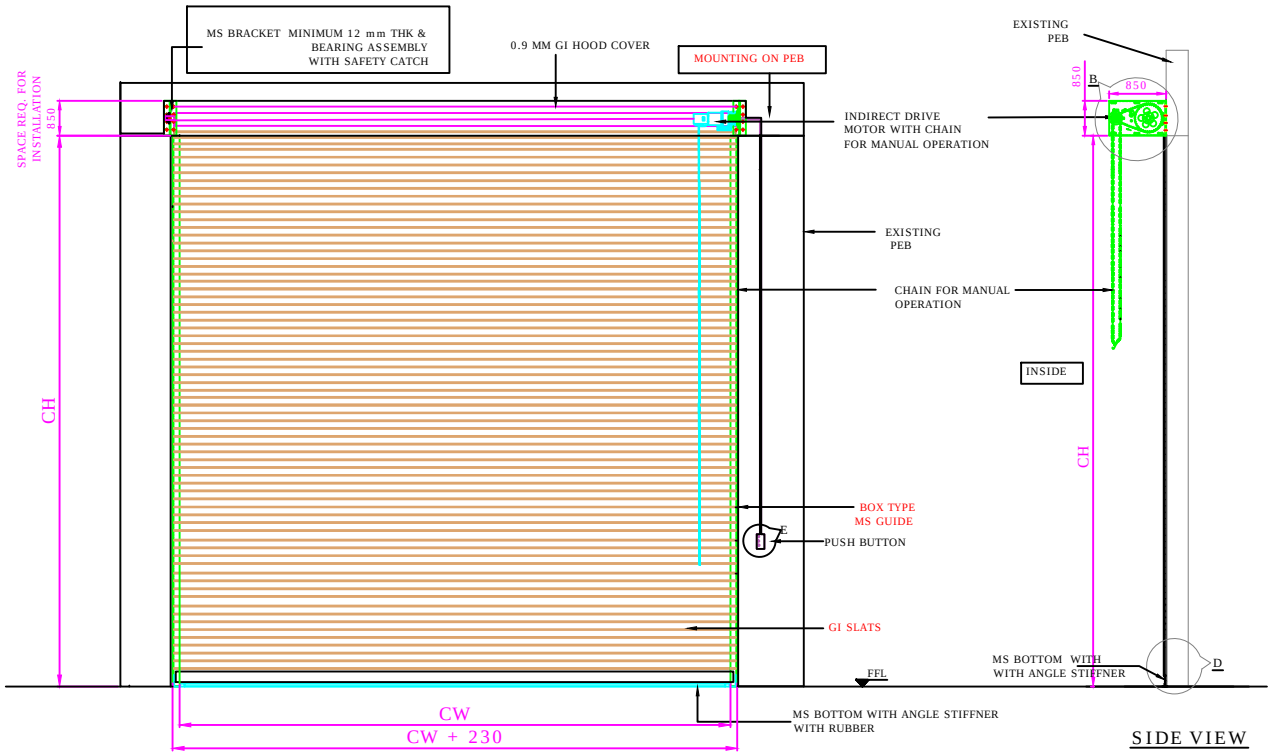



ELEVATION

SIDE VIEW

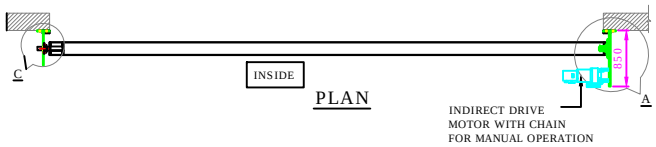


PLAN

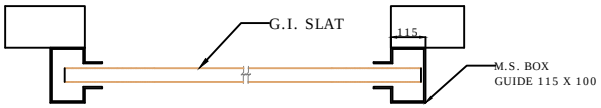


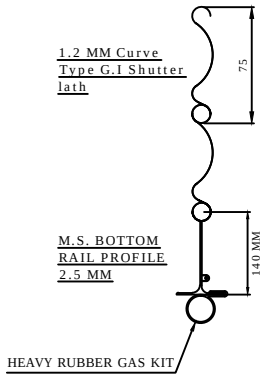


DETAILS : D

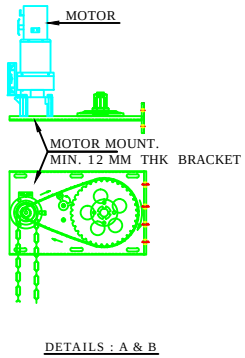

DETAILS : A & B

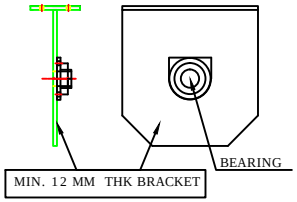

DETAILS : C

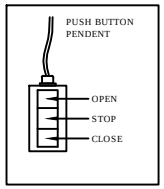

DETAILS : E

SR NO	CLEAR WIDTH(CW)	CLEAR HEIGHT(CH)	QTY	LOCATION	RAL CODE	MOTOR POSITION (LH/RH FROM INSIDE)
6	6000	5850	1	A-GRADE SHUTTER		
5	6000	5850	1	G-GRADE SHUTTER		
4	6070	7700	1	F-19		
3	6070	7700	1	B-19		
2	6070	7700	1	F-1		
1	6070	7700	1	B-1		

NOTES-

(1) RAL CODE & MOTOR MOUNTING SIDE WILL BE SHARED SEPARATELY .

(2) ROLLING SHUTTER MOTOR CONSIDERED SHOULD BE WITH SAFETY CATCH .

(2) REQUIRED MINIMUM THICKNESS OF BRACKET IS 12MM MINIMUM & BRACKET SHOULD WITHSTAND ALL LOAD COMING ON ROLLING SHUTTER, KINDLY SHARE BRACKET & SHAFT DRAWING BEFORE MANUFACTURING .

(3) PROVIDED ROLLING SHUTTER & COMPONENT USED FOR MAKING MRS SHOULD BE CAPABLE TO HANDLE WIND LOAD OF 140KMPH .

This drawing & design is the property of NIHVA TECHNOLOGIES. Not to be sold or copied to any other concern.

TITLE- GI SLAT MOTORIZED ROLLING SHUTTER

	NAME	SIGN	DATE
DRAWN	SIDDHESHWAR		15.12.2020
CHECK			
APPRD.			

If any queries contact : projectsupport@nihva.com

ALL DIMENSION ARE IN mm

NIHVA TECHNOLOGIES PVT. LTD.

NIHVA TECHNOLOGIES PVT. LTD. PUNE
Tel : 020 66304033
Email:- info@nihva.com
Website:- www.nihva.com

CLIENT -

PROJECT -

SITE LOCATION -

DWG. NO. : NIHVA/20-21/VDR/0081 | REV- R00

SCALE: NTS | WT: | SHEET: