
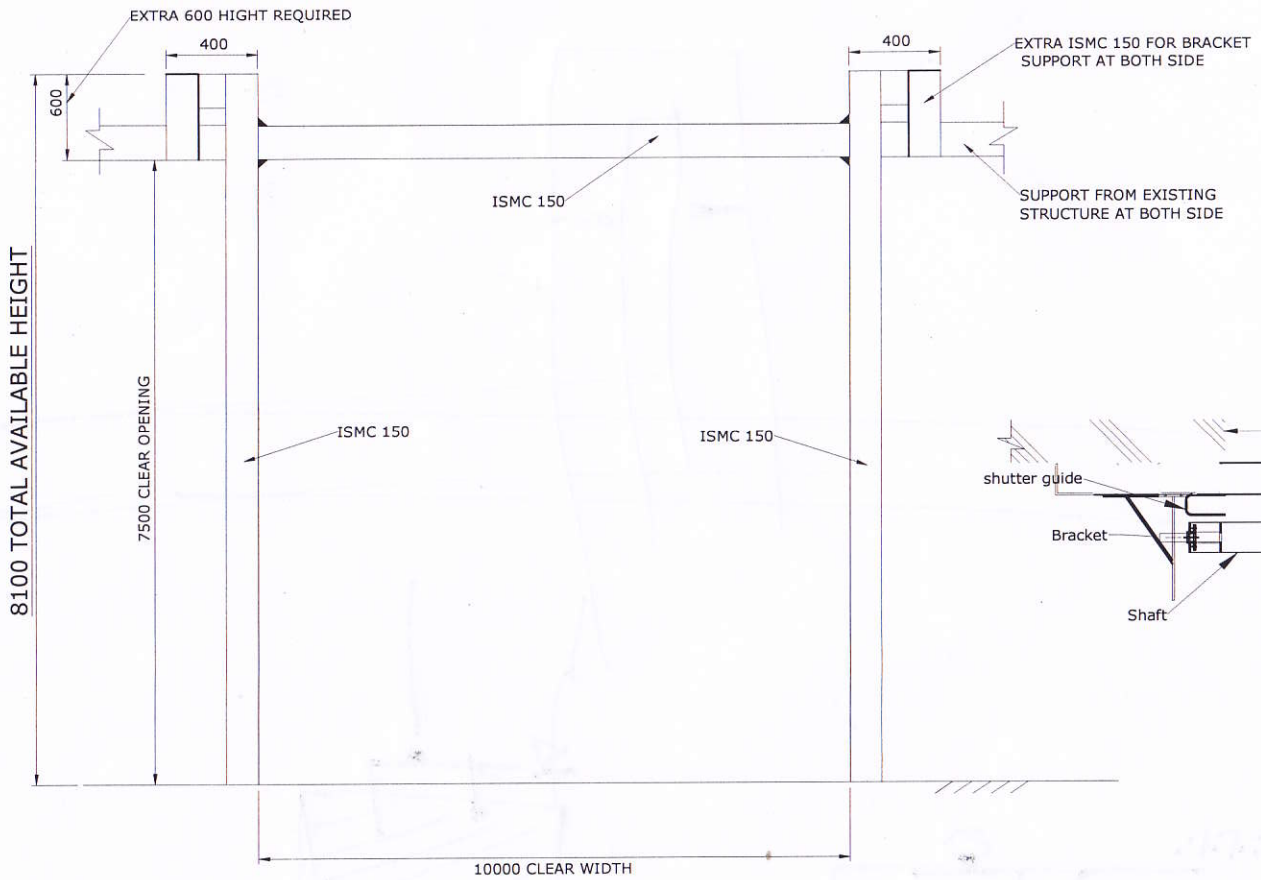


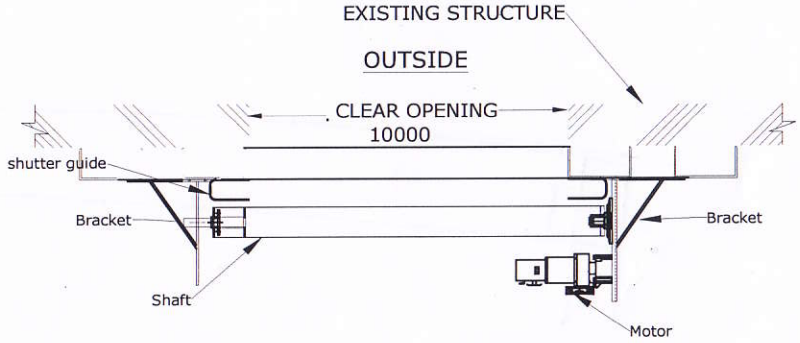

INSIDE

DETAIL VIEW A

(CLEAR OPENING (W)10000X(H)7500)

Approved
R
M S Patil
Patil

(NOTE: REQUIRED STRUCTURE FOR DOOR SHOULD BE IN CLIENT SCOPE.)

structure should bear approx.2500 k.g. weight. (wind pressure included). While Door is in operation, structure should not vibrate and bear/sustain all movements of rolling shutter.

TITLE

STRUCTURE FOR ROLLING SHUTTER

CLIENT APPROVAL

This drawing & designing is the property of NIHVA TECHNOLOGIES. Not be sold or copy to any other concern.

ALL DIMENSION ARE IN mm

	SIGN	DATE
DRAWN	ABHIJIT	20/10/15
CHECK	ANIL	20/10/15
ENG		
APPRD.		
MFG		
Ref. No.		

NIHVA TECHNOLOGIES PVT. LTD.

NIHVA TECHNOLOGY PVT. LTD. PUNE
Tel : 020 66304033
Email:- info@nihva.com
Website:- www.nihva.com

CLIENT - MUKUND CONSTRUCTION


PROJECT- NEUMAN AND ESSER


SITE - BHOSARI MIDC


DWG. NO. - NIHVA/15-16/148

SCALE: 01 | WT: | SHEET: 01

If any queries contact : projects@nihva.com

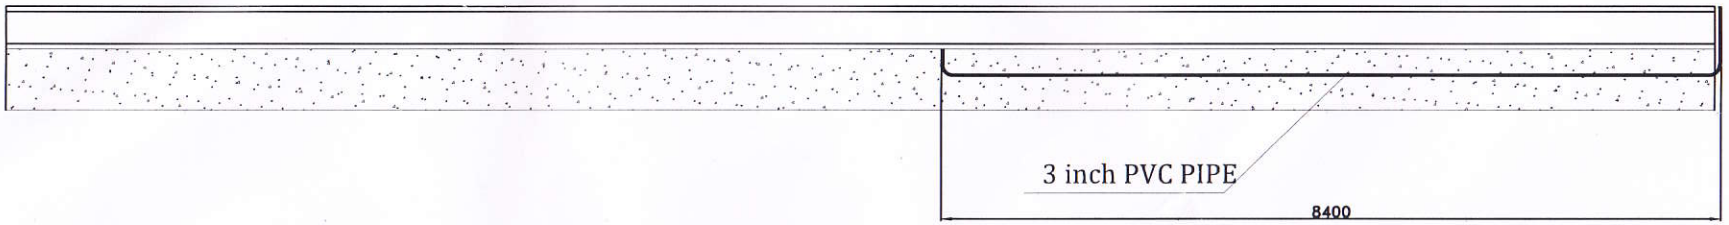

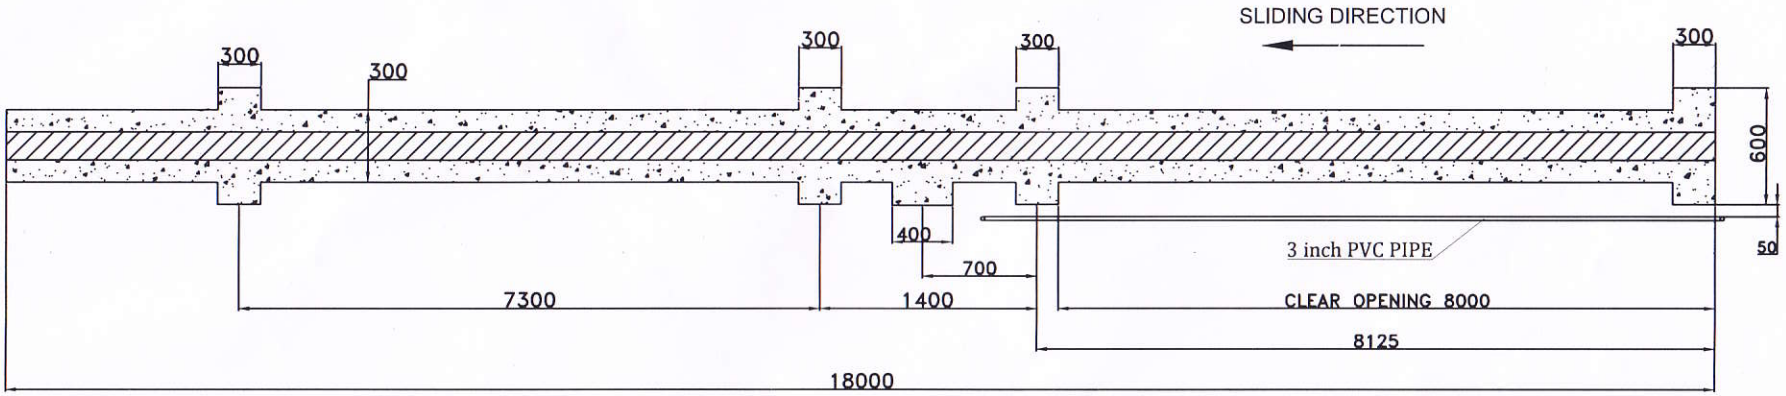

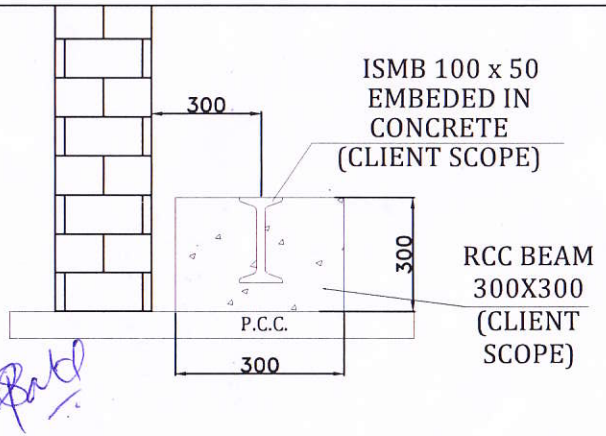

08 METER SLIDING GATE FOUNDATION

This drawing & designing is the property of NIHVA TECHNOLOGIES. Not be sold or copy to any other concern.

TITLE

SLIDING GATE FOUNDATION

CLIENT APPROVAL

ALL DIMENSION ARE IN mm

	SIGN	DATE
DRAWN	ABHIJIT	24/09/15
CHECK	ANIL	24/09/15
REV.	00	
APPRD.		
MFG		
Ref. No.		

NIHVA TECHNOLOGIES PVT. LTD.

NIHVA TECHNOLOGY PVT. LTD. PUNE
Tel : 020 66304033
Email:- info@nihva.com
Website:- www.nihva.com

CLIENT - MUKUND CONSTRUCTION

PROJECT -


SITE -BHOSARI MIDC

DWG. NO. - NIHVA/15-16/152

SCALE: 01 | WT: | SHEET: 01 OF 01

If any queries contact : projects@nihva.com

M S Patil

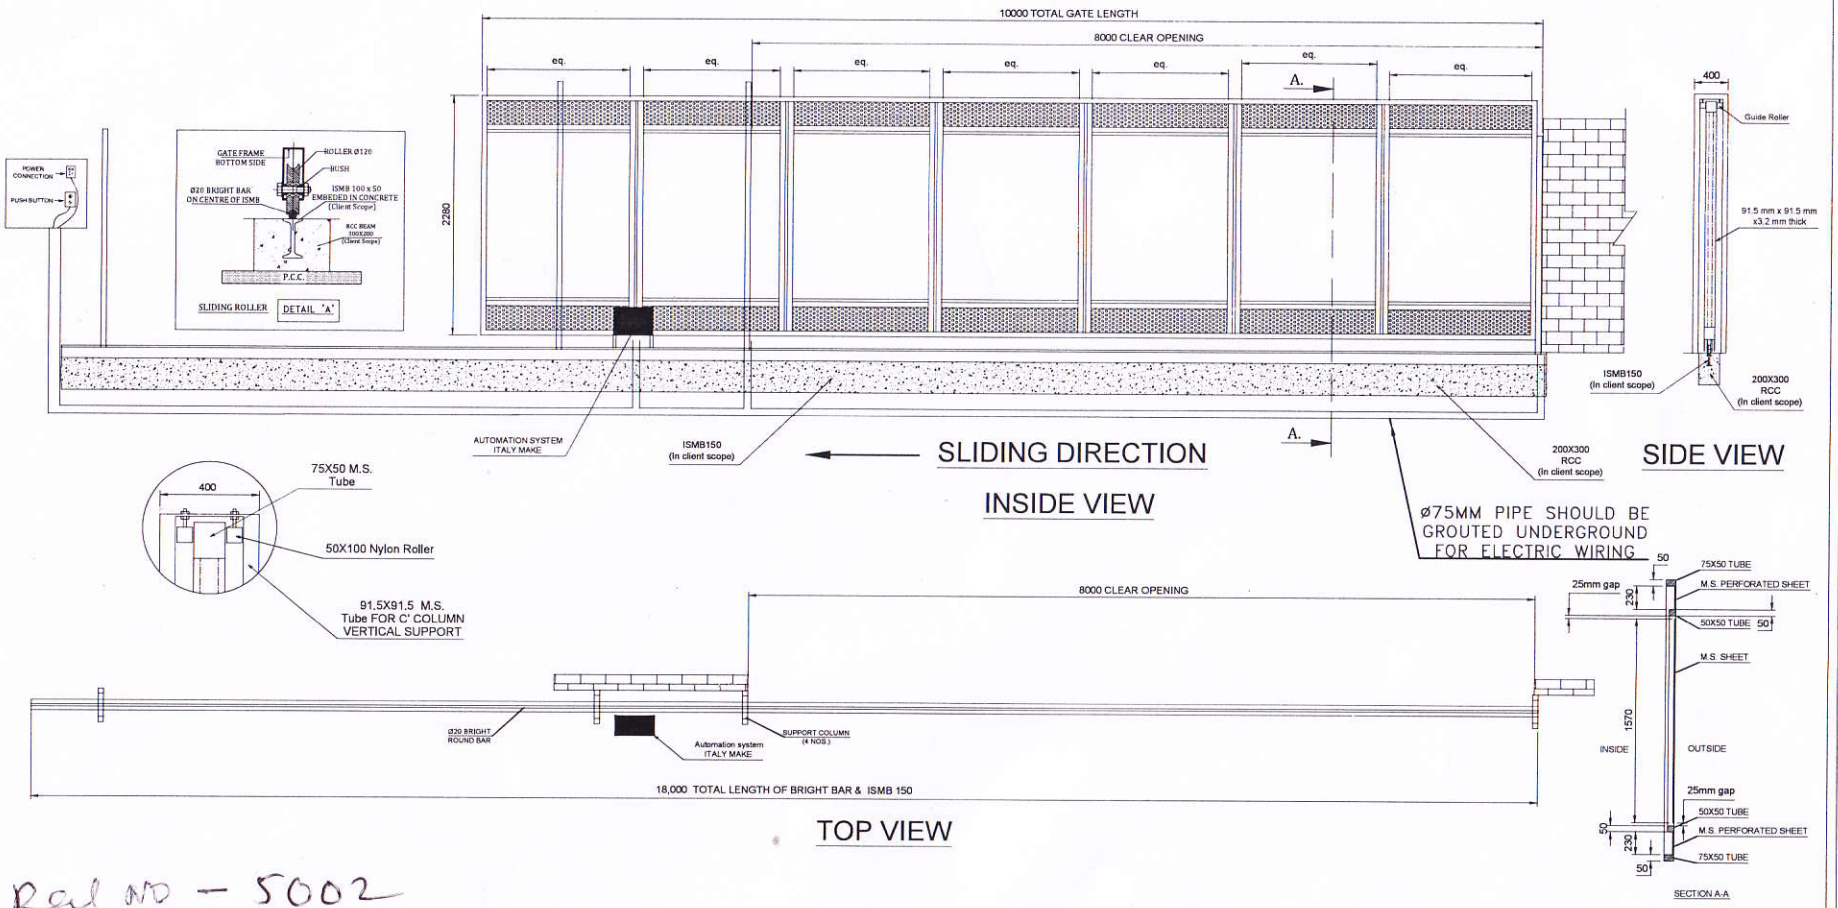

blue – Ral no – 5002
off white Ral no – 9002

Approved


M S Patil

Patil

Clear Opening size - 8000X2280mm
Total length of gate - 10000X2280mm
No. Of Column - 4 nos.
Factory paint finish - Red oxide primer coat
NOTE :- *ALL REQ. CIVIL WORK WILL BE IN CLIENT SCOPE.

This drawing & designing is the property of NIHVA TECHNOLOGIES. Not be sold or copy to any other concern.

TITLE	MOTORIZED SLIDING GATE		NIHVA TECHNOLOGIES PVT. LTD.	NIHVA TECHNOLOGY PVT. LTD. PUNE Tel : 020 66304033 Email:- info@nihva.com Website:- www.nihva.com
	SIGN	DATE		
DRAWN	ABHIJIT	27/10/15	CLIENT - MS MUKUND CONSTRUCTION CO.	
CHECK	ANIL	27/10/15	PROJECT -	
REV.	01		SITE -	
APPROVAL			DWG. NO. : NIHVA/15-16/136	
If any queries contact : projects@nihva.com			SCALE: 01	WT: / SHEET: 01 OF 01
ALL DIMENSION ARE IN mm				

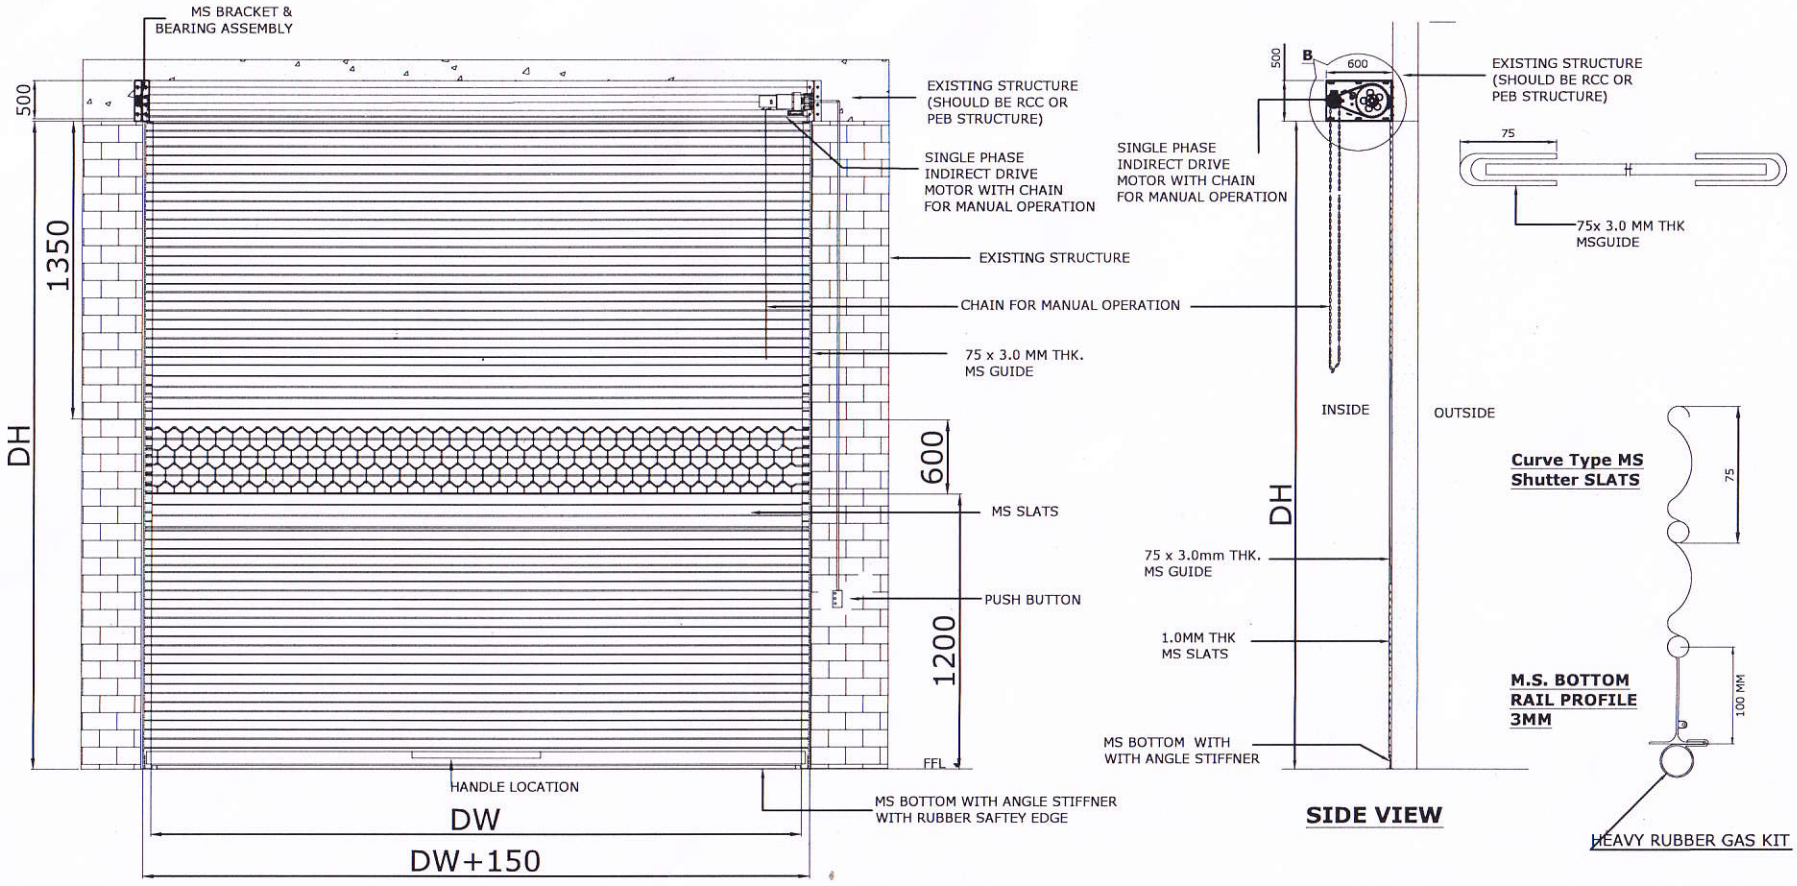

DW Door Width	DH Door Height	QUANTITY
3000 mm	3150 mm	1
3324 mm	3150 mm	1

Approved

MS Patil

This drawing & designing is the property of NIHVA TECHNOLOGIES. Not be sold or copy to any other concern.

MOTORIZED ROLLING SHUTTER


CLIENT APPROVAL

ALL DIMENSION ARE IN mm


NIHVA TECHNOLOGIES PVT. LTD.

NIHVA TECHNOLOGY PVT. LTD. PUNE
Tel : 020 66304033
Email:- info@nihva.com
Website:- www.nihva.com


	SIGN	DATE	
DRAWN	ABHIJIT	25/10/15	CLIENT - MUKUND CONSTRUCTION
CHECK	ANIL	25/10/15	PROJECT - NEUMAN AND ESSER
REV.	01		SITE - BHOSARI MIDC
APPRD.			DWG. NO. - NIHVA/15-16/135
MFG			SCALE: 01 | WT: | SHEET: 01 OF 01
Ref. No.			If any queries contact : projects@nihva.com

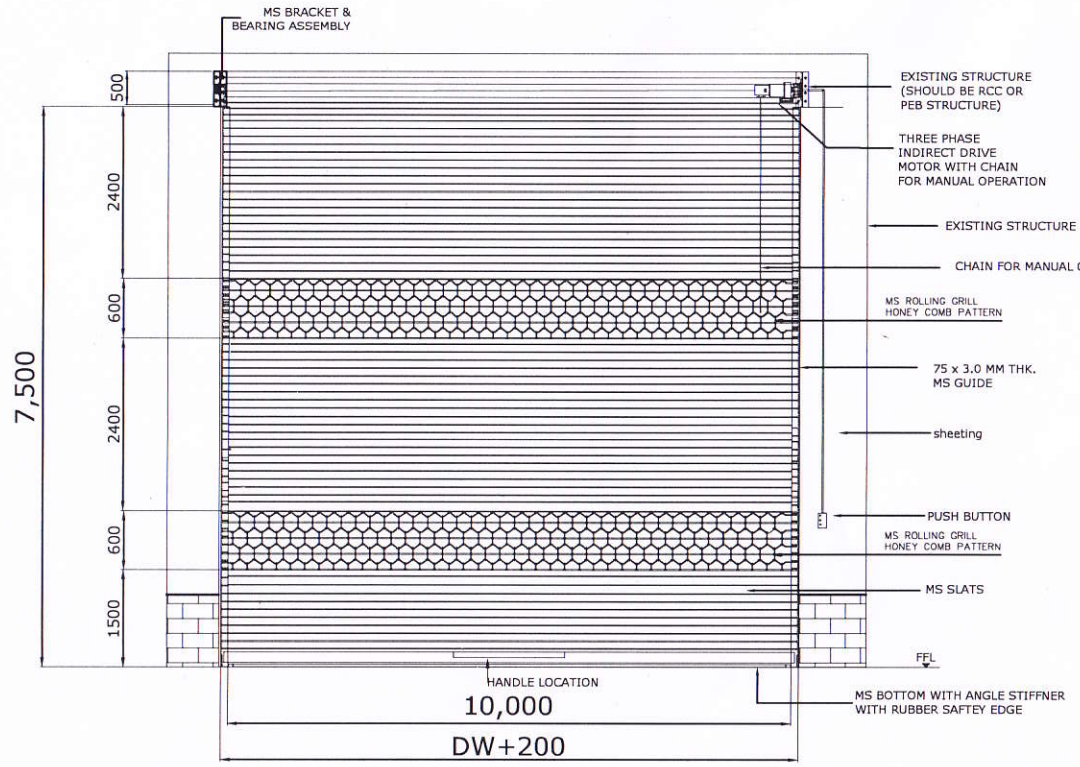


ELEVATION

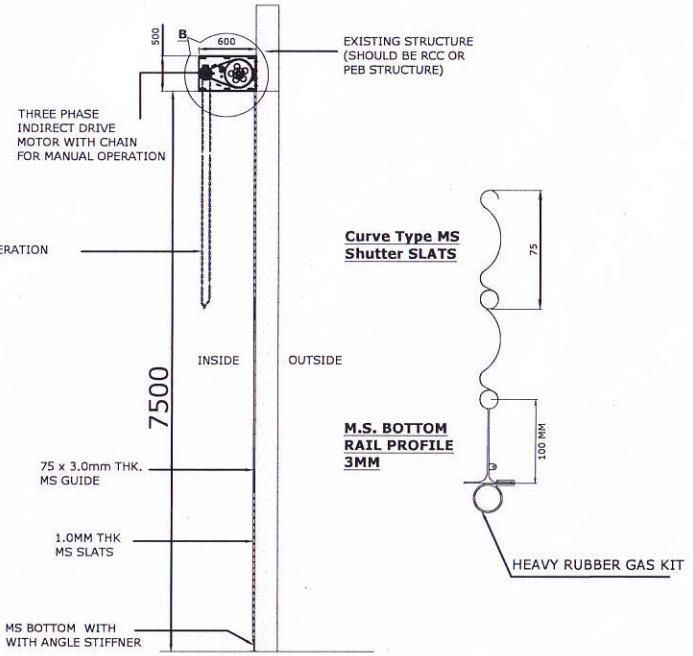

SIDE VIEW

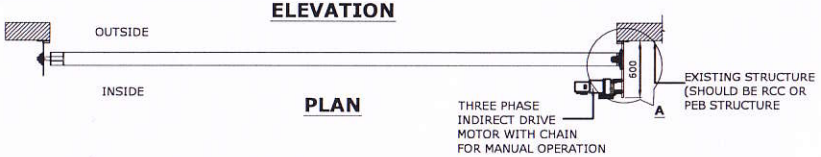

PLAN

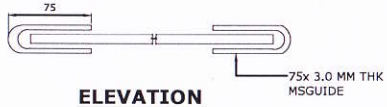

ELEVATION

DW Door Width	DH Door Height	QUANTITY
10000 mm	7500 mm	1

Approved

MS Patil

Patil

This drawing & designing is the property of NIHVA TECHNOLOGIES. Not be sold or copy to any other concern.

MOTORIZED ROLLING SHUTTER

CLIENT APPROVAL

ALL DIMENSION ARE IN mm

NIHVA TECHNOLOGIES PVT. LTD.

NIHVA TECHNOLOGY PVT. LTD. PUNE
Tel : 020 66304033
Email:- info@nihva.com
Website:- www.nihva.com

	SIGN	DATE
DRAWN	ABHIJIT	25/10/15
CHECK	ANIL	25/10/15
REV.	01	
APPRD.		
MFG		
Ref. No.		

CLIENT - MUKUND CONSTRUCTION

PROJECT - NEUMAN AND ESSER

SITE - BHOSARI MIDC

DWG. NO. - NIHVA/15-16/138

SCALE: 01 | WT: | SHEET: 01 OF 01

If any queries contact : projects@nihva.com

PRODUCED BY AN AUTODESK EDUCATIONAL PRODUCT


PRODUCED BY AN AUTODESK EDUCATIONAL PRODUCT


SPECIFICATIONS :-

H – Overall Height of Door Frame.
W – Overall Width of Door Frame.
C – Clear Width opening
T – Nominal Shutter Thickness = 43mm.
D – Depth of Door Frame (100mm approx).


NOTES :-

1) Door Frames shall be fabricated from 1.2MMThk. GI (IS 277) sheets to form a single rebate profile & fixed to wall with Anchor Bolts.
2) Shutter Panels shall be fabricated from 1.2mmThk. GI (IS 277) sheets having Tray & Cover construction to provide a nominal thickness of 43mm. Shutter flatness may vary till 5mm depending upon the door size & Shutter shall have infill material with reinforcements at top, bottom edges & for hardware fitments.
3) 4nos. SS 4" Ball Bearing Hinges shall be provided on one Shutter as shown.
4) DORMA PHCR 1000 Single Point Panic bar
5) Outside Trim 2905
6) Door Closer

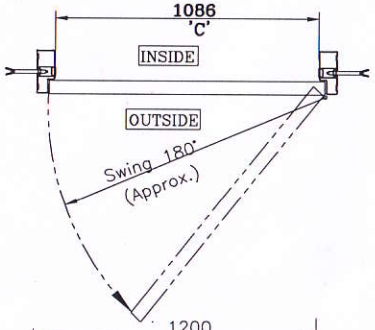


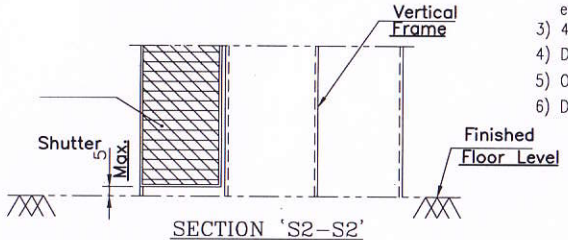

SECTION 'S2–S2'

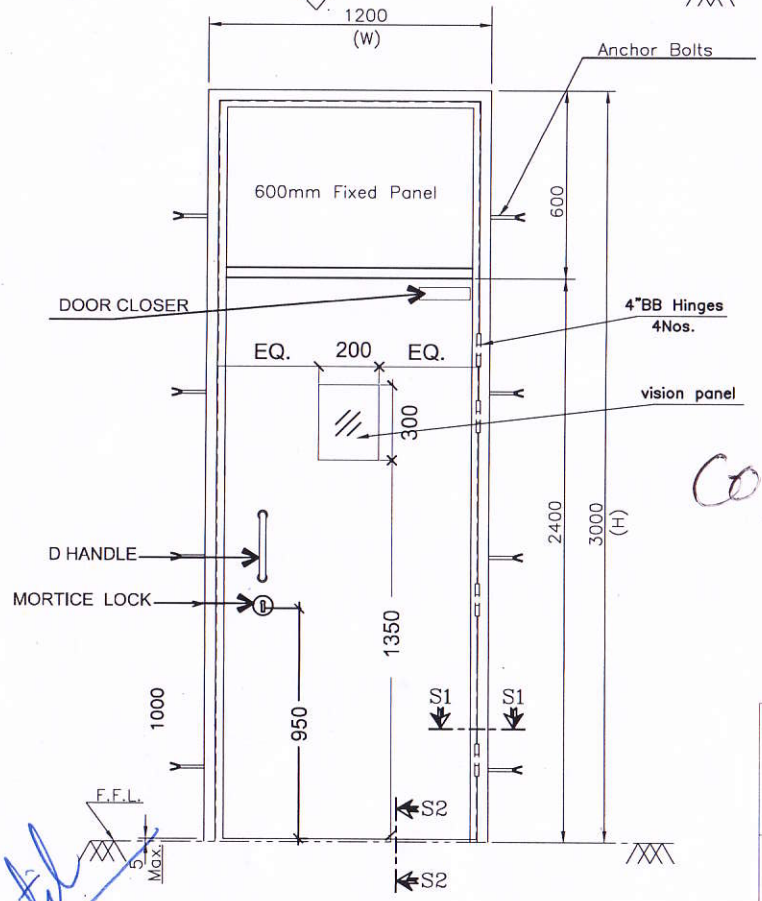

SINGLE LEAF DOOR

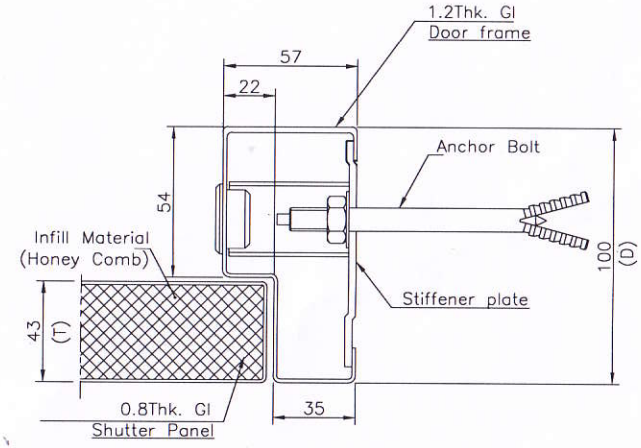

SINGLE REBATE FRAME

Colour – Red

QUANTITY:3Nos.

This drawing & designing is the property of NIHVA TECHNOLOGIES. Not be sold or copy to any other concern

TITLE: FIRE DOOR	ALL DIMENSION ARE IN mm		NIHVA TECHNOLOGIES PVT. LTD.
	SIGN	DATE	
DRAWN	ABHIJIT	25/10/15	CLIENT - MUKUND CONSTRUCTION
CHECK	ANIL	25/10/15	PROJECT- NEUMAN AND ESSER
REV.	01		SITE - BHOSARI MIDC
APPRD.			DWG. NO. - NIHVA/15-16/150
MFG			SCALE: 01 WT: SHEET: 01
Ref. No.			If any queries contact : projects@nihva.com

CLIENT APPROVAL

NIHVA TECHNOLOGY PVT. LTD. PUNE
Tel : 020 66304033
Email:- info@nihva.com
Website:- www.nihva.com

Approved

M S Patil

PRODUCED BY AN AUTODESK EDUCATIONAL PRODUCT