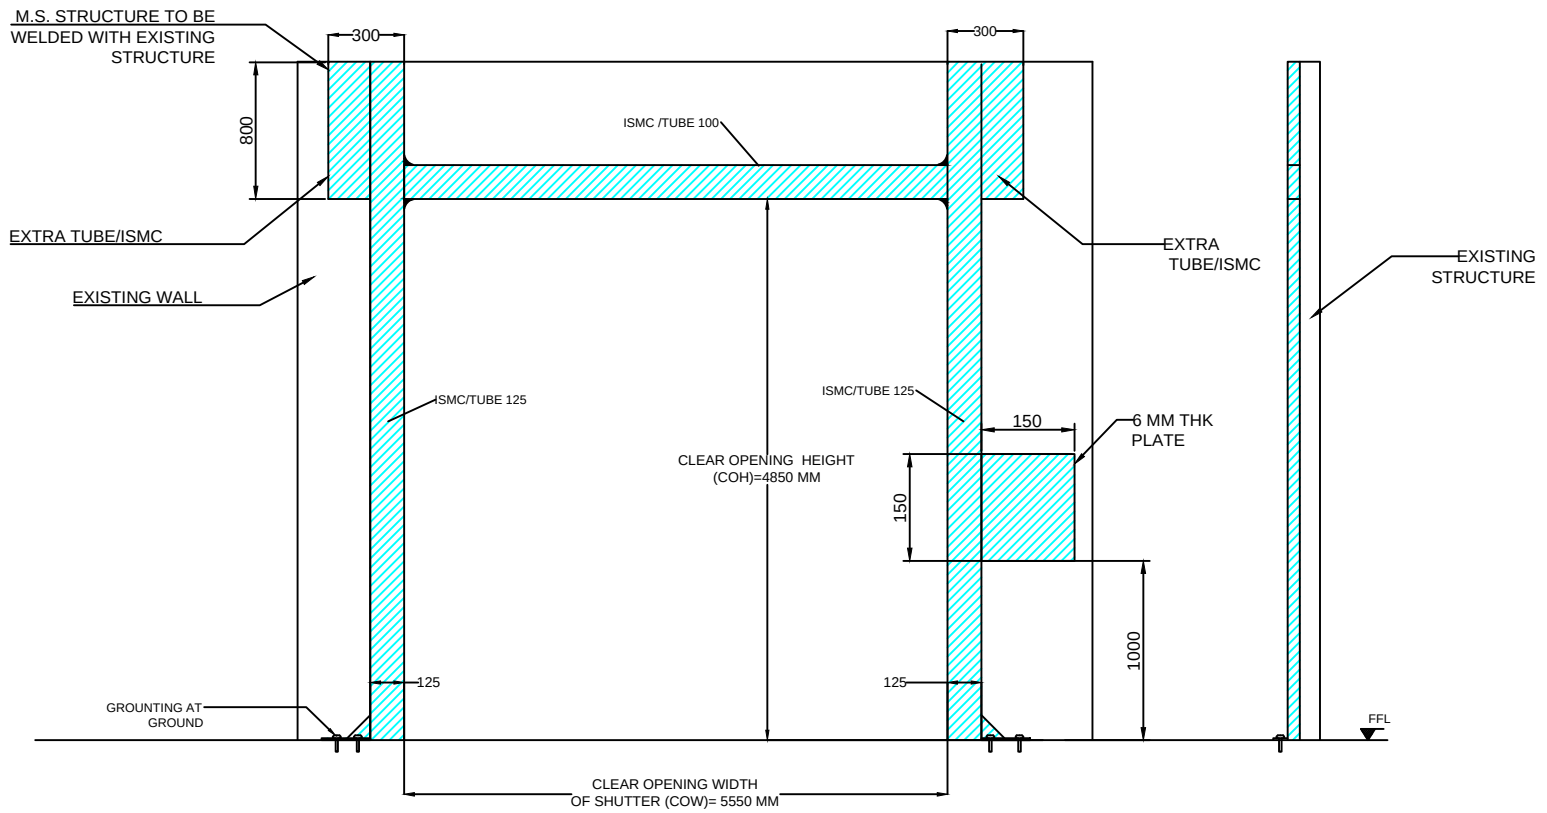


STRUCTURE

SR NO	CLEAR OPENING WIDTH(CW)	CLEAR OPENING HEIGHT(CH)	QTY	LOCATION
1	5550	4850	1	1

TOLERANCE - ±10mm

This drawing & design is the property of NIHVA TECHNOLOGIES. Not to be sold or copied to any other concern.

TITLE M.S. STRUCTURE 1

	NAME	SIGN	DATE
DRAWN	S.M.S.		16.1.2021
CHECK			
APPRD.			

If any queries contact : design@nihva.com

ALL DIMENSION ARE IN mm

NIHVA TECHNOLOGIES PVT. LTD.
NIHVA TECHNOLOGIES PVT. LTD. PUNE
Tel : 020 66304033
Website:- www.nihva.com
Email:- info@nihva.com

CLIENT - V TECH

PROJECT -

SITE LOCATION -

DWG. NO. : NIHVA/20-21/0138

REV- R00

SHEET: 01 OF 01