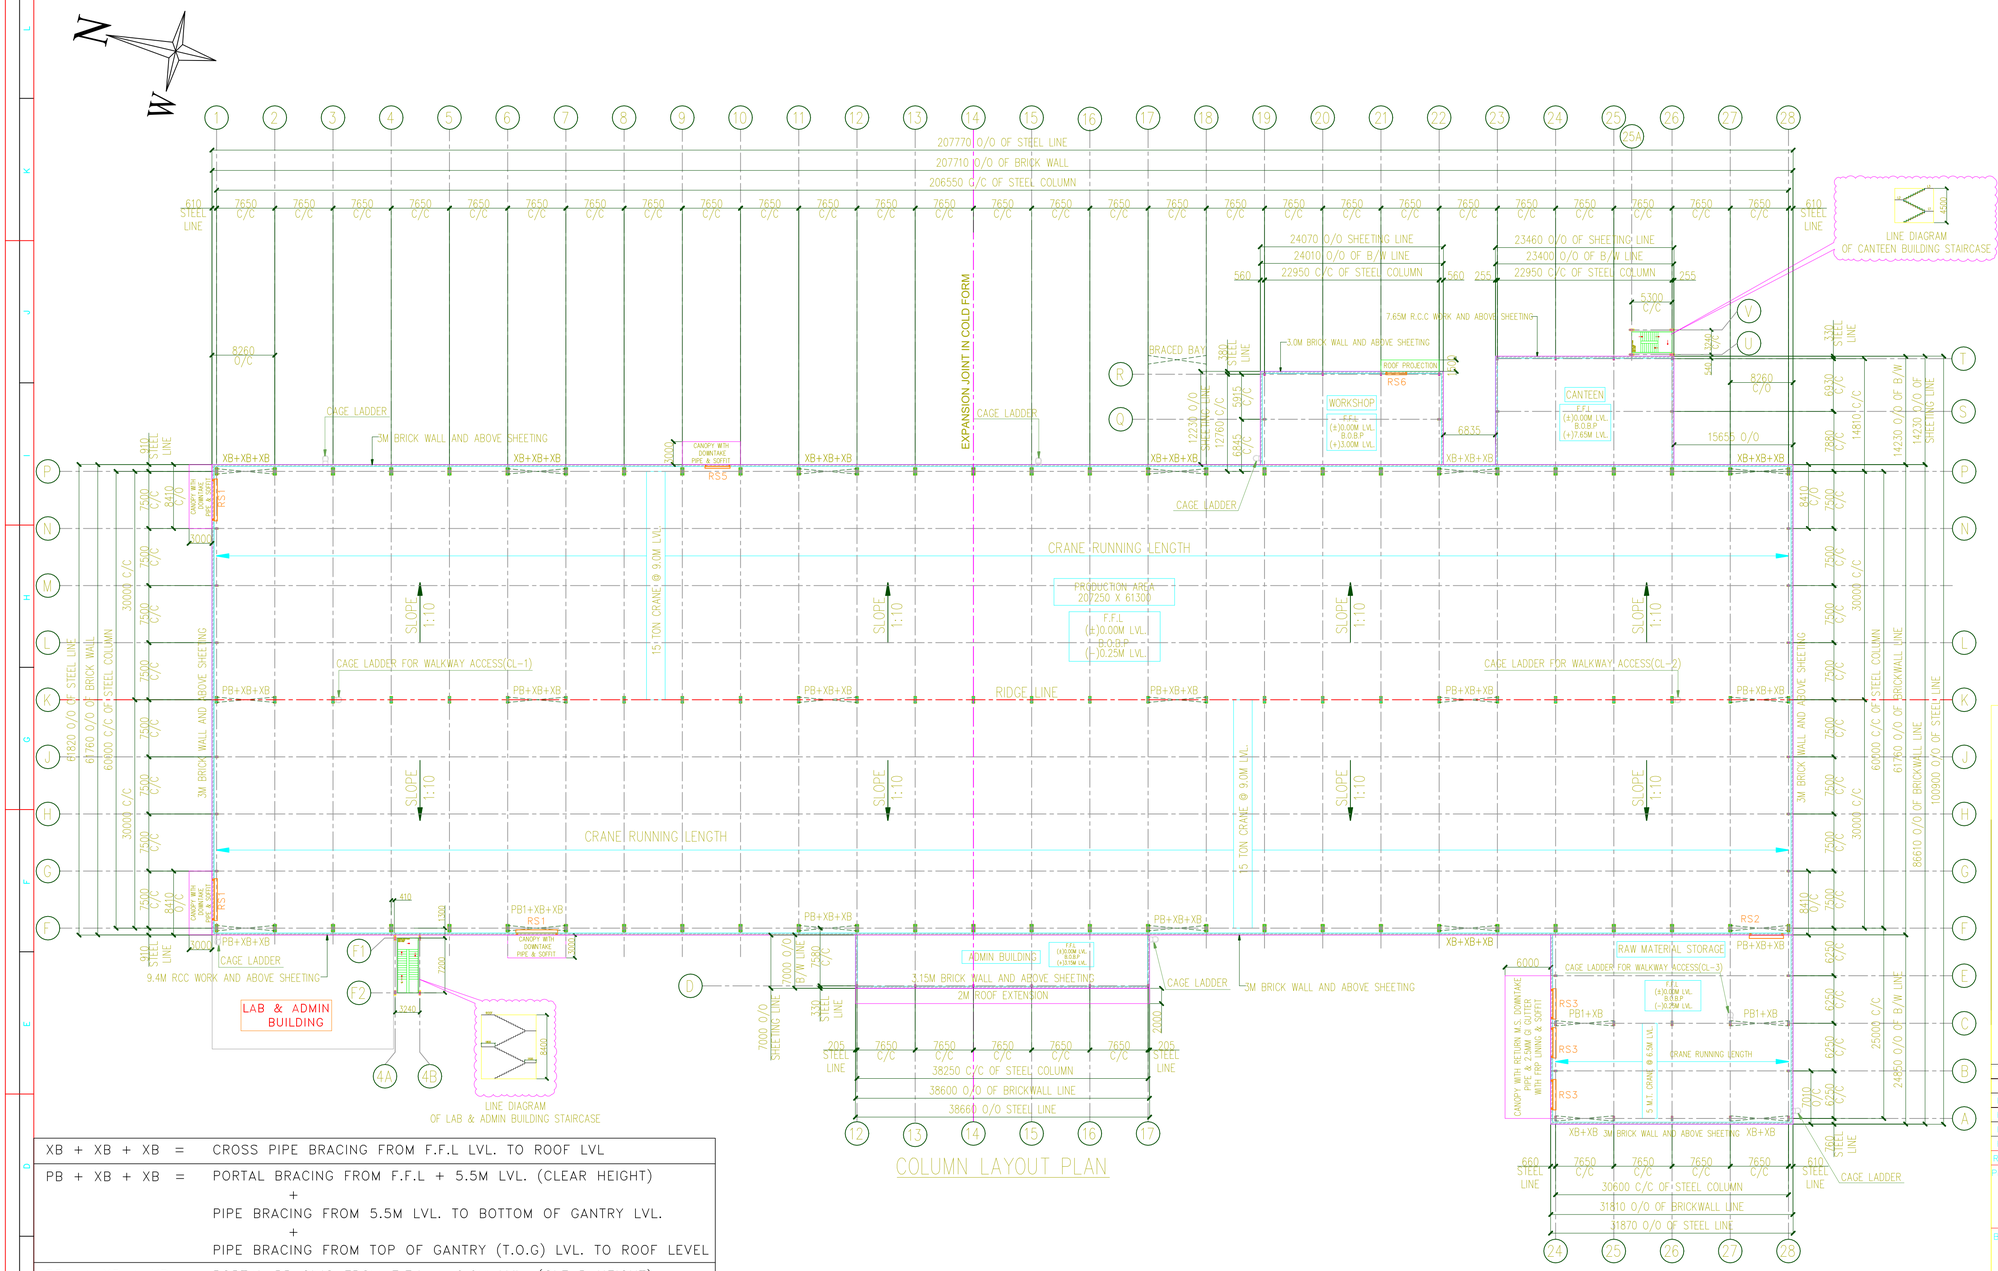


XB + XB + XB =	CROSS PIPE BRACING FROM F.F.L LVL. TO ROOF LVL	
PB + XB + XB =	PORTAL BRACING FROM F.F.L + 5.5M LVL. (CLEAR HEIGHT) + PIPE BRACING FROM 5.5M LVL. TO BOTTOM OF GANTRY LVL. + PIPE BRACING FROM TOP OF GANTRY (T.O.G) LVL. TO ROOF LEVEL	
PB1 + XB + XB =	PORTAL BRACING FROM F.F.L + 6.0M LVL. (CLEAR HEIGHT) + PIPE BRACING FROM 6.0M LVL. TO BOTTOM OF GANTRY LVL. + PIPE BRACING FROM TOP OF GANTRY (T.O.G) LVL. TO ROOF LEVEL	
PB1 + XB =	PORTAL BRACING FROM F.F.L + 6.0M LVL. (CLEAR HEIGHT) + PIPE BRACING FROM 6.0M LVL. TO ROOF LEVEL	
XB + XB =	CROSS PIPE BRACING FROM F.F.L LVL. TO ROOF LVL	
PB =	PORTAL BRACING FROM F.F.L TO ROOF LEVEL	

DOOR SCHEDULE

RS1	5.00	5.00	0.00	3	F.F.L	M.S ROLLING SUTTER
RS2	4.00	4.00	0.00	1	F.F.L	M.S ROLLING SUTTER
RS3	3.50	4.00	0.00	3	F.F.L	M.S ROLLING SUTTER
RS5	3.00	3.00	0.00	1	F.F.L	PERFORATED MS ROLLING SHUTTER
RS6	2.50	3.00	0.00	1	F.F.L	PERFORATED MS ROLLING SHUTTER

ISSUED FOR APPROVAL

SENT ON .....

IN ORDER TO SCHEDULE THIS PROJECT IN THE MOST EFFICIENT MANNER, RETURN THESE DOCUMENTS, MARKED WITH YOUR COMMENTS, WITHIN TWO WEEKS FROM THE ABOVE MENTIONED DATE.

ANY CHANGES MADE AFTER APPROVAL OF THESE DRAWINGS MAY DELAY THE FABRICATION AND DELIVERY PROCESS.

THESE DRAWINGS ARE GOOD FOR CONSTRUCTION.

1. APPROVED
   - ☐ NO CHANGES, PROCEED WITH FABRICATION.
2. APPROVED AS NOTED
   - ☐ FABRICATION MAY PROCEED ON THE BASIS OF
   - ☐ CORRECTIONS INDICATED.
3. NOT APPROVED, RE-SUBMIT FOR APPROVAL.

REVIEWED BY .....

NAME

SIGNATURE DATE

REV	REVISIONS	DRAWN	DESIGN	DATE
R3	AS PER CLIENT COMMENT	S.A.	G.K.	03/10/2024
R2	AS PER CLIENT COMMENT	S.A.	G.K.	26/09/2024
R1	AS PER CLIENT COMMENT	S.A.	G.K.	02/09/2024
R0	AS PER CLIENT COMMENT	S.A.	G.K.	22/08/2024

Project: PRE ENGINEERED BUILDING

Building: PEB BUILDING

Drawing Title: COLUMN LAYOUT PLAN

Consultant: SHAH & TALATI DESIGN & ENGINEERING

Client: M/S ROCATE CABLES LLP

M/S PRESTEEL LLP
4TH FLOOR, 401-402, SHILP SATVED, SINDHU BHAVAN MARG, BODAKDEV, AHMEDABAD, GUJRAT(INDIA). Pin:-380054

Drawn by:	S.A.		Scale: 1:1	Date: 22.08.2024	
Checked by:	G.K.		Project No: PSL-J-196	Drawing No: GA-01	Revision: R3
Designed by:	G.K.				

NOTE: -

1. All rights reserved. This drawing contains proprietary information which is protected by copyright. No part of this drawing may be reproduced, translated in computer language, or transmitted in any form whatsoever without the prior written consent of OWNER

SHEET SIZE-A3