

SCISSOR LIFT SIZE	WIDTH (W)	LENGTH (L)	HEIGHT (H)
	1500	2000	500


PIT DIMENSION	WIDTH (W 1)	LENGTH (L 1)	DEPTH (D)	ALL DIMENSIONS ARE IN mm
	1650	2150	1510	

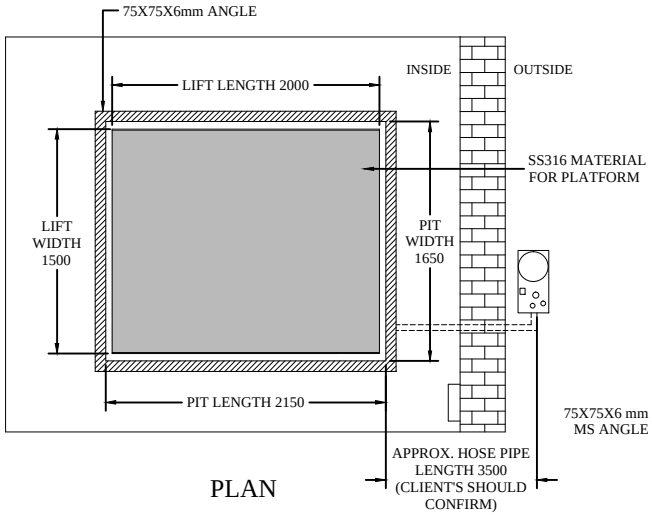

PLAN

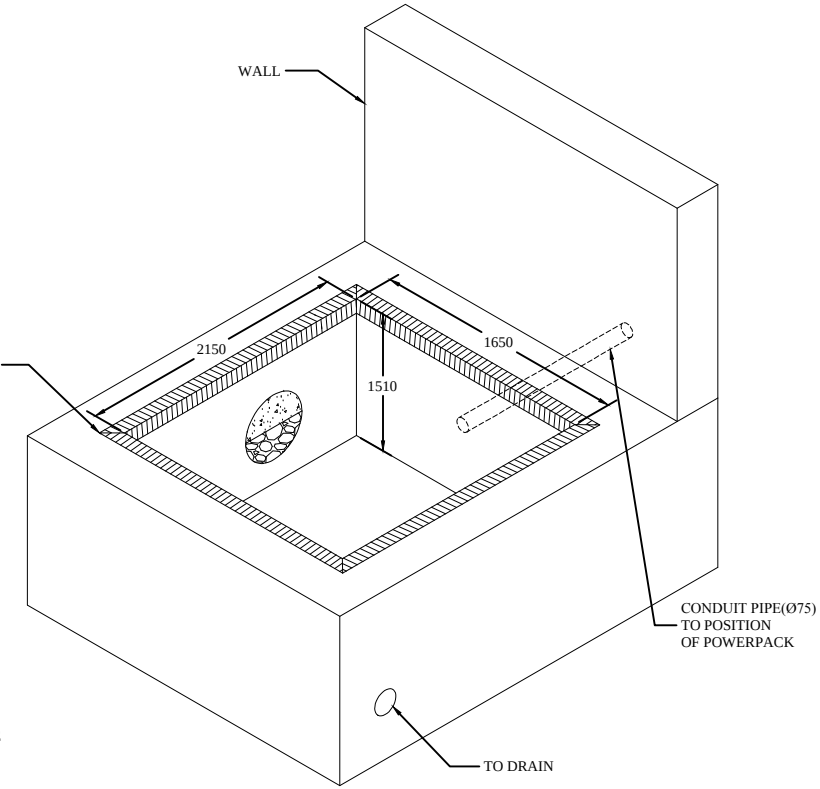

PIT DRAWING

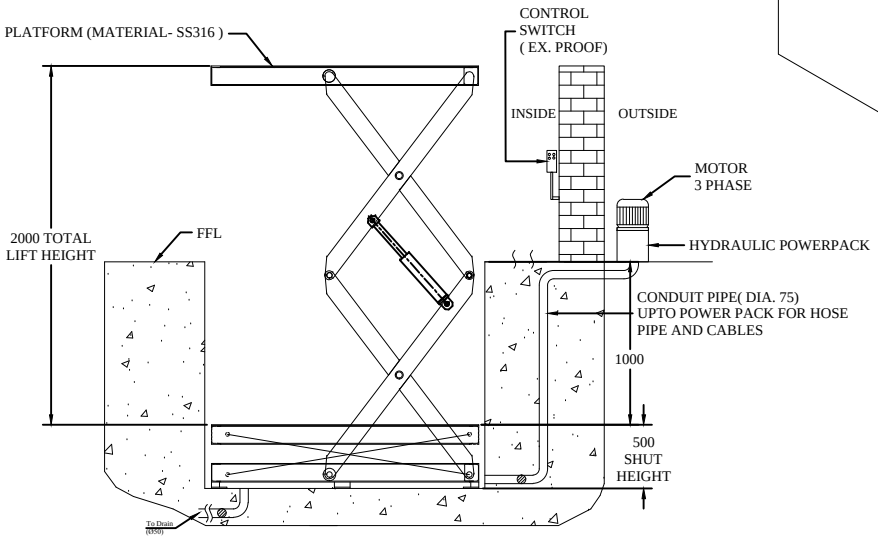

ELEVATION

SCISSOR LIFT- 2MT CAPACITY

DIMENSION :

CLEAR WIDTH	CLEAR HEIGHT	QUANTITY

MATERIAL :

THICKNESS :

IMPORTANT NOTE-
1. ALL REQUIRED CIVIL WORK SHALL BE IN CLIENT'S SCOPE.
2. CLIENT SHOULD SPECIFY THE LENGTH OF HOSE PIPE & WIRE FROM PIT TO THE HYD. POWERPACK POSITION TO AVOID POST DELIVERY ISSUES.
3. CONTROL PANEL WILL BE FLAME/ EXPLOSION PROOF.

REVISION 2-
1. PIT DIMENSION CORRECTED.
2.CAPACITY REVISED.

NIHVA TECHNOLOGIES PVT. LTD.
NIHVA TECHNOLOGIES PVT. LTD. PUNE
Email:- info@nihva.com
Website:- www.nihva.com

TITLE:

SCISSOR LIFT

CLIENT'S APPROVAL :

CLIENT -FUJITA CORPORATION

PROJECT - FUJIKURA KASEI COATING INDIA

SITE LOCATION - HARYANA

DWG. NO. : NIHVA/17-18/0149/R02

SCALE: NTS	WT:	SHEET:1 OF 1

DRAWN BY: SURAJ	DATE: 28-08-2017
CHECK BY:SAGAR	DATE: 28-08-2017
APPROVED BY :SHEKHAR	DATE: 28-08-2017

If any queries contact : projects@nihva.com

NOTE: ALL DIMENSIONS ARE IN mm

THIS DRAWING & DESIGNING IS THE PROPERTY OF NIHVA TECHNOLOGIES. NOT TO BE SOLD OR COPIED TO ANY OTHER CONCERN.