

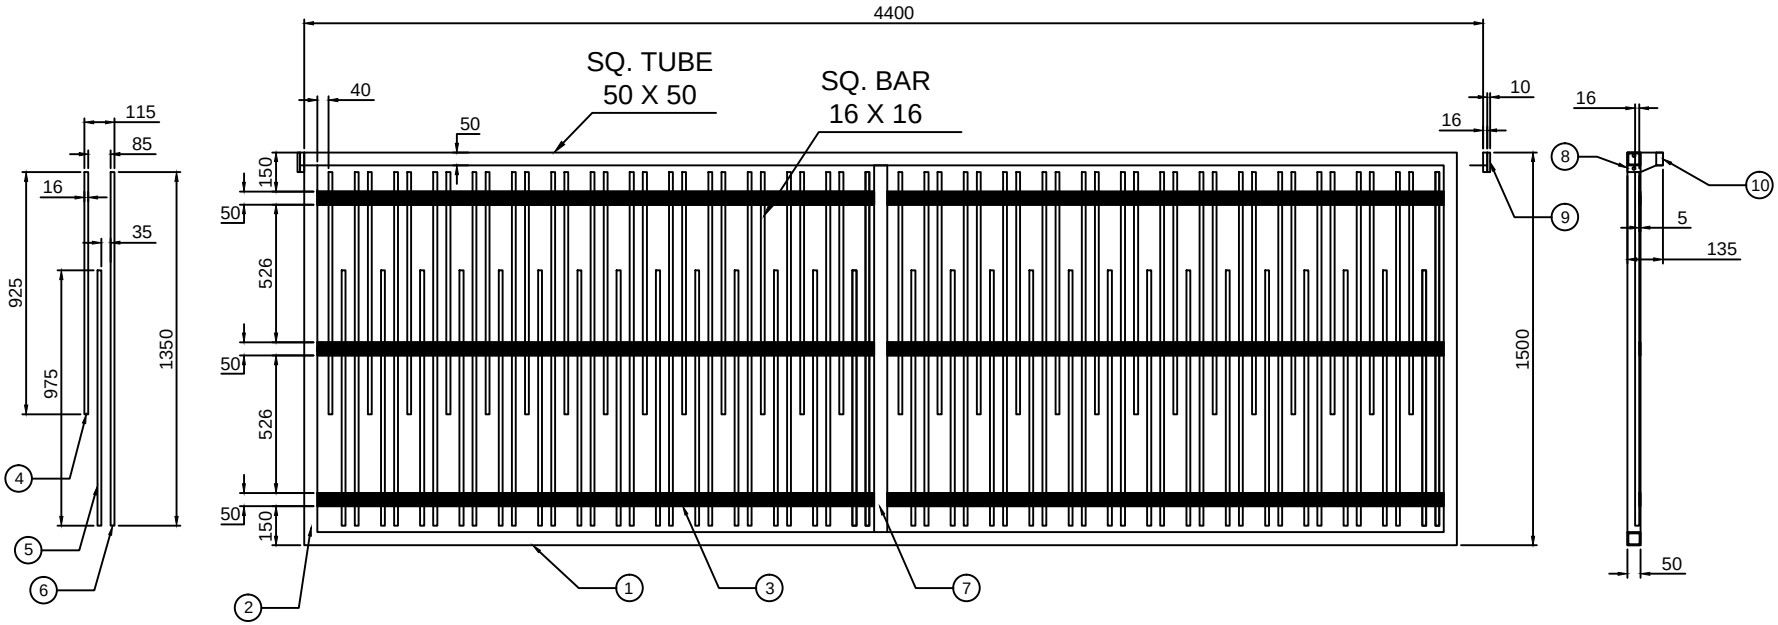


SR NO	DESCRIPTION	SPECIFICATION	QTY
10	R.TUBE	50 X 25 X 3 THK X 4430L	1 NO
9	FLAT	75 X 10 X 135L	2 NOS
8	FLAT	50 X 16 X 75L	2 NOS
7	SQ. TUBE	50 X 50 X 4 THK X 1400L	1 NO
6	MS SQ BAR	16 X 16 X 1350L	28 NOS
5	MS SQ BAR	16 X 16 X 975L	28 NOS
4	MS SQ BAR	16 X 16 X 925L	28 NOS
3	MS FLAT	50 X 5 THK X 4300L	3 NOS
2	SQ. TUBE	50 X 50 X 4 THK X 1500L	2 NOS
1	SQ. TUBE	50 X 50 X 4 THK X 4400L	2 NOS

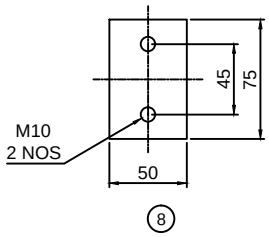

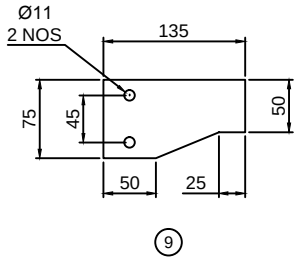

This drawing & designing is the property of NIHVA TECHNOLOGIES. Not to be sold or copied to any other concern.

TITLE: IDEAL LEAF

	NAME	SIGN	DATE
DRAWN	P.A		03.12.19
CHECKED	G.J		03.12.19
APPROVED			

If any queries contact : projects@nihva.com

ALL DIMENSION ARE IN mm

NIHVA TECHNOLOGIES PVT. LTD.
NIHVA TECHNOLOGIES PVT. LTD. PUNE
Tel : 020 66304033
Email:- info@nihva.com
Website:- www.nihva.com

CLIENT -

PROJECT -

SITE LOCATION -

DWG. NO. : NIHVA/19-20/VDR/232 | REV: R00

SCALE: NTS | WT: | SHEET: 01 OF 01