
DO NOT SCALE

REVISION CLOUD CHANGES :

1. DESIGN INTENT CHANGE AS PER KITCHEN WORKSHOP (IKEA)
2. ADDITIONAL DETAILS ADDED
3. CEILING DESIGN CHANGED IN SFM AREA
4. CCN ROOM AND SHAFTS ADDED
5. SECONDARY STRUCTURE AS PER STRUCTURES ADDED
6. 150MM HIGH KERB PROVIDED AT THE END OF PARKING BAYS
7. WHEEL STOPPER HAS BEEN REMOVED
8. SMALL LAND ENTRANCE CLEAR OPENING WIDTH IS 2670MM
9. BLUE/YELLOW PANEL UPDATED
10. CHANNEL DRAIN AND SUMP PIT ADDED
11. SHAFT AND CUTOUT UPDATED
12. ROOF LEVEL MECH. PLATFORM AND SOLAR PANEL AREA UPDATED
13. FACADE COPING LINE UPDATED

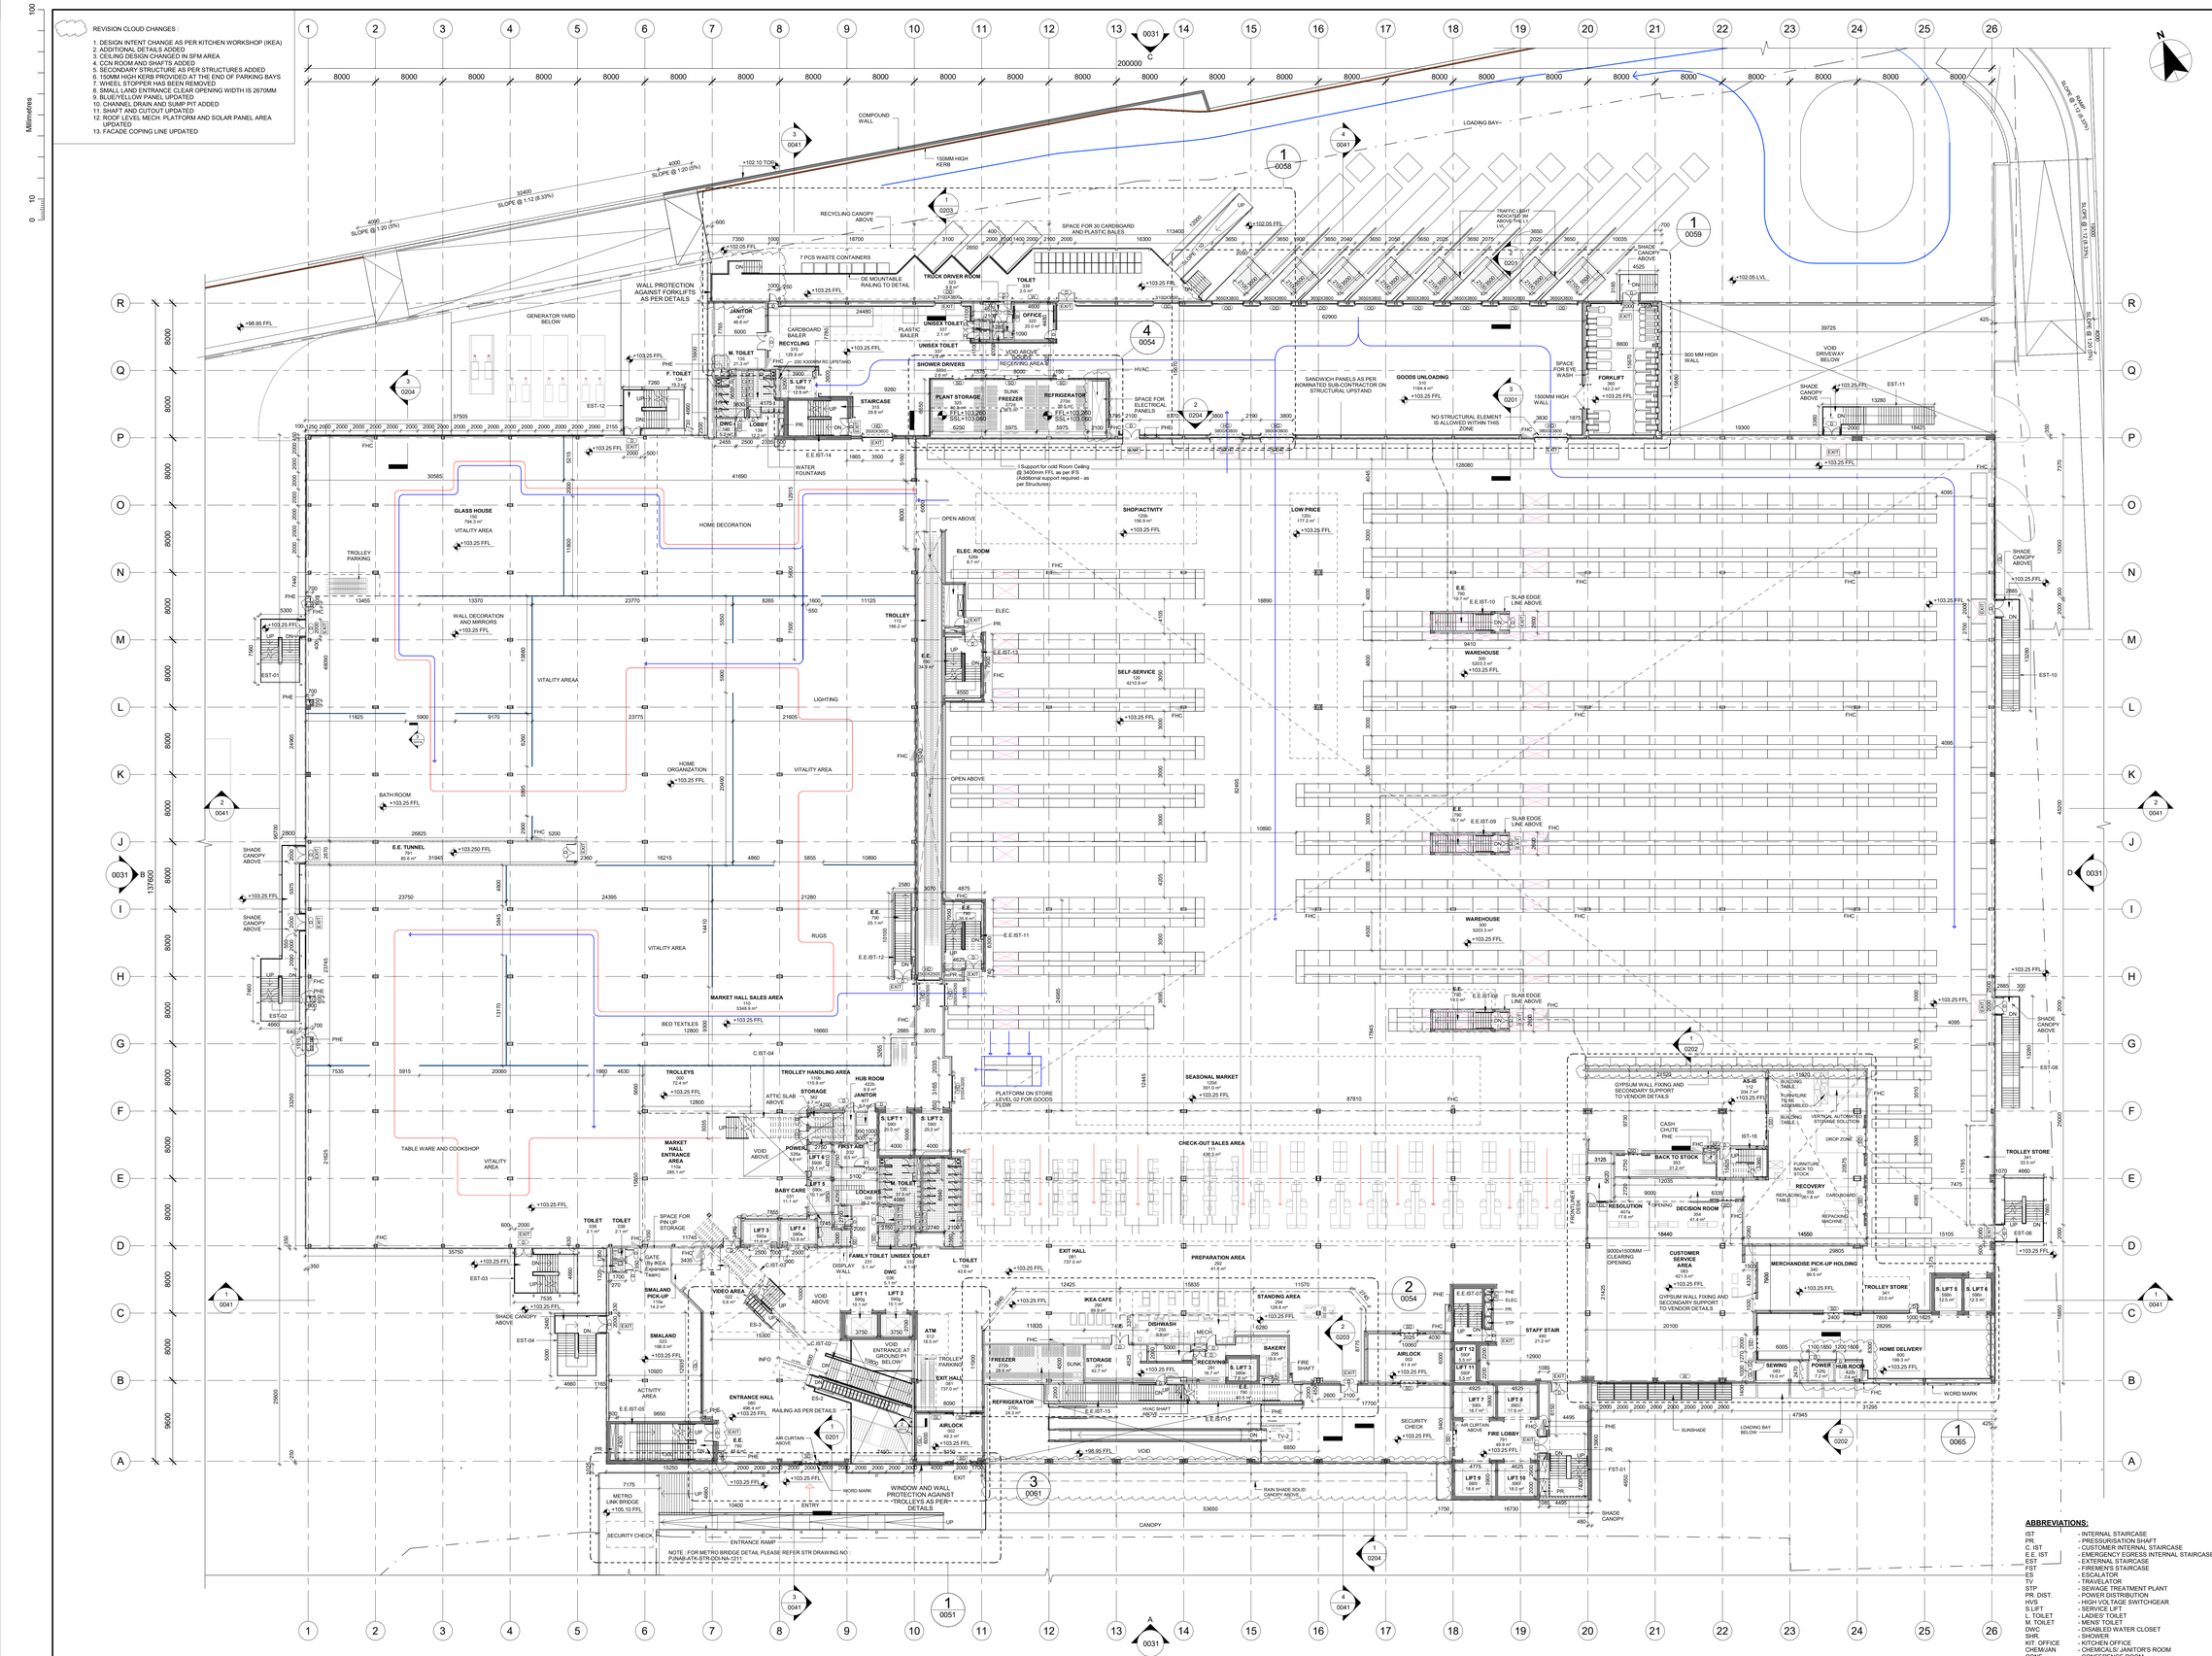

1 / 0024 STORE LEVEL 01 - COMMERCIAL LAYOUT
SCALE 1 : 250

Drawing Status
ISSUED FOR CONSTRUCTION

Rev.	Date	Description	By	Chk'd	Appr'd
R1	29/03/2019	ISSUED FOR CONSTRUCTION	BS	CTK	SD
R0	27/02/2019	ISSUED FOR CONSTRUCTION	LH	CTK	SD

SAFETY, HEALTH AND ENVIRONMENTAL INFORMATION
In addition to the hazards/risks normally associated with the types of work detailed on this drawing, note the following:
CONSTRUCTION
MAINTENANCE/CLEANING
DECOMMISSIONING/DEMOLITION
It is assumed that all works will be carried out by a competent contractor working, where appropriate, to an approved method statement

Client
IKEA India Private Limited
DLF Infinity Tower- A
8th Floor, Cyber City,Sector 25,
Gurgaon- 122002
Haryana, India

This document/drawing is the property of Inter IKEA Systems B.V. and may, in no way other than for the agreed purpose, be used, copied, reproduced, or in any other manner made known to a third party, and shall after its intended use be returned to Inter IKEA Systems B.V.
© Inter IKEA Systems B.V., [2016]

ATKINS
18th and 19th Floor
Tower C, DLF Cyber Greens,
DLF Cyber City,
DLF Phase- III, Gurgaon,
Haryana- 122 002, India
Tel: +(91) 124 384 7199
Fax: +(91) 124 455 2475
www.atkinsglobal.com
Copyright © Atkins Limited (2013)

Project Title
IKEA BENGALURU

Drawing Title
GENERAL ARRANGEMENT STORE (L1) LEVEL PLAN

Scale	Designed	Drawn	Checked	Authorised
1 : 250	BS	BS	AD	SD
Original Size	Date	Date	Date	Date
A0	22/12/2017	15/07/2018	28/08/2018	07/12/2018

Drawing Number
PJNAB-ATK-ARC-GFP-L1-0024
Revision
R1