
OUTRIGGER ASSLY

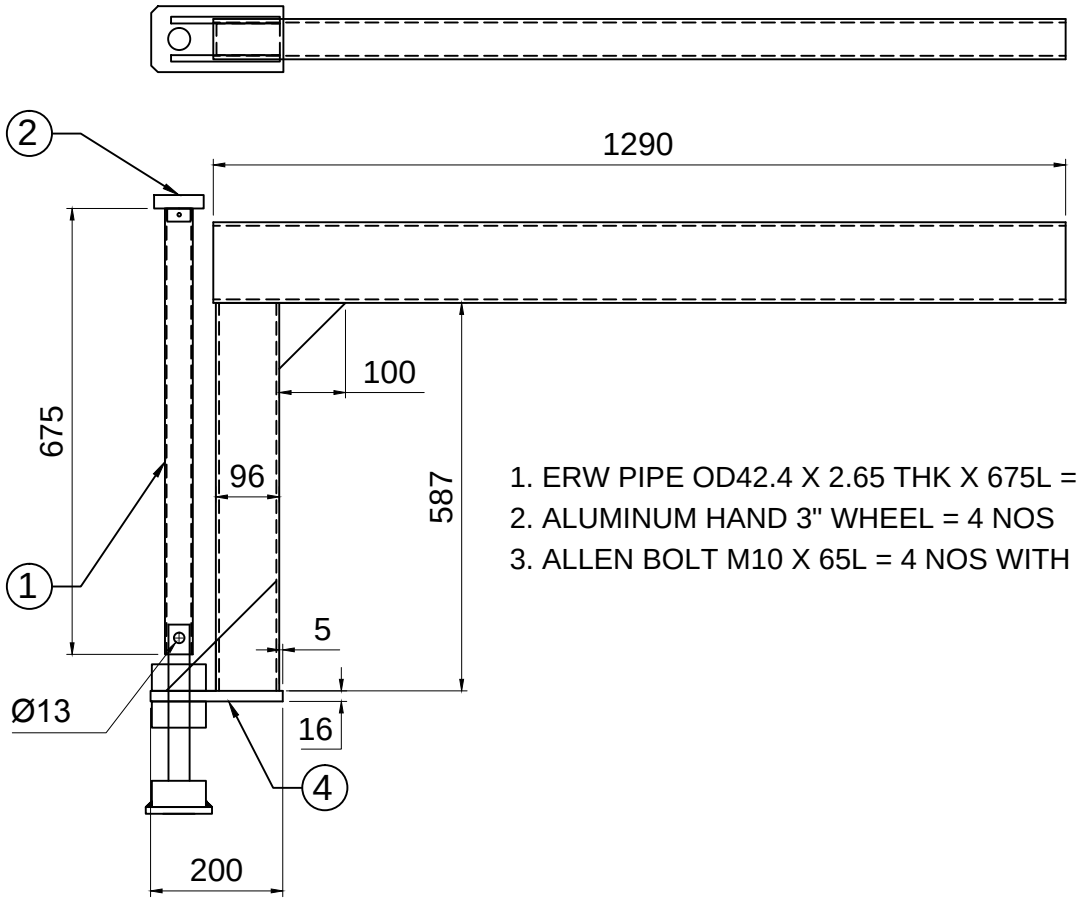

1. ERW PIPE OD42.4 X 2.65 THK X 675L = 4 NOS
2. ALUMINUM HAND 3" WHEEL = 4 NOS
3. ALLEN BOLT M10 X 65L = 4 NOS WITH SPRING WASHER

This drawing & design is the property of NIHVA TECHNOLOGIES. Not to be sold or copied to any other concern.

TITLE : - OUTRIGGER			NIHVA TECHNOLOGIES PVT. LTD. PUNE Tel : 020 66304033 Email:- info@nihva.com Website:- www.nihva.com
	SIGN	DATE	
DRAWN	P.A	04.10.2018	CLIENT -
CHECK	R.D	04.10.2018	PROJECT -
REV.			SITE -
APPROVAL			DWG. NO. : NIHVA/18-19/MFG/NSL/1018/019
If any queries contact : projects@nihva.com			SCALE: NTS | WT: | SHEET: 01 OF 01
ALL DIMENSION ARE IN mm			