


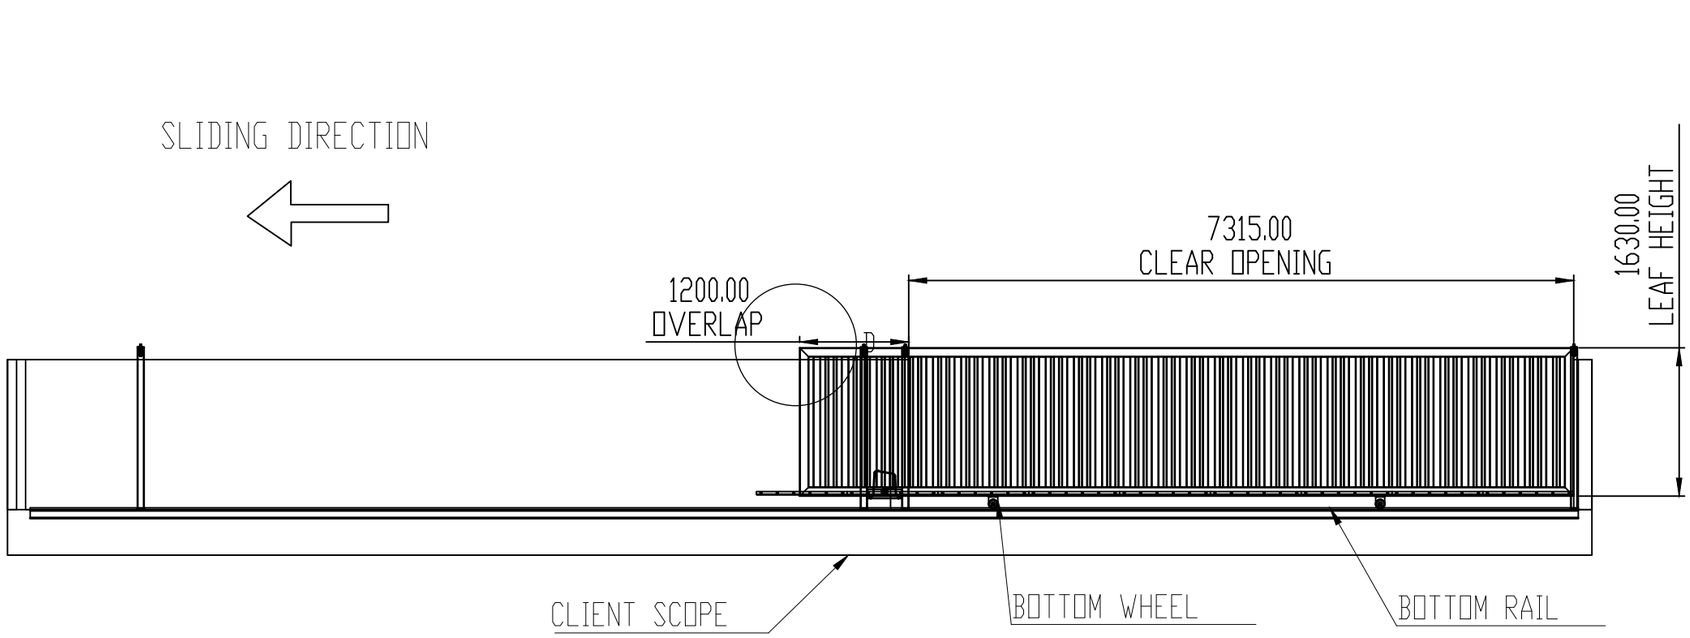


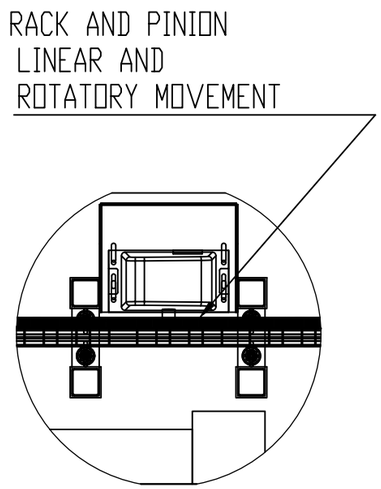

DETAIL A
SCALE 1 : 15


POST 1 NYLON
BEARING ASM

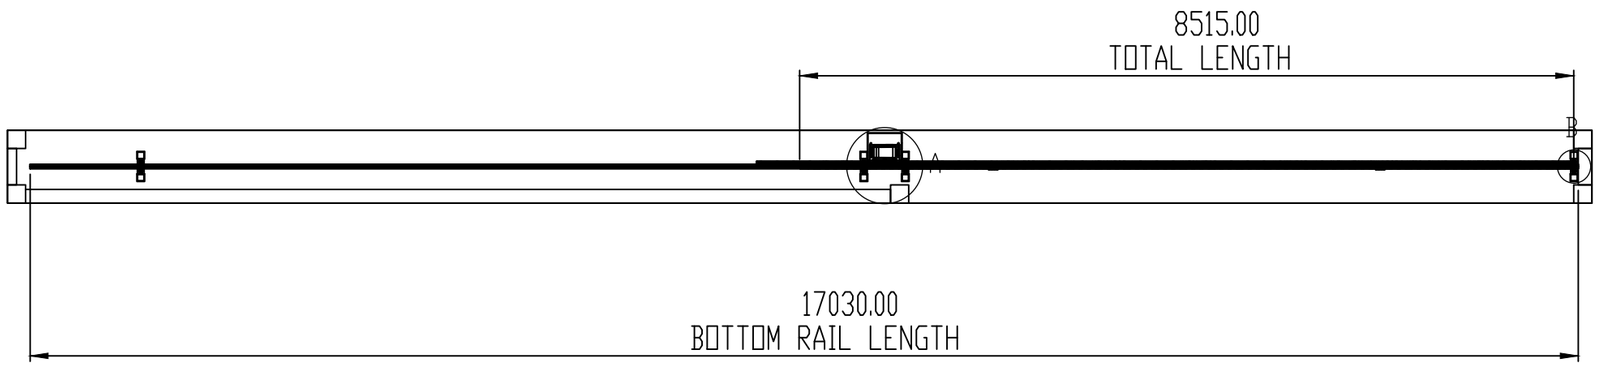

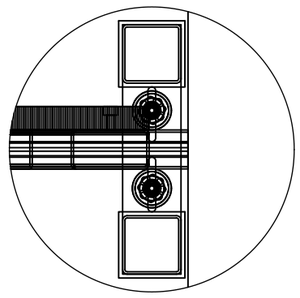

DETAIL B
SCALE 1 : 7

POST 2 NYLON
BEARING ASM

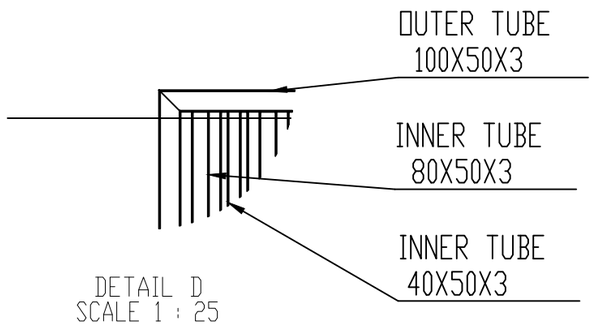

DETAIL D
SCALE 1 : 25

SLIDING GATE
8515L X 1630 H
(OVELAPPING +MOTOR MOUNTING
DISTANCE CONSIDER)

TITLE - GATE				NIHVA Technologies Pvt. Ltd. — NIHVA TECHNOLOGIES PVT.LTD.PUNE — Website - www.nihva.com
DWG NO - NTPL			QTY - 1	
	NAME	SIGNATURE	DATE	PROJECT NO - NTPL
DRAWN	V.B.		21-05-25	PRODUCT - SLIDING GATE
CHK'D	S.W.		21-05-25	SITE LOCATION -LUCKNOW
APPV'D	V.T.		21-05-25	
if any queries contact supportautomation@nihva.com				REVISION -
ALL DIMENSION ARE IN mm			A3	SCALE - SHEET 1 OF 1