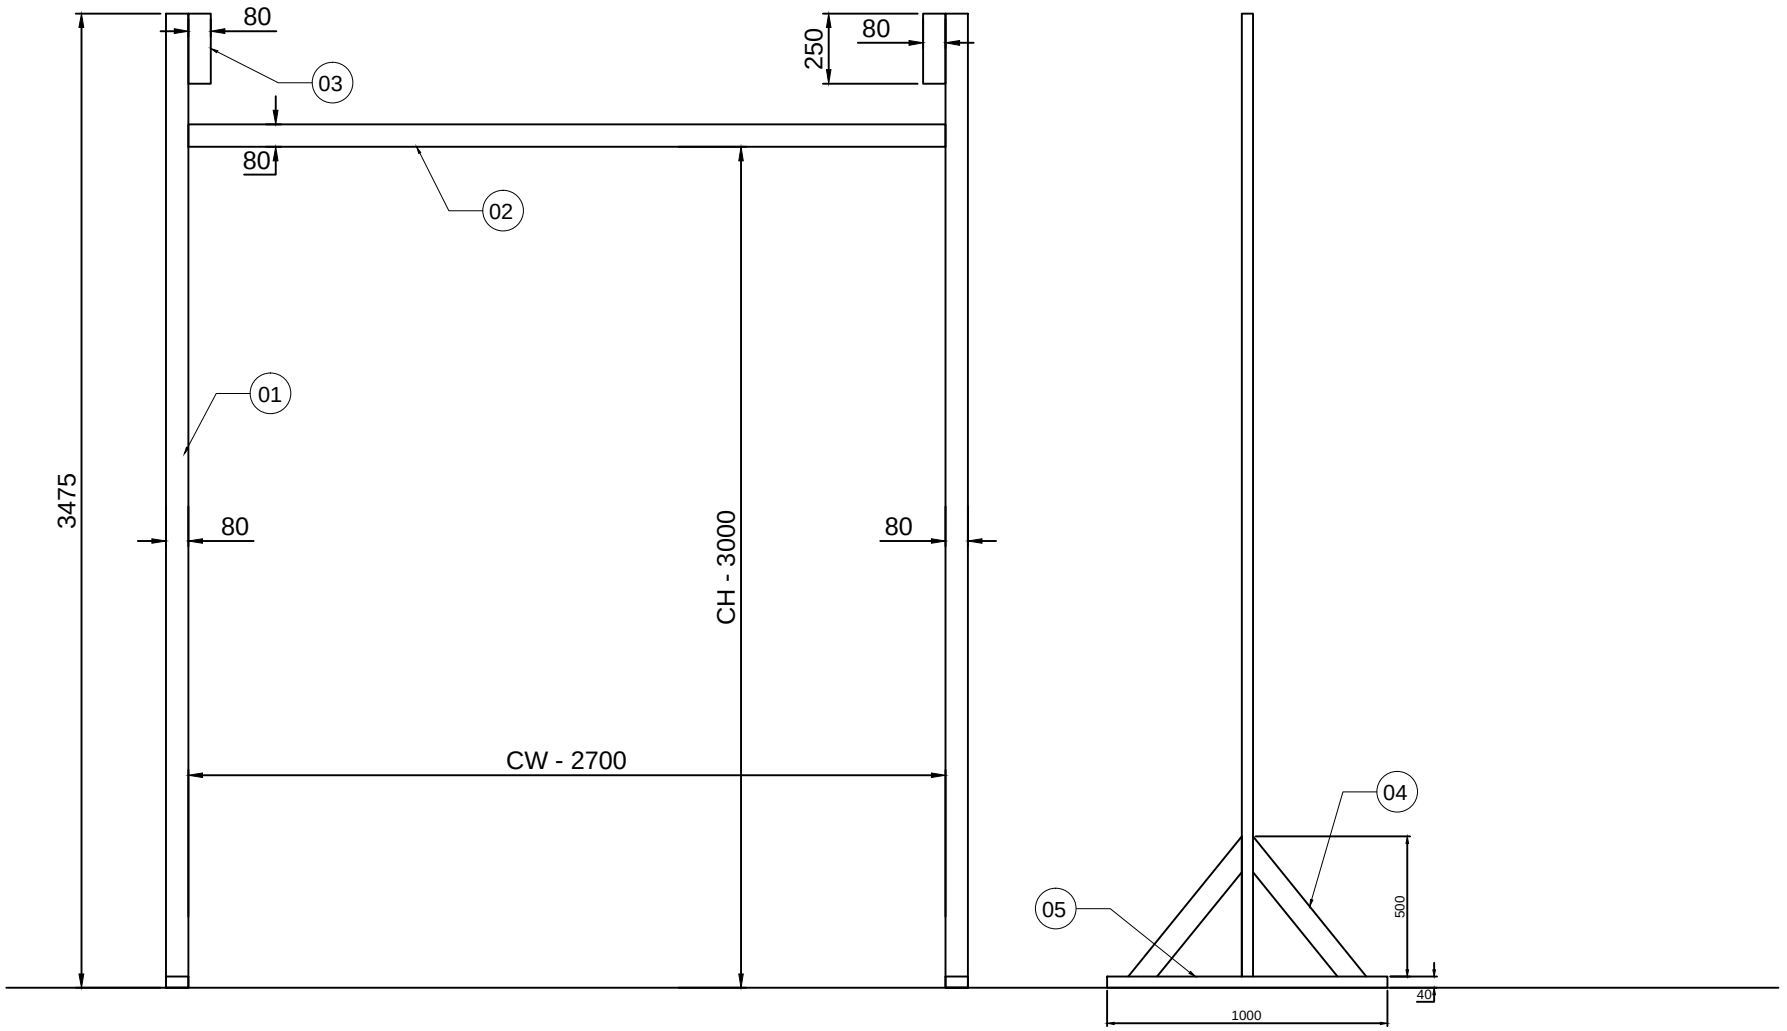

NOTE : ALL STRUCTURE SHOULD BE ON BOLTING ARRANGEMENT

SR.NO	DESCRIPTION	SPECIFICATION	QTY
05	R.TUBE	80 X 40 X 3 THK X 1000L	1 NO
04	R.TUBE	80 X 40 X 3 THK X 650L	4 NOS
03	R.TUBE	80 X 40 X 3 THK X 250L	2 NOS
02	R.TUBE	80 X 40 X 3 THK X 2700L	1 NO
01	R.TUBE	80 X 40 X 3 THK X 3475L	2 NOS

This drawing & designing is the property of NIHVA TECHNOLOGIES. Not to be sold or copied to any other concern.

TITLE
SECTIONAL DOOR STRUCTURE.

	NAME	SIGN	DATE
DRAWN	P.V.A		31.05.19
CHECK	V.M.T		31.05.19
APPROVAL			

If any queries contact : design@nihva.com

ALL DIMENSION ARE IN mm

NIHVA
NIHVA TECHNOLOGIES PVT. LTD.
Website:- www.nihva.com
NIHVA TECHNOLOGIES PVT. LTD. PUNE
Tel : 020 66304033
Email:- info@nihva.com

CLIENT -

PROJECT -

SITE -

DWG. NO. : NIHVA/19-20/VDR/050 | REV- 00

SCALE: NTS | WT: | SHEET: 01 OF 01