

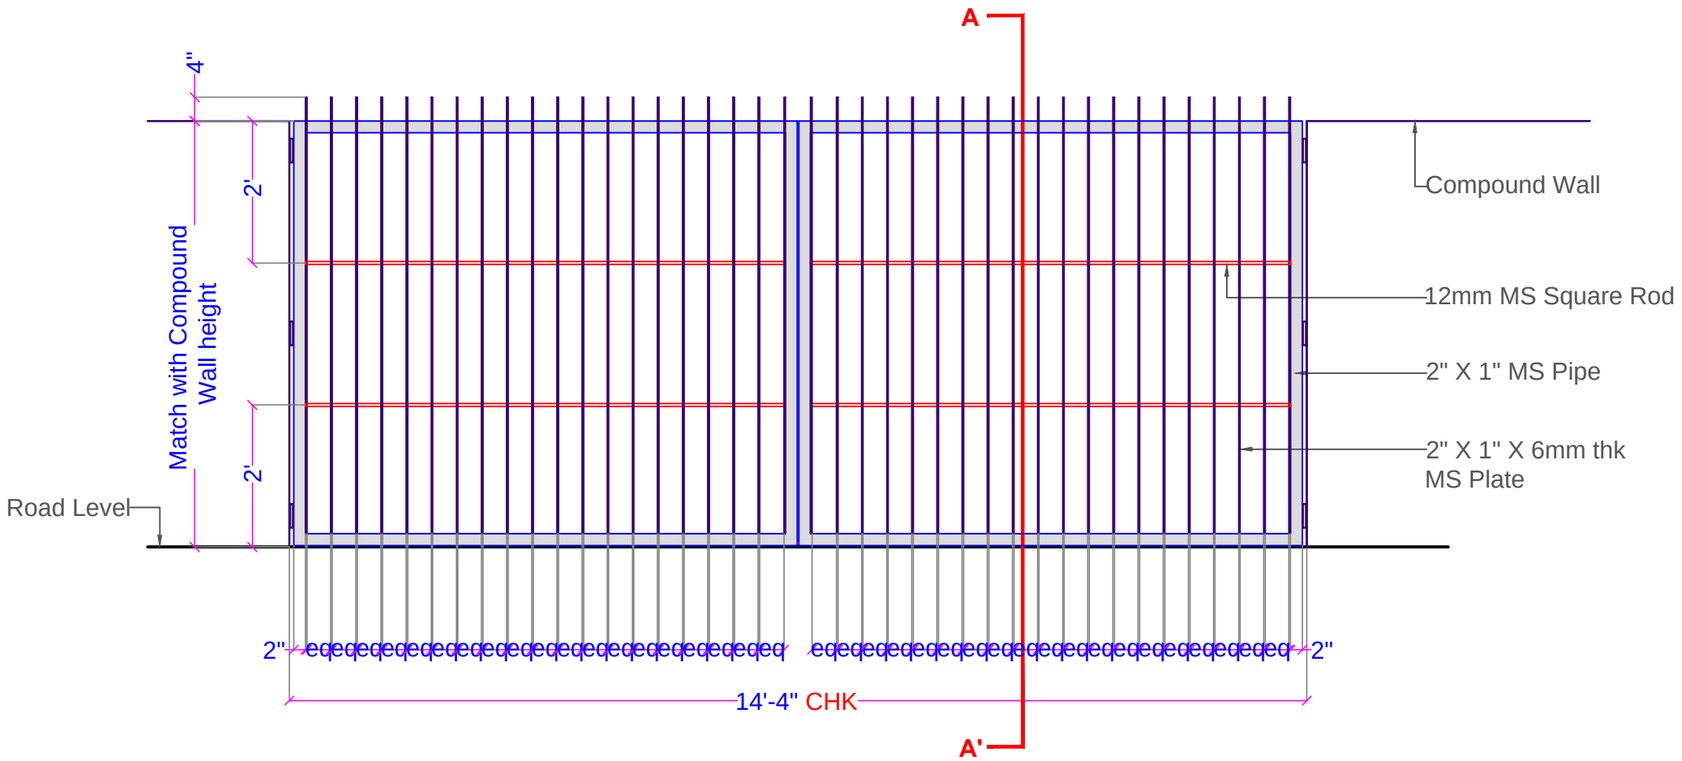


FRONT ELEVATION

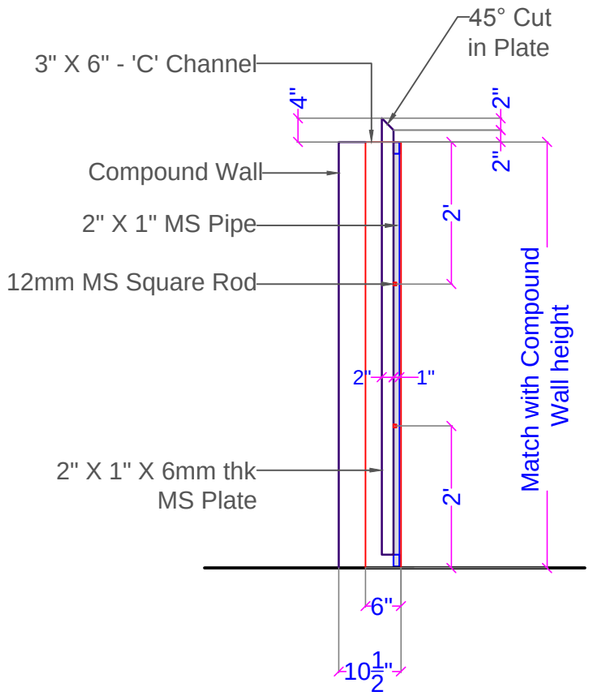

SECTION A-A'

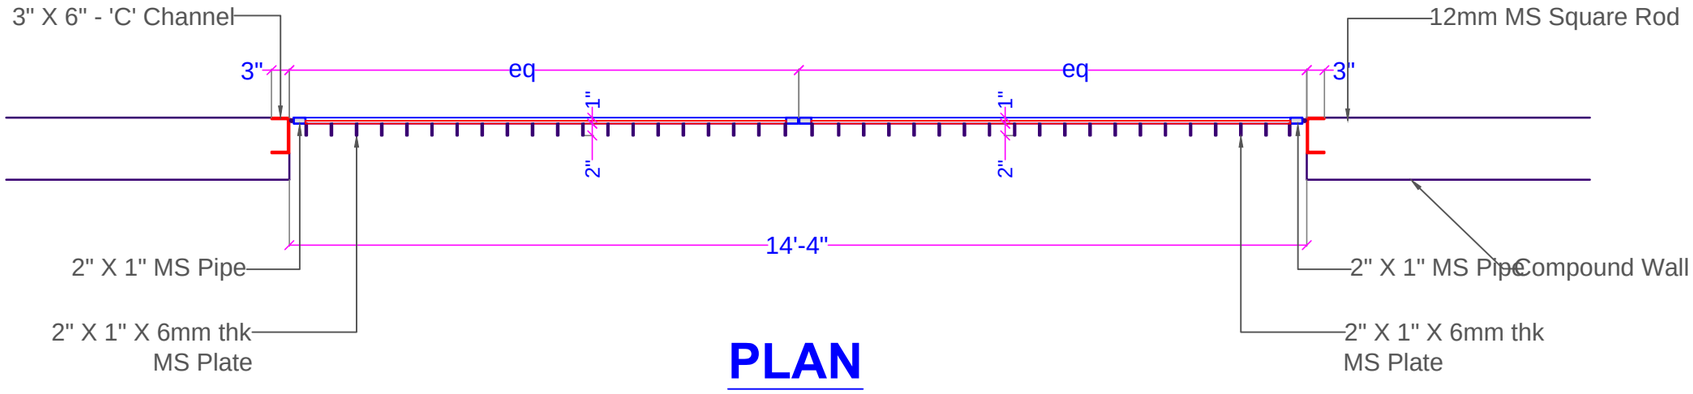

PLAN

REVISION:	**DATE:**	**SIGN:** Designer	**DRAWING STATUS:** ADVANCE COPY	**PROJECT:** PROPOSED INTERIOR DESIGNING WORK OF RESIDENCE FOR MR. SANJAY ADHAV	**NOTE:** * Do not scale the drawing for measurements. * All dimensions are in feet and inches * Drawings with multiple reference are to be read in conjunction of respective drawings. * Dimensions are to be verified at site before starting the work. * Any discrepancy in the drawing should be bought to the attention of designer or site coordinator and clarified before starting the work.	* This Drawing is the property of ANIRUDDHA SANE & ASSOCIATES. It should not be copied, reproduced or retransfer in any manner either in part or full, and it shall be used only for the job issued for.
REVISION NOTE: * This revised drawing supercedes all the previous drawings given for the same job title/ drg no .		**SIGN:** Client	**TITLE:** LANDSCAPE AREA - PARKING GATE DETAILS			Scale : NTS; Date : 30.05.2022; Drg No : COM/WD/FUR/03; Job No : ; Drg By : NIKHIL; Chk By : ASA

ANIRUDDHA SANE & ASSOCIATES
Interior Designers & Consultants
A12, Shree Keshav Smruti,
197 Sadashiv Peth, Pune 30.
Ph No : 020 - 24530277
email: aniruddha.sane@yahoo.in