
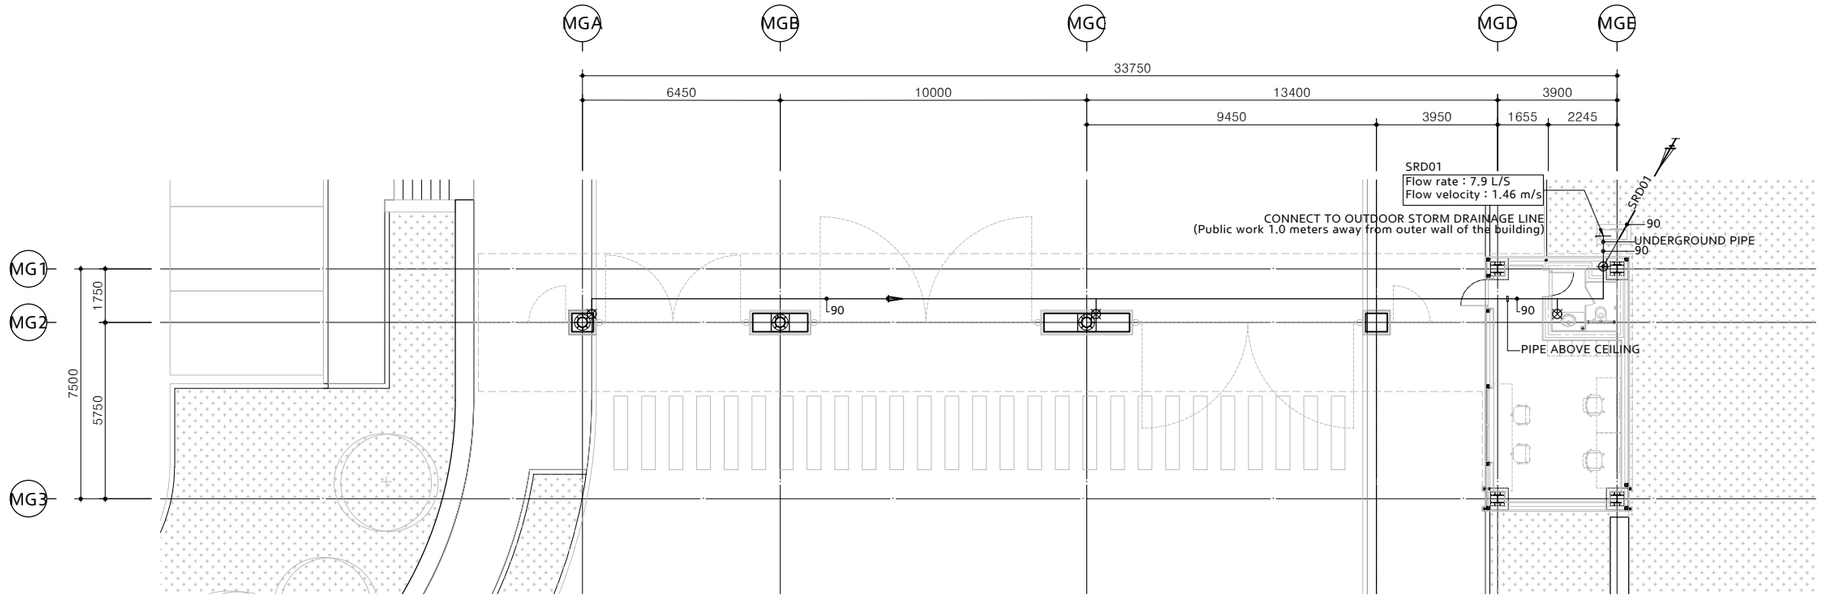



1 GROUND FLOOR STORMWATER DRAIN PLAN

SCALE : 1/100

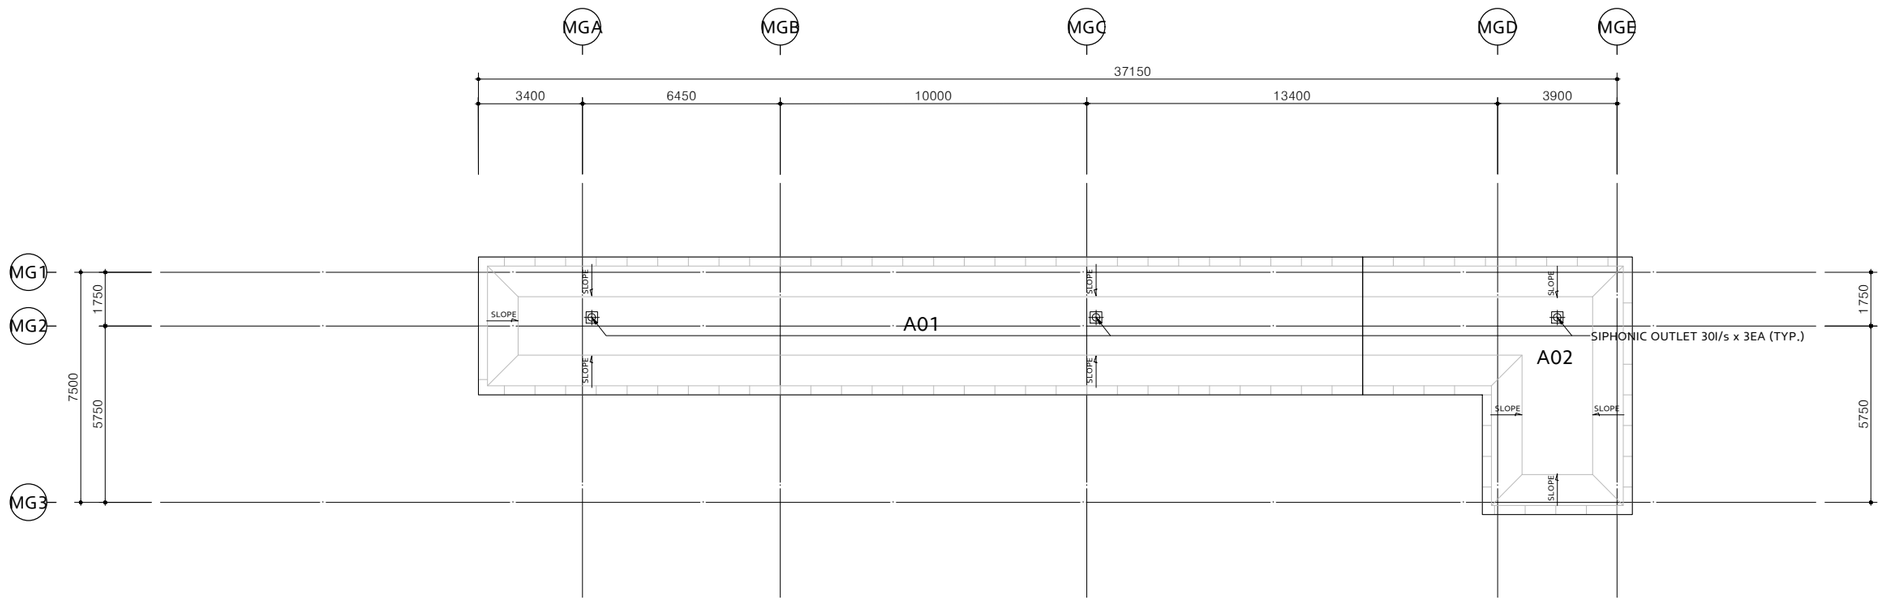

2 ROOF STORMWATER DRAIN PLAN

SCALE : 1/100

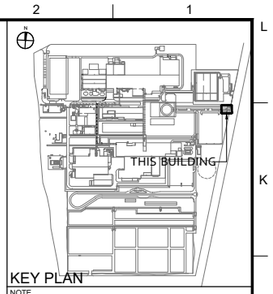

KEY PLAN

NOTE

1. GROUND FLOOR LEVEL
   -GROUND FLOOR FL ±0.00 = EL+663.20
2. LEVEL(T.O.C) OF GROUND FLOOR, WHICH IS THE BASE LEVEL OF ALL LEVEL DIMENSIONS.
3. THIS DRAWING SHOULD BE APPROVED BY HEC & HMI BEFORE APPLICATION
4. REFER TO DRAWING NUMBER "000-G-0001~0900" FOR GENERAL NOTES AND STANDARDS DETAIL.
5. SITE SURVEY FOR THIS DRAWING SHALL BE REQUIRED AND SUPERVISOR'S APPROVAL SHALL BE OBTAINED PRIOR TO CONSTRUCTION.
6. IF THE DRAWING IS DIFFERENT FROM CURRENT SITE, SUPERVISORS AND DESIGNER'S APPROVAL SHALL BE OBTAINED PRIOR TO CONSTRUCTION.
7. STRUCTURES IN THE BUILDING SHOULD BE ALKYD ENAMEL PAINT ON ANTI- RUST PAINT.
8. ALL SEALANT SHALL BE SUBMITTED TO THE MANUFACTURING ENGINEERING TEAM AND APPROVED PRIOR TO THE INSTALLATION BY THEM.

REV.	DESCRIPTION	DRAWN	DATE
0	CONSTRUCTION DRAWING	OH.J.S	2025. 02.14

CLIENT

HYUNDAI

ARCHITECTS & ENGINEERS

JUNGLIM ARCHITECTURE

PROJECT TITLE

PUNE HMI PROJECT

DRAWING TITLE

[MAIN GATE]
GROUND FLOOR & ROOF STORMWATER DRAIN PLAN

SCALE	DRAWN	CHECKED	REVIEWED	APPROVED	APPROVED
A1: 1/100 A3:1/200	OH.J.S	HONG.G.D	LEE.S.L	HEC INDIA	PARK.T.S
DATE 14 FEB,2025					

MAIN CONTRACTOR

HEC INDIA LLP

DRAWING NO.	REV.
WA-IPB-640-A-3002	0

A1 SIZE (841mm x 594mm)